

Estación Bigbag / Conjunto general

ALZADO LONGITUDINAL ESCALA 1:40

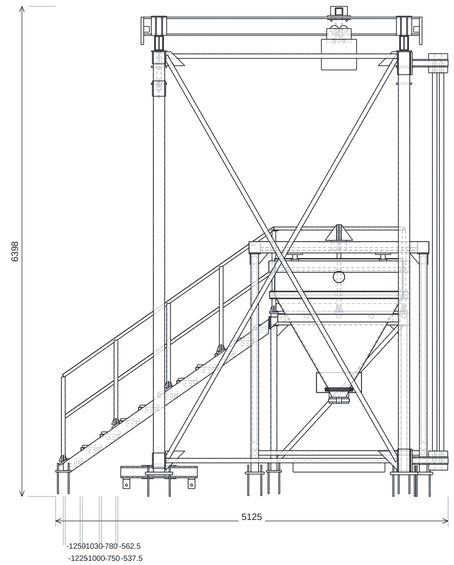

REFERENCIA X (mm)


ALZADO TRANSVERSAL ESCALA 1:50

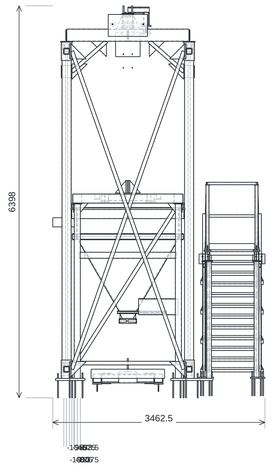

REFERENCIA Y (mm)

CONJUNTO	PLANO
Cimentación y placas base	EB-02
Pórticos transversales ensamblados	EB-03
Arriostramiento longitudinal y uniones	EB-04
Viga carril y topes de fin de carrera	EB-05
Bastidor de tolva ensamblado	EB-06
Tolva, anillos y revestimiento	EB-07
Cortador y parrilla de apoyo de bolsa	EB-08
Compuerta de descarga ensamblada	EB-09
Guarda, ensacado y captación	EB-10
Carro, suspensión y traba de posición	EB-11
Plataforma de acceso ensamblada	EB-12
Escalera y desembarco ensamblados	EB-13
Barandas, pasamanos y rodapiés	EB-14
Cruceta de izaje 2 t ensamblada	EB-15

ISOMÉTRICO A COLOR / REFERENCIA DE MONTAJE

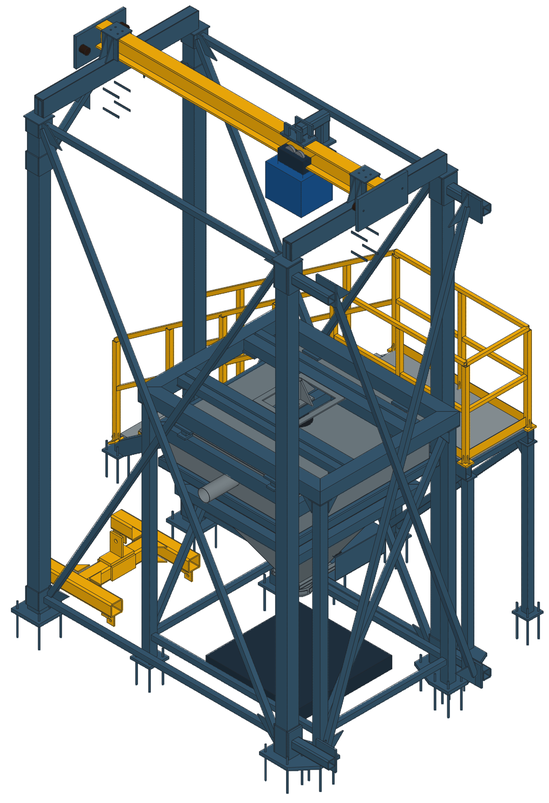

NOTAS DE FABRICACIÓN Y MONTAJE


1. Cruceta y tecle nominales 2 t; proceso de bolsas de 1 t.
2. Traslado con fondo de bolsa a Z = 3 520; guarda superior Z = 3 430; punta de cortador Z = 3 230.
3. Enclavamientos, prueba de carga y recepción según memoria.
4. POS.: número de pieza en la lista de 248 piezas únicas.

Cotas en mm. ISO2768-m. Soldaduras según cuadro JF. Contornos: CAD/DXF.


				REBABAR Y ROMPER ARISTAS	NO CAMBIAR LA ESCALA	REVISIÓN
SESUVECA DEL PERÚ						
	NOMBRE	FIRMA	FECHA			TÍTULO: Estación Bigbag / Conjunto general
DIBUJ.	Javier Acevedo		16/10/26			
VERIF.						
APROB.						
FABR.						
CALID.				MATERIAL: SEGÚN LISTA DE MATERIALES		N.º DE DIBUJO EB-01 / A1
PESO: SEGÚN CAD / lista de materiales				ESCALA: INDICADA		ESTACIÓN DE DESCARGA BIGBAG / HOJA 1 DE 17

Cimentación y placas base

PLANTA ESCALA 1:20

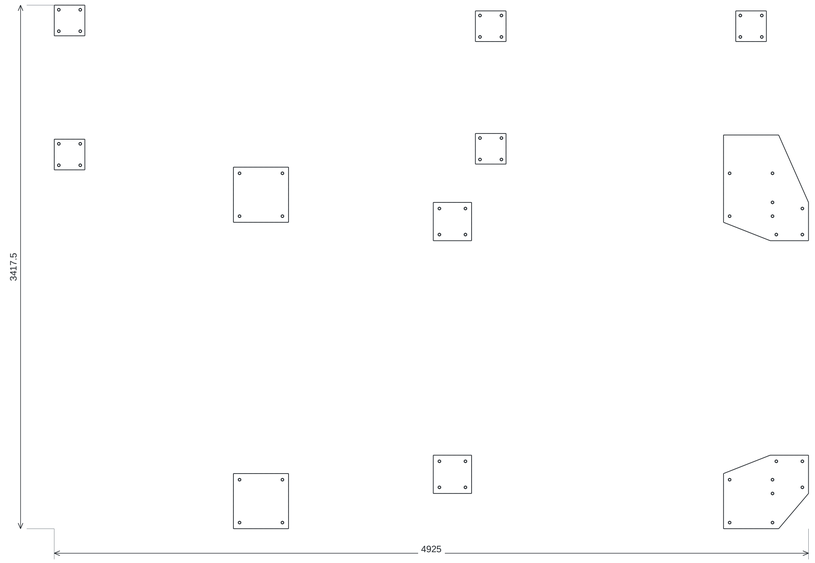

ALZADO ESCALA 1:15

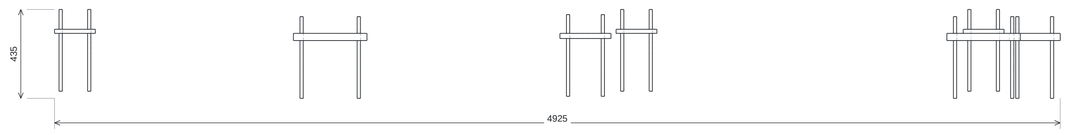

POS.	CANT.	PIEZA / MEDIDAS EN mm	MATERIAL / SUMINISTRO
38	2	Placa base de columna principal; ancho 360; alto 360; espesor 35; taladros Ø18	ASTM A36 / Fabricar
39	2	Placa base de pata de tolva; ancho 250; alto 250; espesor 25; taladros Ø18	ASTM A36 / Fabricar
40	5	Placa base de acceso; ancho 200; alto 200; espesor 20; taladros Ø18	ASTM A36 / Fabricar
125	1	Placa base compartida de columnas; ancho 555; alto 480; espesor 35; taladros Ø18	ASTM A36 / Fabricar
126	1	Placa base compartida de columnas; ancho 555; alto 690; espesor 35; taladros Ø18	ASTM A36 / Fabricar
127	52	Anclaje Hilti HAS-U 8.8 M16; M16 × 400; empotramiento 275	Acero clase 8.8 / ISO898-1 / Comprar
128	52	Arandela M16; largo 3; pared 6; Ø exterior 30; Ø interior 18	Acero 200HV / ISO7089 / Comprar
129	52	Tuerca M16; Rosca M16; clase 8	Acero clase 8 / ISO898-2 / Comprar

ISOMÉTRICO A COLOR / REFERENCIA DE MONTAJE



NOTAS DE FABRICACIÓN Y MONTAJE

1. Losa: espesor 650 mm; f'c = 20,59 MPa (datos del cliente).
2. HAS-U 8.8 M16: longitud total 400; empotramiento efectivo 275; resina HIT-RE 500 V4.
3. Replanteo en coordenadas globales; cota Z0 = cara superior del concreto. Borde mínimo de proyecto: 500 mm.
4. Respetar patrón y diámetro de agujeros del CAD; instalación, limpieza y curado según fabricante.

Cotas en mm. ISO2768-m. Soldaduras según cuadro JF. Contornos: CAD/DXF.


TALADROS DE PIEZAS DEL CONJUNTO / COORDENADAS LOCALES mm / ORIGEN LOCAL

P38 T1: Ø18; X-140 Y-140 Z0; eje Z
P38 T2: Ø18; X-140 Y140 Z0; eje Z
P38 T3: Ø18; X140 Y-140 Z0; eje Z
P38 T4: Ø18; X140 Y140 Z0; eje Z
P39 T1: Ø18; X-85 Y-85 Z0; eje Z
P39 T2: Ø18; X-85 Y85 Z0; eje Z
P39 T3: Ø18; X85 Y-85 Z0; eje Z
P39 T4: Ø18; X85 Y85 Z0; eje Z
P40 T1: Ø18; X-70 Y-70 Z0; eje Z
P40 T2: Ø18; X-70 Y70 Z0; eje Z
P40 T3: Ø18; X70 Y-70 Z0; eje Z
P40 T4: Ø18; X70 Y70 Z0; eje Z
P125 T1: Ø18; X-140 Y-140 Z0; eje Z
P125 T2: Ø18; X-140 Y140 Z0; eje Z
P125 T3: Ø18; X140 Y-140 Z0; eje Z
P125 T4: Ø18; X140 Y140 Z0; eje Z
P125 T5: Ø18; X140 Y50 Z0; eje Z
P125 T6: Ø18; X165 Y260 Z0; eje Z
P125 T7: Ø18; X335 Y90 Z0; eje Z
P125 T8: Ø18; X335 Y260 Z0; eje Z
P126 T1: Ø18; X-140 Y-140 Z0; eje Z
P126 T2: Ø18; X-140 Y140 Z0; eje Z
P126 T3: Ø18; X140 Y-140 Z0; eje Z
P126 T4: Ø18; X140 Y140 Z0; eje Z
P126 T5: Ø18; X165 Y-260 Z0; eje Z
P126 T6: Ø18; X140 Y-50 Z0; eje Z
P126 T7: Ø18; X335 Y-260 Z0; eje Z
P126 T8: Ø18; X335 Y-90 Z0; eje Z

				REBABAR Y ROMPER ARISTAS	NO CAMBIAR LA ESCALA	REVISIÓN
SESUVECA DEL PERÚ						
	NOMBRE	FIRMA	FECHA			TÍTULO: Cimentación y placas base
DIBUJ.	Javier Acevedo		16/10/26			
VERIF.						
APROB.						
FABR.						
CALID.				MATERIAL: SEGÚN LISTA DE MATERIALES		N.º DE DIBUJO EB-02 / A1
PESO: SEGÚN CAD / lista de materiales				ESCALA: INDICADA		ESTACIÓN DE DESCARGA BIGBAG / HOJA 2 DE 17

Pórticos transversales ensamblados

PERFIL ESCALA 1:40

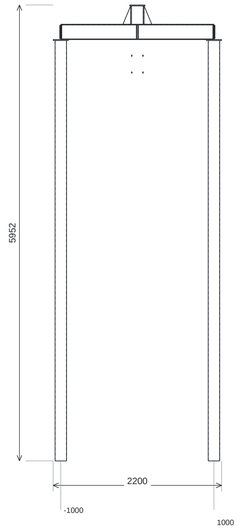


REFERENCIA Y (mm)

PLANTA ESCALA 1:15

POS.	CANT.	PIEZA / MEDIDAS EN mm	MATERIAL / SUMINISTRO
1	4	Tramo de tubo cuadrado; ancho 150; alto 150; largo 5488; pared 6	ASTM A500 Gr.B / Fabricar
2	2	Viga transversal IPE 200; ancho 100; alto 200; largo 2000; pared 5.6; espesor ala 8.5	ASTM A36 / Fabricar
41	2	Placa superior de unión a viga; ancho 200; alto 200; espesor 12; taladros Ø18	ASTM A36 / Fabricar
42	4	Placa lateral de unión a viga; ancho 200; alto 240; espesor 12	ASTM A36 / Fabricar
43	8	Placa separadora de unión a viga; ancho 200; alto 20; espesor 6	ASTM A36 / Fabricar
44	24	Placa de refuerzo de unión a viga; ancho 44; alto 175; espesor 6	ASTM A36 / Fabricar
45	8	Refuerzo triangular de unión a viga; ancho 100; alto 240; espesor 12	ASTM A36 / Fabricar
46	4	Tapa de columna principal; ancho 200; alto 200; espesor 12	ASTM A36 / Fabricar

ISOMÉTRICO A COLOR / REFERENCIA DE MONTAJE

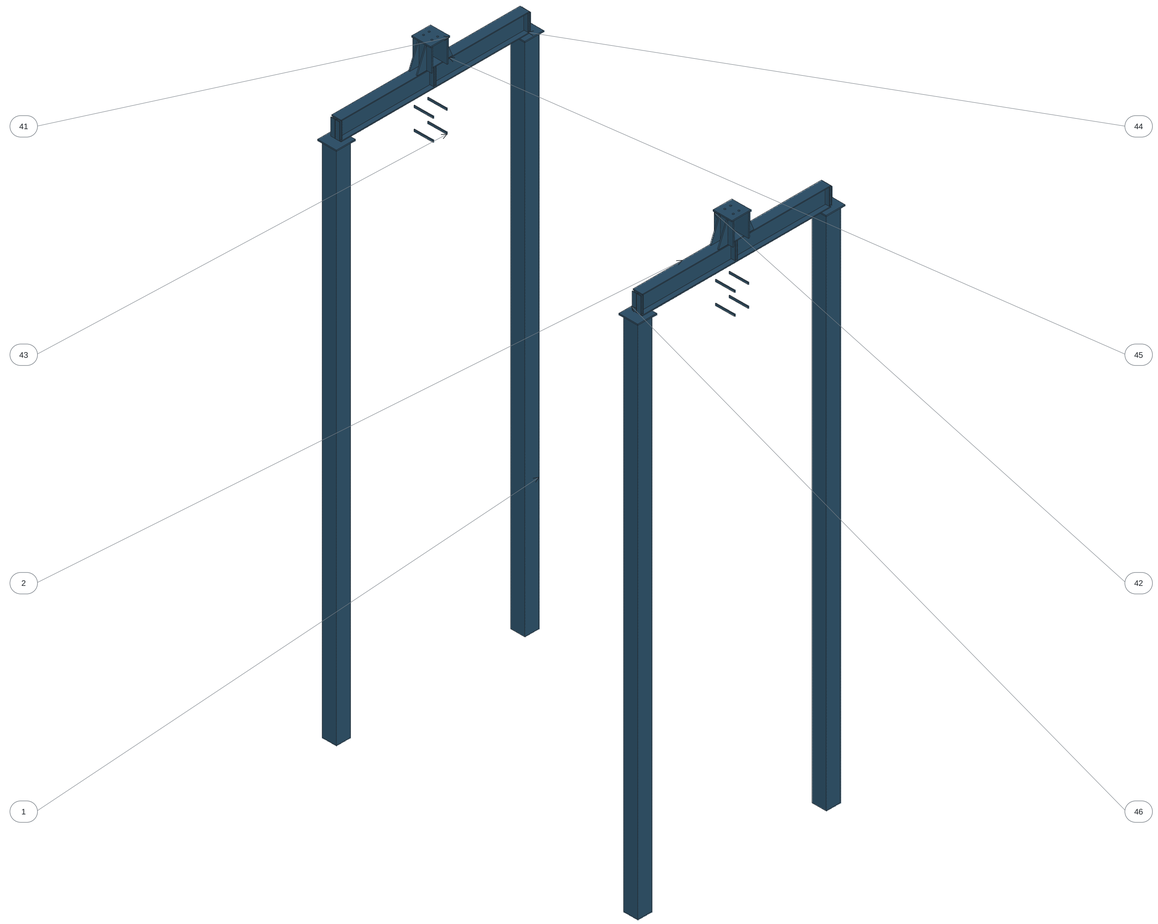

NOTAS DE FABRICACIÓN Y MONTAJE

1. Dos pórticos, ejes X = 0 y 3 200; separación Y = 2 000 entre columnas.
2. Columnas SHS150x150x6; travesaños IPE200. Chapas de unión U01 / P01 según lista de materiales.
3. Cotas referidas a la posición nominal montada. Soldadura de taller; montaje desmontable según detalle.

Cotas en mm. ISO2768-m. Soldaduras según cuadro JF. Contornos: CAD/DXF.


TALADROS DE PIEZAS DEL CONJUNTO / COORDENADAS LOCALES mm / ORIGEN LOCAL

P41 T1: Ø18; X-45 Y-30 Z0; eje Z
P41 T2: Ø18; X-45 Y30 Z0; eje Z
P41 T3: Ø18; X45 Y-30 Z0; eje Z
P41 T4: Ø18; X45 Y30 Z0; eje Z

				REBABAR Y ROMPER ARISTAS	NO CAMBIAR LA ESCALA		REVISIÓN
SESUVECA DEL PERÚ							
	NOMBRE	FIRMA	FECHA			TÍTULO: Pórticos transversales ensamblados	
DIBUJ.	Javier Acevedo		16/10/26				
VERIF.							
APROB.							
FABR.							
CALID.				MATERIAL: SEGÚN LISTA DE MATERIALES		N.º DE DIBUJO EB-03	A1
PESO: SEGÚN CAD / lista de materiales				ESCALA: INDICADA		ESTACIÓN DE DESCARGA BIGBAG	HOJA 3 DE 17

Arriostramiento longitudinal y uniones

ALZADO ESCALA 1:40

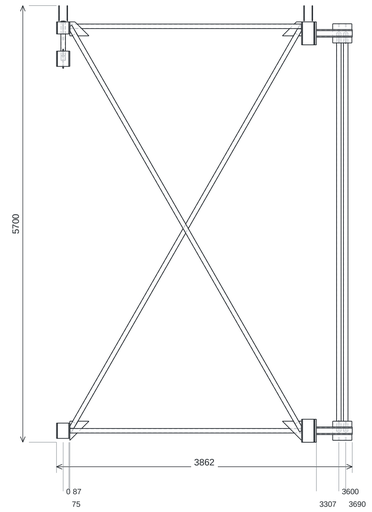


REFERENCIA X (mm)

PLANTA ESCALA 1:15

POS.	CANT.	PIEZA / MEDIDAS EN mm	MATERIAL / SUMINISTRO
47	8	Placa de unión de diagonal a columna; ancho 150; alto 200; espesor 12	ASTM A36 / Fabricar
48	8	Placa de unión de diagonal a columna; ancho 174; alto 200; espesor 12	ASTM A36 / Fabricar
49	4	Placa de unión de diagonal a columna; ancho 150; alto 158; espesor 12	ASTM A36 / Fabricar
50	4	Placa de unión de diagonal a columna; ancho 174; alto 158; espesor 12	ASTM A36 / Fabricar
51-62	12	Refuerzo triangular de diagonal; ancho 250; alto 250; espesor 12	ASTM A36 / Fabricar
130	4	Placa de cierre de viga transversal; ancho 2000; alto 200; espesor 8	ASTM A36 / Fabricar
153,156	2	Diagonal de refuerzo longitudinal; ancho 60; alto 60; largo 5499.97; pared 4	ASTM A500 Gr.B / Fabricar
154-155,157-158	4	Placa de unión de diagonal; ancho 250; alto 250; espesor 12	ASTM A36 / Fabricar
159	8	Placa de unión a columna; ancho 150; alto 300; espesor 12	ASTM A36 / Fabricar
160	8	Placa de unión a columna; ancho 174; alto 300; espesor 12	ASTM A36 / Fabricar
161	4	Placa de refuerzo de columna; ancho 174; alto 300; espesor 20	ASTM A36 / Fabricar
162	4	Brazo lateral de refuerzo; ancho 100; alto 100; largo 468; pared 10	S355NH / EN10210-1 / Fabricar
163	4	Placa exterior de unión; ancho 250; alto 250; espesor 20	ASTM A36 / Fabricar
182-183,185-186	4	Tramo de tubo cuadrado; ancho 60; alto 60; largo 6085.65; pared 4	ASTM A500 Gr.B / Fabricar
184,187	2	Tramo de tubo cuadrado; ancho 60; alto 60; largo 748.81; pared 4	ASTM A500 Gr.B / Fabricar
195-198	4	Tramo de tubo cuadrado; ancho 60; alto 60; largo 3050; pared 4	ASTM A500 Gr.B / Fabricar

ISOMÉTRICO A COLOR / REFERENCIA DE MONTAJE

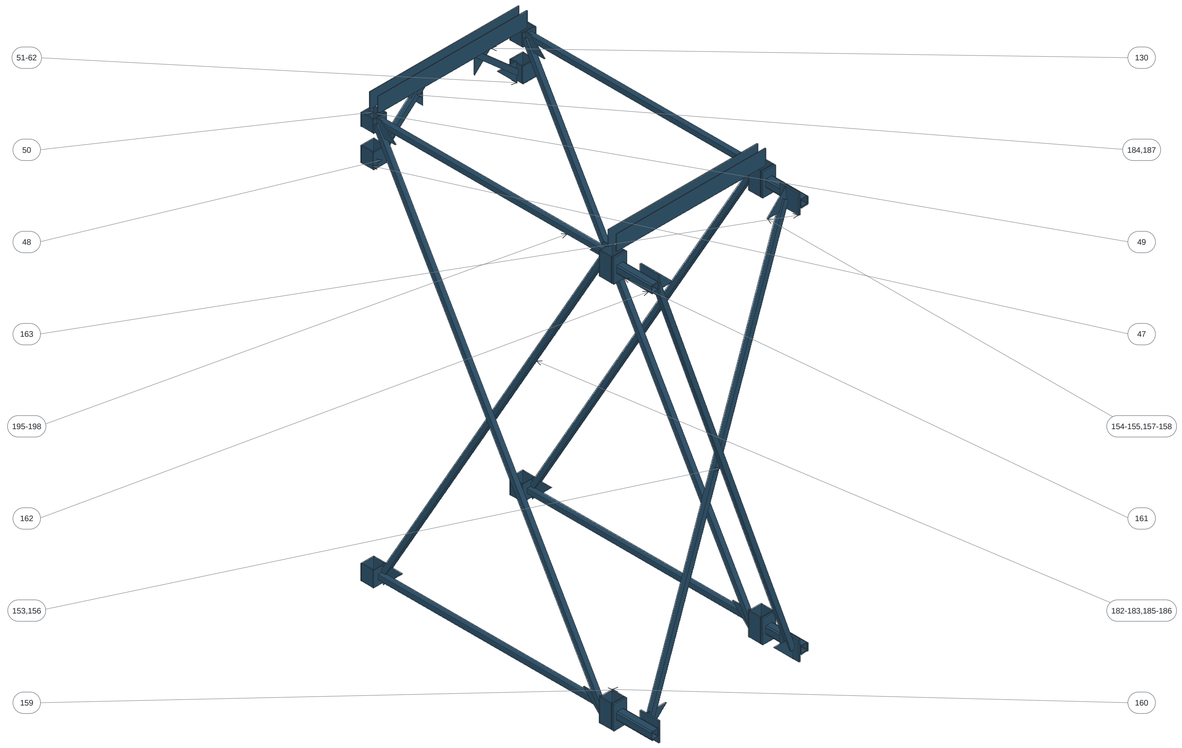

NOTAS DE FABRICACIÓN Y MONTAJE


1. Dos planos longitudinales Y = -1 000 y +1 000. Luz entre pórticos: 3 200.
2. Conservar ranuras y recortes de extremos; no soldar las holguras JF identificadas como LUZ.
3. Collares, lengüetas y diagonales: preparaciones según CAD; mantener holguras libres de soldadura.
4. Geometría BRT y posición de collares según CAD final; reacción longitudinal de diseño: 12 kN.

Cotas en mm. ISO2768-m. Soldaduras según cuadro JF. Contornos: CAD/DXF.

				REBABAR Y ROMPER ARISTAS	NO CAMBIAR LA ESCALA	REVISIÓN
SESUVECA DEL PERÚ						
	NOMBRE	FIRMA	FECHA			TÍTULO: Arriostramiento longitudinal y uniones
DIBUJ.	Javier Acevedo		16/10/26			
VERIF.						
APROB.						
FABR.						
CALID.				MATERIAL: SEGÚN LISTA DE MATERIALES		N.º DE DIBUJO EB-04 / A1
PESO: SEGÚN CAD / lista de materiales				ESCALA: INDICADA		ESTACIÓN DE DESCARGA BIGBAG / HOJA 4 DE 17


Viga carril y topes de fin de carrera

ALZADO ESCALA 1:15

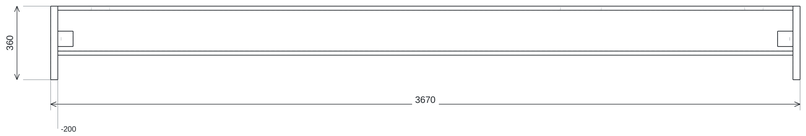


REFERENCIA X (mm)

PLANTA ESCALA 1:15

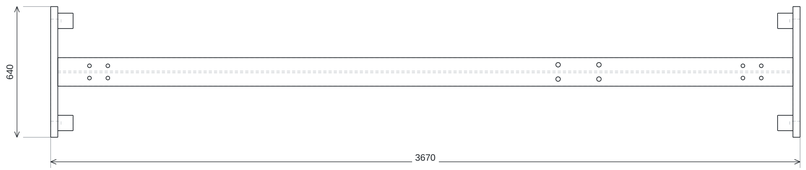

POS.	CANT.	PIEZA / MEDIDAS EN mm	MATERIAL / SUMINISTRO
3	1	Viga carril I soldada 240×140; ancho 140; alto 240; largo 3600; pared 8; espesor ala 20; taladros Ø18, Ø22	ASTM A36 / Fabricar
175	2	Placa de respaldo de amortiguador; ancho 640; alto 360; espesor 35; taladros Ø18	ASTM A36 / Fabricar
176	4	Amortiguador ACE TS75-39; largo 75; Ø exterior 75	Elastómero copoliéster Shore 40D / Comprar
177	4	Tornillo de fijación del amortiguador; largo 51; Ø exterior 16	Tornillo ACE suministrado con TS75-39 / Comprar

ISOMÉTRICO A COLOR / REFERENCIA DE MONTAJE

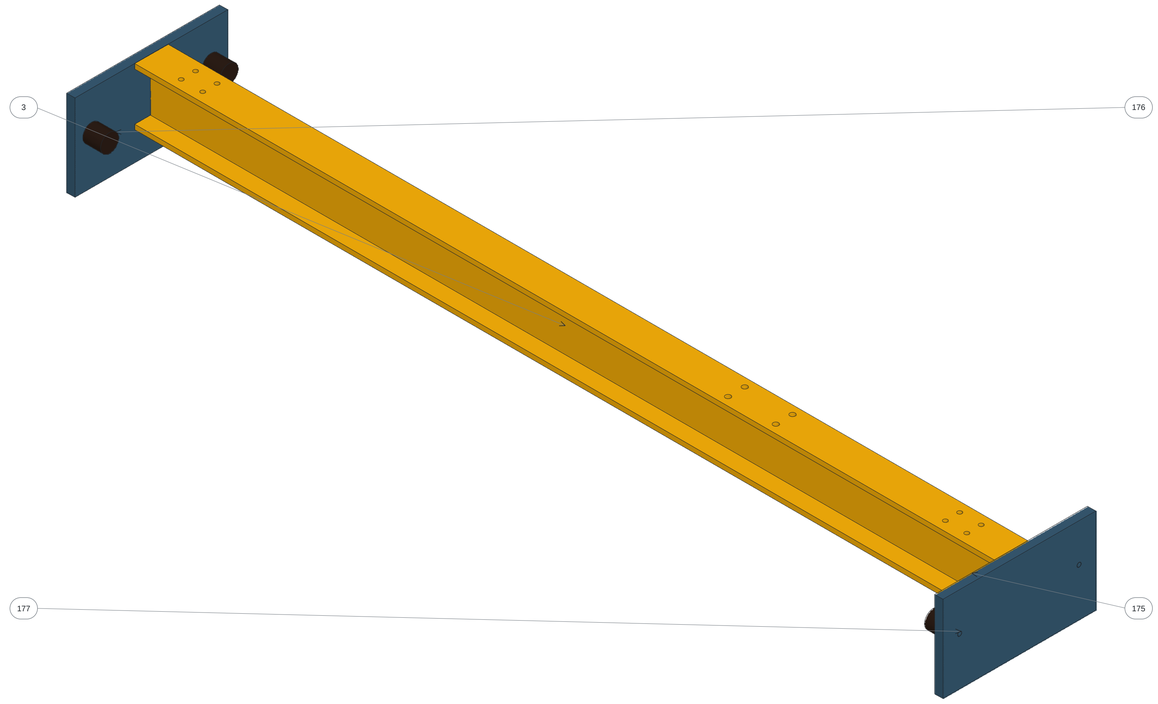

NOTAS DE FABRICACIÓN Y MONTAJE

1. Viga fabricada I240x140x8x20; longitud 3 600; ala de rodadura 140 x 20.
2. Dos topes ACE TS75-39 por extremo; placas de reacción 640 x 360 x 35.
3. Carrera nominal del amortiguador39; energía de proyecto420,80 J; reacción estructural12 kN.
4. Montaje KITO y topes: ver especificación y memoria.
5. Perfil 240 × 140 × 8 fabricado: 1 tiras 200 × 8 + 2 tiras 140 × 20 de ASTM A36. Cuatro soldaduras longitudinales que atraviesan el espesor completo.

Cotas en mm. ISO2768-m. Soldaduras según cuadro JF. Contornos: CAD/DXF.


TALADROS DE PIEZAS DEL CONJUNTO / COORDENADAS LOCALES mm / ORIGEN LOCAL

P3 B1: Ø18; X-30 Y95 Z155; eje Y
P3 B2: Ø18; X30 Y95 Z155; eje Y
P3 B3: Ø18; X-30 Y95 Z245; eje Y
P3 B4: Ø18; X30 Y95 Z245; eje Y
P3 B5: Ø18; X-30 Y95 Z3355; eje Y
P3 B6: Ø18; X30 Y95 Z3355; eje Y
P3 B7: Ø18; X-30 Y95 Z3445; eje Y
P3 B8: Ø18; X30 Y95 Z3445; eje Y
P3 B9: Ø22; X-35 Y99 Z2450; eje Y
P3 B10: Ø22; X35 Y99 Z2450; eje Y
P3 B11: Ø22; X-35 Y99 Z2650; eje Y
P3 B12: Ø22; X35 Y99 Z2650; eje Y
P175 T1: Ø18; X-250 Y20 Z0; eje Z
P175 T2: Ø18; X250 Y20 Z0; eje Z

				REBABAR Y ROMPER ARISTAS	NO CAMBIAR LA ESCALA	REVISIÓN
SESUVECA DEL PERÚ						
	NOMBRE	FIRMA	FECHA			TÍTULO: Viga carril y topes de fin de carrera
DIBUJ.	Javier Acevedo		16/10/26			
VERIF.						
APROB.						
FABR.						
CALID.				MATERIAL: SEGÚN LISTA DE MATERIALES		N.º DE DIBUJO EB-05 / A1
PESO: SEGÚN CAD / lista de materiales				ESCALA: INDICADA		ESTACIÓN DE DESCARGA BIGBAG / HOJA 5 DE 17


Bastidor de tolva ensamblado

ALZADO ESCALA 1:20

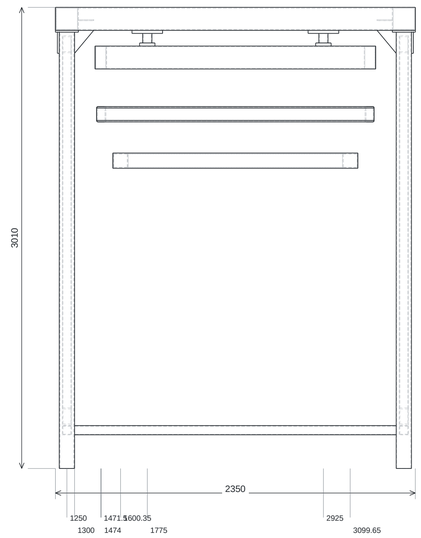


REFERENCIA X (mm)

PLANTA ESCALA 1:15

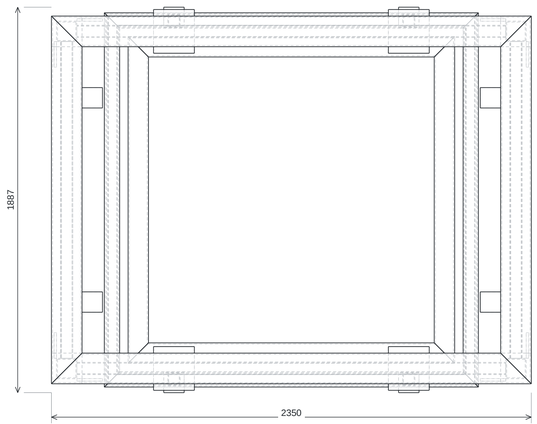

POS.	CANT.	PIEZA / MEDIDAS EN mm	MATERIAL / SUMINISTRO
4	4	Tramo de tubo cuadrado; ancho 100; alto 100; largo 2848; pared 5	ASTM A500 Gr.B / Fabricar
5	2	Tramo de tubo cuadrado; ancho 150; alto 150; largo 2200; pared 6	ASTM A500 Gr.B / Fabricar
6	2	Tramo de tubo cuadrado; ancho 150; alto 150; largo 1650; pared 6	ASTM A500 Gr.B / Fabricar
7	2	Tramo de tubo cuadrado; ancho 60; alto 60; largo 2100; pared 4	ASTM A500 Gr.B / Fabricar
8	2	Tramo de tubo cuadrado; ancho 60; alto 60; largo 1550; pared 4	ASTM A500 Gr.B / Fabricar
9	4	Tramo de tubo cuadrado; ancho 100; alto 100; largo 1499.3; pared 6	ASTM A500 Gr.B / Fabricar
10-11	4	Tramo de tubo rectangular; ancho 75; alto 150; largo 1757; pared 5	ASTM A500 Gr.B / Fabricar
12	2	Tramo de tubo cuadrado; ancho 60; alto 60; largo 2882.26; pared 4	ASTM A500 Gr.B / Fabricar
32	4	Tramo de tubo cuadrado; ancho 60; alto 60; largo 62.41; pared 4	ASTM A500 Gr.B / Fabricar
63	4	Tapa de pata de tolva; ancho 150; alto 150; espesor 12	ASTM A36 / Fabricar
66	8	Refuerzo triangular de apoyo de tolva; ancho 125; alto 150; espesor 12	ASTM A36 / Fabricar
67	4	Placa de apoyo del carril; ancho 100; alto 100; espesor 6	ASTM A36 / Fabricar
68	4	Placa inferior de unión de vigas; ancho 100; alto 100; espesor 20	ASTM A36 / Fabricar
69	4	Placa superior de unión de vigas; ancho 200; alto 214; espesor 20	ASTM A36 / Fabricar
170-173	4	Tramo de marco intermedio de tolva; ancho 60; alto 100; largo 1752; pared 6.3	S355NH / EN10210-1 / Fabricar

ISOMÉTRICO A COLOR / REFERENCIA DE MONTAJE

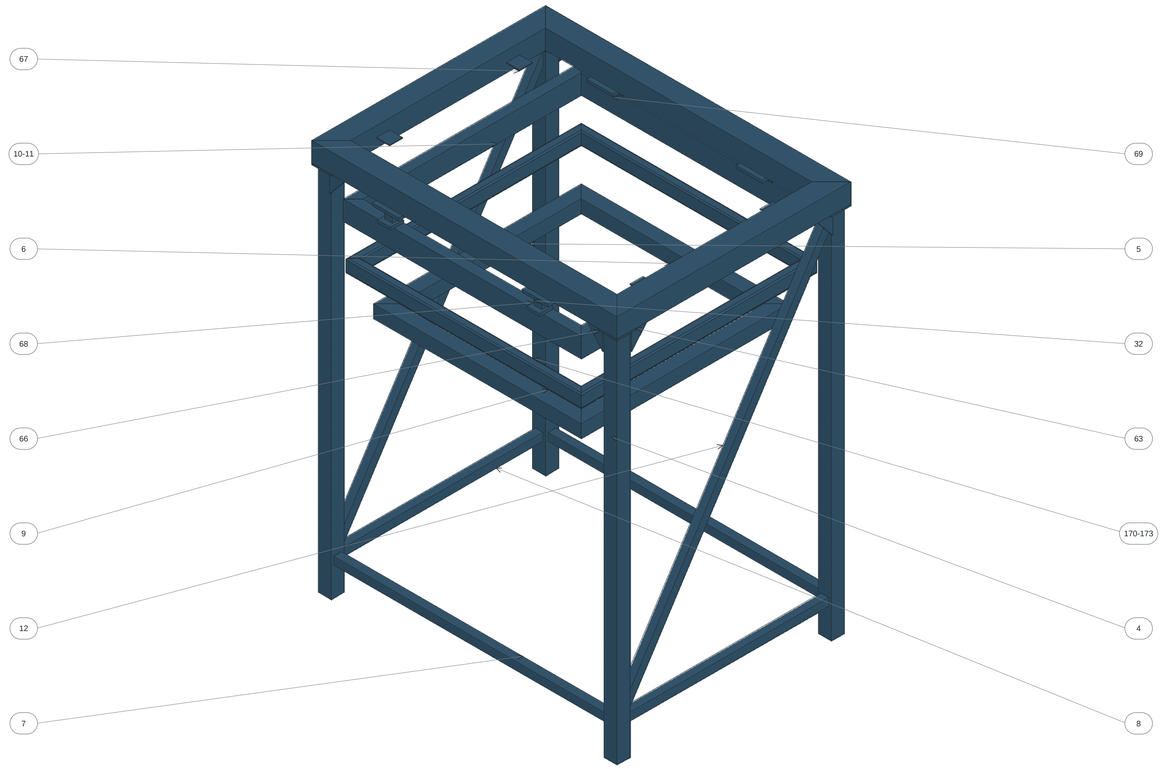

NOTAS DE FABRICACIÓN Y MONTAJE


1. Cuatro patas SHS100x100x5; marco superior SHS150x150x6. Longitudes y cantidades en lista de materiales.
2. Ejes de patas X = 1 250 / 3 450; Y = -825 / +825.
3. Anillos: Z 2009.33 / SHS100x100x6; Z 2312.44 / RHS100x60x6.3; Z 2682.59 / RHS150x75x5.
4. Soldadura de taller según conjunto y espesores; mantener libres las superficies de apoyo y revestimiento.
5. Cuatro asientos inferiores de colgante100×100×20: ejes Y±893.5; colgantes Y±878.5. Luz mínima2.5 mm al casco; dos filetes4×70 efectivos por asiento.
6. Esquinas de anillos: CJP6 en Z 2009.33; CJP6.3 en Z 2312.44; CJP5 en Z 2682.59.

Cotas en mm. ISO2768-m. Soldaduras según cuadro JF. Contornos: CAD/DXF.


				REBABAR Y ROMPER ARISTAS	NO CAMBIAR LA ESCALA	REVISIÓN
SESUVECA DEL PERÚ						
	NOMBRE	FIRMA	FECHA			TÍTULO: Bastidor de tolva ensamblado
DIBUJ.	Javier Acevedo		16/10/26			
VERIF.						
APROB.						
FABR.						
CALID.				MATERIAL: SEGÚN LISTA DE MATERIALES		N.º DE DIBUJO EB-06 / A1
PESO: SEGÚN CAD / lista de materiales				ESCALA: INDICADA		ESTACIÓN DE DESCARGA BIGBAG / HOJA 6 DE 17

Tolva, anillos y revestimiento

ALZADO ESCALA 1:10

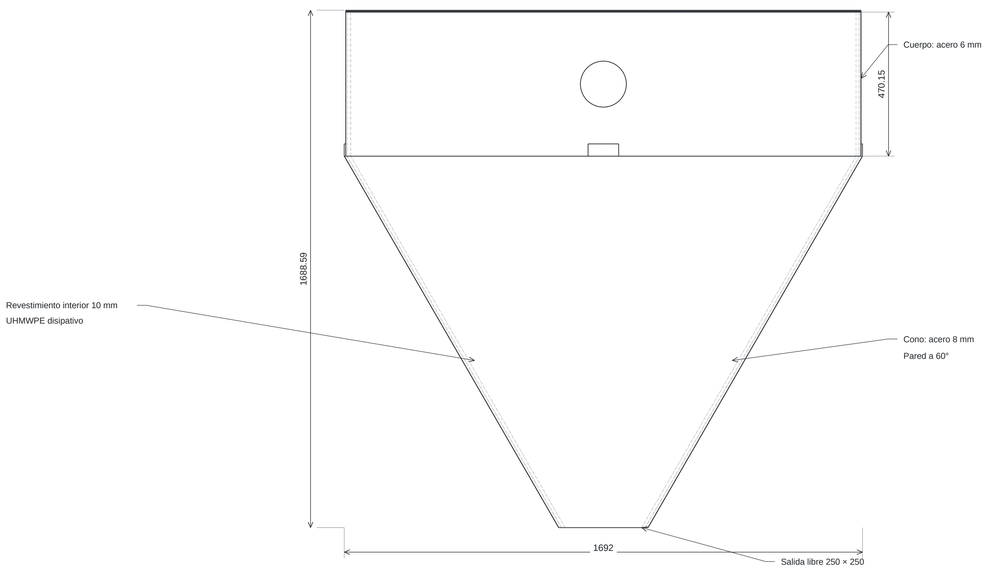


PLANTA ESCALA 1:15

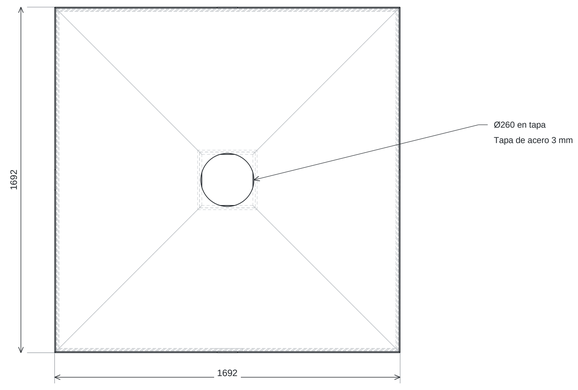

POS.	CANT.	PIEZA / MEDIDAS EN mm	MATERIAL / SUMINISTRO
33	4	Pared inclinada de tolva; Corte envolvente 1691.57×1404.62; espesor 8	ASTM A36 / Fabricar
34	3	Pared vertical de tolva; Corte envolvente 1682×470.15; espesor 6	ASTM A36 / Fabricar
35	1	Pared vertical con conexión de polvo; Corte envolvente 1682×470.15; espesor 6; taladros Ø150	ASTM A36 / Fabricar
36	1	Tapa de tolva; ancho 1682; alto 1682; espesor 3; taladros Ø260	ASTM A36 / Fabricar
37	1	Empaque de tapa de tolva; ancho 1682; alto 1682; espesor 3	EPDM / Fabricar
80	4	Revestimiento interior de pared inclinada; Corte envolvente 1673.09×1405.77; espesor 10	PE-UHMW1000 disipativo / ASTM D4020 / Fabricar
81	3	Revestimiento interior de pared vertical; Corte envolvente 1670×470.15; espesor 10	PE-UHMW1000 disipativo / ASTM D4020 / Fabricar
82	1	Revestimiento vertical con conexión de polvo; Corte envolvente 1670×470.15; espesor 10; taladros Ø150	PE-UHMW1000 disipativo / ASTM D4020 / Fabricar
174	4	Placa de apoyo del marco de tolva; ancho 100; alto 40; espesor 5	ASTM A36 / Fabricar

ISOMÉTRICO A COLOR / REFERENCIA DE MONTAJE

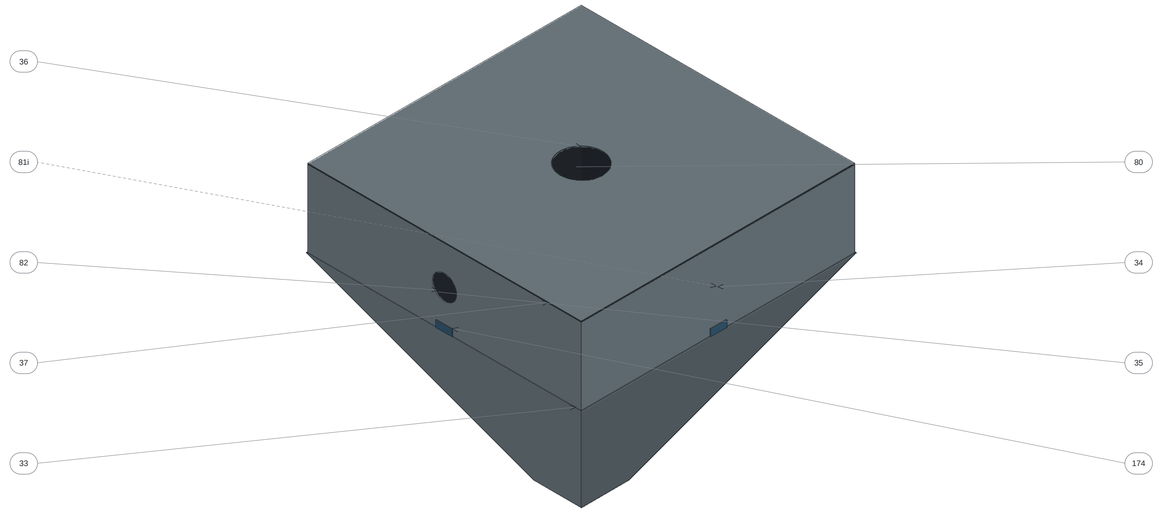

i = pieza interior; línea discontinua.


CONEXIÓN DE DESCARGA

ALZADO 1:2



Conexión a EB-10; materiales incluidos en EB-10.

PLANTA 1:3,33

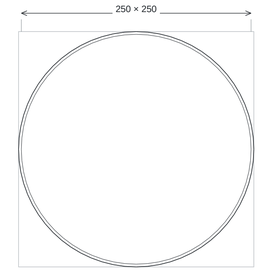

Paso de salida Ø250

NOTAS DE FABRICACIÓN Y MONTAJE

1. Boca interior libre 1 650; salida libre 250; paredes a 60 grados.
2. Tronco piramidal: altura interior1212,44. Cuerpo interior: altura470,15.
3. Chapa de cono: 8 mm; cuerpo: 6 mm. Esquinas del cono: CJP8 continuo.
4. Revestimiento UHMWPE disipativo de 10 mm; dimensiones interiores libres después del revestimiento.
5. Puerto DN150 con paso continuo a través de casco y revestimiento; no obstruir el conducto.
6. Volumen útil y ensayo de descarga por gravedad según memoria.
7. Cuerpo vertical470.15 mm. Volumen total2.572 m³; útil2.058 m³. Salida a1100 mm; apoyo de bolsa a3010 mm.

Cotas en mm. ISO2768-m. Soldaduras según cuadro JF. Contornos: CAD/DXF.

TALADROS DE PIEZAS DEL CONJUNTO / COORDENADAS LOCALES mm / ORIGEN LOCAL


P35 B1: Ø150; X0 Y235.08 Z9; eje Z
P36 T1: Ø260; X0 Y0 Z0; eje Z

P82 B1: Ø150; X0 Y235.08 Z-1; eje Z

				REBABAR Y ROMPER ARISTAS	NO CAMBIAR LA ESCALA	REVISIÓN
SESUVECA DEL PERÚ						
	NOMBRE	FIRMA	FECHA			TÍTULO: Tolva, anillos y revestimiento
DIBUJ.	Javier Acevedo		16/10/26			
VERIF.						
APROB.						
FABR.						
CALID.				MATERIAL: SEGÚN LISTA DE MATERIALES		N.º DE DIBUJO EB-07 / A1
PESO: SEGÚN CAD / lista de materiales				ESCALA: INDICADA		ESTACIÓN DE DESCARGA BIGBAG / HOJA 7 DE 17


Cortador y parrilla de apoyo de bolsa

ALZADO ESCALA 1:8

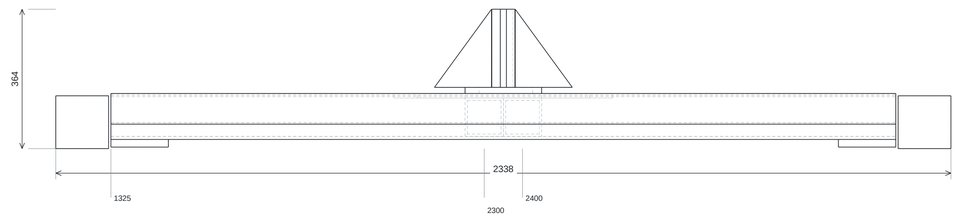


REFERENCIA X (mm)

PLANTA ESCALA 1:8

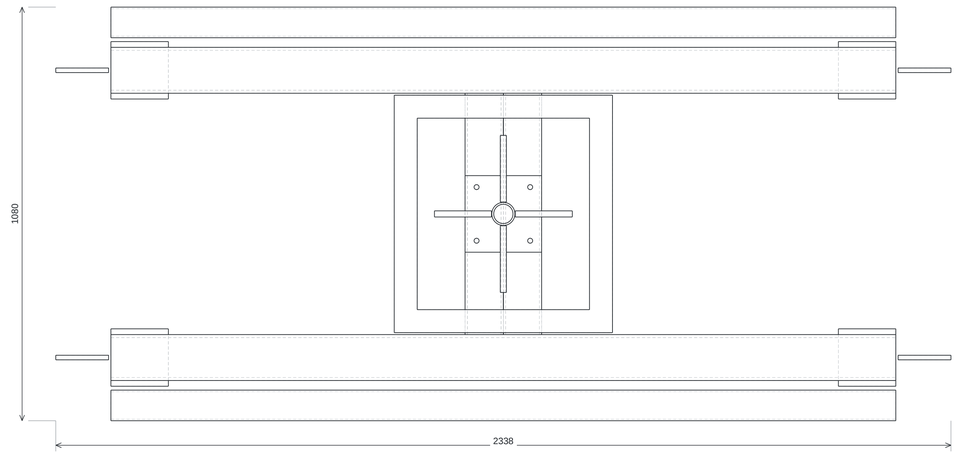

POS.	CANT.	PIEZA / MEDIDAS EN mm	MATERIAL / SUMINISTRO
13	2	Tramo de tubo cuadrado; ancho 80; alto 80; largo 2050; pared 4	ASTM A500 Gr.B / Fabricar
83-84	2	Cuchilla de apertura de bolsa; ancho 149; alto 204; espesor 16	AISI304 / ASTM A240 / Fabricar
85-86	2	Cuchilla de apertura de bolsa; ancho 174; alto 204; espesor 16	AISI304 / ASTM A240 / Fabricar
87	1	Tubo central del cortador; largo 204; pared 5; Ø exterior 60.3; Ø interior 50.3	AISI304 / ASTM A276 / Fabricar
88	1	Marco de apoyo del cortador; ancho 570; alto 620; espesor 12	ASTM A36 / Fabricar
89	1	Placa base del cortador; ancho 200; alto 200; espesor 16; taladros Ø13	ASTM A36 / Fabricar
164,167	2	Travesaño de apoyo de bolsa; ancho 120; alto 120; largo 2050; pared 8	ASTM A500 Gr.B / Fabricar
165	4	Placa de apoyo de travesaño; ancho 150; alto 150; espesor 20	ASTM A36 / Fabricar
166	4	Placa interior de refuerzo de travesaño; ancho 138; alto 138; espesor 12	ASTM A36 / Fabricar
168	2	Travesaño de apoyo del cortador; ancho 100; alto 100; largo 630; pared 6	ASTM A500 Gr.B / Fabricar
169	1	Placa separadora del cortador; ancho 200; alto 200; espesor 12	ASTM A36 / Fabricar

ISOMÉTRICO A COLOR / REFERENCIA DE MONTAJE

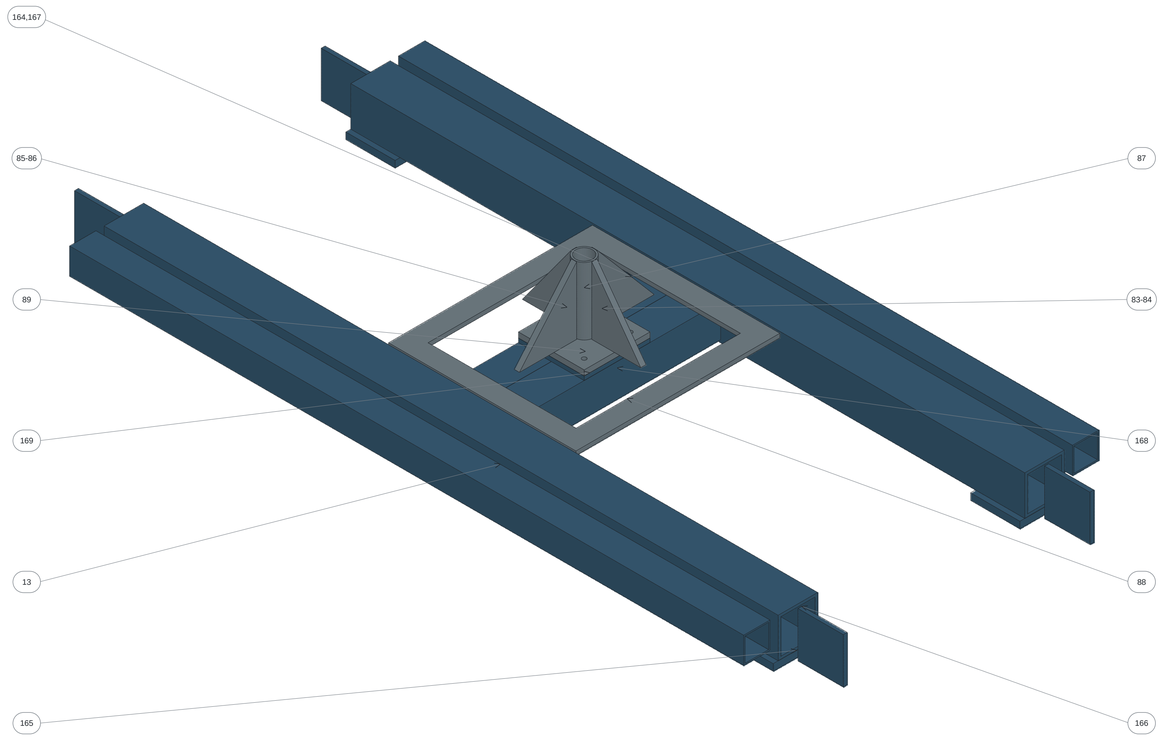

NOTAS DE FABRICACIÓN Y MONTAJE

1. Cuchilla piramidal fija de cuatro filos AISI304; chapas de filo t16 según lista de materiales.
2. Mástil, marco y travesaños forman un conjunto. Mantener posición centrada sobre salida.
3. Altura de punta Z = 3 230. El bigbag se desplaza con fondo a Z = 3 520.
4. Sustituir filos con equipo aislado, bolsa retirada y protección de acceso instalada.

Cotas en mm. ISO2768-m. Soldaduras según cuadro JF. Contornos: CAD/DXF.


TALADROS DE PIEZAS DEL CONJUNTO / COORDENADAS LOCALES mm / ORIGEN LOCAL

P89 T1: Ø13; X-70 Y-70 Z0; eje Z
P89 T2: Ø13; X70 Y-70 Z0; eje Z
P89 T3: Ø13; X-70 Y70 Z0; eje Z
P89 T4: Ø13; X70 Y70 Z0; eje Z


				REBABAR Y ROMPER ARISTAS	NO CAMBIAR LA ESCALA		REVISIÓN
SESUVECA DEL PERÚ							
	NOMBRE	FIRMA	FECHA			TÍTULO: Cortador y parrilla de apoyo de bolsa	
DIBUJ.	Javier Acevedo		16/10/26				
VERIF.							
APROB.							
FABR.							
CALID.				MATERIAL: SEGÚN LISTA DE MATERIALES		N.º DE DIBUJO EB-08	A1
PESO: SEGÚN CAD / lista de materiales				ESCALA: INDICADA		ESTACIÓN DE DESCARGA BIGBAG	HOJA 8 DE 17

Compuerta de descarga ensamblada

PLANTA ESCALA 1:5

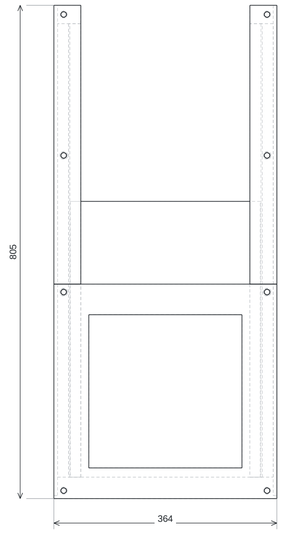


ALZADO ESCALA 1:2

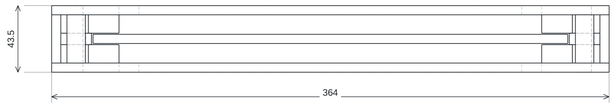


POS.	CANT.	PIEZA / MEDIDAS EN mm	MATERIAL / SUMINISTRO
95	1	Marco superior de compuerta; ancho 364; alto 350; espesor 6; taladros Ø9	ASTM A36 / Fabricar
96	1	Marco inferior de compuerta; ancho 364; alto 350; espesor 6; taladros Ø9	ASTM A36 / Fabricar
97	1	Placa deslizante de compuerta; ancho 310; alto 450; espesor 6	ASTM A36 / Fabricar
98	1	Guía superior de compuerta; ancho 44; alto 455; espesor 6; taladros Ø9	ASTM A36 / Fabricar
99	1	Guía superior de compuerta; ancho 44; alto 455; espesor 6; taladros Ø9	ASTM A36 / Fabricar
100	1	Guía inferior de compuerta; ancho 44; alto 455; espesor 6; taladros Ø9	ASTM A36 / Fabricar
101	1	Guía inferior de compuerta; ancho 44; alto 455; espesor 6; taladros Ø9	ASTM A36 / Fabricar
102-103	2	Barra separadora de compuerta; ancho 6; alto 800; espesor 31.5	ASTM A36 / Fabricar
104-105	2	Tira plástica de guía superior; ancho 20; alto 740; espesor 12	PE-UHMW1000 / ASTM D4020 / Fabricar
106-107	2	Tira plástica de guía inferior; ancho 20; alto 740; espesor 12	PE-UHMW1000 / ASTM D4020 / Fabricar
108-109	2	Tira plástica de guía lateral; ancho 20; alto 740; espesor 7.5; taladros Ø13	PE-UHMW1000 / ASTM D4020 / Fabricar
110	8	Separador tubular para perno; largo 31.5; pared 1.5; Ø exterior 12; Ø interior 9	ASTM A36 / Fabricar

ISOMÉTRICO A COLOR / REFERENCIA DE MONTAJE

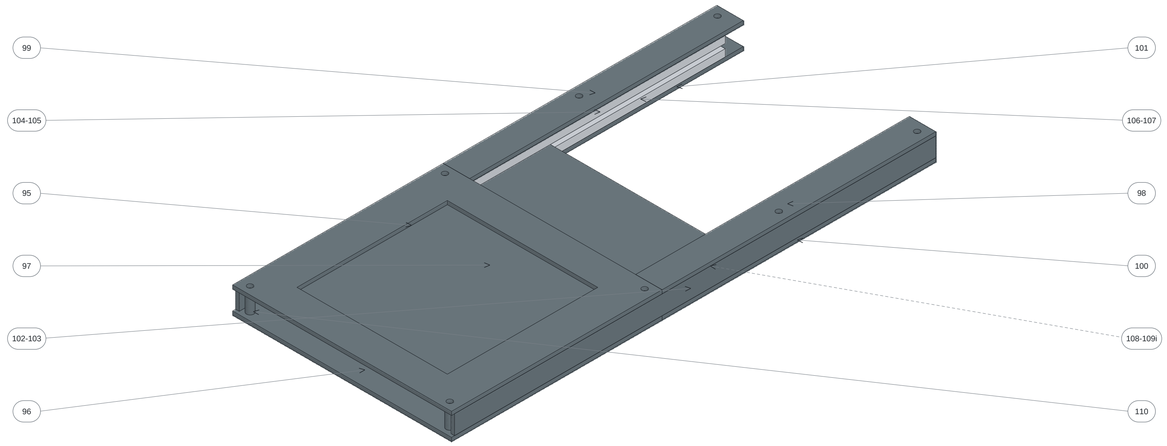

i = pieza interior; línea discontinua.

PLACAS DE COMPUERTA / POS. 95 / 96

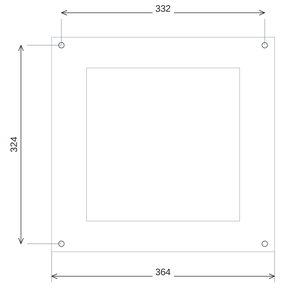

Planchas de acero 6 mm

Abertura 250 × 250

4 agujeros Ø9

Entre centros 332 × 324

Exterior 364 × 350

Medidas en mm. Vista ampliada de las placas; sin elementos de fijación.

NOTAS DE FABRICACIÓN Y MONTAJE

1. Hoja de cierre, guías y revestimientos se muestran en posición cerrada de referencia.
2. Accionamiento: cremallera y piñón con reducción manual; pasador cautivo de bloqueo.
3. Ajustar paralelismo de guías y comprobar recorrido completo antes del montaje de la guarda.
4. Conservar espesores de casquillos y UHMWPE del CAD; ajustar fijaciones manteniendo libre la corredera.

Cotas en mm. ISO2768-m. Soldaduras según cuadro JF. Contornos: CAD/DXF.

TALADROS DE PIEZAS DEL CONJUNTO / COORDENADAS LOCALES mm / ORIGEN LOCAL


P95 T1: Ø9; X-166 Y-162 Z0; eje Z
P95 T2: Ø9; X166 Y-162 Z0; eje Z
P95 T3: Ø9; X-166 Y162 Z0; eje Z
P95 T4: Ø9; X166 Y162 Z0; eje Z
P96 T1: Ø9; X-166 Y-162 Z0; eje Z
P96 T2: Ø9; X166 Y-162 Z0; eje Z
P96 T3: Ø9; X-166 Y162 Z0; eje Z
P96 T4: Ø9; X166 Y162 Z0; eje Z

P98 T1: Ø9; X6 Y-17.5 Z0; eje Z
P98 T2: Ø9; X6 Y212.5 Z0; eje Z
P99 T1: Ø9; X-6 Y-17.5 Z0; eje Z
P99 T2: Ø9; X-6 Y212.5 Z0; eje Z
P100 T1: Ø9; X6 Y-17.5 Z0; eje Z
P100 T2: Ø9; X6 Y212.5 Z0; eje Z
P101 T1: Ø9; X-6 Y-17.5 Z0; eje Z
P101 T2: Ø9; X-6 Y212.5 Z0; eje Z


				REBABAR Y ROMPER ARISTAS	NO CAMBIAR LA ESCALA	REVISIÓN
SESUVECA DEL PERÚ						
	NOMBRE	FIRMA	FECHA			TÍTULO: Compuerta de descarga ensamblada
DIBUJ.	Javier Acevedo		16/10/26			
VERIF.						
APROB.						
FABR.						
CALID.				MATERIAL: SEGÚN LISTA DE MATERIALES		N.º DE DIBUJO EB-09 / A1
PESO: SEGÚN CAD / lista de materiales				ESCALA: INDICADA		ESTACIÓN DE DESCARGA BIGBAG / HOJA 9 DE 17

Guarda, ensacado y captación

ALZADO ESCALA 1:15

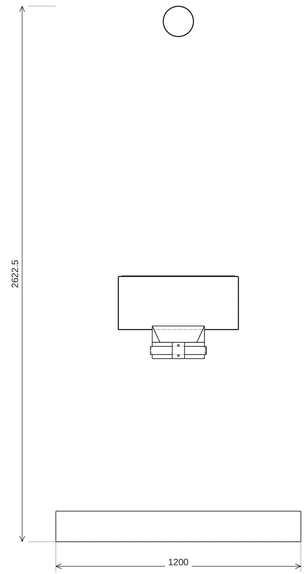


PLANTA ESCALA 1:15

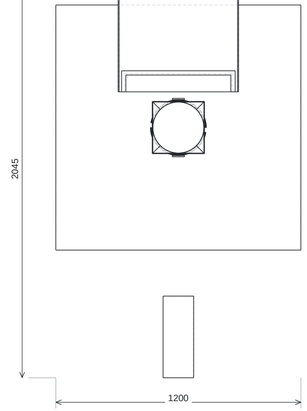

POS.	CANT.	PIEZA / MEDIDAS EN mm	MATERIAL / SUMINISTRO
111	1	Adaptador de salida cuadrada a redonda; alto 80; espesor 3; Ø interior 250; boca cuadrada 250	ASTM A36 / Fabricar
112	1	Tubo de salida de producto; largo 80; pared 3; Ø exterior 256; Ø interior 250	ASTM A36 / Fabricar
113	2	Abrazadera curva de sujeción del saco; ancho 402.3; alto 40; espesor 3; Ø exterior 274; Ø interior 268; R interior 134; R exterior 137; arco 170°	ASTM A36 / Fabricar
114	2	Banda de goma de abrazadera; ancho 268; alto 40; espesor 3; Ø exterior 268; Ø interior 262; R interior 131; R exterior 134; arco 170°	EPDM / Fabricar
115	2	Placa de soporte de abrazadera; ancho 60; alto 80; espesor 6; taladros Ø9	ASTM A36 / Fabricar
116	1	Saco de ensacado de 25–50 kg; ancho 380; alto 220; largo 766.5	Polipropileno tejido / Comprar
117	1	Balanza de plataforma 1200×1200, capacidad 2 t; ancho 1200; alto 1200; largo 150	Plataforma de pesaje completa / Comprar
120	1	Manguera de captación de polvo Ø150; Ø interior 150; manguera flexible para captación de polvo	Poliuretano disipativo con espiral metálica / Comprar
121	1	Cubierta doblada de protección de compuerta; ancho 590; alto 262; largo 645; espesor 2; R interior 3	ASTM A36 / Fabricar
122	1	Tapa inferior de protección de compuerta; ancho 590; alto 645; espesor 2	ASTM A36 / Fabricar
123	1	Tapa de extremo de protección de compuerta; ancho 586; alto 258; espesor 2; R esquinas 3	ASTM A36 / Fabricar
124	1	Empaque flexible de protección de compuerta; ancho 556; alto 103; espesor 2	EPDM disipativo / Fabricar


ISOMÉTRICO A COLOR / REFERENCIA DE MONTAJE

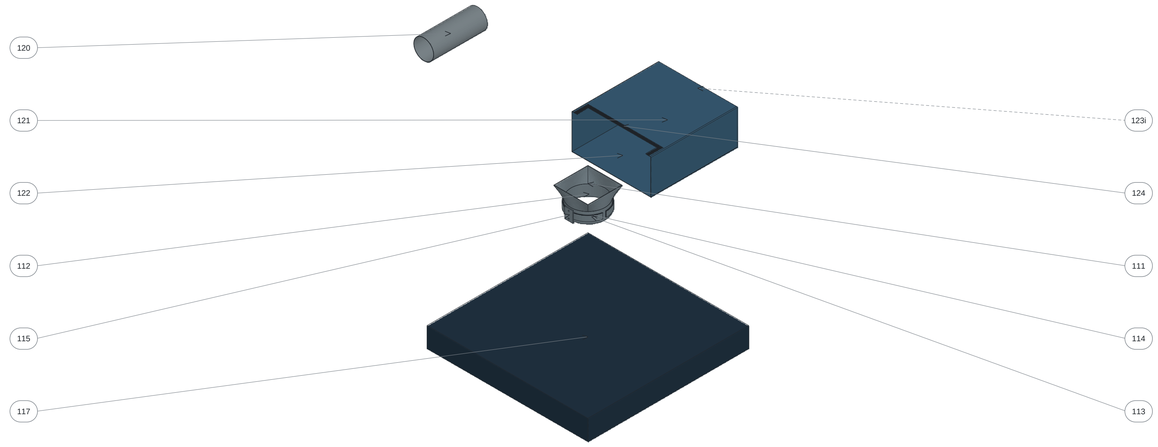

i = pieza interior; línea discontinua.

ABRAZADERA Y CAUCHO

POS.113 / 114

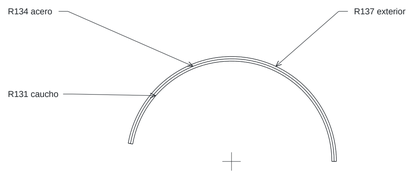


Arco 170°; ancho 40

Acero 3 mm; caucho 3 mm

Dos piezas de cada tipo. Radios en mm.

R3 interior

GUARDA ESCALA 1:5

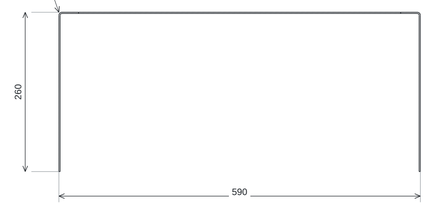

Radio interior de doblado R3

Plancha 2 mm

NOTAS DE FABRICACIÓN Y MONTAJE

1. Guarda cerrada de compuerta: envolvente final 590 x 645 x 262.
2. Cota superior de recinto protegido Z = 3 430; despeje nominal de traslado: 90.
3. Salida libre DN250; interfaz de saco y balanza de plataforma 1 200 x 1 200 / 2 t.
4. Captación DN150: 800 m3/h a 1 500 Pa en colector; balance de presión según memoria.
5. Conexiones desmontables para limpieza y mantenimiento. Protección contra polvo combustible según análisis del proyecto.

Cotas en mm. ISO2768-m. Soldaduras según cuadro JF. Contornos: CAD/DXF.

TALADROS DE PIEZAS DEL CONJUNTO / COORDENADAS LOCALES mm / ORIGEN LOCAL


P115 T1: Ø9; X0 Y-25 Z0; eje Z

P115 T2: Ø9; X0 Y25 Z0; eje Z

				REBABAR Y ROMPER ARISTAS	NO CAMBIAR LA ESCALA	REVISIÓN
SESUVECA DEL PERÚ						
	NOMBRE	FIRMA	FECHA			TÍTULO: Guarda, ensacado y captación
DIBUJ.	Javier Acevedo		16/10/26			
VERIF.						
APROB.						
FABR.						
CALID.				MATERIAL: SEGÚN LISTA DE MATERIALES		N.º DE DIBUJO EB-10 / A1
PESO: SEGÚN CAD / lista de materiales				ESCALA: INDICADA		ESTACIÓN DE DESCARGA BIGBAG / HOJA 10 DE 17


Carro, suspensión y traba de posición

ALZADO ESCALA 1:5

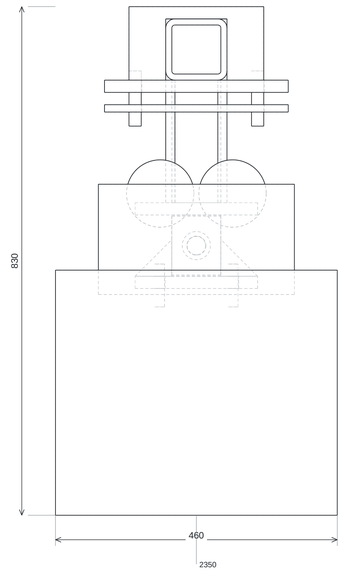


REFERENCIA X (mm)

PERFIL ESCALA 1:8

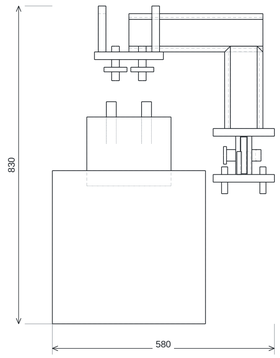

POS.	CANT.	PIEZA / MEDIDAS EN mm	MATERIAL / SUMINISTRO
90	1	Tecle eléctrico KITO SHER2M020IS-IS de 2 t; Conjunto KITO SHER2M020IS-IS, capacidad 2 t	Conjunto KITO SHER2M020IS-IS / Comprar
91	1	Carro motorizado del tecle KITO; Conjunto KITO SHER2M020IS-IS, capacidad 2 t	Conjunto KITO SHER2M020IS-IS / Comprar
92	1	Cadena de carga del tecle KITO; Repuesto original del conjunto KITO SHER2M020IS-IS de 2 t	Conjunto KITO SHER2M020IS-IS / Comprar
93	1	Bolsa bigbag de 1 t; ancho 1000; alto 1000; largo 1000	Polipropileno tejido / Comprar
94	4	Asa de bolsa bigbag; Asas integrales de la bolsa bigbag de 1 t	Polipropileno tejido / Comprar
128	8	Arandela M16; largo 3; pared 6; Ø exterior 30; Ø interior 18	Acero 200HV / ISO7089 / Comprar
129	8	Tuerca M16; Rosca M16; clase 8	Acero clase 8 / ISO898-2 / Comprar
131	1	Placa de apoyo de traba del carro; ancho 300; alto 180; espesor 20; taladros Ø22	ASTM A36 / Fabricar
132	2	Placa de refuerzo del ala de viga; ancho 300; alto 60; espesor 12; taladros Ø22	ASTM A36 / Fabricar
133	1	Brazo de traba del carro; ancho 100; alto 100; largo 350; pared 10	S355NH / EN10210-1 / Fabricar
134	1	Poste de traba del carro; ancho 100; alto 100; largo 215; pared 10	S355NH / EN10210-1 / Fabricar
135	1	Placa de apoyo del pasador; ancho 200; alto 160; espesor 20	ASTM A36 / Fabricar
136	2	Placa exterior de traba del carro; ancho 80; alto 100; espesor 12; taladros Ø31	ASTM A36 / Fabricar
137	1	Placa central de traba del carro; ancho 80; alto 96; espesor 16; taladros Ø31	ASTM A36 / Fabricar
138	1	Placa de unión al carro; ancho 200; alto 160; espesor 20; taladros Ø18	ASTM A36 / Fabricar
139	2	Placa de apoyo del brazo; ancho 220; alto 120; espesor 20	ASTM A36 / Fabricar
140	2	Refuerzo triangular de traba; ancho 60; alto 60; espesor 12	ASTM A36 / Fabricar
141	1	Pasador de bloqueo del carro; largo 90; Ø exterior 30; taladros Ø4.5	C45E+QT / EN ISO683-1 / Fabricar
142	1	Cabeza del pasador; largo 8; Ø exterior 46	ASTM A36 / Fabricar
143	1	Seguro tipo R del pasador; largo 38; Ø exterior 3	Acero para resorte / EN10270-1 / Comprar
144	1	Placa para sujetar cable del pasador; ancho 40; alto 12; espesor 3; taladros Ø4	ASTM A36 / Fabricar
145-147	3	Cable de retención del pasador; Cable Ø3; largo total mínimo 350; una sola pieza	AISI316 / EN12385-4 / Fabricar
148	4	Perno M20 de traba del carro; M20 × 90; clase 8.8	Acero clase 8.8 / ISO898-1 / Comprar
149	8	Arandela M20; largo 3; pared 7.5; Ø exterior 37; Ø interior 22	Acero 200HV / ISO7089 / Comprar
150	8	Tuerca M20; Rosca M20; clase 8	Acero clase 8 / ISO898-2 / Comprar
151	4	Espárrago M16 de unión al carro; M16 × 70; clase 8.8	Acero clase 8.8 / ISO898-1 / Comprar
152	4	Rueda del carro KITO; Repuesto original del conjunto KITO SHER2M020IS-IS de 2 t	Conjunto KITO SHER2M020IS-IS / Comprar

ISOMÉTRICO A COLOR / REFERENCIA DE MONTAJE

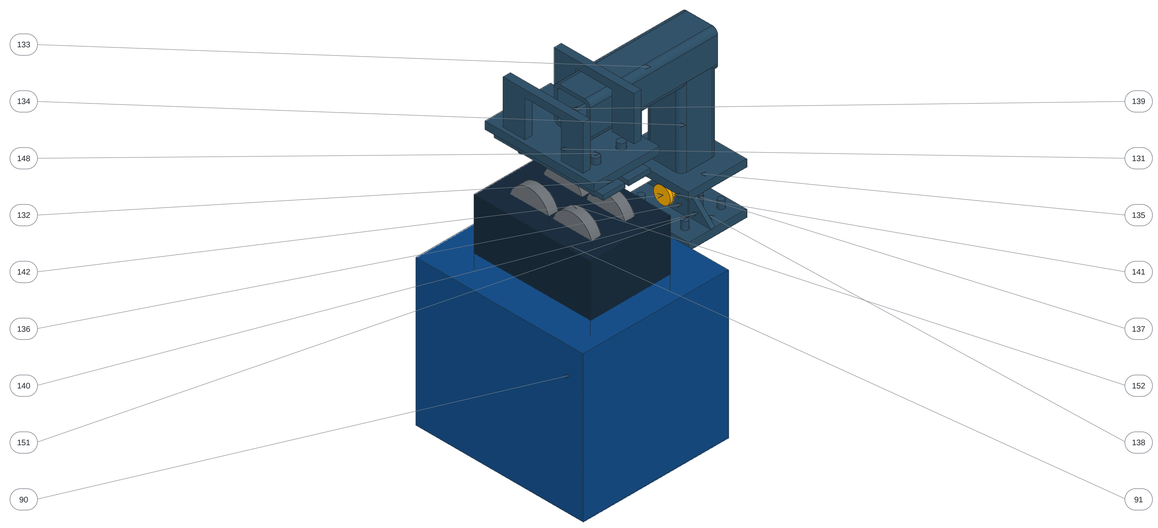

NOTAS DE FABRICACIÓN Y MONTAJE

1. Referencia comercial KITO SHER2M020IS-IS / 2 t; C de catálogo = 475.
2. Mantener el conjunto comercial de tecle y carro según especificación de compra.
3. Pasador cautivo D30 Fy >=355 MPa; dos orejas t12 y placa receptora t16; taladros D31.
4. Inserción únicamente con carro detenido. Inhibir traslación con pasador insertado.
5. Patrones de fijación TC y tolerancias de montaje según detalle / CAD.
6. Brazo y poste de traba100×100×10 S355NH: extremos a placas20 y encuentro brazo/poste con penetración completa10 mm; garganta efectiva mínima9 mm.
7. Brazo350 mm. Poste: reserva215 mm; contornear extremo al radio del brazo. Altura nominal200 mm; eje de poste y pasador Y300.

Cotas en mm. ISO2768-m. Soldaduras según cuadro JF. Contornos: CAD/DXF.


TALADROS DE PIEZAS DEL CONJUNTO / COORDENADAS LOCALES mm / ORIGEN LOCAL

P131 T1: Ø22; X-100 Y-35 Z0; eje Z
P131 T2: Ø22; X-100 Y35 Z0; eje Z
P131 T3: Ø22; X100 Y-35 Z0; eje Z
P131 T4: Ø22; X100 Y35 Z0; eje Z
P132 T1: Ø22; X-100 Y0 Z0; eje Z
P132 T2: Ø22; X100 Y0 Z0; eje Z
P136 T1: Ø31; X0 Y0 Z0; eje Z
P137 T1: Ø31; X0 Y0 Z0; eje Z
P138 T1: Ø18; X-60 Y-50 Z0; eje Z
P138 T2: Ø18; X-60 Y50 Z0; eje Z
P138 T3: Ø18; X60 Y-50 Z0; eje Z
P138 T4: Ø18; X60 Y50 Z0; eje Z
P141 B1: Ø4.5; X0 Y16 Z78; eje Y
P144 T1: Ø4; X12 Y0 Z0; eje Z

				REBABAR Y ROMPER ARISTAS	NO CAMBIAR LA ESCALA	REVISIÓN
SESUVECA DEL PERÚ						
	NOMBRE	FIRMA	FECHA			TÍTULO: Carro, suspensión y traba de posición
DIBUJ.	Javier Acevedo		16/10/26			
VERIF.						
APROB.						
FABR.						
CALID.				MATERIAL: SEGÚN LISTA DE MATERIALES		N.º DE DIBUJO EB-11 / A1
PESO: SEGÚN CAD / lista de materiales				ESCALA: INDICADA		ESTACIÓN DE DESCARGA BIGBAG / HOJA 11 DE 17


Plataforma de acceso ensamblada

PLANTA ESCALA 1:8

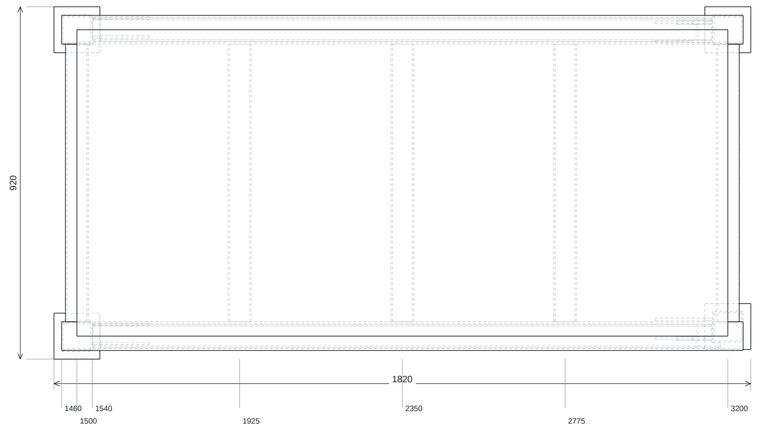


REFERENCIA X (mm)

ALZADO ESCALA 1:15

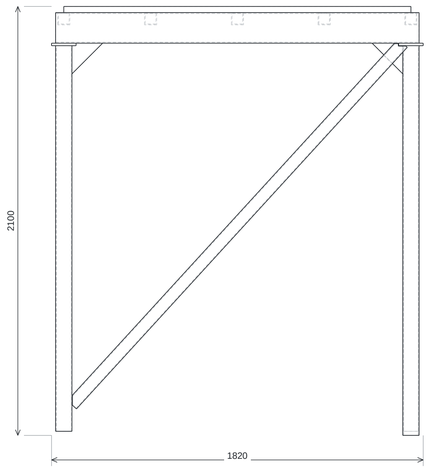

POS.	CANT.	PIEZA / MEDIDAS EN mm	MATERIAL / SUMINISTRO
14	3	Tramo de tubo cuadrado; ancho 80; alto 80; largo 1888; pared 4	ASTM A500 Gr.B / Fabricar
15	1	Tramo de tubo cuadrado; ancho 80; alto 80; largo 1908; pared 4	ASTM A500 Gr.B / Fabricar
16	2	Tramo de tubo rectangular; ancho 75; alto 150; largo 1780; pared 5	ASTM A500 Gr.B / Fabricar
17	5	Tramo de tubo cuadrado; ancho 60; alto 60; largo 725; pared 4	ASTM A500 Gr.B / Fabricar
64	4	Tapa de columna de acceso; ancho 120; alto 120; espesor 12	ASTM A36 / Fabricar
65	8	Refuerzo triangular de acceso; ancho 150; alto 150; espesor 6	ASTM A36 / Fabricar
118	1	Piso de rejilla de plataforma; ancho 1700; alto 800; espesor 30	ASTM A36 galvanizado / Comprar
188-189	2	Tramo de tubo cuadrado; ancho 60; alto 60; largo 2399.44; pared 4	ASTM A500 Gr.B / Fabricar

ISOMÉTRICO A COLOR / REFERENCIA DE MONTAJE

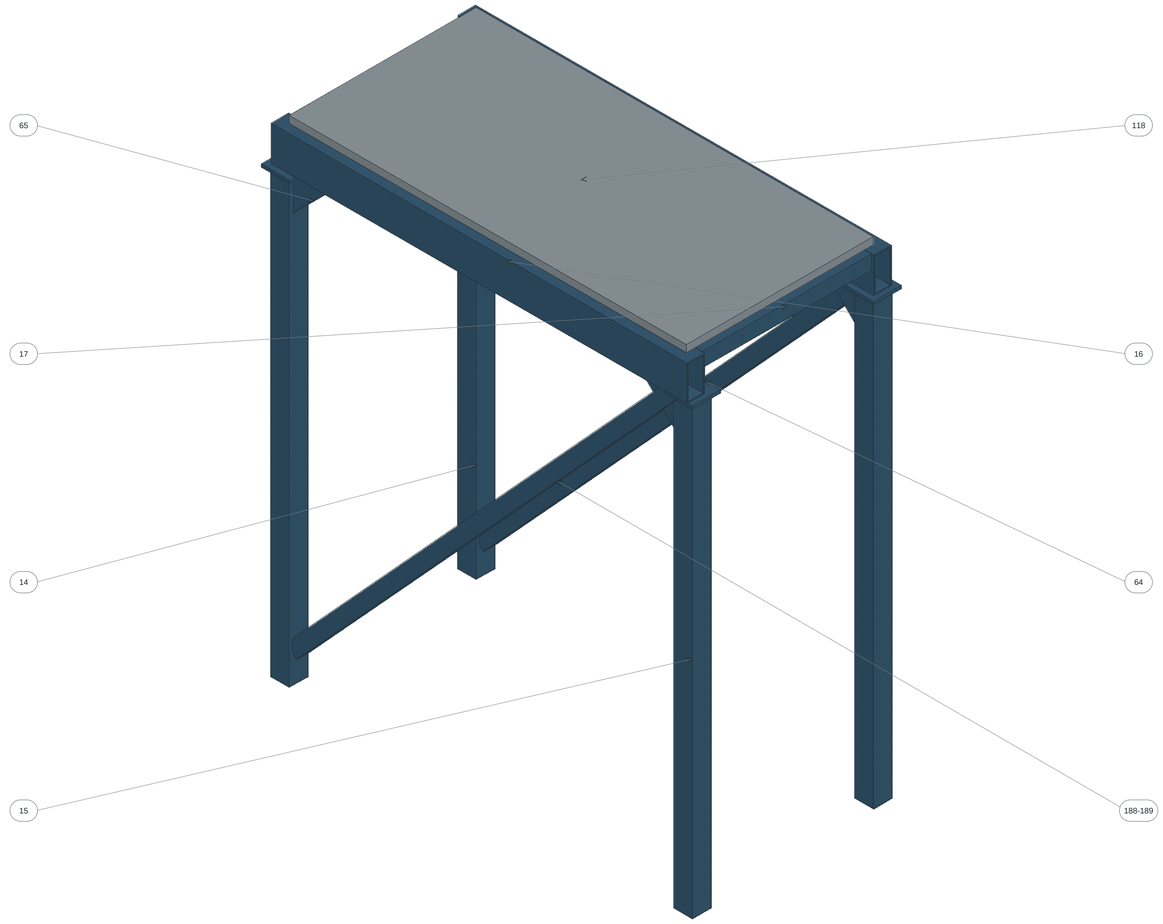

NOTAS DE FABRICACIÓN Y MONTAJE


1. Bastidor, cuatro postes y apoyos de rejilla forman el conjunto de plataforma.
2. No soldar la rejilla comercial a través de superficies de drenaje; fijaciones según compra.
3. Unión J01 con escalera según cuadro de juntas. Montaje en campo mediante uniones desmontables.

Cotas en mm. ISO2768-m. Soldaduras según cuadro JF. Contornos: CAD/DXF.

				REBABAR Y ROMPER ARISTAS	NO CAMBIAR LA ESCALA	REVISIÓN
SESUVECA DEL PERÚ						
	NOMBRE	FIRMA	FECHA			TÍTULO: Plataforma de acceso ensamblada
DIBUJ.	Javier Acevedo		16/10/26			
VERIF.						
APROB.						
FABR.						
CALID.				MATERIAL: SEGÚN LISTA DE MATERIALES		N.º DE DIBUJO EB-12 / A1
PESO: SEGÚN CAD / lista de materiales				ESCALA: INDICADA		ESTACIÓN DE DESCARGA BIGBAG / HOJA 12 DE 17


Escalera y desembarco ensamblados

ALZADO ESCALA 1:15

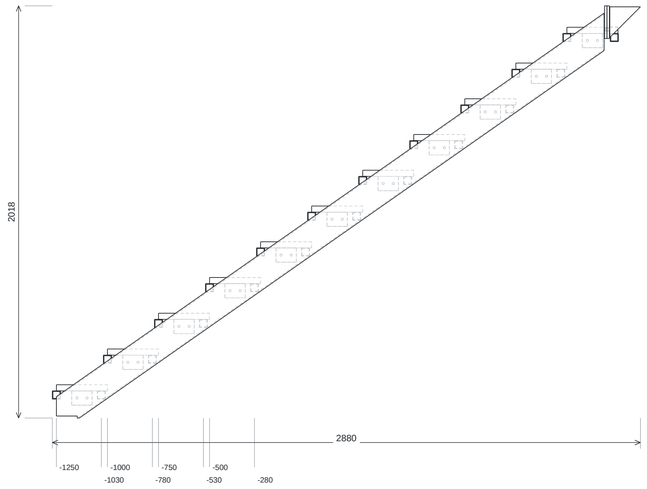


REFERENCIA X (mm)

PLANTA ESCALA 1:10

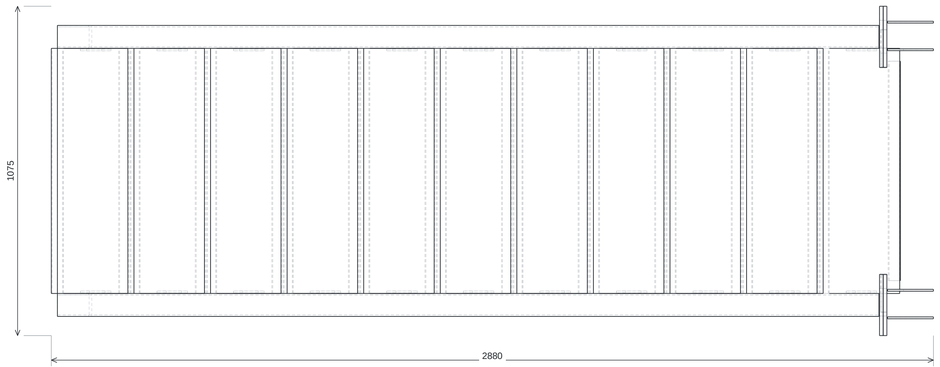

POS.	CANT.	PIEZA / MEDIDAS EN mm	MATERIAL / SUMINISTRO
18,192	22	Tramo de tubo cuadrado; ancho 40; alto 40; largo 800; pared 3	ASTM A500 Gr.B / Fabricar
70,193-194	4	Refuerzo triangular de diagonal de tolva; ancho 150; alto 150; espesor 6	ASTM A36 / Fabricar
71	22	Placa de unión de diagonal de tolva; ancho 100; alto 70; espesor 6; taladros Ø11	ASTM A36 / Fabricar
119	11	Peldaño de rejilla; ancho 250; alto 800; espesor 30	ASTM A36 galvanizado / Comprar
190-191	2	Tramo de tubo rectangular; ancho 75; alto 150; largo 3356.8; pared 5	ASTM A500 Gr.B / Fabricar
211,213	2	Placa de extremo de refuerzo; ancho 200; alto 160; espesor 12; taladros Ø18	ASTM A36 / Fabricar
212,214	2	Placa de apoyo de refuerzo; ancho 200; alto 160; espesor 12; taladros Ø18	ASTM A36 / Fabricar

ISOMÉTRICO A COLOR / REFERENCIA DE MONTAJE

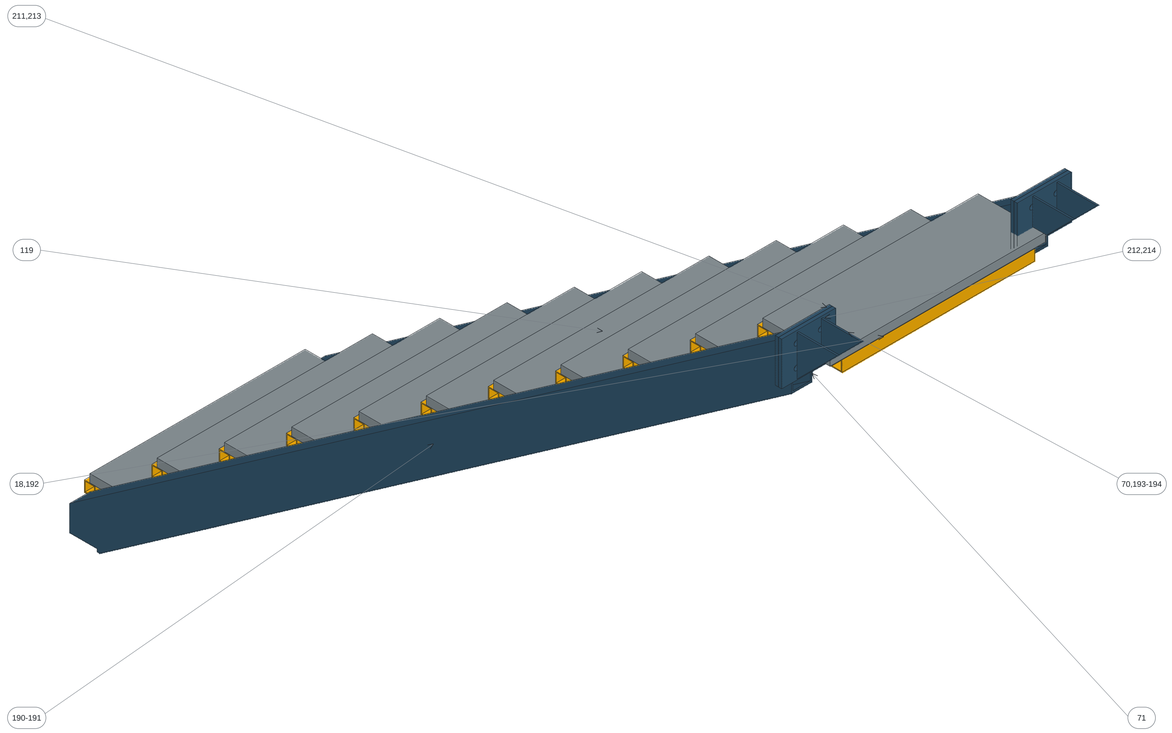

NOTAS DE FABRICACIÓN Y MONTAJE

1. Dos zancas RHS150x75x5 con recorte final de desembarco; peldaños según lista de materiales.
2. Cortar según lista y ensamblar en útil sobre los ejes indicados.
3. Preparaciones J01 / J02 y extremos con luz 2 mm según las juntas indicadas; no soldar las holguras LUZ.

Cotas en mm. ISO2768-m. Soldaduras según cuadro JF. Contornos: CAD/DXF.


TALADROS DE PIEZAS DEL CONJUNTO / COORDENADAS LOCALES mm / ORIGEN LOCAL

P71 T1: Ø11; X-25 Y0 Z0; eje Z
P71 T2: Ø11; X25 Y0 Z0; eje Z
P211 T1: Ø18; X-45 Y-40 Z0; eje Z
P211 T2: Ø18; X-45 Y40 Z0; eje Z
P211 T3: Ø18; X45 Y-40 Z0; eje Z
P211 T4: Ø18; X45 Y40 Z0; eje Z
P212 T1: Ø18; X-45 Y-40 Z0; eje Z
P212 T2: Ø18; X-45 Y40 Z0; eje Z
P212 T3: Ø18; X45 Y-40 Z0; eje Z
P212 T4: Ø18; X45 Y40 Z0; eje Z
P213 T1: Ø18; X-45 Y-40 Z0; eje Z
P213 T2: Ø18; X-45 Y40 Z0; eje Z
P213 T3: Ø18; X45 Y-40 Z0; eje Z
P213 T4: Ø18; X45 Y40 Z0; eje Z
P214 T1: Ø18; X-45 Y-40 Z0; eje Z
P214 T2: Ø18; X-45 Y40 Z0; eje Z
P214 T3: Ø18; X45 Y-40 Z0; eje Z
P214 T4: Ø18; X45 Y40 Z0; eje Z

				REBABAR Y ROMPER ARISTAS	NO CAMBIAR LA ESCALA	REVISIÓN
SESUVECA DEL PERÚ						
	NOMBRE	FIRMA	FECHA			TÍTULO: Escalera y desembarco ensamblados
DIBUJ.	Javier Acevedo		16/10/26			
VERIF.						
APROB.						
FABR.						
CALID.				MATERIAL: SEGÚN LISTA DE MATERIALES		N.º DE DIBUJO EB-13 / A1
PESO: SEGÚN CAD / lista de materiales				ESCALA: INDICADA		ESTACIÓN DE DESCARGA BIGBAG / HOJA 13 DE 17


Barandas, pasamanos y rodapiés

ALZADO ESCALA 1:20

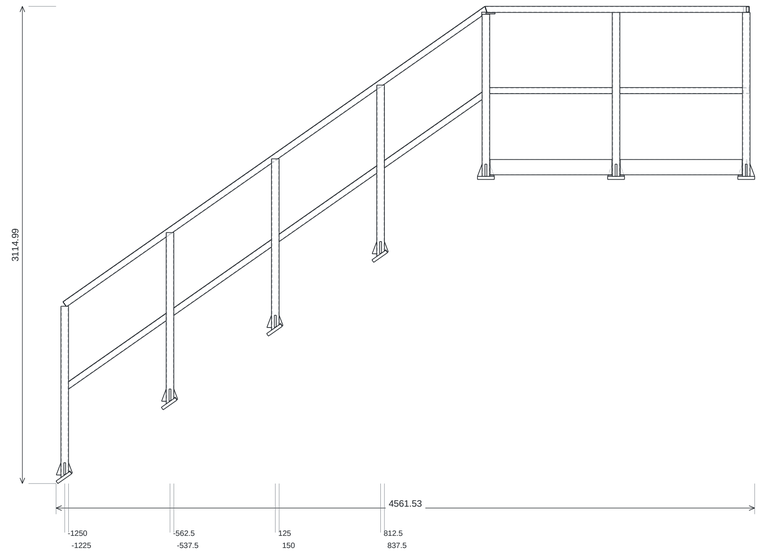


REFERENCIA X (mm)

PLANTA ESCALA 1:15

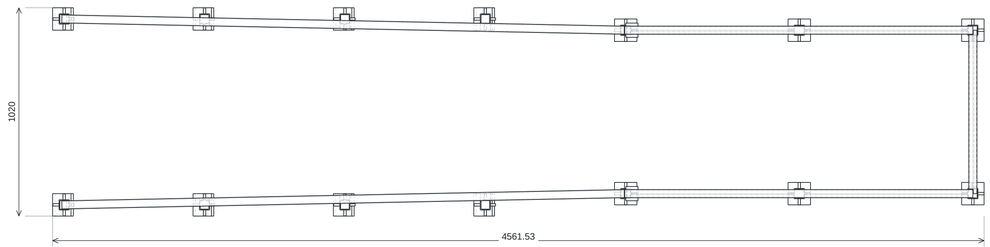

POS.	CANT.	PIEZA / MEDIDAS EN mm	MATERIAL / SUMINISTRO
18,202	5	Tramo de tubo cuadrado; ancho 40; alto 40; largo 800; pared 3	ASTM A500 Gr.B / Fabricar
19,180	6	Tramo de tubo cuadrado; ancho 50; alto 50; largo 1070; pared 4	ASTM A500 Gr.B / Fabricar
20-27	8	Tramo de tubo cuadrado; ancho 40; alto 40; largo 778.27; pared 3	ASTM A500 Gr.B / Fabricar
28	1	Tramo de tubo cuadrado; ancho 40; alto 40; largo 750; pared 3	ASTM A500 Gr.B / Fabricar
31,203-205,208-210	8	Tramo de tubo cuadrado; ancho 50; alto 50; largo 1101.27; pared 4	ASTM A500 Gr.B / Fabricar
72	14	Placa base de poste de baranda; ancho 110; alto 110; espesor 20	ASTM A36 / Fabricar
73,215-248	56	Refuerzo triangular de poste de baranda; ancho 30; alto 80; espesor 12	ASTM A36 / Fabricar
178-179	2	Tramo de tubo cuadrado; ancho 40; alto 40; largo 1700; pared 3	ASTM A500 Gr.B / Fabricar
181	2	Tapa de unión de baranda; ancho 60; alto 70; espesor 8	ASTM A36 / Fabricar
199,206	2	Tramo de tubo cuadrado; ancho 40; alto 40; largo 3357.25; pared 3	ASTM A500 Gr.B / Fabricar
200,207	2	Banda de borde de plataforma; ancho 1700; alto 100; espesor 5	ASTM A36 / Fabricar
201	1	Banda de borde de plataforma; ancho 800; alto 100; espesor 5	ASTM A36 / Fabricar

ISOMÉTRICO A COLOR / REFERENCIA DE MONTAJE

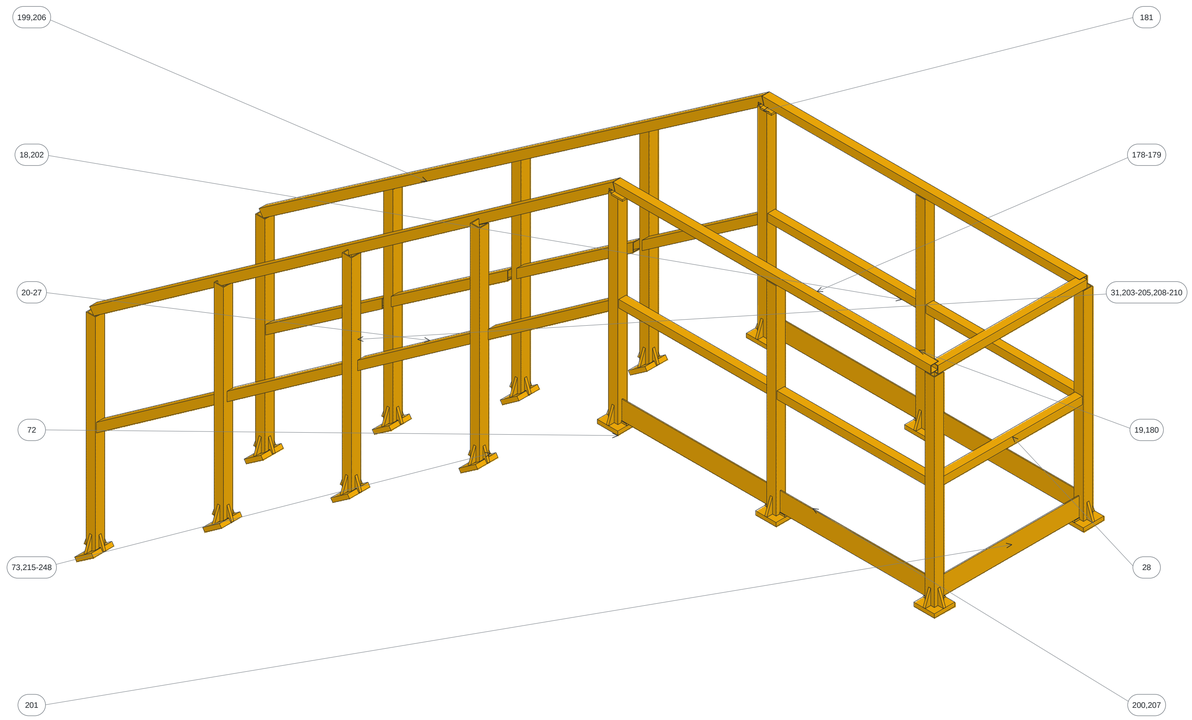

NOTAS DE FABRICACIÓN Y MONTAJE


1. Rodapiés t5; postes SHS50x50x4; pasamanos SHS40x40x3.
2. Conservar ingletes reales y tapas de transición 60x70x8 en extremos superiores.
3. Uniones a pared de 3 mm: PJP a2 según preparación y cuadro de juntas.
4. Soldar en taller según cuadro; eliminar bordes cortantes y asegurar continuidad del pasamanos.

Cotas en mm. ISO2768-m. Soldaduras según cuadro JF. Contornos: CAD/DXF.

				REBABAR Y ROMPER ARISTAS	NO CAMBIAR LA ESCALA		REVISIÓN
SESUVECA DEL PERÚ							
	NOMBRE	FIRMA	FECHA			TÍTULO: Barandas, pasamanos y rodapiés	
DIBUJ.	Javier Acevedo		16/10/26				
VERIF.							
APROB.							
FABR.							
CALID.				MATERIAL: SEGÚN LISTA DE MATERIALES		N.º DE DIBUJO EB-14	A1
PESO: SEGÚN CAD / lista de materiales				ESCALA: INDICADA		ESTACIÓN DE DESCARGA BIGBAG	HOJA 14 DE 17


Cruceta de izaje 2 t ensamblada

PLANTA ESCALA 1:8

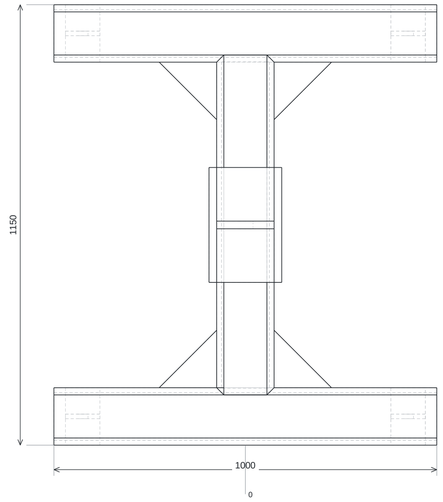


REFERENCIA X (mm)

ALZADO ESCALA 1:4

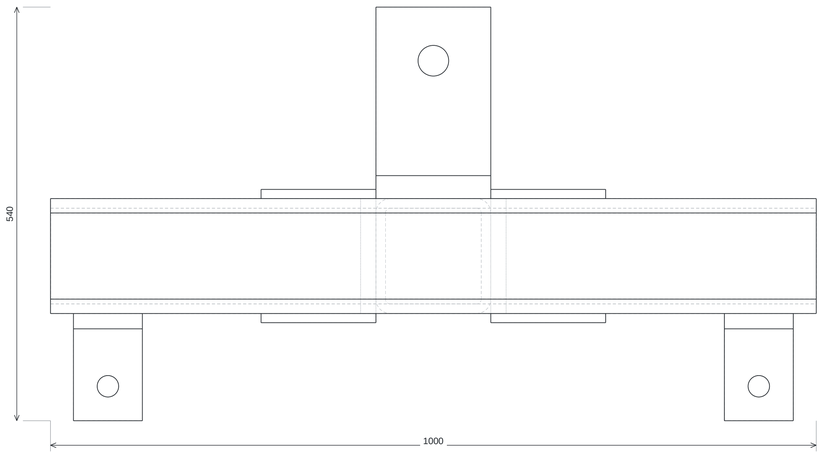

POS.	CANT.	PIEZA / MEDIDAS EN mm	MATERIAL / SUMINISTRO
29	2	Tramo de tubo cuadrado; ancho 150; alto 150; largo 1000; pared 12.5	S355NH / EN10210-1 / Fabricar
30	1	Tramo de tubo cuadrado; ancho 150; alto 150; largo 850; pared 12.5	S355NH / EN10210-1 / Fabricar
74	1	Placa central para levantar cruceta; ancho 150; alto 220; espesor 20; taladros Ø40	ASTM A36 / Fabricar
75	4	Placa extrema para sujetar asa; ancho 90; alto 120; espesor 12; taladros Ø28	ASTM A36 / Fabricar
76	4	Placa de refuerzo de enganche; ancho 90; alto 150; espesor 20	ASTM A36 / Fabricar
77	8	Refuerzo triangular de cruceta; ancho 150; alto 150; espesor 12	ASTM A36 / Fabricar
78	1	Placa superior de cruceta; ancho 150; alto 300; espesor 30	ASTM A36 / Fabricar
79	2	Placa lateral de cruceta; ancho 300; alto 150; espesor 20	ASTM A36 / Fabricar

ISOMÉTRICO A COLOR / REFERENCIA DE MONTAJE

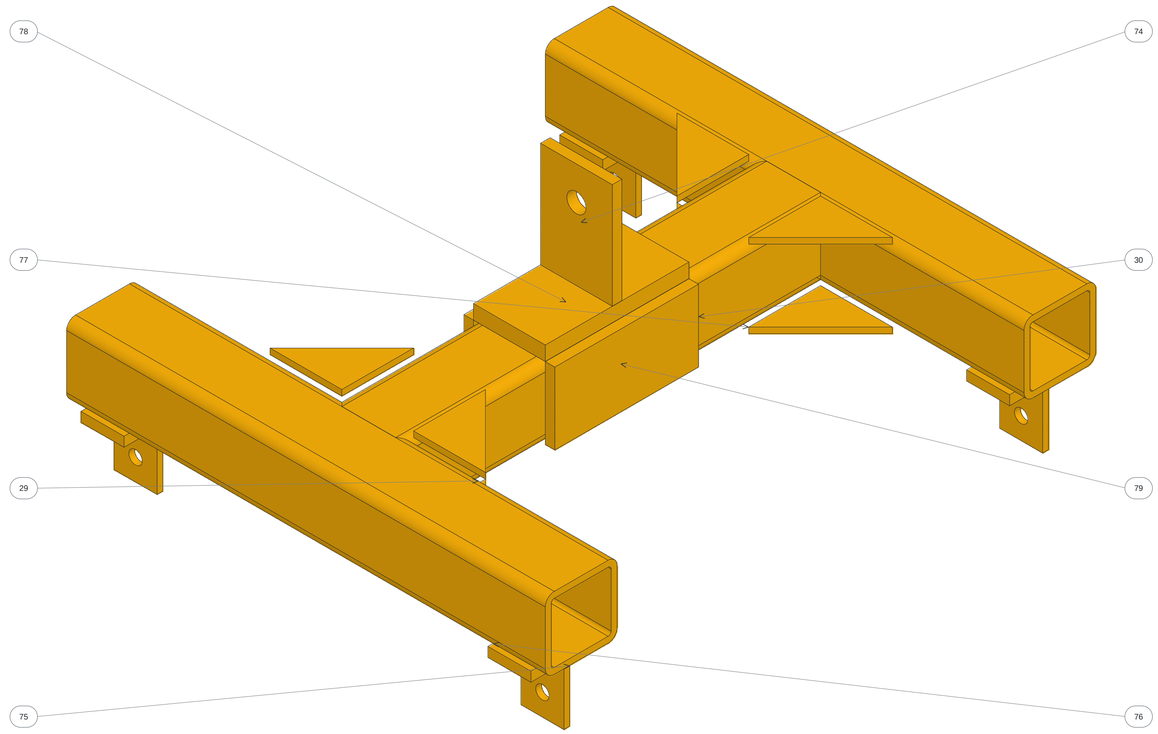

NOTAS DE FABRICACIÓN Y MONTAJE

1. Capacidad nominal 2 000 kg; 125 000 ciclos; Categoría B / Servicio Clase 2.
2. Tubos comerciales Celsius150×150×12.5 S355NH; placas y herrajes según lista.
3. Mantener reparto y geometría de toma del cálculo; identificación indeleble de capacidad y trazabilidad.
4. Ejecutar inspección y prueba de carga según protocolo antes de la puesta en servicio.
5. Tubo central: reserva de corte887.5 mm; luz entre caras850 mm. Contornear ambos extremos al radio real del tubo transversal; soldar todo el perímetro con filete6 mm.
6. Radios nominales R18.75 exterior y R6.25 interior. Acero S355NH con certificado3.1; conservar garganta y contorno de soldaduras indicados.
7. Placas laterales300×150 y respaldos90×150: dos cordones verticales de filete6×98.5 efectivos, centrados en altura, en sus bordes reales. Terminar antes de los radios; sin cordones horizontales sobre las esquinas.

Cotas en mm. ISO2768-m. Soldaduras según cuadro JF. Contornos: CAD/DXF.

TALADROS DE PIEZAS DEL CONJUNTO / COORDENADAS LOCALES mm / ORIGEN LOCAL

P74 T1: Ø40; X0 Y150 Z0; eje Z

P75 T1: Ø28; X0 Y75 Z0; eje Z

				REBABAR Y ROMPER ARISTAS	NO CAMBIAR LA ESCALA		REVISIÓN
SESUVECA DEL PERÚ							
	NOMBRE	FIRMA	FECHA			TÍTULO: Cruceta de izaje 2 t ensamblada	
DIBUJ.	Javier Acevedo		16/10/26				
VERIF.							
APROB.							
FABR.							
CALID.				MATERIAL: SEGÚN LISTA DE MATERIALES		N.º DE DIBUJO EB-15	A1
PESO: SEGÚN CAD / lista de materiales				ESCALA: INDICADA		ESTACIÓN DE DESCARGA BIGBAG	HOJA 15 DE 17

Uniones de fabricación / Cuadro 1 de 2

ID	MIEMBRO	SOPORTE	TIPO	a mm	L mm	CENTRO GLOBAL X/Y/Z mm	EJECUCIÓN
JF-001	BRL-A--1	COL-0--1	LUZ	-	-	POR MIEMBRO / SOPORTE	NO SOLDAR / LUZ 2
JF-002	BRL-A--1	COL-3.2--1	LUZ	-	-	POR MIEMBRO / SOPORTE	NO SOLDAR / LUZ 2
JF-003	BRL-B--1	COL-0--1	LUZ	-	-	POR MIEMBRO / SOPORTE	NO SOLDAR / LUZ 2
JF-004	BRL-B--1	COL-3.2--1	LUZ	-	-	POR MIEMBRO / SOPORTE	NO SOLDAR / LUZ 2
JF-005	KNE--1	COL-0--1	LUZ	-	-	POR MIEMBRO / SOPORTE	NO SOLDAR / LUZ 2
JF-006	BRL-A-1	COL-0-1	LUZ	-	-	POR MIEMBRO / SOPORTE	NO SOLDAR / LUZ 2
JF-007	BRL-A-1	COL-3.2-1	LUZ	-	-	POR MIEMBRO / SOPORTE	NO SOLDAR / LUZ 2
JF-008	BRL-B-1	COL-0-1	LUZ	-	-	POR MIEMBRO / SOPORTE	NO SOLDAR / LUZ 2
JF-009	BRL-B-1	COL-3.2-1	LUZ	-	-	POR MIEMBRO / SOPORTE	NO SOLDAR / LUZ 2
JF-010	KNE-1	COL-0-1	LUZ	-	-	POR MIEMBRO / SOPORTE	NO SOLDAR / LUZ 2
JF-011	PBRACE-1.1	PPOST-1.5-1.1	CJP	3.72	173.92	1542 / 1300 / 181.8	TALLER / WPS
JF-012	PBRACE-1.1	PPOST-3.2-1.125	CJP	3.72	115.05	3161.3 / 1306.2 / 1883.7	TALLER / WPS
JF-013	PBRACE-1.9	PPOST-1.5-1.9	CJP	3.72	173.92	1542 / 2100 / 181.8	TALLER / WPS
JF-014	PBRACE-1.9	PPOST-3.2-1.9	CJP	3.72	94.83	3158 / 2106.7 / 1880.9	TALLER / WPS
JF-015	STRING-1.1	BASE_ACCESO_STRING-1.1	CJP	4.65	224	-1194.4 / 1262.5 / 21.6	TALLER / WPS
JF-016	STRING-1.9	BASE_ACCESO_STRING-1.9	CJP	4.65	224	-1194.4 / 2137.5 / 21.6	TALLER / WPS
JF-017	STEP-11-1.47	PPOST-1.5-1.1	CJP	2.79	148	1482 / 1342 / 1875	TALLER / WPS
JF-018	STEP-11-1.47	PPOST-1.5-1.9	CJP	2.79	148	1482 / 2058 / 1875	TALLER / WPS
JF-019	KNE--1	TRA-0	CJP	3.72	156.71	0 / -381 / 5498	TALLER / WPS
JF-020	KNE-1	TRA-0	CJP	3.72	156.71	-0 / 381 / 5498	TALLER / WPS
JF-021	BRL-A--1	TIE--1-0.15	LUZ	-	-	POR MIEMBRO / SOPORTE	NO SOLDAR / LUZ 2
JF-022	BRL-B--1	TIE--1-0.15	LUZ	-	-	POR MIEMBRO / SOPORTE	NO SOLDAR / LUZ 2
JF-023	TIE--1-0.15	U02_COLLARX_0_1	CJP	3.72	224	89 / -1000 / 150	TALLER / WPS
JF-024	TIE--1-0.15	BRT_COLLARX_-1_0.15_-1	CJP	3.72	224	3111 / -1000 / 150	TALLER / WPS
JF-025	BRL-A--1	TIE--1-4.79	LUZ	-	-	POR MIEMBRO / SOPORTE	NO SOLDAR / LUZ 2
JF-026	BRL-B--1	TIE--1-4.79	LUZ	-	-	POR MIEMBRO / SOPORTE	NO SOLDAR / LUZ 2
JF-027	TIE--1-4.79	BRT_COLLARX_-1_5.338_-1	CJP	3.72	224	3111 / -1000 / 5430	TALLER / WPS
JF-028	BRL-A--1	U02_COLLARX_0_1	LUZ	-	-	POR MIEMBRO / SOPORTE	NO SOLDAR / LUZ 2
JF-029	BRL-A--1	BRT_COLLARX_-1_5.338_-1	LUZ	-	-	POR MIEMBRO / SOPORTE	NO SOLDAR / LUZ 2
JF-030	BRL-B--1	BRT_COLLARX_-1_0.15_-1	LUZ	-	-	POR MIEMBRO / SOPORTE	NO SOLDAR / LUZ 2
JF-031	KNE--1	U02_COLLARY_8_1	LUZ	-	-	POR MIEMBRO / SOPORTE	NO SOLDAR / LUZ 2
JF-032	BRL-A-1	TIE-1-0.15	LUZ	-	-	POR MIEMBRO / SOPORTE	NO SOLDAR / LUZ 2
JF-033	BRL-B-1	TIE-1-0.15	LUZ	-	-	POR MIEMBRO / SOPORTE	NO SOLDAR / LUZ 2
JF-034	TIE-1-0.15	U02_COLLARX_2_1	CJP	3.72	224	89 / 1000 / 150	TALLER / WPS
JF-035	TIE-1-0.15	BRT_COLLARX_1_0.15_-1	CJP	3.72	224	3111 / 1000 / 150	TALLER / WPS
JF-036	BRL-A-1	TIE-1-4.79	LUZ	-	-	POR MIEMBRO / SOPORTE	NO SOLDAR / LUZ 2
JF-037	BRL-B-1	TIE-1-4.79	LUZ	-	-	POR MIEMBRO / SOPORTE	NO SOLDAR / LUZ 2
JF-038	TIE-1-4.79	BRT_COLLARX_1_5.338_-1	CJP	3.72	224	3111 / 1000 / 5430	TALLER / WPS
JF-039	BRL-A-1	U02_COLLARX_2_1	LUZ	-	-	POR MIEMBRO / SOPORTE	NO SOLDAR / LUZ 2
JF-040	BRL-A-1	BRT_COLLARX_1_5.338_-1	LUZ	-	-	POR MIEMBRO / SOPORTE	NO SOLDAR / LUZ 2
JF-041	BRL-B-1	BRT_COLLARX_1_0.15_-1	LUZ	-	-	POR MIEMBRO / SOPORTE	NO SOLDAR / LUZ 2
JF-042	KNE-1	U02_COLLARY_9_-1	LUZ	-	-	POR MIEMBRO / SOPORTE	NO SOLDAR / LUZ 2
JF-043	PBRACE-1.1	PLONG-1.1	CJP	3.72	97.93	3123.4 / 1300.8 / 1918	TALLER / WPS

a = garganta efectiva de cálculo; L = longitud efectiva. CJP atraviesa la pared menor; PJP según preparación indicada.

LUZ = holgura de 2 mm libre de soldadura. Transferencia de carga por conexión primaria según memoria.

CJP / V60 / RAÍZ 2



PJP a2 / 2 x 45



FILETE / a SEGÚN CÁLCULO



NOTAS DE FABRICACIÓN Y MONTAJE

1. Soldadura conforme a AWS D1.1; verificación AISC360 según memoria.
2. Material de aporte compatible con metal base. CJP/PJP: procedimiento WPS calificado y aceptación según especificación.
3. Juntas primarias U01 / U02 / BRT / TC y anclajes: ver detalles y memoria. Interfaces JF según este cuadro.
4. Montaje en campo mediante uniones desmontables; conservar piezas KITO sin mecanizado ni soldaduras.

Cotas en mm. ISO2768-m. Soldaduras según cuadro JF. Contornos: CAD/DXF.

				REBABAR Y ROMPER ARISTAS	NO CAMBIAR LA ESCALA		REVISIÓN
SESUVECA DEL PERÚ							
	NOMBRE	FIRMA	FECHA			TÍTULO: Uniones de fabricación / Cuadro 1 de 2	
DIBUJ.	Javier Acevedo		16/10/26				
VERIF.							
APROB.							
FABR.							
CALID.				MATERIAL: SEGÚN LISTA DE MATERIALES		N.º DE DIBUJO EB-16	A1
PESO: SEGÚN CAD / lista de materiales				ESCALA: INDICADA		ESTACIÓN DE DESCARGA BIGBAG	HOJA 16 DE 17

Uniones de fabricación / Cuadro 2 de 2

ID	MIEMBRO	SOPORTE	TIPO	a mm	L mm	CENTRO GLOBAL X/Y/Z mm	EJECUCIÓN
JF-044	PBRACE-1.9	PLONG-1.9	CJP	3.72	77.43	3122.2 / 2104.1 / 1918	TALLER / WPS
JF-045	PBRACE-1.1	P02_CAP_PPOST-3.2-1.125	CJP	3.72	79.58	3149.3 / 1293.9 / 1907.8	TALLER / WPS
JF-046	PBRACE-1.1	P02_CARTELA_PPOST-3.2-1.125_-0.025	CJP	3.72	325.48	3111.4 / 1294 / 1867.6	TALLER / WPS
JF-047	PBRACE-1.9	P02_CAP_PPOST-3.2-1.9	CJP	3.72	31.14	3144.4 / 2128 / 1908.3	TALLER / WPS
JF-048	PBRACE-1.9	P02_CARTELA_PPOST-3.2-1.9_-0.025	CJP	3.72	227.65	3104.5 / 2073.5 / 1859.9	TALLER / WPS
JF-049	PBRACE-1.9	P02_CARTELA_PPOST-3.2-1.9_0.025	CJP	3.72	325.48	3111.4 / 2119 / 1867.6	TALLER / WPS
JF-050	RPOST-1.5-1.1	JF_CAP_RPOST-1.5-1.1	CJP	3.72	96	1516.5 / 1300 / 3148	TALLER / WPS
JF-051	RODAPIE_1.1	RPOST-1.5-1.1	CJP	3.72	100	1527 / 1297.5 / 2150	TALLER / WPS
JF-052	RODAPIE_1.1	RPOST-2.35-1.1	CJP	3.72	200	2350 / 1297.5 / 2150	TALLER / WPS
JF-053	RODAPIE_1.1	RPOST-3.2-1.1	CJP	3.72	100	3173 / 1297.5 / 2150	TALLER / WPS
JF-054	RODAPIE_TESTERO	RPOST-3.2-1.1	CJP	3.72	100	3202.5 / 1327 / 2150	TALLER / WPS
JF-055	SRAIL-1.1-1.1	RLONG-1.1-3.2	CJP	2.79	126.71	1497.8 / 1300.1 / 3183.7	TALLER / WPS
JF-056	REND-3.2	RLONG-1.1-3.2	CJP	2.79	120.28	3192.2 / 1318 / 3180	TALLER / WPS
JF-057	SRAILPOST--0.5625-1.045	SRAIL-1.1-1.1	CJP	2.79	120.57	-576.2 / 1255.2 / 1703.6	TALLER / WPS
JF-058	SRAILPOST-0.125-1.045	SRAIL-1.1-1.1	CJP	2.79	104.13	112.9 / 1261.1 / 2186.5	TALLER / WPS
JF-059	SRAILPOST-0.8125-1.045	SRAIL-1.1-1.1	CJP	2.79	87.7	802.6 / 1266.5 / 2670	TALLER / WPS
JF-060	RPOST-1.5-1.9	JF_CAP_RPOST-1.5-1.9	CJP	3.72	96	1516.5 / 2100 / 3148	TALLER / WPS
JF-061	RODAPIE_1.9	RPOST-1.5-1.9	CJP	3.72	100	1527 / 2097.5 / 2150	TALLER / WPS
JF-062	RODAPIE_1.9	RPOST-2.35-1.9	CJP	3.72	200	2350 / 2097.5 / 2150	TALLER / WPS
JF-063	RODAPIE_1.9	RPOST-3.2-1.9	CJP	3.72	100	3173 / 2097.5 / 2150	TALLER / WPS
JF-064	RODAPIE_TESTERO	RPOST-3.2-1.9	CJP	3.72	100	3202.5 / 2073 / 2150	TALLER / WPS
JF-065	SRAIL-1.9-1.1	RLONG-1.9-3.2	CJP	2.79	126.71	1497.8 / 2099.9 / 3183.7	TALLER / WPS
JF-066	REND-3.2	RLONG-1.9-3.2	CJP	2.79	120.28	3192.2 / 2082 / 3180	TALLER / WPS
JF-067	SRAILPOST--0.5625-1.955	SRAIL-1.9-1.1	CJP	2.79	120.57	-576.2 / 2144.8 / 1703.6	TALLER / WPS
JF-068	SRAILPOST-0.125-1.955	SRAIL-1.9-1.1	CJP	2.79	104.13	112.9 / 2138.9 / 2186.5	TALLER / WPS
JF-069	SRAILPOST-0.8125-1.955	SRAIL-1.9-1.1	CJP	2.79	87.7	802.6 / 2133.5 / 2670	TALLER / WPS
JF-070	J01_EXTREMO_1.0625	P02_CAP_PPOST-1.5-1.1	LUZ	-	-	POR MIEMBRO / SOPORTE	NO SOLDAR / LUZ 2
JF-071	J01_SOPORTE_1.0625	P02_CAP_PPOST-1.5-1.1	CJP	11.16	280.43	1452 / 1300.1 / 1913.7	TALLER / WPS
JF-072	J01_CARTELA_1.0625_1	P02_CAP_PPOST-1.5-1.1	LUZ	-	-	POR MIEMBRO / SOPORTE	NO SOLDAR / LUZ 2
JF-073	J01_EXTREMO_1.9375000000000002	P02_CAP_PPOST-1.5-1.9	LUZ	-	-	POR MIEMBRO / SOPORTE	NO SOLDAR / LUZ 2
JF-074	J01_SOPORTE_1.9375000000000002	P02_CAP_PPOST-1.5-1.9	CJP	11.16	280.43	1452 / 2099.9 / 1913.7	TALLER / WPS
JF-075	J01_CARTELA_1.9375000000000002_-1	P02_CAP_PPOST-1.5-1.9	LUZ	-	-	POR MIEMBRO / SOPORTE	NO SOLDAR / LUZ 2
JF-076	J01_CARTELA_1.0625_-1	J01_EXTREMO_1.0625	LUZ	-	-	POR MIEMBRO / SOPORTE	NO SOLDAR / LUZ 2
JF-077	J01_CARTELA_1.0625_1	J01_EXTREMO_1.0625	LUZ	-	-	POR MIEMBRO / SOPORTE	NO SOLDAR / LUZ 2
JF-078	J01_CARTELA_1.0625_-1	J01_SOPORTE_1.0625	CJP	5.58	150	1460 / 1220.5 / 1950	TALLER / WPS
JF-079	J01_CARTELA_1.0625_1	J01_SOPORTE_1.0625	CJP	5.58	98	1460 / 1310.5 / 1976	TALLER / WPS
JF-080	J01_CARTELA_1.9375000000000002_-1	J01_EXTREMO_1.9375000000000002	LUZ	-	-	POR MIEMBRO / SOPORTE	NO SOLDAR / LUZ 2
JF-081	J01_CARTELA_1.9375000000000002_1	J01_EXTREMO_1.9375000000000002	LUZ	-	-	POR MIEMBRO / SOPORTE	NO SOLDAR / LUZ 2
JF-082	J01_CARTELA_1.9375000000000002_-1	J01_SOPORTE_1.9375000000000002	CJP	5.58	98	1460 / 2095.5 / 1976	TALLER / WPS
JF-083	J01_CARTELA_1.9375000000000002_1	J01_SOPORTE_1.9375000000000002	CJP	5.58	150	1460 / 2185.5 / 1950	TALLER / WPS
JF_CAP_RPOST-1.5-1.1-RAIL	JF_CAP_RPOST-1.5-1.1	RLONG-1.1-3.2	PJP	2	90	1532.5 / 1300 / 3158	TALLER / WPS
JF_CAP_RPOST-1.5-1.9-RAIL	JF_CAP_RPOST-1.5-1.9	RLONG-1.9-3.2	PJP	2	90	1532.5 / 2100 / 3158	TALLER / WPS

a = garganta efectiva de cálculo; L = longitud efectiva. CJP atraviesa la pared menor; PJP según preparación indicada.

LUZ = holgura de 2 mm libre de soldadura. Transferencia de carga por conexión primaria según memoria.

CJP / V60 / RAÍZ 2



PJP a2 / 2 x 45



FILETE / a SEGÚN CÁLCULO



POSICIÓN DE LOS 37 MIEMBROS JF / ORIGEN X,Y,Z mm / VECTOR LOCAL LONGITUDINAL

BRL-A--1 | 87,-955,150 | 0.5,0,0.87
BRL-B--1 | 87,-1045,5430 | 0.5,0,-0.87
KNE--1 | 0,-913,5006.29 | 0,0.75,0.66
BRL-A-1 | 87,1045,150 | 0.5,0,0.87
BRL-B-1 | 87,955,5430 | 0.5,0,-0.87
KNE-1 | 0,913,5006.29 | 0,-0.75,0.66
PBRACE-1.1 | 1540,1300,150 | 0.68,0,0.74
PBRACE-1.9 | 1540,2100,150 | 0.68,0,0.74
STRING-1.1 | -1250,1262.5,25 | 0.82,0,0.57
STRING-1.9 | -1250,2137.5,25 | 0.82,0,0.57
STEP-11-1.47 | 1482,1300,1875 | 0,1,0
TIE--1-0.15 | 75,-1000,150 | 1,0,0
TIE--1-4.79 | 75,-1000,5430 | 1,0,0
TIE-1-0.15 | 75,1000,150 | 1,0,0
TIE-1-4.79 | 75,1000,5430 | 1,0,0
RPOST-1.5-1.1 | 1500,1300,2090 | 0,0,1
RODAPIE_1.1 | 2350,1300,2150 | 0,-1,0
RODAPIE_TESTERO | 3200,1700,2150 | 1,0,0
SRAIL-1.1-1.1 | -1250,1245,1255 | 0.82,0.02,0.57
REND-3.2 | 3200,1300,3180 | 0,1,0
SRAILPOST--0.5625-1.045 | -562.5,1245,622.21 | 0,0,1
SRAILPOST-0.125-1.045 | 125,1245,1103.46 | 0,0,1
SRAILPOST-0.8125-1.045 | 812.5,1245,1584.71 | 0,0,1
RPOST-1.5-1.9 | 1500,2100,2090 | 0,0,1
RODAPIE_1.9 | 2350,2100,2150 | 0,-1,0
SRAIL-1.9-1.1 | -1250,2155,1255 | 0.82,-0.02,0.57
SRAILPOST--0.5625-1.955 | -562.5,2155,622.21 | 0,0,1
SRAILPOST-0.125-1.955 | 125,2155,1103.46 | 0,0,1
SRAILPOST-0.8125-1.955 | 812.5,2155,1584.71 | 0,0,1
J01_EXTREMO_1.0625 | 1434,1262.5,1950 | 1,0,0
J01_SOPORTE_1.0625 | 1446,1262.5,1950 | 1,0,0
J01_CARTELA_1.0625_1 | 1460,1307.5,2025 | 0,1,0
J01_EXTREMO_1.9375000000000002 | 1434,2137.5,1950 | 1,0,0
J01_SOPORTE_1.9375000000000002 | 1446,2137.5,1950 | 1,0,0
J01_CARTELA_1.9375000000000002_-1 | 1460,2092.5,2025 | 0,1,0
J01_CARTELA_1.0625_-1 | 1460,1217.5,2025 | 0,1,0
J01_CARTELA_1.9375000000000002_1 | 1460,2182.5,2025 | 0,1,0

El vector local define la orientación; perfiles / cortes nominales por POS. y conjunto. Preparaciones exactas: CAD / DXF.

				REBABAR Y ROMPER ARISTAS	NO CAMBIAR LA ESCALA		REVISIÓN
SESUVECA DEL PERÚ							
	NOMBRE	FIRMA	FECHA			TÍTULO: Uniones de fabricación / Cuadro 2 de 2	
DIBUJ.	Javier Acevedo		16/10/26				
VERIF.							
APROB.							
FABR.							
CALID.				MATERIAL: SEGÚN LISTA DE MATERIALES		N.º DE DIBUJO EB-17	A1
PESO: SEGÚN CAD / lista de materiales				ESCALA: INDICADA		ESTACIÓN DE DESCARGA BIGBAG	HOJA 17 DE 17