

POS.	CANT.	DESCRIPCIÓN	MATERIAL	OBSERVACIÓN
1.1	1	Estructura portante	ASTM A500 Gr.B	
1.2	1	Monorriel y tecle	HEB 200 S355 / conjunto 2 t	
1.3	1	Soporte de tolva	ASTM A500 Gr.B	
1.4	1	Tolva de recepción	ASTM A36	
1.5	1	Compuerta de descarga	ASTM A36	
1.6	1	Plataforma y acceso	ASTM A500 Gr.B	
1.7	1	Cruceta de izaje	ASTM A500 Gr.B	
1.8	1	Balanza de ensacado	ASTM A36	


Part. 1

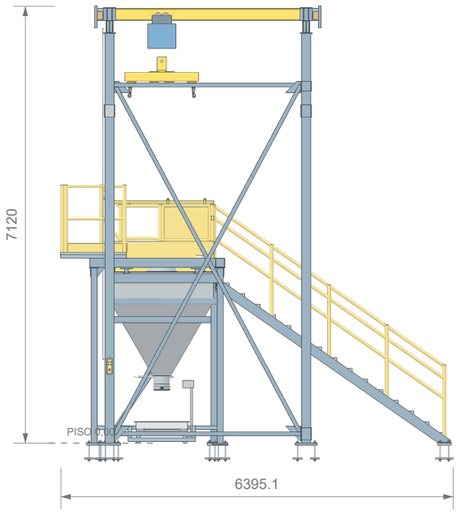


VISTA FRONTAL ESCALA 1:100

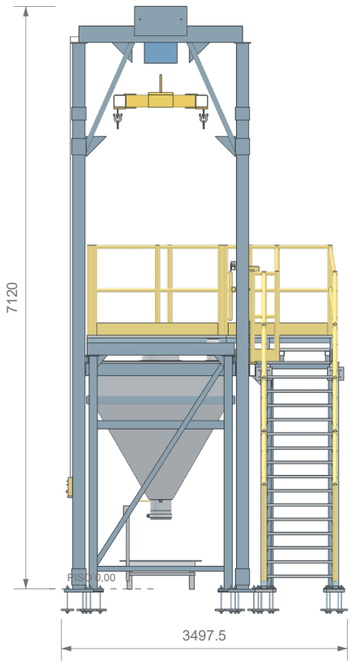

VISTA LATERAL ESCALA 1:75

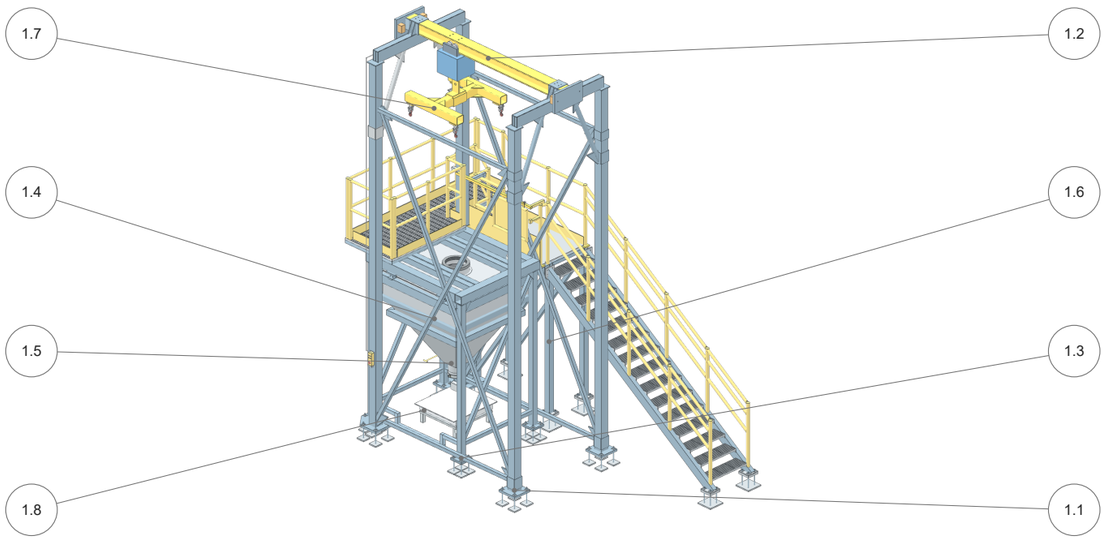

ISOMÉTRICA

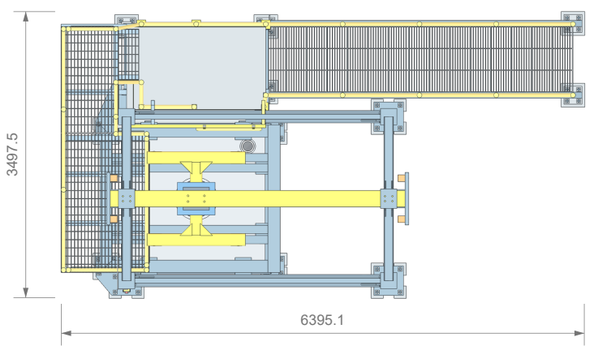

PLANTA ESCALA 1:75

BigBag: 1.000 kg. Ensacado: 25 y 50 kg.
Altura sobre piso: 7.120. Entrada Ø450. Espacio BigBag-tolva: 800.

SESUVECA DEL PERÚ

ELIMINAR REBABAS Y ARISTAS VIVAS	NO CAMBIE LA ESCALA	REVISIÓN

	NOMBRE	FIRMA	FECHA
DIB.	Javier Acevedo		10/11/26
VERIF.			
APROB.			
FABR.			
CALID.			

TÍTULO:


Estación de descarga de BigBags

MATERIAL:	N° DIBUJO:	
SEGÚN TABLA	BB-01	A3


PROYECTO:	PESO:	ESCALA:	HOJA:
DESCARGA DE BIGBAGS		INDICADAS	1 DE 17

POS.	CANT.	DESCRIPCIÓN	MATERIAL	OBSERVACIÓN
2.1	4	Columna SHS 150x 150x 6 x 6668	ASTM A500 Gr.B	
2.2	2	Travesano IPE 200 x 2000, cerrado con placa 8	ASTM A36	
2.3	4	Diagonal SHS 60x 60x 4, eje 6435,77	ASTM A500 Gr.B	
2.4	4	Tirantes laterales SHS 60x 60x 4	ASTM A500 Gr.B	
2.5	4	Rodillas SHS 60x 60x 4	ASTM A500 Gr.B	
2.6	1	Cartelas y collares de union	ASTM A36	Juego
2.7	1	Placas de base, tapas y refuerzos	ASTM A36	Juego


Part. 2

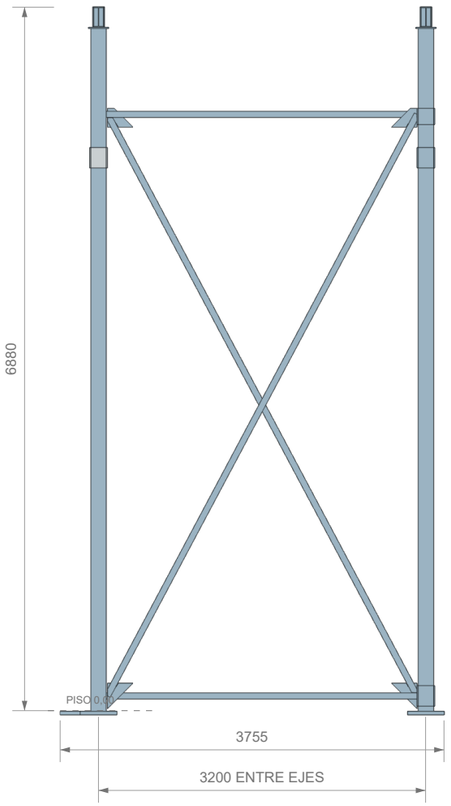


VISTA FRONTAL ESCALA 1:60

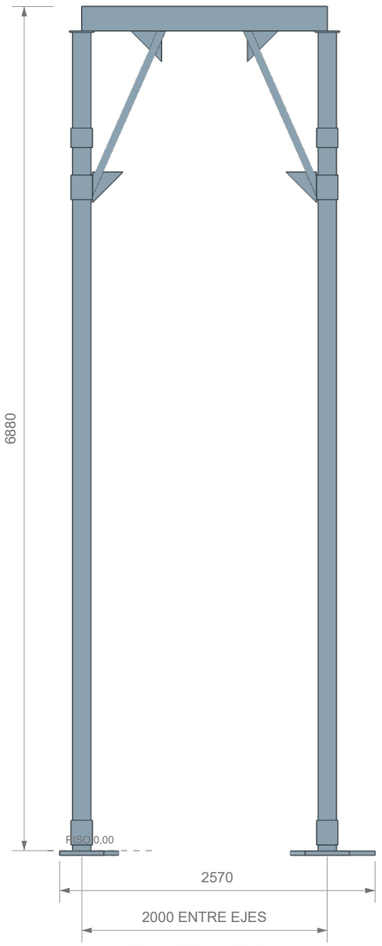

VISTA LATERAL ESCALA 1:50

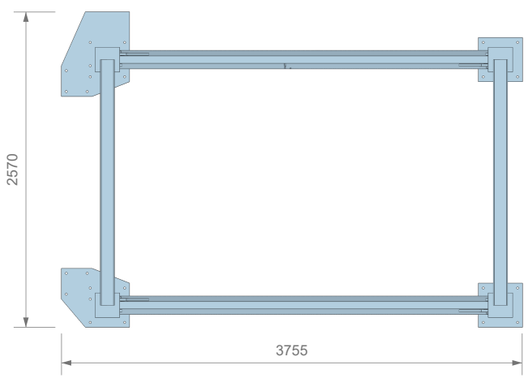

PLANTA ESCALA 1:50

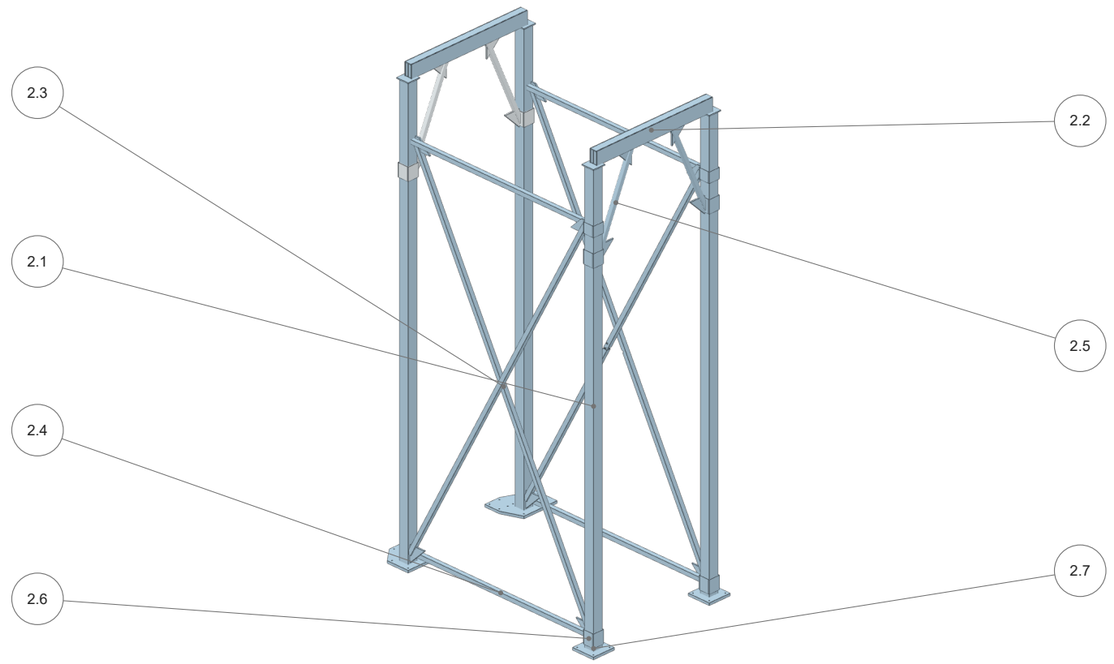

ISOMÉTRICA

Columnas SHS 150 × 150 × 6, L6668; riostras SHS 60 × 60 × 4, L6435,8.
Ejes de pórticos: 3200 × 2000. Altura de asiento del monorriel: 6880.

SESUVECA DEL PERÚ

ELIMINAR REBABAS Y ARISTAS VIVAS	NO CAMBIE LA ESCALA	REVISIÓN

	NOMBRE	FIRMA	FECHA
DIB.	Javier Acevedo		10/11/26
VERIF.			
APROB.			
FABR.			
CALID.			


TÍTULO: Estructura portante

MATERIAL:	N° DIBUJO:	
SEGÚN TABLA	BB-02	A3


PROYECTO: DESCARGA DE BIGBAGS	PESO:	ESCALA: INDICADAS	HOJA: 2 DE 17

POS.	CANT.	DESCRIPCIÓN	MATERIAL	OBSERVACIÓN
3.1	1	Viga HEB 200 x 3600	S355	
3.2	2	Placa superior 200x 236x 12	ASTM A36	
3.3	4	Lateral 200x 200x 12	ASTM A36	
3.4	8	Calce 200x 15x 6	ASTM A36	
3.5	8	Cartela 100x 200x 12	ASTM A36	
3.6	2	Placa de tope, espesor 45	ASTM A36	
3.7	4	Rigidizador 100x 200x 12	ASTM A36	
3.8	4	Amortiguadores comerciales	Suministro	


Part. 3

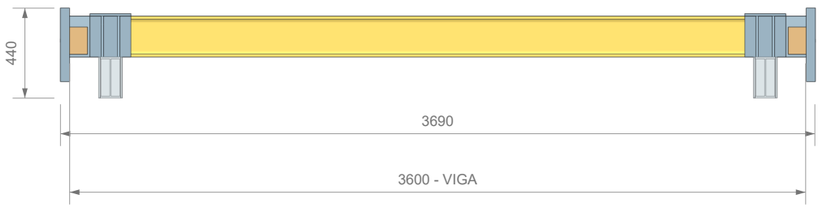


VISTA FRONTAL ESCALA 1:30

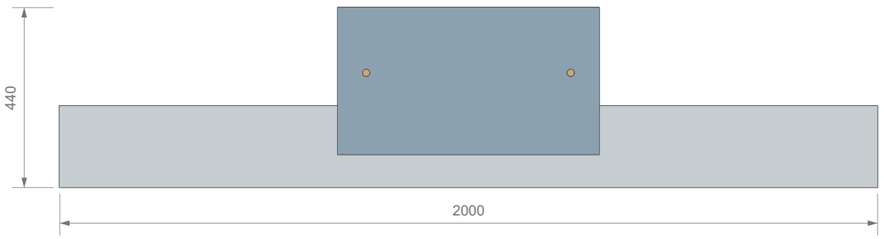

VISTA LATERAL ESCALA 1:15

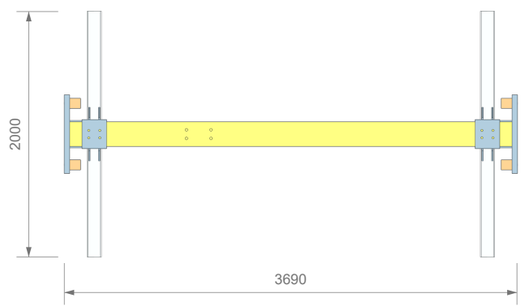

PLANTA ESCALA 1:50

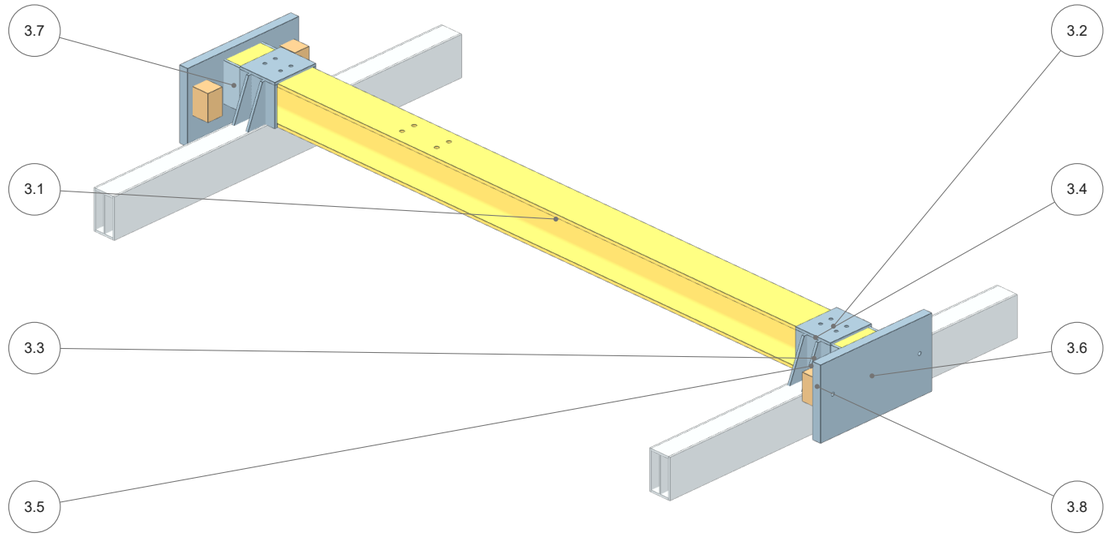

ISOMÉTRICA

Sillas: 4 pernos M16 F3125/A325M por apoyo.
Ala de rodadura 200x 15. No soldar sobre la pista inferior.

SESUVECA DEL PERÚ

ELIMINAR REBABAS Y ARISTAS VIVAS	NO CAMBIE LA ESCALA	REVISIÓN


	NOMBRE	FIRMA	FECHA
DIB.	Javier Acevedo		10/11/26
VERIF.			
APROB.			
FABR.			
CALID.			

PROYECTO: DESCARGA DE BIGBAGS


TÍTULO: Monorriel y sillas de apoyo

MATERIAL:	N° DIBUJO:	
SEGÚN TABLA	BB-03	A3


PESO:	ESCALA:	HOJA:
	INDICADAS	3 DE 17

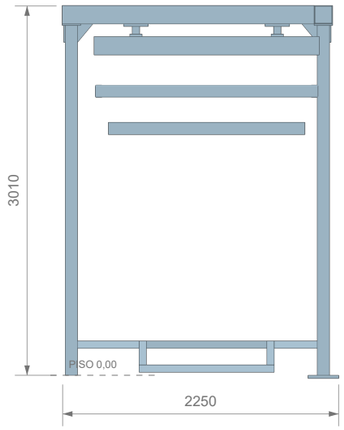

VISTA FRONTAL ESCALA 1:50

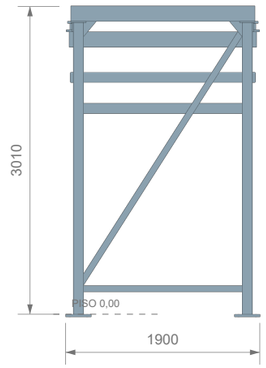


VISTA LATERAL ESCALA 1:60

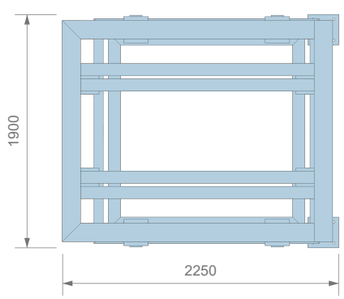

PLANTA ESCALA 1:50

POS.	CANT.	DESCRIPCIÓN	MATERIAL	OBSERVACIÓN
4.1	4	Patas RHS 150x 75x 5	ASTM A500 Gr.B	
4.2	1	Marco superior e inferior	ASTM A500 Gr.B	Juego
4.3	12	Riostras de bastidor	ASTM A500 Gr.B	
4.4	2	Diagonales laterales	ASTM A500 Gr.B	
4.5	4	Ménsulas de tolva	ASTM A36	
4.6	4	Vigas apoyo BigBag SHS 100x 100x 5	ASTM A500 Gr.B	
4.7	1	Bases, asientos, tapas y cartelas	ASTM A36	Juego

Part. 4

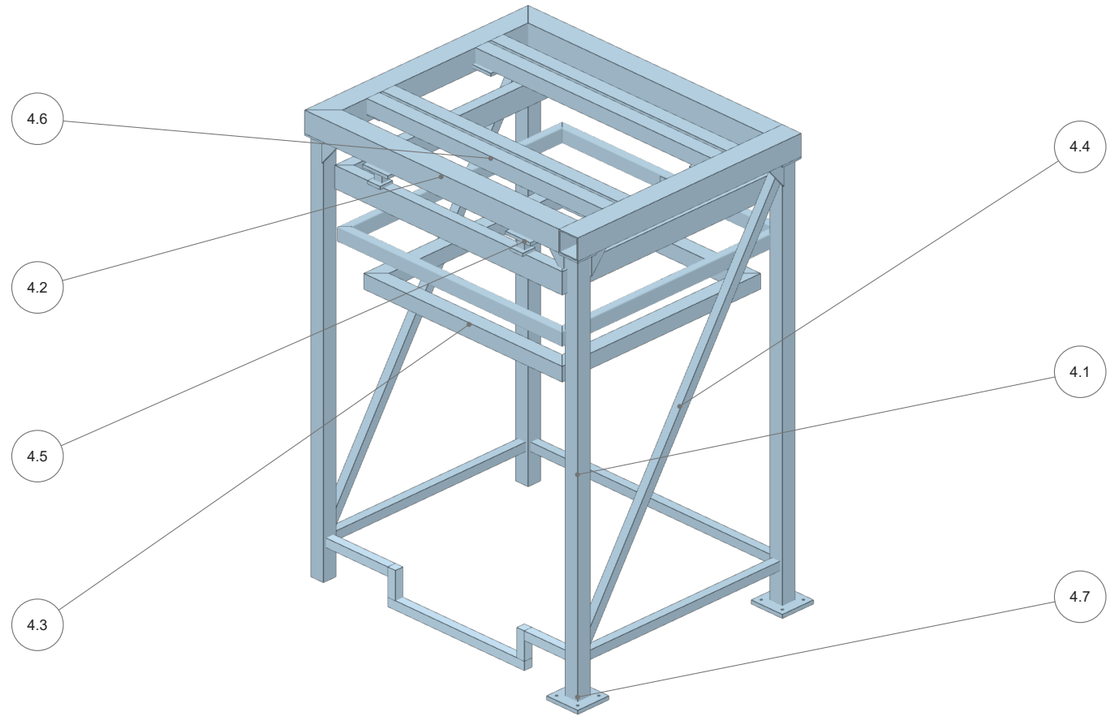

ISOMÉTRICA

Nivel de apoyo del BigBag Z3010.

SESUVECA DEL PERÚ

ELIMINAR REBABAS Y ARISTAS VIVAS	NO CAMBIE LA ESCALA	REVISIÓN


	NOMBRE	FIRMA	FECHA
DIB.	Javier Acevedo		10/11/26
VERIF.			
APROB.			
FABR.			
CALID.			

PROYECTO: DESCARGA DE BIGBAGS


TÍTULO: Bastidor de soporte de tolva

MATERIAL:	N° DIBUJO:	
SEGÚN TABLA	BB-04	A3


PESO:	ESCALA:	HOJA:
	INDICADAS	4 DE 17

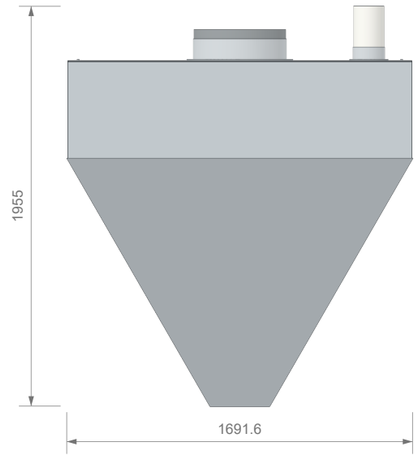

VISTA FRONTAL ESCALA 1:30

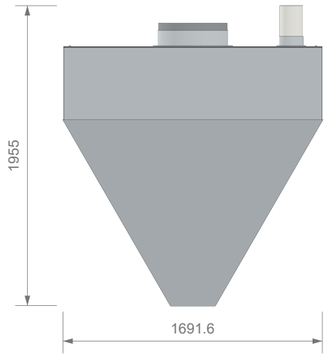


VISTA LATERAL ESCALA 1:40

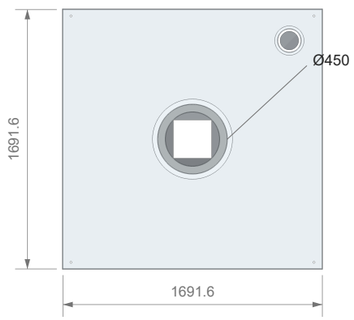

PLANTA ESCALA 1:40

POS.	CANT.	DESCRIPCIÓN	MATERIAL	OBSERVACIÓN
5.1	4	Paneles del cuerpo	ASTM A36	
5.2	4	Paneles del cono	ASTM A36	
5.3	1	Tapa desmontable y fijaciones	ASTM A36	
5.4	1	Receptor Ø450 y aro Ø520	ASTM A36	
5.5	1	Revestimiento interior	UHMWPE	Juego
5.6	1	Sello de manga Ø350	Elastomero	
5.7	1	Venteo DN150 y filtro	Suministro	

Part. 5

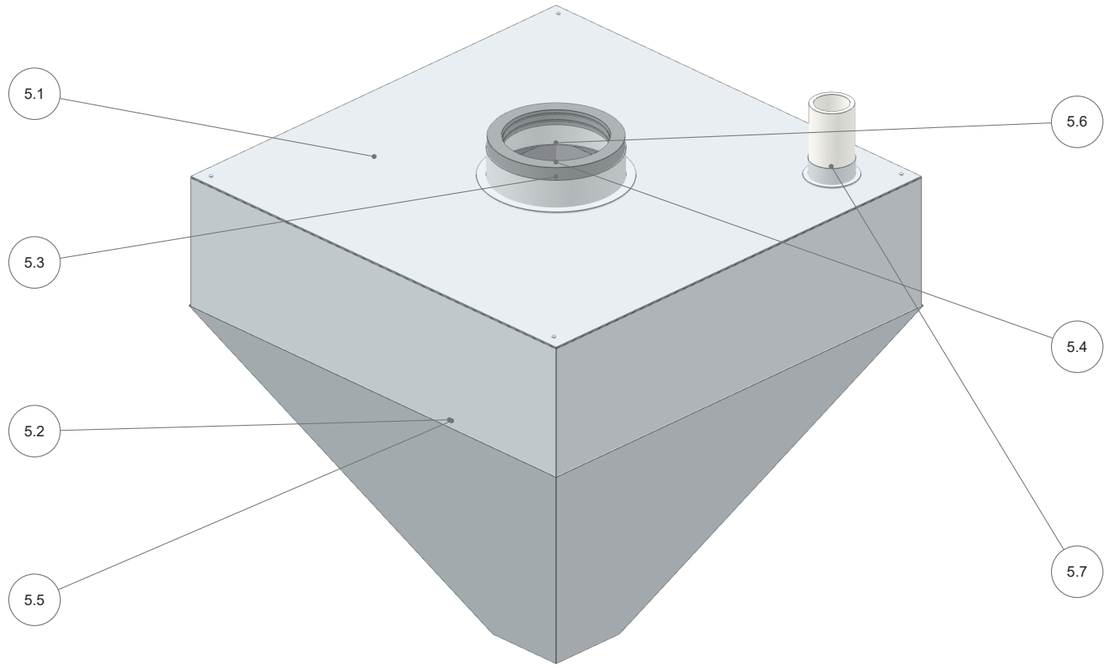

ISOMÉTRICA

Chapa cuerpo t 6; cono t 8; tapa t 3. Revestimiento UHMWPE t 10.
Receptor: paso Ø450; aro Ø520 × 6; cuello rolado t 3.

SESUVECA DEL PERÚ

ELIMINAR REBABAS Y ARISTAS VIVAS	NO CAMBIE LA ESCALA	REVISIÓN

	NOMBRE	FIRMA	FECHA
DIB.	Javier Acevedo		10/11/26
VERIF.			
APROB.			
FABR.			
CALID.			

PROYECTO: DESCARGA DE BIGBAGS


TÍTULO: Tolva y boca de recepción

MATERIAL:	N° DIBUJO:	
SEGÚN TABLA	BB-05	A3


PESO:	ESCALA:	HOJA:
	INDICADAS	5 DE 17

POS.	CANT.	DESCRIPCIÓN	MATERIAL	OBSERVACIÓN
6.1	1	Cuerpo fijo DN250	ASTM A36	
6.2	1	Paleta, eje y mando	ASTM A36	Disco 249x 6; eje 20; giro 90 grados
6.3	1	Cuello de ensacado DN250	ASTM A36	
6.4	1	Abrazadera manual	ASTM A36	Con revestimiento de goma
6.5	1	Bujes y collares de eje	Suministro	2 GSM-2022-20 +2 MSP-20-F


Part. 6

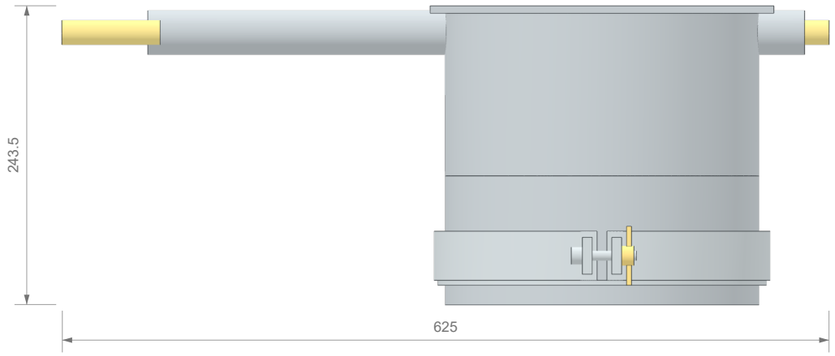


VISTA FRONTAL ESCALA 1:5

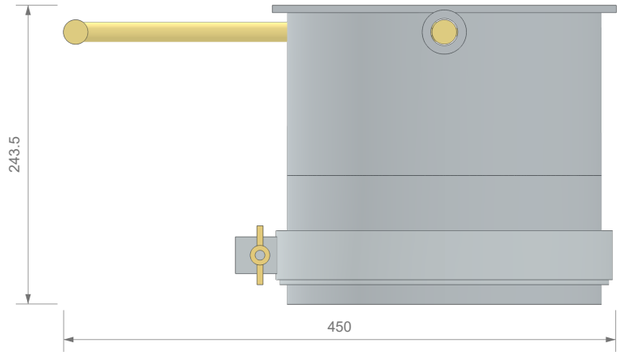

VISTA LATERAL ESCALA 1:5

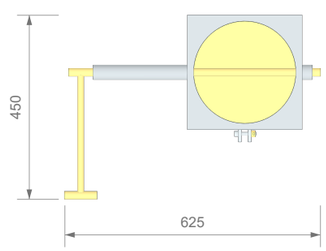

PLANTA ESCALA 1:15

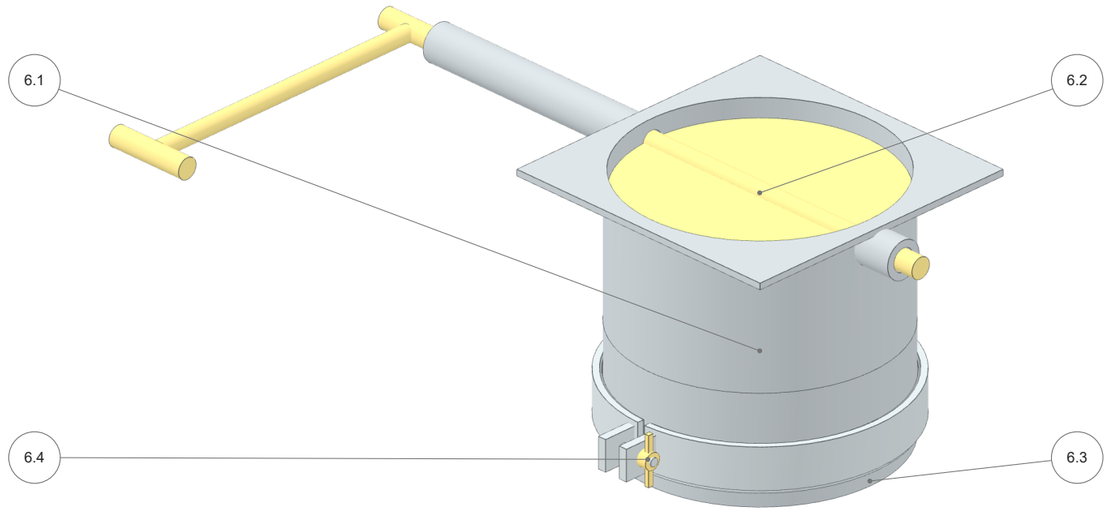

ISOMÉTRICA

Disco Ø249 × 6, eje Ø20h 9 y giro 90°. Cuello de salida Ø250.
Alojamiento Ø22H7; 2 bujes y 2 collares. Juego axial 0,2-0,5.

SESUVECA DEL PERÚ

	NOMBRE	FIRMA	FECHA
DIB.	Javier Acevedo		10/11/26
VERIF.			
APROB.			
FABR.			
CALID.			

PROYECTO: DESCARGA DE BIGBAGS

ELIMINAR REBABAS Y ARISTAS VIVAS | NO CAMBIE LA ESCALA | REVISIÓN


TÍTULO: Compuerta de descarga

MATERIAL: SEGÚN TABLA | N° DIBUJO: BB-06 | A3


PESO: | ESCALA: INDICADAS | HOJA: 6 DE 17

POS.	CANT.	DESCRIPCIÓN	MATERIAL	OBSERVACIÓN
7.1	4	Postes SHS 100x 100x 5	ASTM A500 Gr.B	
7.2	1	Marco y voladizos	ASTM A500 Gr.B	Juego
7.3	2	Diagonales SHS 100x 100x 5	ASTM A500 Gr.B	
7.4	1	Bastidor de ampliación	ASTM A500 Gr.B	
7.5	1	Rejillas de piso	Rejilla 32x 5	Juego
7.6	1	Bases y cartelas	ASTM A36	Juego


Part. 7

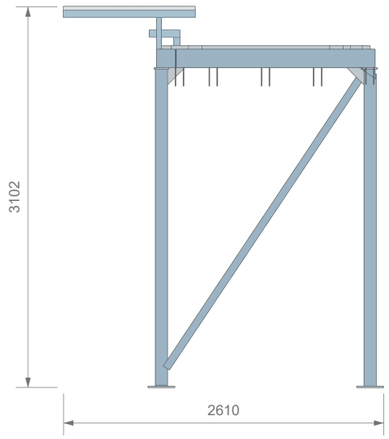


VISTA FRONTAL ESCALA 1:50

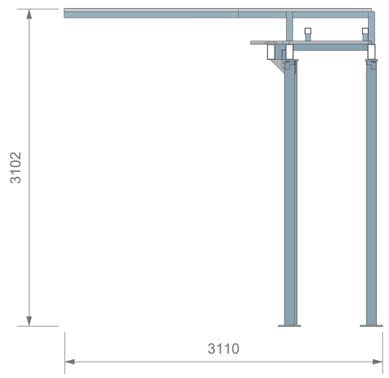

VISTA LATERAL ESCALA 1:60

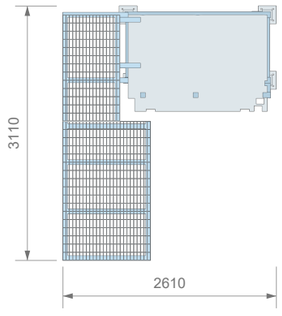

PLANTA ESCALA 1:75

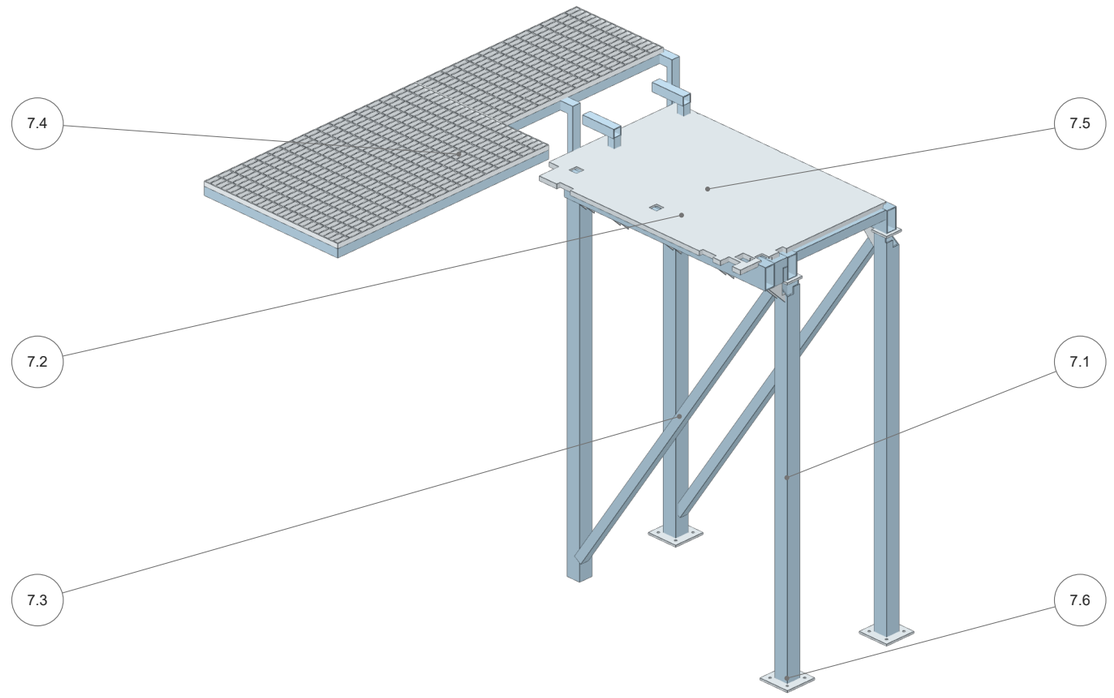

ISOMÉTRICA

Rejilla existente Z2782,59; ampliación Z3102.
Paso principal 955; retorno 580.

SESUVECA DEL PERÚ

ELIMINAR REBABAS Y ARISTAS VIVAS	NO CAMBIE LA ESCALA	REVISIÓN

	NOMBRE	FIRMA	FECHA
DIB.	Javier Acevedo		10/11/26
VERIF.			
APROB.			
FABR.			
CALID.			

PROYECTO: DESCARGA DE BIGBAGS


TÍTULO: Plataforma de trabajo

MATERIAL:	N° DIBUJO:	
SEGÚN TABLA	BB-07	A3


PESO:	ESCALA:	HOJA:
	INDICADAS	7 DE 17

POS.	CANT.	DESCRIPCIÓN	MATERIAL	OBSERVACIÓN
8.1	2	Zancas de escalera	ASTM A500 Gr.B	
8.2	15	Peldaños 800x 250	Rejilla 32x 5	
8.3	1	Peldaño de transición 620x 250	Rejilla 32x 5	
8.4	1	Placas de apoyo y union	ASTM A36	Juego


Part. 8

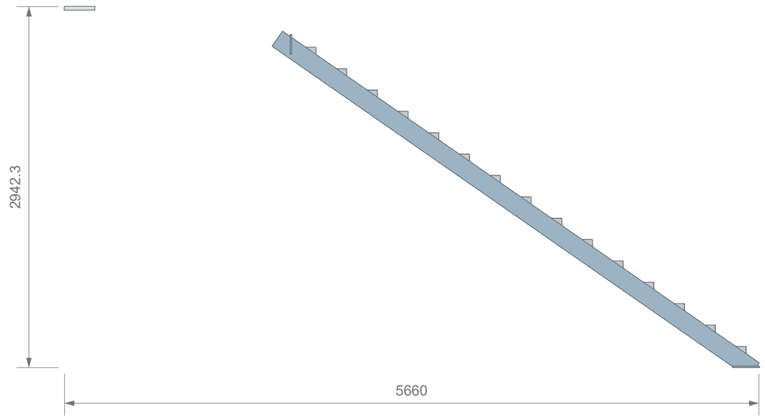


VISTA FRONTAL ESCALA 1:50

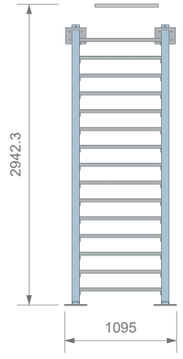

VISTA LATERAL ESCALA 1:60

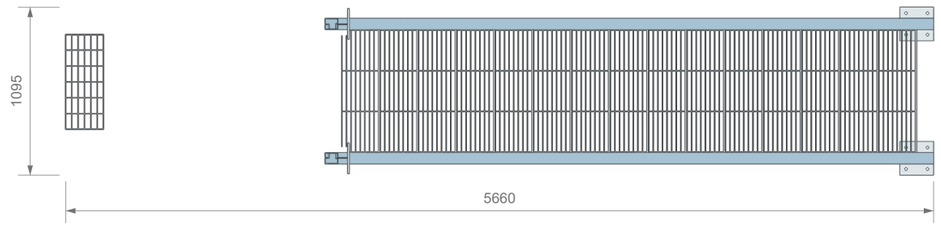

PLANTA ESCALA 1:40

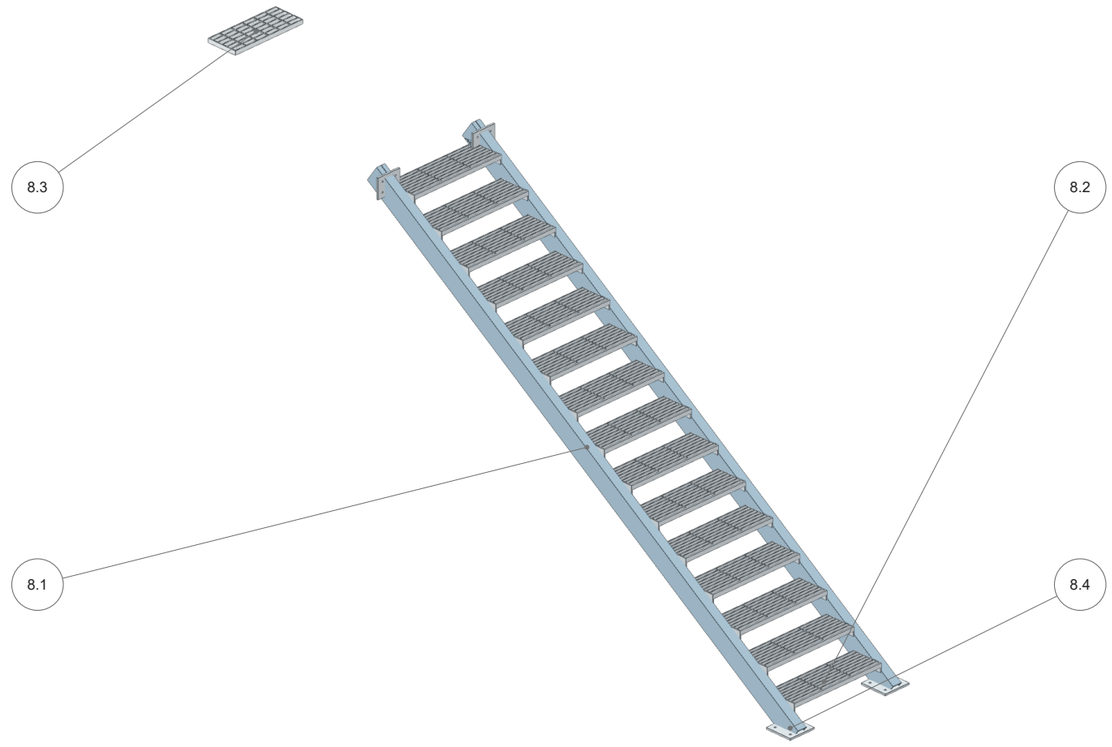

ISOMÉTRICA

15 peldaños 800 × 250; paso longitudinal 250.
Plataforma: +2782,59. Peldaño de transición: +2942,30.

SESUVECA DEL PERÚ

ELIMINAR REBABAS Y ARISTAS VIVAS	NO CAMBIE LA ESCALA	REVISIÓN	
	NOMBRE	FIRMA	FECHA
DIB.	Javier Acevedo		10/11/26
VERIF.			
APROB.			
FABR.			
CALID.			
PROYECTO: DESCARGA DE BIGBAGS			

TÍTULO:


Escalera de acceso

MATERIAL:	N° DIBUJO:	
SEGÚN TABLA	BB-08	A3


PESO:	ESCALA:	HOJA:
	INDICADAS	8 DE 17

POS.	CANT.	DESCRIPCIÓN	MATERIAL	OBSERVACIÓN
9.1	15	Postes circulares 60,3x 4	A53 SCH40	
9.2	33	Pasamanos circulares 48,3x 3	ISO65	
9.3	1	Puerta de acceso	ISO65	Tubo 42,4x 3
9.4	1	Rodapies y proteccion inferior	ASTM A36	Juego
9.5	1	Bases, guias y cierre	ASTM A36	Juego


Part. 9

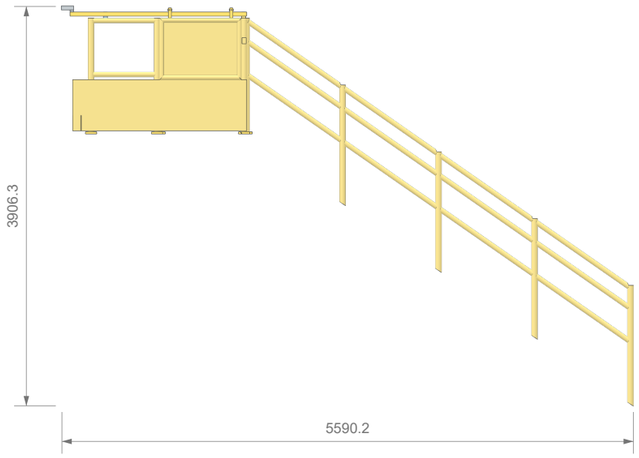


VISTA FRONTAL ESCALA 1:60

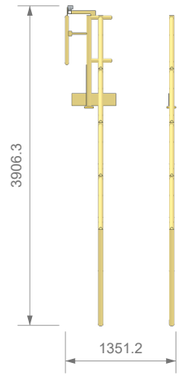

VISTA LATERAL ESCALA 1:75

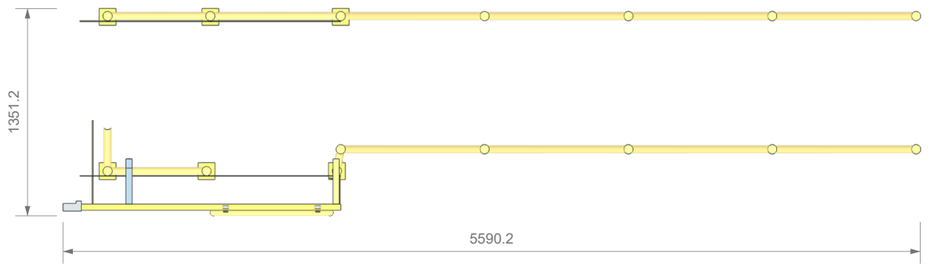

PLANTA ESCALA 1:40

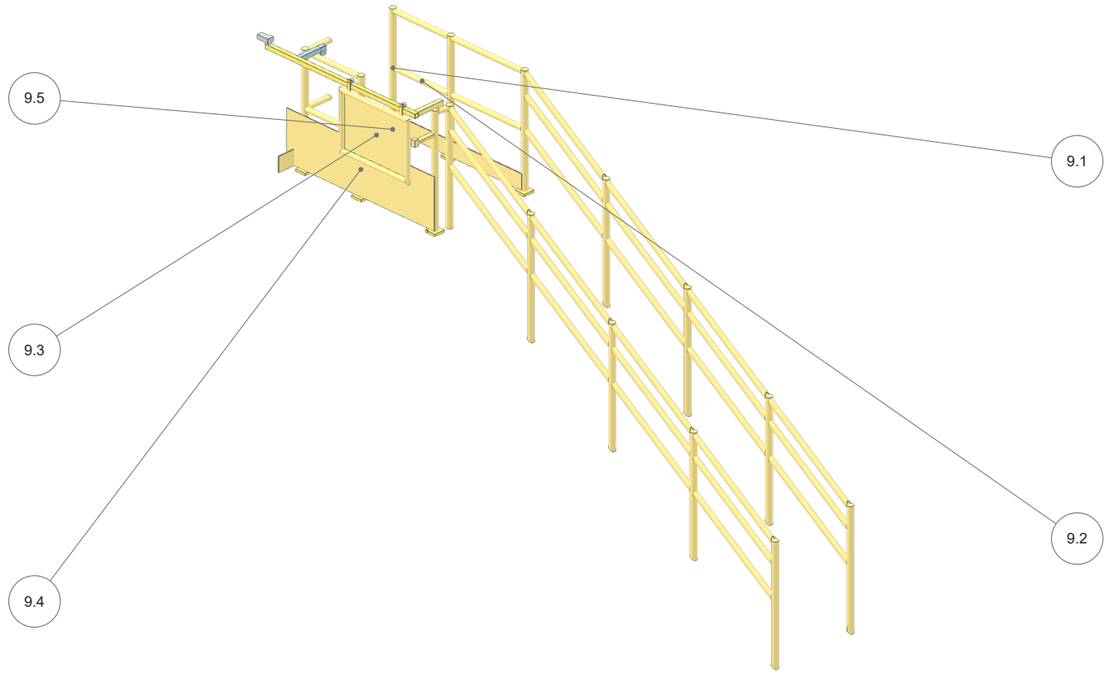

ISOMÉTRICA

Altura nominal de baranda 1100. Rodapie 150x 6.
Pasamanos y marcos de tubo circular.

SESUVECA DEL PERÚ

	NOMBRE	FIRMA	FECHA
DIB.	Javier Acevedo		10/11/26
VERIF.			
APROB.			
FABR.			
CALID.			

PROYECTO: DESCARGA DE BIGBAGS

ELIMINAR REBABAS Y ARISTAS VIVAS | NO CAMBIE LA ESCALA | REVISIÓN


TÍTULO: Barandas de acceso y plataforma

MATERIAL: SEGÚN TABLA | N° DIBUJO: BB-09 | A3


PESO: | ESCALA: INDICADAS | HOJA: 9 DE 17

POS.	CANT.	DESCRIPCIÓN	MATERIAL	OBSERVACIÓN
10.1	1	Paño exterior	Tubo circular	
10.2	1	Paño frontal	Tubo circular	
10.3	1	Paño junto a bolsa	Tubo circular	
10.4	1	Retorno y testero	Tubo circular	Juego
10.5	1	Entrante y transición	Tubo circular	Juego


Part. 10

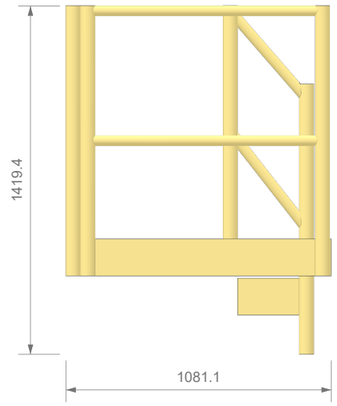


VISTA FRONTAL ESCALA 1:25

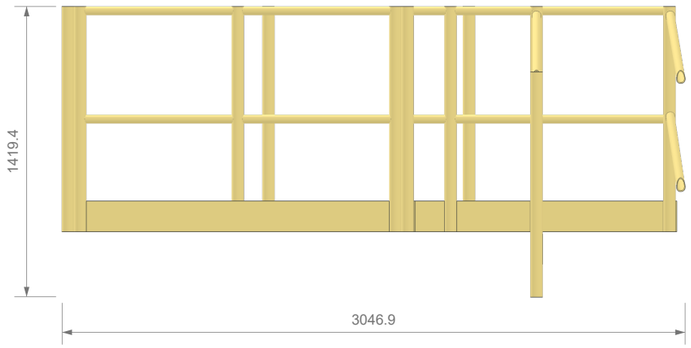

VISTA LATERAL ESCALA 1:30

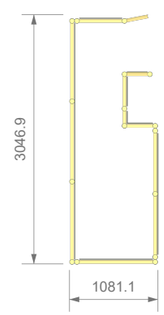

PLANTA ESCALA 1:75

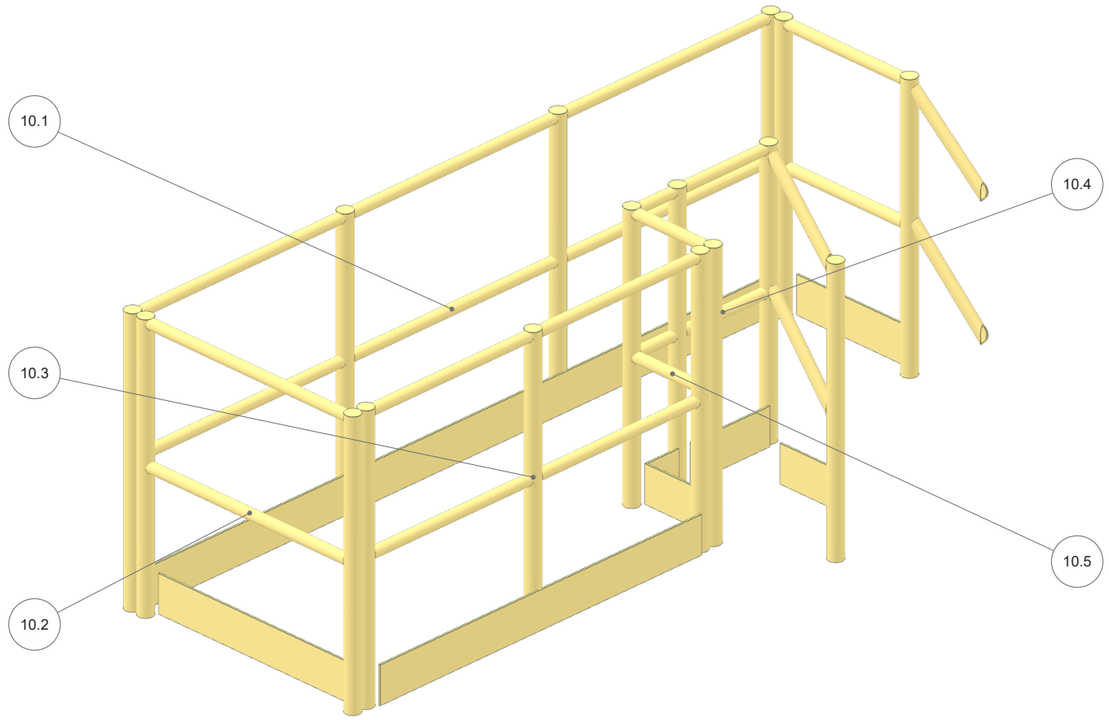

ISOMÉTRICA

Postes 60,3x 4; pasamanos 42,4x 3. Rodapie 150x 6.

SESUVECA DEL PERÚ

ELIMINAR REBABAS Y ARISTAS VIVAS	NO CAMBIE LA ESCALA	REVISIÓN

	NOMBRE	FIRMA	FECHA
DIB.	Javier Acevedo		10/11/26
VERIF.			
APROB.			
FABR.			
CALID.			

PROYECTO: DESCARGA DE BIGBAGS

TÍTULO: Barandas de la ampliación

MATERIAL: SEGÚN TABLA

N° DIBUJO: BB-10

A3


PESO:

ESCALA: INDICADAS


HOJA: 10 DE 17

POS.	CANT.	DESCRIPCIÓN	MATERIAL	OBSERVACIÓN
11.1	2	Vigas extremas SHS 150x 150x 6 x 1200	ASTM A500 Gr.B	
11.2	1	Viga central SHS 150x 150x 6	ASTM A500 Gr.B	L bruto 887,5
11.3	1	Oreja central y refuerzos	ASTM A36	Juego
11.4	4	Oreja extrema 90x 120x 12	ASTM A36	
11.5	4	Respaldo 140x 150x 20	ASTM A36	
11.6	8	Cartelas de refuerzo	ASTM A36	
11.7	4	Ganchos y grilletes de izaje	Suministro	4 juegos

Part. 11

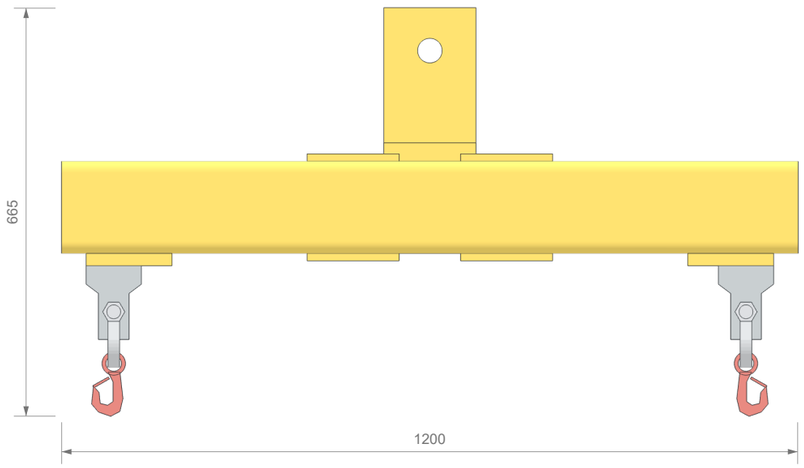


VISTA FRONTAL ESCALA 1:10

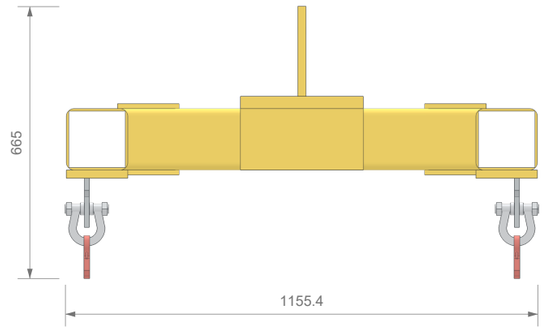

VISTA LATERAL ESCALA 1:15

PLANTA ESCALA 1:30

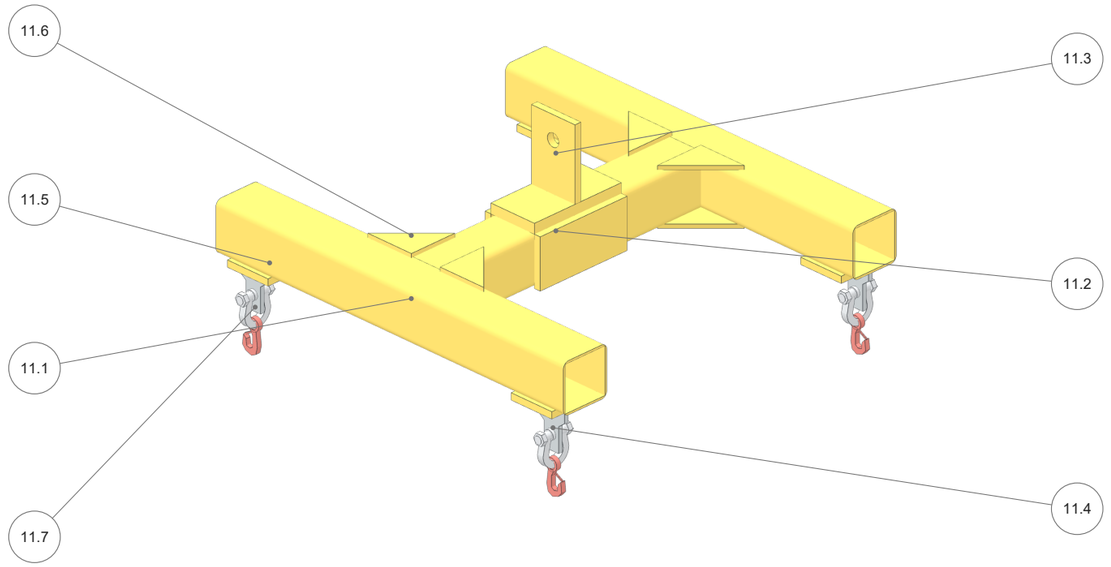

ISOMÉTRICA

Capacidad de proceso 1000 kg.
Gancho y grillete con seguros de cierre.

SESUVECA DEL PERÚ

ELIMINAR REBABAS Y ARISTAS VIVAS	NO CAMBIE LA ESCALA	REVISIÓN

	NOMBRE	FIRMA	FECHA
DIB.	Javier Acevedo		10/11/26
VERIF.			
APROB.			
FABR.			
CALID.			

PROYECTO: DESCARGA DE BIGBAGS


TÍTULO: Cruceta de izaje

MATERIAL:	N° DIBUJO:	
SEGÚN TABLA	BB-11	A3


PESO:	ESCALA:	HOJA:
	INDICADAS	11 DE 17

POS.	CANT.	DESCRIPCIÓN	MATERIAL	OBSERVACIÓN
12.1	1	Bastidor fijo	ASTM A36	
12.2	1	Plato 900x 1000	ASTM A36	
12.3	1	Soporte del indicador	ASTM A36	
12.4	1	Celdas y caja de conexion	Suministro	4 celdas 200 kg
12.5	1	Indicador digital	Suministro	Rango neto 150 kg; lectura 50 g


Part. 12

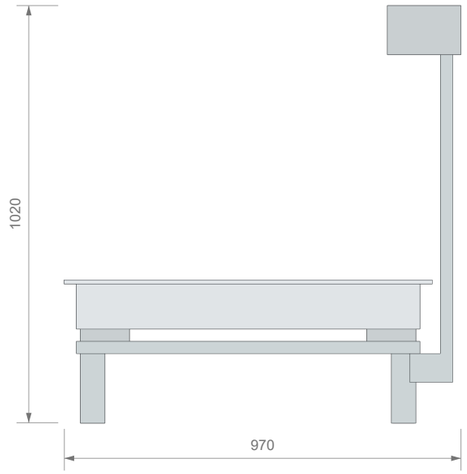


VISTA FRONTAL ESCALA 1:15

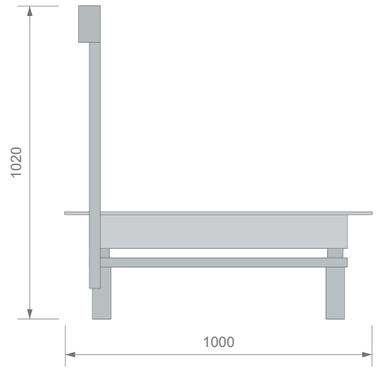

VISTA LATERAL ESCALA 1:20

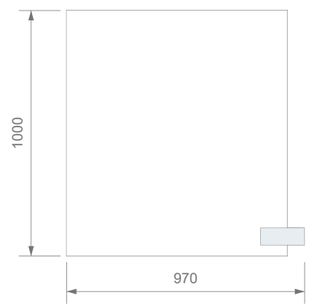

PLANTA ESCALA 1:25

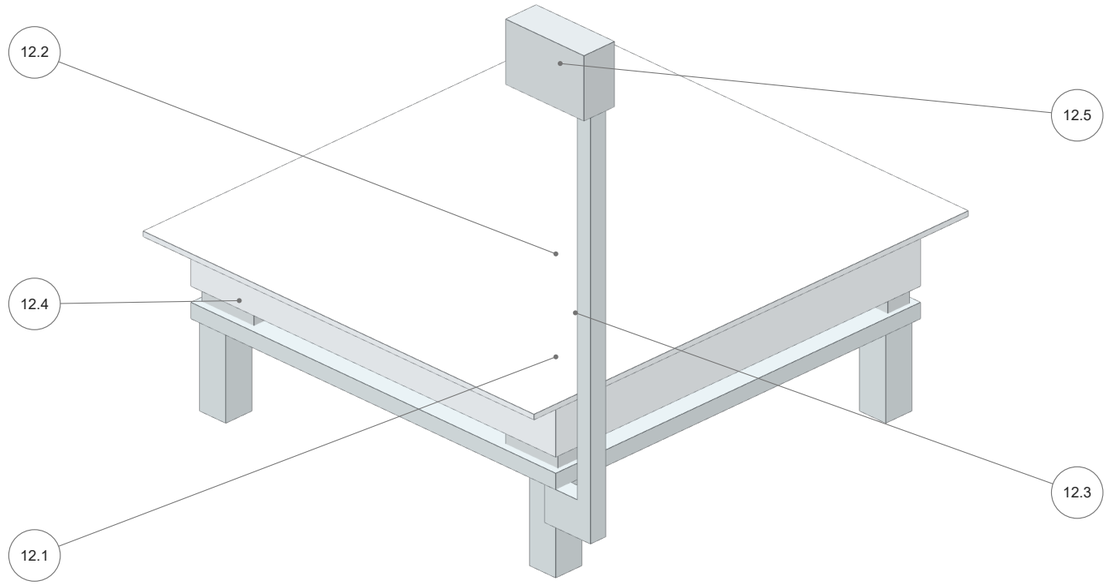

ISOMÉTRICA

Plato a Z350. Tara de plato 97,13 kg.
Calibrar despues del montaje de las cuatro celdas.

SESUVECA DEL PERÚ

	NOMBRE	FIRMA	FECHA
DIB.	Javier Acevedo		10/11/26
VERIF.			
APROB.			
FABR.			
CALID.			

PROYECTO: DESCARGA DE BIGBAGS

ELIMINAR REBABAS Y ARISTAS VIVAS | NO CAMBIE LA ESCALA | REVISIÓN


TÍTULO: Balanza de ensacado

MATERIAL: SEGÚN TABLA | N° DIBUJO: BB-12 | A3


PESO: | ESCALA: INDICADAS | HOJA: 12 DE 17

POS.	CANT.	DESCRIPCIÓN	MATERIAL	OBSERVACIÓN
13.1	1	Placa base 360x 360x 35; 4 Ø18	ASTM A36	
13.2	4	PasantesM16x 340	Clase 10.9	
13.3	8	TuercasM16	Clase 10	
13.4	8	Arandelas 50x 50x 10 Ø18	ASTM A36	
13.5	4	Contraplaca 150x 150x 18	ASTM A36	


Part. 13

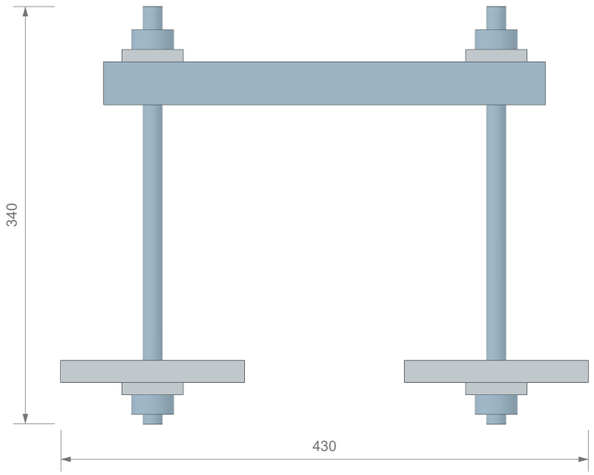


VISTA FRONTAL ESCALA 1:5

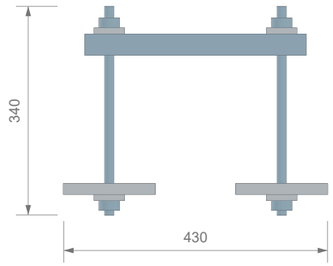

VISTA LATERAL ESCALA 1:10

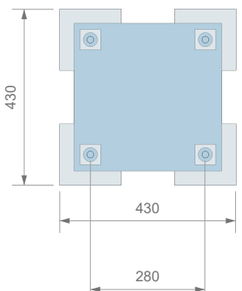

PLANTA ESCALA 1:15

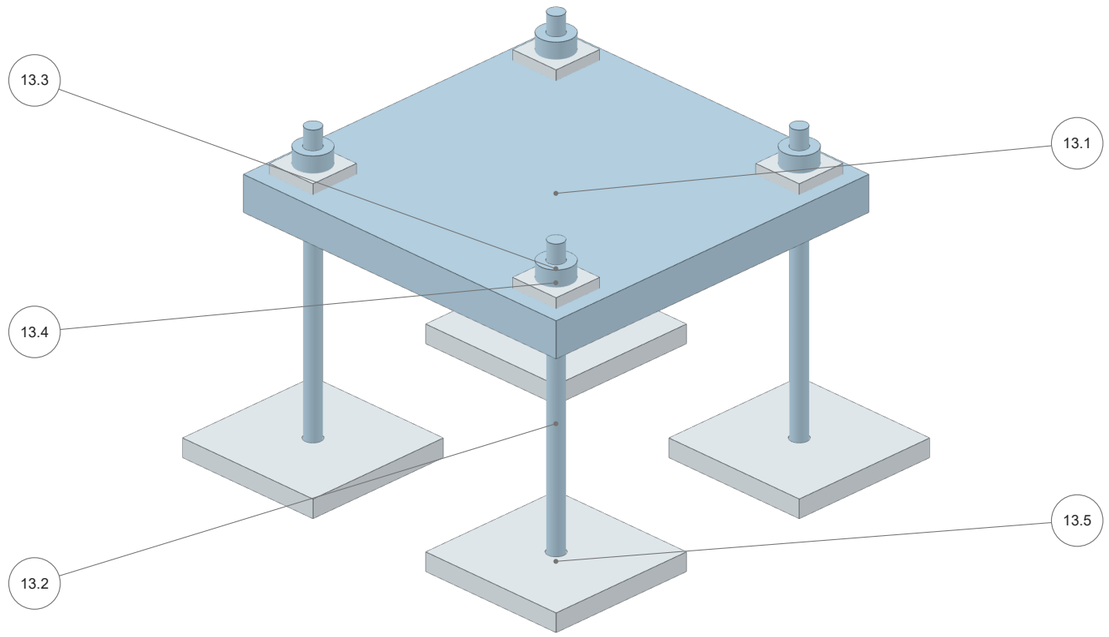

ISOMÉTRICA

Montaje con apoyo continuo de la placa.
Arandelas y contraplacas segun detalle.

SESUVECA DEL PERÚ

ELIMINAR REBABAS Y ARISTAS VIVAS	NO CAMBIE LA ESCALA	REVISIÓN

	NOMBRE	FIRMA	FECHA
DIB.	Javier Acevedo		10/11/26
VERIF.			
APROB.			
FABR.			
CALID.			


TÍTULO: Apoyo y anclaje metalico

MATERIAL:	N° DIBUJO:	
SEGÚN TABLA	BB-13	A3


PROYECTO:	PESO:	ESCALA:	HOJA:
DESCARGA DE BIGBAGS		INDICADAS	13 DE 17

POS.	CANT.	DESCRIPCIÓN	MATERIAL	OBSERVACIÓN
14.1	1	Placa superior 200x 236x 12	ASTM A36	
14.2	2	Laterales 200x 200x 12	ASTM A36	
14.3	4	Calces 200x 15x 6	ASTM A36	
14.4	4	Cartelas 100x 200x 12	ASTM A36	
14.5	4	Diafragmas del travesano	ASTM A36	
14.6	1	Travesano IPE 200 cerrado	ASTM A36	

Part. 14

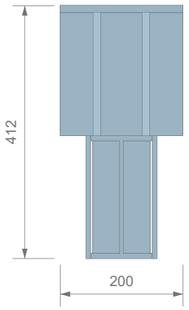


VISTA FRONTAL ESCALA 1:10

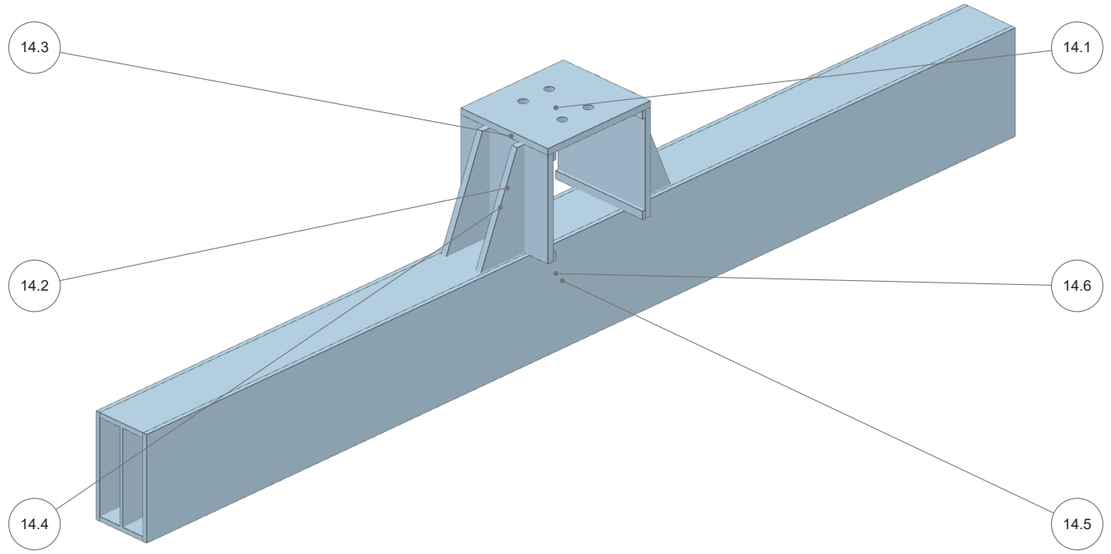

ISOMÉTRICA

VISTA LATERAL ESCALA 1:15

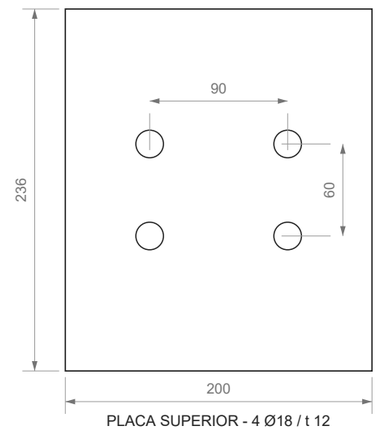

PLACA SUPERIOR - 4 Ø18 / t 12

Placa superior: 200 × 236 × 12; 4 Ø18, patrón 90 × 60.
Cartelas: filete z 6 en ambas caras. Diafragmas del IPE: filete z 4.

SESUVECA DEL PERÚ

	NOMBRE	FIRMA	FECHA
DIB.	Javier Acevedo		10/11/26
VERIF.			
APROB.			
FABR.			
CALID.			

PROYECTO: DESCARGA DE BIGBAGS

ELIMINAR REBABAS Y ARISTAS VIVAS | NO CAMBIE LA ESCALA | REVISIÓN


TÍTULO:

Unión del monorriel al travesano

MATERIAL: SEGÚN TABLA | N° DIBUJO: BB-14 | A3


PESO: | ESCALA: INDICADAS | HOJA: 14 DE 17

4 PANELES DE CUERPO

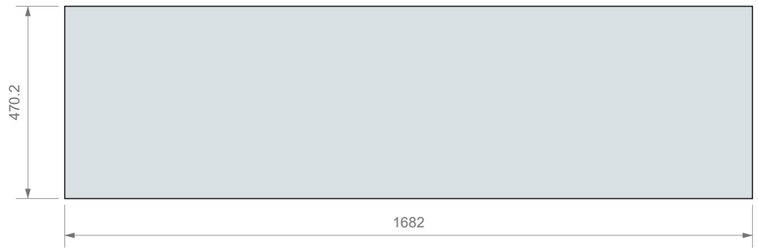

ASTM A36 / t 6 / ESCALA 1:15

4 PANELES DE CONO

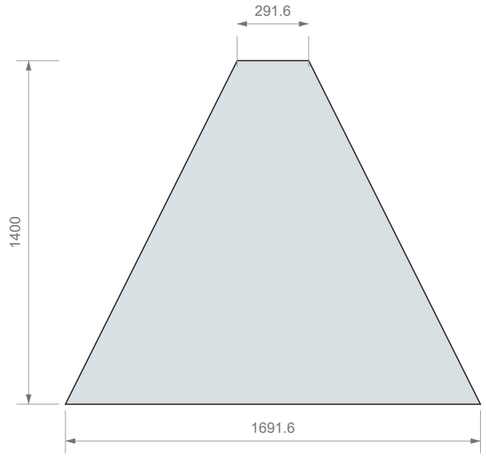

ASTM A36 / t 8 / ESCALA 1:25

4 FORROS DE CUERPO



UHMWPE / t 10 / ESCALA 1:15

4 FORROS DE CONO

UHMWPE / t 10 / ESCALA 1:30

Cotas de corte en mm. Cantidades para una tolva completa.

Montar el revestimiento después de soldar y limpiar el cuerpo.

SESUVECA DEL PERÚ

ELIMINAR REBABAS Y ARISTAS VIVAS	NO CAMBIE LA ESCALA	REVISIÓN

	NOMBRE	FIRMA	FECHA
DIB.	Javier Acevedo		10/11/26
VERIF.			
APROB.			
FABR.			
CALID.			

PROYECTO: DESCARGA DE BIGBAGS

TÍTULO:

Paneles y revestimiento de tolva

MATERIAL:	N° DIBUJO:	
SEGÚN TABLA	BB-15	A3

PESO:	ESCALA:	HOJA:
	INDICADAS	15 DE 17

PLANO	POS.	CANT.	PERFIL	L mm
BB-02	2.1	4	SHS 150x 150x 6	6668
BB-02	2.2	2	IPE 200	2000
BB-02	2.3	4	SHS 60x 60x 4	6435.8
BB-02	2.4	4	SHS 60x 60x 4	3038
BB-02	2.5	4	SHS 60x 60x 4	1466.6
BB-03	3.1	1	HEB 200	3600
BB-04	4.1	4	SHS 100x 100x 5	2848
BB-04	4.2	2	Macizo 60x 60	195
BB-04	4.2	1	Macizo 60x 60	350
BB-04	4.2	1	Macizo 60x 60	500
BB-04	4.2	1	Macizo 60x 60	1100
BB-04	4.2	2	SHS 150x 150x 6	1800
BB-04	4.2	2	SHS 150x 150x 6	2050
BB-04	4.2	2	SHS 60x 60x 4	1550
BB-04	4.2	1	SHS 60x 60x 4	1950
BB-04	4.3	4	RHS 100x 60x 6.3	1812
BB-04	4.3	4	RHS 150x 75x 5	1832
BB-04	4.3	4	SHS 100x 100x 5	1599.3
BB-04	4.4	2	SHS 60x 60x 4	2976.3
BB-04	4.5	4	SHS 60x 60x 4	62.4
BB-04	4.6	4	SHS 100x 100x 5	1900
BB-06	6.1	1	Redondo 40	40
BB-06	6.1	1	Redondo 40	245
BB-06	6.2	1	Redondo 16	300
BB-06	6.2	1	Redondo 20	695
BB-07	7.1	1	SHS 100x 100x 5	2570.6

PLANO	POS.	CANT.	PERFIL	L mm
BB-07	7.1	3	SHS 100x 100x 5	2578.6
BB-07	7.2	5	RHS 150x 75x 5	105
BB-07	7.2	1	RHS 150x 75x 5	1620
BB-07	7.2	2	RHS 150x 75x 5	1780
BB-07	7.2	5	SHS 60x 60x 4	725
BB-07	7.3	2	SHS 60x 60x 4	2914.3
BB-07	7.4	2	Macizo 40x 60	60
BB-07	7.4	2	RHS 60x 40x 4	257.4
BB-07	7.4	2	SHS 50x 50x 4	67.7
BB-07	7.4	2	SHS 60x 60x 4	250
BB-07	7.4	2	SHS 60x 60x 4	760
BB-07	7.4	4	SHS 60x 60x 4	1075
BB-07	7.4	1	SHS 60x 60x 4	1300
BB-07	7.4	1	SHS 60x 60x 4	1700
BB-07	7.4	1	SHS 60x 60x 4	3000
BB-08	8.1	2	RHS 150x 75x 5	4728.1
BB-09	9.1	6	CHS 60.3x 4	1107
BB-09	9.1	1	CHS 60.3x 4	1127
BB-09	9.1	8	CHS 60.3x 4	1174.6
BB-09	9.2	1	CHS 48.3x 3	108.6
BB-09	9.2	2	CHS 48.3x 3	263.9
BB-09	9.2	2	CHS 48.3x 3	608.9
BB-09	9.2	2	CHS 48.3x 3	633.9
BB-09	9.2	2	CHS 48.3x 3	813.9
BB-09	9.2	24	CHS 48.3x 3	1105.9
BB-09	9.3	2	CHS 42.4x 3	602.4

Longitudes de corte en mm. Columnas y riostras longitudinales de una sola barra.

Presentar ingletes y encuentros antes de soldar. Corte recto: ±2 mm.

SESUVECA DEL PERÚ

	NOMBRE	FIRMA	FECHA
DIB.	Javier Acevedo		10/11/26
VERIF.			
APROB.			
FABR.			
CALID.			

PROYECTO: DESCARGA DE BIGBAGS

ELIMINAR REBABAS Y ARISTAS VIVAS | NO CAMBIE LA ESCALA | REVISIÓN

TÍTULO:

Lista de cortes de perfiles

MATERIAL: SEGÚN TABLA | N° DIBUJO: BB-C1 | A3

PESO: | ESCALA: INDICADAS | HOJA: 16 DE 17

PLANO	POS.	CANT.	PERFIL	L mm
BB-09	9.3	1	CHS 42.4x 3	802.7
BB-09	9.3	1	CHS 42.4x 3	802.9
BB-09	9.5	1	SHS 40x 40x 3	1725
BB-10	10.1	6	CHS 42.4x 3	937.1
BB-10	10.1	4	CHS 60.3x 4	1097
BB-10	10.2	2	CHS 42.4x 3	912.1
BB-10	10.2	2	CHS 60.3x 4	1097
BB-10	10.3	4	CHS 42.4x 3	727.1
BB-10	10.3	3	CHS 60.3x 4	1097
BB-10	10.4	2	CHS 42.4x 3	377.1
BB-10	10.4	2	CHS 42.4x 3	537.1
BB-10	10.4	4	CHS 60.3x 4	1097
BB-10	10.5	2	CHS 42.4x 3	167.1
BB-10	10.5	2	CHS 42.4x 3	332.1
BB-10	10.5	1	CHS 42.4x 3	429.3
BB-10	10.5	1	CHS 42.4x 3	433.2
BB-10	10.5	1	CHS 42.4x 3	459.3
BB-10	10.5	1	CHS 42.4x 3	463
BB-10	10.5	3	CHS 60.3x 4	1097
BB-11	11.1	2	SHS 150x 150x 6	1200
BB-11	11.2	1	SHS 150x 150x 6	887.5

Longitudes de corte en mm. Columnas y riostras longitudinales de una sola barra.

Presentar ingletes y encuentros antes de soldar. Corte recto: ±2 mm.

SESUVECA DEL PERÚ

	NOMBRE	FIRMA	FECHA
DIB.	Javier Acevedo		10/11/26
VERIF.			
APROB.			
FABR.			
CALID.			

PROYECTO: DESCARGA DE BIGBAGS

ELIMINAR REBABAS Y ARISTAS VIVAS

NO CAMBIE LA ESCALA

REVISIÓN

TÍTULO:

Lista de cortes de perfiles

MATERIAL: SEGÚN TABLA

N° DIBUJO: BB-C2

A3

PESO:

ESCALA: INDICADAS

HOJA: 17 DE 17