
ESTACION BIGBAG / REDISEÑO P05 /20-10-2026

Conjunto	Detalle vigente	Verificación
U02	Cartela18, ranura20, collar12; dos cordones pata9 conL158mín.	Capacidad24.921kN >18.100kN.
Monorriel/topes	Tope45 ydos rigidizadores12; duplicadores superiores12x300 con2f6x300.	16 controlesLX conformes a18kN.
Cimentación	52M16L340; arandelasA36 50x50x10; tuercasbrida10;33contraplacas t18.	FS2.014 N+V condicionado; losa global y flexión de perno no acreditadas.
Amortiguador	TR83 insuficiente; reserva envolvente TR100-60 preliminar.	No curva pico ni fijaciónOEM acreditadas. No fabricar perfil desde cajaCAD.
Control	RZ1-K4x4+PE; EUCHNER084820; FestoHGL530031/5-2 575511.	Ver esquemasA3; capacidad1t de mesa no acreditada.
Colector	800m3/h,1500Pa,2.2kW;V1.2;panelpropuesto0.15m2;B-FlapDN150.	ObjetivoPred0.25bar; no certificaciónNFPA68/ATEX.
Cotas ymodelo	Fondo bolsa3520;210piezas/889posiciones enSTEP actual.	Formato importado aceptado; sincronización nativa actual verificada.

Las hojas siguientes contienen la geometría del rediseño. El alcance real y los resultados están en la memoria vigente. SIN LIBERACIÓN INTEGRAL.


Estación Bigbag / Conjunto general

ALZADO LONGITUDINAL ESCALA 1:40

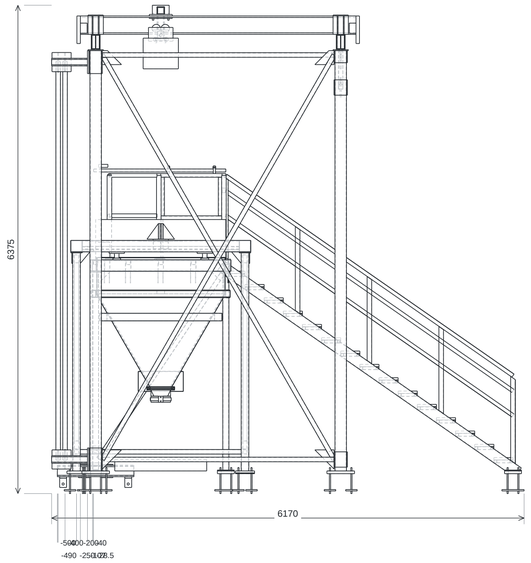

REFERENCIA X (mm)

ALZADO TRANSVERSAL ESCALA 1:50

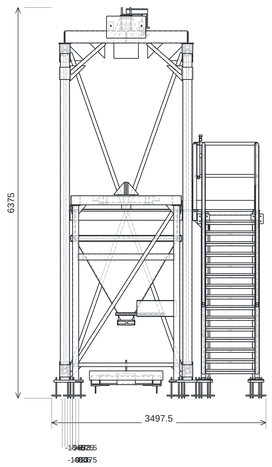

REFERENCIA Y (mm)

CONJUNTO	PLANO
Cimentación y placas base	EB-02
Pórticos transversales ensamblados	EB-03
Arriostramiento longitudinal y uniones	EB-04
Viga carril y topes de fin de carrera	EB-05
Bastidor de tolva ensamblado	EB-06
Tolva, anillos y revestimiento	EB-07
Cortador y parrilla de apoyo de bolsa	EB-08
Compuerta de descarga ensamblada	EB-09
Guarda, ensacado y captación	EB-10
Carro, suspensión y traba de posición	EB-11
Plataforma de acceso ensamblada	EB-12
Escalera y desembarco ensamblados	EB-13
Barandas, pasamanos y rodapiés	EB-14
Cruceta de izaje 2 t ensamblada	EB-15

ISOMÉTRICO A COLOR / REFERENCIA DE MONTAJE



NOTAS DE FABRICACIÓN Y MONTAJE


1. Cruceta y tecle nominales 2 t; proceso de bolsas de 1 t.
2. Traslado con fondo de bolsa a Z = 3 520; guarda superior Z = 3 430; punta de cortador Z = 3 230.
3. Enclavamientos, prueba de carga y recepción según memoria.
4. POS.: número de pieza en la lista de 210 piezas únicas.

Cotas en mm. ISO2768-m. Soldaduras según cuadro JF. Contornos: CAD/DXF.


				REBABAR Y ROMPER ARISTAS	NO CAMBIAR LA ESCALA	REVISIÓN
SESUVECA DEL PERÚ						
	NOMBRE	FIRMA	FECHA			TÍTULO: Estación Bigbag / Conjunto general
DIBUJ.	Javier Acevedo		20/10/26			
VERIF.						
APROB.						
FABR.						
CALID.				MATERIAL: SEGÚN LISTA DE MATERIALES		N.º DE DIBUJO EB-01 / A1
PESO: SEGÚN CAD / lista de materiales				ESCALA: INDICADA		ESTACIÓN DE DESCARGA BIGBAG / HOJA 1 DE 16

Cimentación y placas base

PLANTA ESCALA 1:20

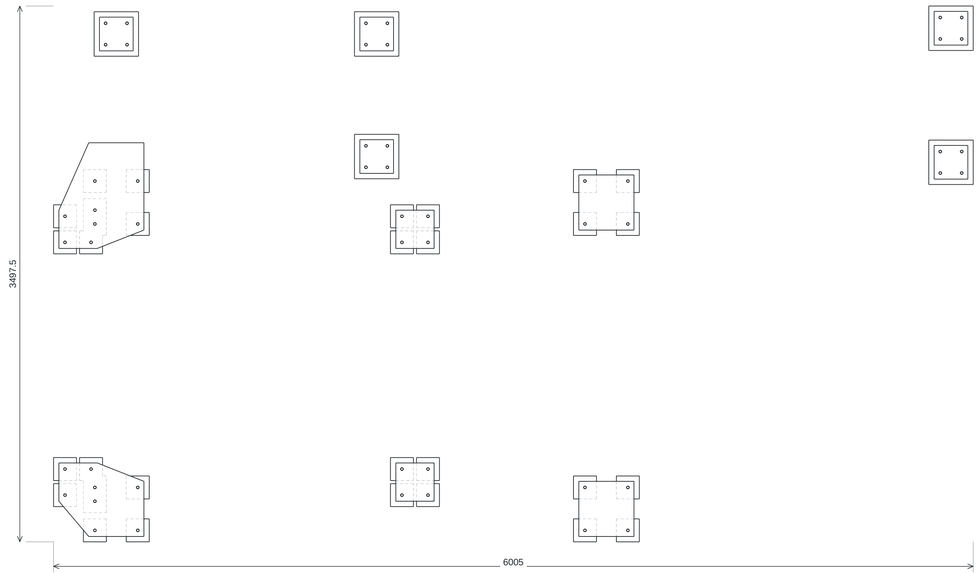


ALZADO ESCALA 1:20

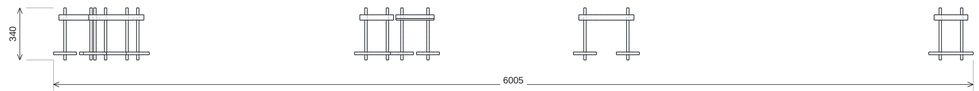

POS.	CANT.	PIEZA / MEDIDAS EN mm	MATERIAL / SUMINISTRO
22	2	Placa base de columna principal; ancho 360; alto 360; espesor 35; taladros Ø18	ASTM A36 / Fabricar
23	2	Placa base de pata de tolva; ancho 250; alto 250; espesor 25; taladros Ø18	ASTM A36 / Fabricar
99	1	Placa base compartida de columnas; ancho 555; alto 480; espesor 35; taladros Ø18	ASTM A36 / Fabricar
100	1	Placa base compartida de columnas; ancho 555; alto 690; espesor 35; taladros Ø18	ASTM A36 / Fabricar
101	20	Arandela M16; largo 3; pared 6; Ø exterior 30; Ø interior 18	Acero 200HV / ISO7089 / Comprar
102	20	Tuerca M16; Rosca M16; clase 8	Acero clase 8 / ISO898-2 / Comprar
195	52	Esparrago pasante M16 clase 8.8; M16 x 340; paso 2; clase 8.8; rosca no representada	ISO 898-1 clase 8.8 certificado / Comprar
196	2	Placa separadora pasante base tolva; ancho 250; alto 250; espesor 10; taladros Ø18	ASTM A36 / Fabricar
199	104	Arandela estructural A36 soldable; 50x50x10; D18	ASTM A36 / Fabricar
200	104	Tuerca con brida lisa M16 clase10; M16x2; dc<=34.5; dw>=31.9; m<=16	ISO898-2 clase10 / Comprar
202	5	Placa separadora pasante ac base; ancho 220; alto 220; espesor 35; taladros Ø18	ASTM A36 / Fabricar
203-207	5	Contraplaca inferior A36; ancho 290; alto 290; espesor 18; taladros Ø18	ASTM A36 / Fabricar
208	26	Contraplaca inferior A36; ancho 150; alto 150; espesor 18; taladros Ø18	ASTM A36 / Fabricar
209	1	Contraplaca inferior A36; ancho 175; alto 360; espesor 18; taladros Ø18	ASTM A36 / Fabricar
210	1	Contraplaca inferior A36; ancho 175; alto 360; espesor 18; taladros Ø18	ASTM A36 / Fabricar

ISOMÉTRICO A COLOR / REFERENCIA DE MONTAJE

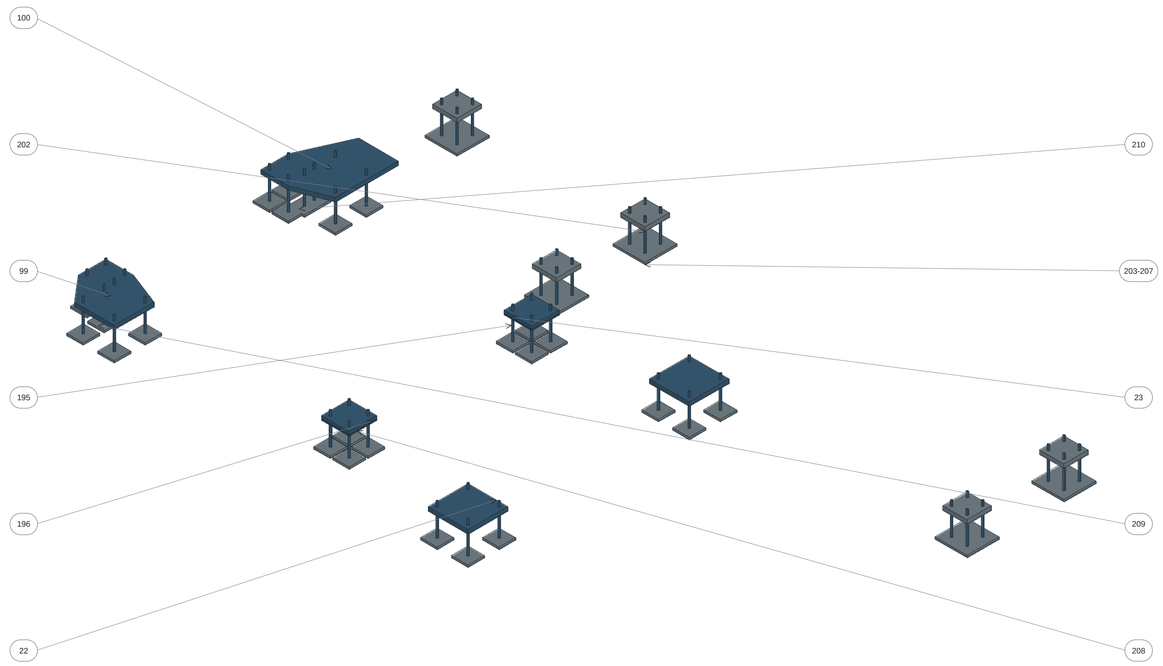

NOTAS DE FABRICACIÓN Y MONTAJE

1. Losa: espesor 200 mm; cara inferior accesible. Cotas adoptadas Z -43 / -243.
2. 52 pasantes M16 8.8 L340; 33 contraplacas A36 t18, simples150 y comunes segun contorno CAD.
3. Replanteo global: Z0 es referencia del equipo; cara superior de losa Z -43. Verificar bordes y armaduras reales.
4. Arandelas A36 50x50x10 D18: superior a5 perimetral, inferior libre; tuercas brida lisa M16 clase10.

Cotas en mm. ISO2768-m. Soldaduras según cuadro JF. Contornos: CAD/DXF.


TALADROS DE PIEZAS DEL CONJUNTO / COORDENADAS LOCALES mm / ORIGEN LOCAL

P22 T1: Ø18; X-140 Y-140 Z0; eje Z
P22 T2: Ø18; X-140 Y140 Z0; eje Z
P22 T3: Ø18; X140 Y-140 Z0; eje Z
P22 T4: Ø18; X140 Y140 Z0; eje Z
P23 T1: Ø18; X-85 Y-85 Z0; eje Z
P23 T2: Ø18; X-85 Y85 Z0; eje Z
P23 T3: Ø18; X85 Y-85 Z0; eje Z
P23 T4: Ø18; X85 Y85 Z0; eje Z
P99 T1: Ø18; X-140 Y-140 Z0; eje Z
P99 T2: Ø18; X-140 Y140 Z0; eje Z
P99 T3: Ø18; X140 Y-140 Z0; eje Z
P99 T4: Ø18; X140 Y140 Z0; eje Z
P99 T5: Ø18; X140 Y50 Z0; eje Z
P99 T6: Ø18; X165 Y260 Z0; eje Z
P99 T7: Ø18; X335 Y90 Z0; eje Z
P99 T8: Ø18; X335 Y260 Z0; eje Z
P100 T1: Ø18; X-140 Y-140 Z0; eje Z
P100 T2: Ø18; X-140 Y140 Z0; eje Z
P100 T3: Ø18; X140 Y-140 Z0; eje Z
P100 T4: Ø18; X140 Y140 Z0; eje Z
P100 T5: Ø18; X165 Y-260 Z0; eje Z
P100 T6: Ø18; X140 Y-50 Z0; eje Z
P100 T7: Ø18; X335 Y-260 Z0; eje Z
P100 T8: Ø18; X335 Y-90 Z0; eje Z
P196 T1: Ø18; X-85 Y-85 Z0; eje Z
P196 T2: Ø18; X-85 Y85 Z0; eje Z
P196 T3: Ø18; X85 Y-85 Z0; eje Z
P196 T4: Ø18; X85 Y85 Z0; eje Z
P199 T1: Ø18; X0 Y0 Z0; eje Z
P202 T1: Ø18; X-70 Y-70 Z0; eje Z
P202 T2: Ø18; X70 Y-70 Z0; eje Z
P202 T3: Ø18; X70 Y70 Z0; eje Z
P202 T4: Ø18; X-70 Y70 Z0; eje Z
P203 T1: Ø18; X-70 Y-70 Z0; eje Z
P203 T2: Ø18; X-70 Y70 Z0; eje Z
P203 T3: Ø18; X70 Y-70 Z0; eje Z
P203 T4: Ø18; X70 Y70 Z0; eje Z
P204 T1: Ø18; X-70 Y-70 Z0; eje Z
P204 T2: Ø18; X-70 Y70 Z0; eje Z
P204 T3: Ø18; X70 Y-70 Z0; eje Z
P204 T4: Ø18; X70 Y70 Z0; eje Z
P205 T1: Ø18; X-70 Y-70 Z0; eje Z
P205 T2: Ø18; X-70 Y70 Z0; eje Z
P205 T3: Ø18; X70 Y-70 Z0; eje Z
P205 T4: Ø18; X70 Y70 Z0; eje Z
P206 T1: Ø18; X-70 Y-70 Z0; eje Z
P206 T2: Ø18; X-70 Y70 Z0; eje Z
P206 T3: Ø18; X70 Y-70 Z0; eje Z
P206 T4: Ø18; X70 Y70 Z0; eje Z
P207 T1: Ø18; X-70 Y-70 Z0; eje Z
P207 T2: Ø18; X-70 Y70 Z0; eje Z
P207 T3: Ø18; X70 Y-70 Z0; eje Z
P207 T4: Ø18; X70 Y70 Z0; eje Z
P208 T1: Ø18; X0 Y0 Z0; eje Z
P209 T1: Ø18; X12.5 Y-15 Z0; eje Z
P209 T2: Ø18; X12.5 Y-105 Z0; eje Z
P209 T3: Ø18; X-12.5 Y105 Z0; eje Z
P210 T1: Ø18; X12.5 Y15 Z0; eje Z
P210 T2: Ø18; X-12.5 Y-105 Z0; eje Z
P210 T3: Ø18; X12.5 Y105 Z0; eje Z

				REBABAR Y ROMPER ARISTAS	NO CAMBIAR LA ESCALA	REVISIÓN
SESUVECA DEL PERÚ						
	NOMBRE	FIRMA	FECHA			TÍTULO: Cimentación y placas base
DIBUJ.	Javier Acevedo		20/10/26			
VERIF.						
APROB.						
FABR.						
CALID.				MATERIAL: SEGÚN LISTA DE MATERIALES		N.º DE DIBUJO EB-02 / A1
PESO: SEGÚN CAD / lista de materiales				ESCALA: INDICADA		ESTACIÓN DE DESCARGA BIGBAG / HOJA 2 DE 16


Pórticos transversales ensamblados

PERFIL ESCALA 1:40

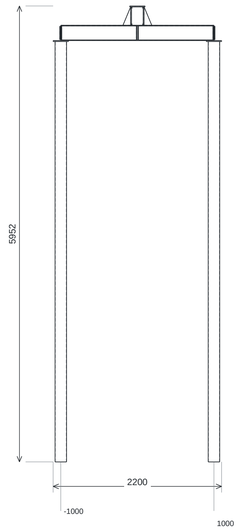


REFERENCIA Y (mm)

PLANTA ESCALA 1:15

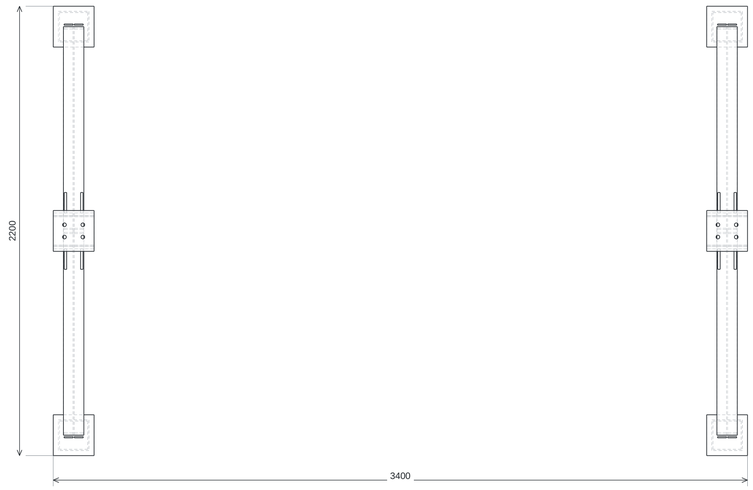

POS.	CANT.	PIEZA / MEDIDAS EN mm	MATERIAL / SUMINISTRO
1	4	Tramo de tubo cuadrado; ancho 150; alto 150; largo 5488; pared 6	ASTM A500 Gr.B / Fabricar
2	2	Viga transversal IPE 200; ancho 100; alto 200; largo 2000; pared 5.6; espesor ala 8.5	ASTM A36 / Fabricar
24	2	Placa superior de unión a viga; ancho 200; alto 200; espesor 12; taladros Ø18	ASTM A36 / Fabricar
25	4	Placa lateral de unión a viga; ancho 200; alto 240; espesor 12	ASTM A36 / Fabricar
26	8	Placa separadora de unión a viga; ancho 200; alto 20; espesor 6	ASTM A36 / Fabricar
27	24	Placa de refuerzo de unión a viga; ancho 44; alto 175; espesor 6	ASTM A36 / Fabricar
28	8	Refuerzo triangular de unión a viga; ancho 100; alto 240; espesor 12	ASTM A36 / Fabricar
29	4	Tapa de columna principal; ancho 200; alto 200; espesor 12	ASTM A36 / Fabricar

ISOMÉTRICO A COLOR / REFERENCIA DE MONTAJE

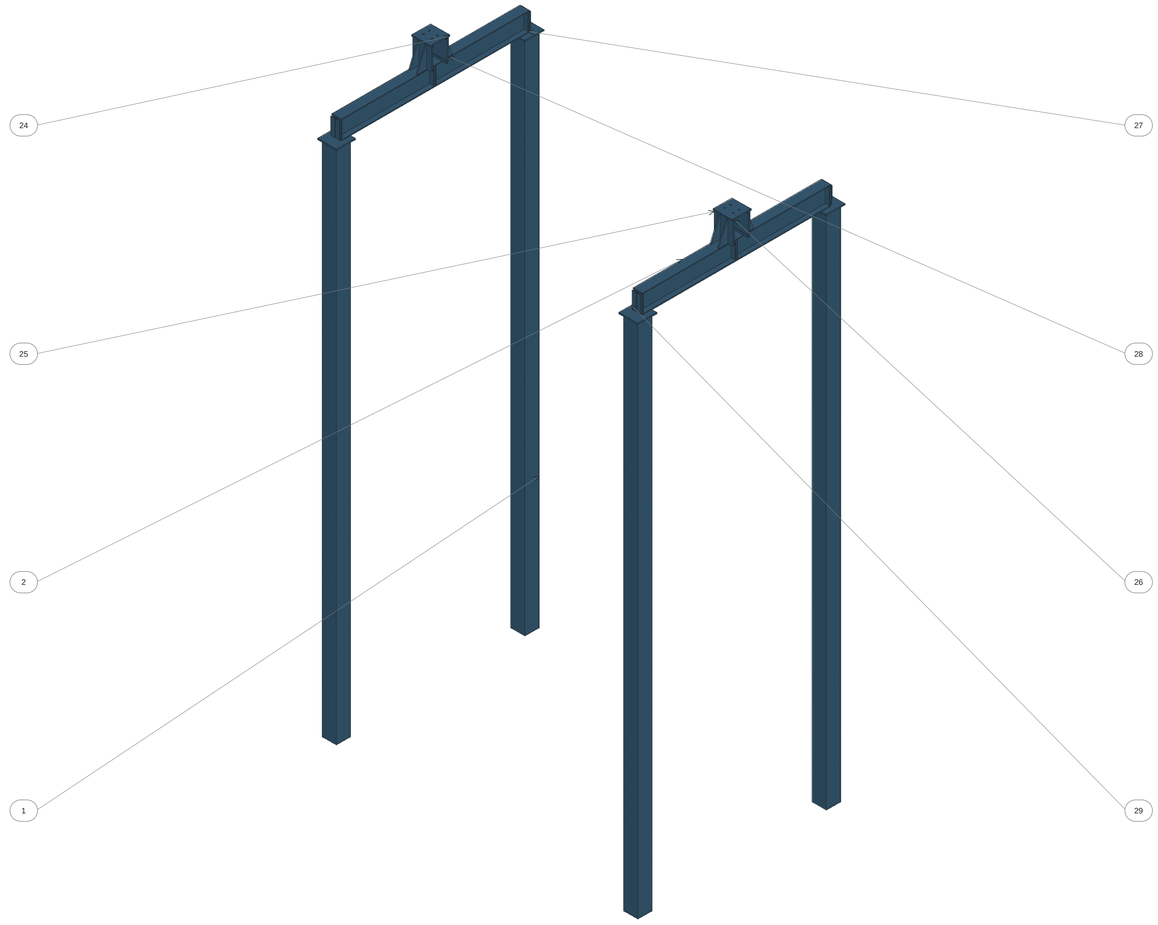

NOTAS DE FABRICACIÓN Y MONTAJE

1. Dos pórticos, ejes X = 0 y 3 200; separación Y = 2 000 entre columnas.
2. Columnas SHS150x150x6; travesaños IPE200. Chapas de unión U01 / P01 según lista de materiales.
3. Cotas referidas a la posición nominal montada. Soldadura de taller; montaje desmontable según detalle.

Cotas en mm. ISO2768-m. Soldaduras según cuadro JF. Contornos: CAD/DXF.

TALADROS DE PIEZAS DEL CONJUNTO / COORDENADAS LOCALES mm / ORIGEN LOCAL


P24 T1: Ø18; X-45 Y-30 Z0; eje Z
P24 T2: Ø18; X-45 Y30 Z0; eje Z
P24 T3: Ø18; X45 Y-30 Z0; eje Z
P24 T4: Ø18; X45 Y30 Z0; eje Z

				REBABAR Y ROMPER ARISTAS	NO CAMBIAR LA ESCALA	REVISIÓN
SESUVECA DEL PERÚ						
	NOMBRE	FIRMA	FECHA			TÍTULO: Pórticos transversales ensamblados
DIBUJ.	Javier Acevedo		20/10/26			
VERIF.						
APROB.						
FABR.						
CALID.				MATERIAL: SEGÚN LISTA DE MATERIALES		N.º DE DIBUJO EB-03 / A1
PESO: SEGÚN CAD / lista de materiales				ESCALA: INDICADA		ESTACIÓN DE DESCARGA BIGBAG / HOJA 3 DE 16

REVISION P05 - REDISENO20/10/2026 - ALCANCE VERIFICADO EN MEMORIA - SIN LIBERACION INTEGRAL


Arriostramiento longitudinal y uniones

ALZADO ESCALA 1:40

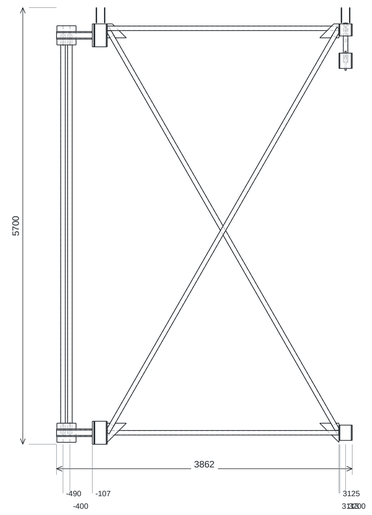


REFERENCIA X (mm)

PLANTA ESCALA 1:15

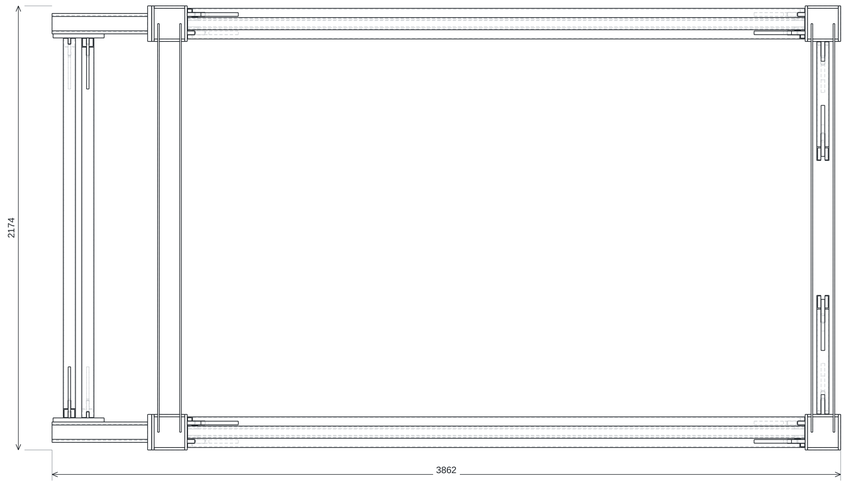

POS.	CANT.	PIEZA / MEDIDAS EN mm	MATERIAL / SUMINISTRO
30	8	Placa de unión de diagonal a columna; ancho 150; alto 200; espesor 12	ASTM A36 / Fabricar
31	8	Placa de unión de diagonal a columna; ancho 174; alto 200; espesor 12	ASTM A36 / Fabricar
32	4	Placa de unión de diagonal a columna; ancho 150; alto 158; espesor 12	ASTM A36 / Fabricar
33	4	Placa de unión de diagonal a columna; ancho 174; alto 158; espesor 12	ASTM A36 / Fabricar
34-45	12	Refuerzo triangular de diagonal; ancho 250; alto 250; espesor 18	ASTM A36 / Fabricar
103	4	Placa de cierre de viga transversal; ancho 2000; alto 200; espesor 8	ASTM A36 / Fabricar
126,129	2	Diagonal de refuerzo longitudinal; ancho 60; alto 60; largo 5499.97; pared 4	ASTM A500 Gr.B / Fabricar
127-128,130-131	4	Placa de unión de diagonal; ancho 250; alto 250; espesor 12	ASTM A36 / Fabricar
132	8	Placa de unión a columna; ancho 150; alto 300; espesor 12	ASTM A36 / Fabricar
133	8	Placa de unión a columna; ancho 174; alto 300; espesor 12	ASTM A36 / Fabricar
134	4	Placa de refuerzo de columna; ancho 174; alto 300; espesor 20	ASTM A36 / Fabricar
135	4	Brazo lateral de refuerzo; ancho 100; alto 100; largo 468; pared 10	S355NH / EN10210-1 / Fabricar
136	4	Placa exterior de unión; ancho 250; alto 250; espesor 20	ASTM A36 / Fabricar
148-149,151-152	4	Tramo de tubo cuadrado; ancho 60; alto 60; largo 6085.65; pared 4	ASTM A500 Gr.B / Fabricar
150,153	2	Tramo de tubo cuadrado; ancho 60; alto 60; largo 748.81; pared 4	ASTM A500 Gr.B / Fabricar
154-157	4	Tramo de tubo cuadrado; ancho 60; alto 60; largo 3050; pared 4	ASTM A500 Gr.B / Fabricar

ISOMÉTRICO A COLOR / REFERENCIA DE MONTAJE

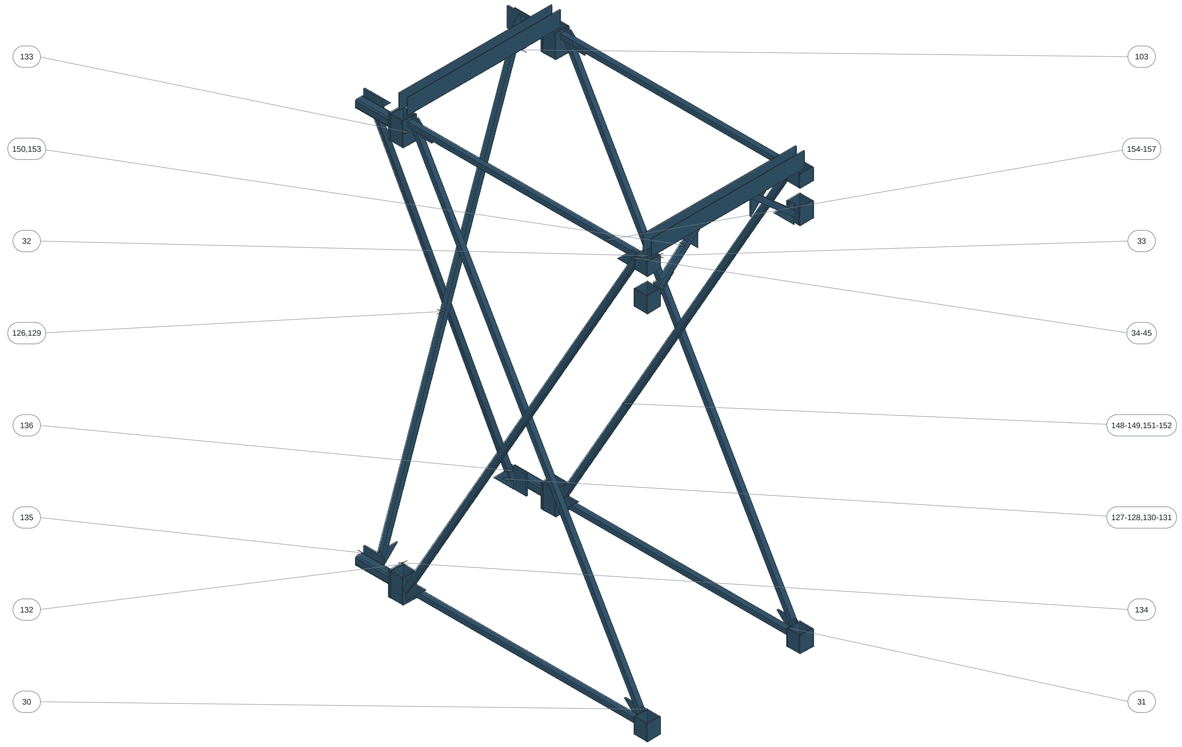

NOTAS DE FABRICACIÓN Y MONTAJE


1. Dos planos longitudinales Y = -1 000 y +1 000. Luz entre pórticos: 3 200.
2. Conservar ranuras y recortes de extremos; no soldar las holguras JF identificadas como LUZ.
3. Collares, lengüetas y diagonales: preparaciones según CAD; mantener holguras libres de soldadura.
4. Cartelas U02 t18 y ranuras20; collares12. Envolvente longitudinal18kN; WPS AWS D1.1 E7018/ER70S-6.

Cotas en mm. ISO2768-m. Soldaduras según cuadro JF. Contornos: CAD/DXF.

				REBABAR Y ROMPER ARISTAS	NO CAMBIAR LA ESCALA	REVISIÓN
SESUVECA DEL PERÚ						
	NOMBRE	FIRMA	FECHA			TÍTULO: Arriostramiento longitudinal y uniones
DIBUJ.	Javier Acevedo		20/10/26			
VERIF.						
APROB.						
FABR.						
CALID.				MATERIAL: SEGÚN LISTA DE MATERIALES		N.º DE DIBUJO EB-04 / A1
PESO: SEGÚN CAD / lista de materiales				ESCALA: INDICADA		ESTACIÓN DE DESCARGA BIGBAG / HOJA 4 DE 16


Viga carril y topes de fin de carrera

ALZADO ESCALA 1:15

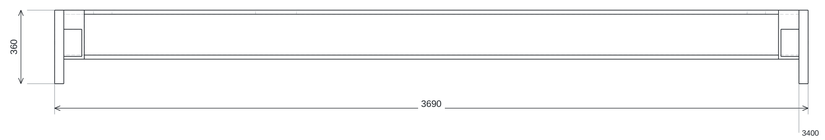


REFERENCIA X (mm)

PLANTA ESCALA 1:15

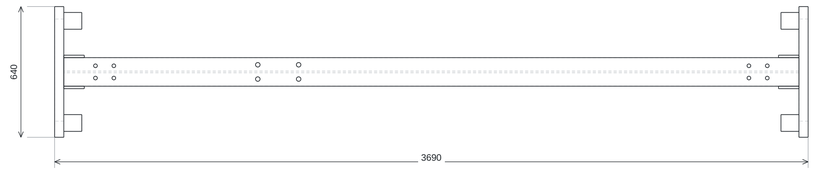

POS.	CANT.	PIEZA / MEDIDAS EN mm	MATERIAL / SUMINISTRO
3	1	Viga carril I soldada 240×140; ancho 140; alto 240; largo 3600; pared 8; espesor ala 20; taladros Ø18, Ø22	ASTM A36 / Fabricar
147	4	Reserva de espacio ACE TR100-60; A88 x B82 x D133; carrera60; referencia radial	Copoliester; envolvente preliminar / Comprar
197	2	Placa de respaldo de amortiguador; ancho 640; alto 360; espesor 45; taladros Ø18	ASTM A36 / Fabricar
198	4	Tope placa de refuerzo terminal; ancho 100; alto 240; espesor 12	ASTM A36 / Fabricar

ISOMÉTRICO A COLOR / REFERENCIA DE MONTAJE

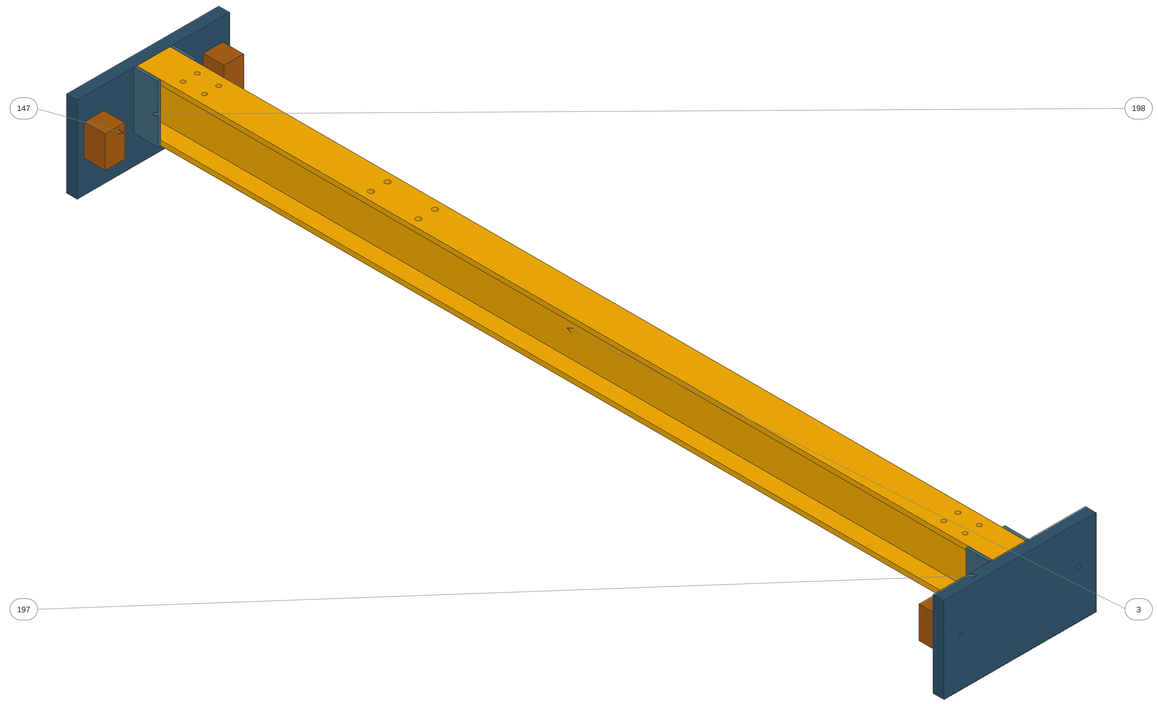

NOTAS DE FABRICACIÓN Y MONTAJE

1. Viga fabricada I240x140x8x20; longitud 3 600; ala de rodadura 140 x 20.
2. Placas de reaccion640x360x45; dos rigidizadores12 por extremo, CJP al rail.
3. Reservas de espacio TR100-60: preseleccion, curva y fijacion NO acreditadas; E224.04J, v0.35m/s.
4. Montaje KITO y topes: ver especificación y memoria.
5. Perfil 240 × 140 × 8 fabricado: 1 tiras 200 × 8 + 2 tiras 140 × 20 de ASTM A36. Cuatro soldaduras longitudinales que atraviesan el espesor completo.

Cotas en mm. ISO2768-m. Soldaduras según cuadro JF. Contornos: CAD/DXF.


TALADROS DE PIEZAS DEL CONJUNTO / COORDENADAS LOCALES mm / ORIGEN LOCAL

P3 B1: Ø18; X-30 Y95 Z155; eje Y
P3 B2: Ø18; X30 Y95 Z155; eje Y
P3 B3: Ø18; X-30 Y95 Z245; eje Y
P3 B4: Ø18; X30 Y95 Z245; eje Y
P3 B5: Ø18; X-30 Y95 Z3355; eje Y
P3 B6: Ø18; X30 Y95 Z3355; eje Y
P3 B7: Ø18; X-30 Y95 Z3445; eje Y
P3 B8: Ø18; X30 Y95 Z3445; eje Y
P3 B9: Ø22; X-35 Y99 Z2450; eje Y
P3 B10: Ø22; X35 Y99 Z2450; eje Y
P3 B11: ØZ2; X-35 Y99 Z2650; eje Y
P3 B12: Ø22; X35 Y99 Z2650; eje Y
P197 T1: Ø18; X-250 Y20 Z0; eje Z
P197 T2: Ø18; X250 Y20 Z0; eje Z

				REBABAR Y ROMPER ARISTAS	NO CAMBIAR LA ESCALA	REVISIÓN
SESUVECA DEL PERÚ						
	NOMBRE	FIRMA	FECHA			TÍTULO: Viga carril y topes de fin de carrera
DIBUJ.	Javier Acevedo		20/10/26			
VERIF.						
APROB.						
FABR.						
CALID.				MATERIAL: SEGÚN LISTA DE MATERIALES		N.º DE DIBUJO EB-05 / A1
PESO: SEGÚN CAD / lista de materiales				ESCALA: INDICADA		ESTACIÓN DE DESCARGA BIGBAG / HOJA 5 DE 16


Bastidor de tolva ensamblado

ALZADO ESCALA 1:20

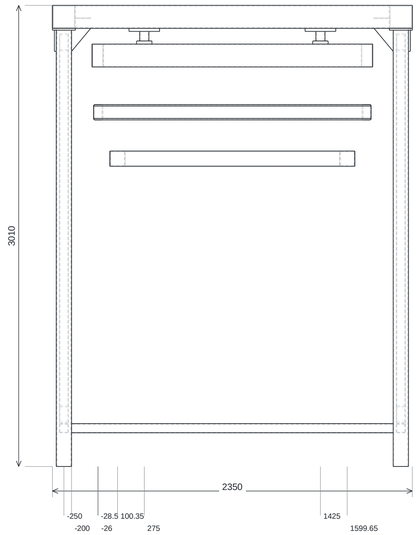


REFERENCIA X (mm)

PLANTA ESCALA 1:15

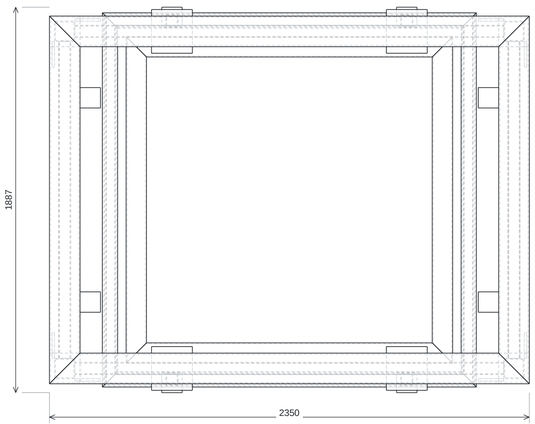

POS.	CANT.	PIEZA / MEDIDAS EN mm	MATERIAL / SUMINISTRO
4	4	Tramo de tubo cuadrado; ancho 100; alto 100; largo 2848; pared 5	ASTM A500 Gr.B / Fabricar
5	2	Tramo de tubo cuadrado; ancho 150; alto 150; largo 2200; pared 6	ASTM A500 Gr.B / Fabricar
6	2	Tramo de tubo cuadrado; ancho 150; alto 150; largo 1650; pared 6	ASTM A500 Gr.B / Fabricar
7	2	Tramo de tubo cuadrado; ancho 60; alto 60; largo 2100; pared 4	ASTM A500 Gr.B / Fabricar
8	2	Tramo de tubo cuadrado; ancho 60; alto 60; largo 1550; pared 4	ASTM A500 Gr.B / Fabricar
9	4	Tramo de tubo cuadrado; ancho 100; alto 100; largo 1499.3; pared 5	ASTM A500 Gr.B / Fabricar
10-11	4	Tramo de tubo rectangular; ancho 75; alto 150; largo 1757; pared 5	ASTM A500 Gr.B / Fabricar
12	2	Tramo de tubo cuadrado; ancho 60; alto 60; largo 2882.26; pared 4	ASTM A500 Gr.B / Fabricar
16	4	Tramo de tubo cuadrado; ancho 60; alto 60; largo 62.41; pared 4	ASTM A500 Gr.B / Fabricar
46	4	Tapa de pata de tolva; ancho 150; alto 150; espesor 12	ASTM A36 / Fabricar
47	8	Refuerzo triangular de apoyo de tolva; ancho 125; alto 150; espesor 12	ASTM A36 / Fabricar
48	4	Placa de apoyo del carril; ancho 100; alto 100; espesor 6	ASTM A36 / Fabricar
49	4	Placa inferior de unión de vigas; ancho 100; alto 100; espesor 20	ASTM A36 / Fabricar
50	4	Placa superior de unión de vigas; ancho 200; alto 214; espesor 20	ASTM A36 / Fabricar
143-146	4	Tramo de marco intermedio de tolva; ancho 60; alto 100; largo 1752; pared 6.3	S355NH / EN10210-1 / Fabricar

ISOMÉTRICO A COLOR / REFERENCIA DE MONTAJE

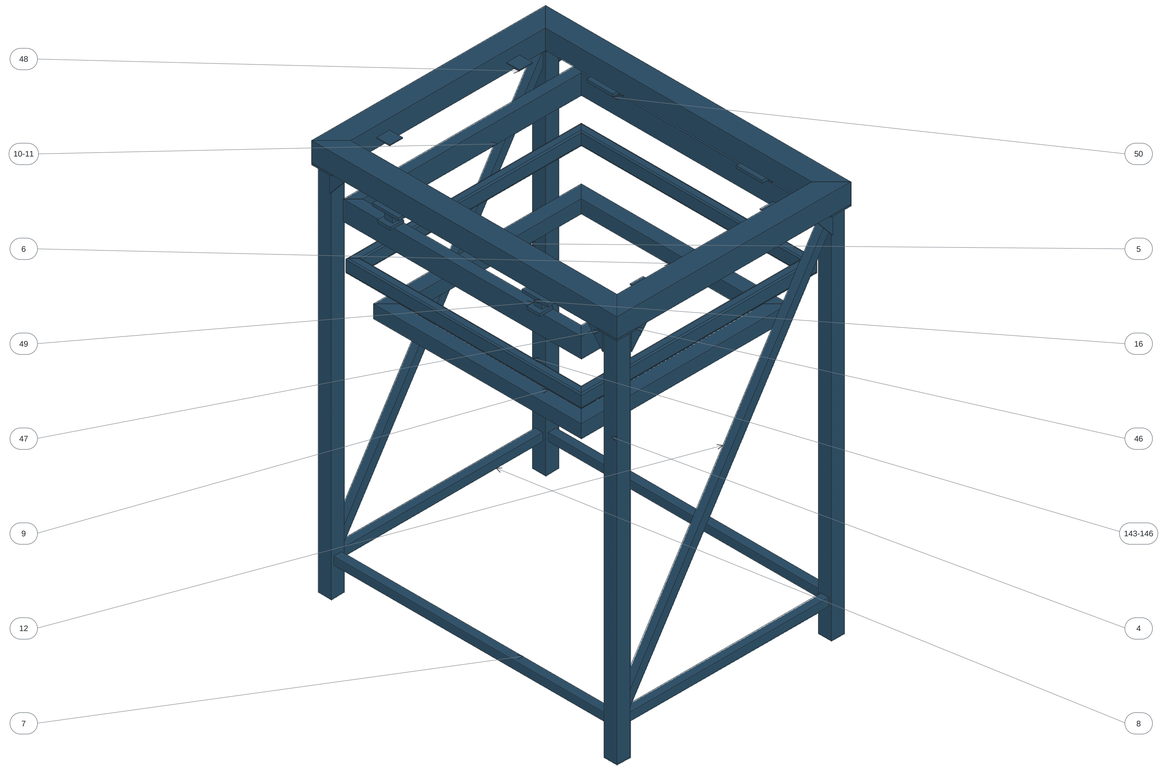

NOTAS DE FABRICACIÓN Y MONTAJE

1. Cuatro patas SHS100x100x5; marco superior SHS150x150x6. Longitudes y cantidades en lista de materiales.
2. Ejes de patas X = -250 / 1 950; Y = -825 / +825.
3. Anillos: Z 2009.33 / SHS100x100x5; Z 2312.44 / RHS100x60x6.3; Z 2682.59 / RHS150x75x5.
4. Soldadura de taller según conjunto y espesores; mantener libres las superficies de apoyo y revestimiento.
5. Cuatro asientos inferiores de colgante100×100×20: ejes Y±893.5; colgantes Y±878.5. Luz mínima2.5 mm al casco; dos filetes4×70 efectivos por asiento.
6. Esquinas de anillos: CJP5 en Z 2009.33; CJP6.3 en Z 2312.44; CJP5 en Z 2682.59.


Cotas en mm. ISO2768-m. Soldaduras según cuadro JF. Contornos: CAD/DXF.

				REBABAR Y ROMPER ARISTAS	NO CAMBIAR LA ESCALA		REVISIÓN
SESUVECA DEL PERÚ							
	NOMBRE	FIRMA	FECHA			TÍTULO: Bastidor de tolva ensamblado	
DIBUJ.	Javier Acevedo		20/10/26				
VERIF.							
APROB.							
FABR.							
CALID.				MATERIAL: SEGÚN LISTA DE MATERIALES		N.º DE DIBUJO EB-06	A1
PESO: SEGÚN CAD / lista de materiales				ESCALA: INDICADA		ESTACIÓN DE DESCARGA BIGBAG	HOJA 6 DE 16


REVISION P05 - REDISENO20/10/2026 - ALCANCE VERIFICADO EN MEMORIA - SIN LIBERACION INTEGRAL

Tolva, anillos y revestimiento

ALZADO ESCALA 1:10

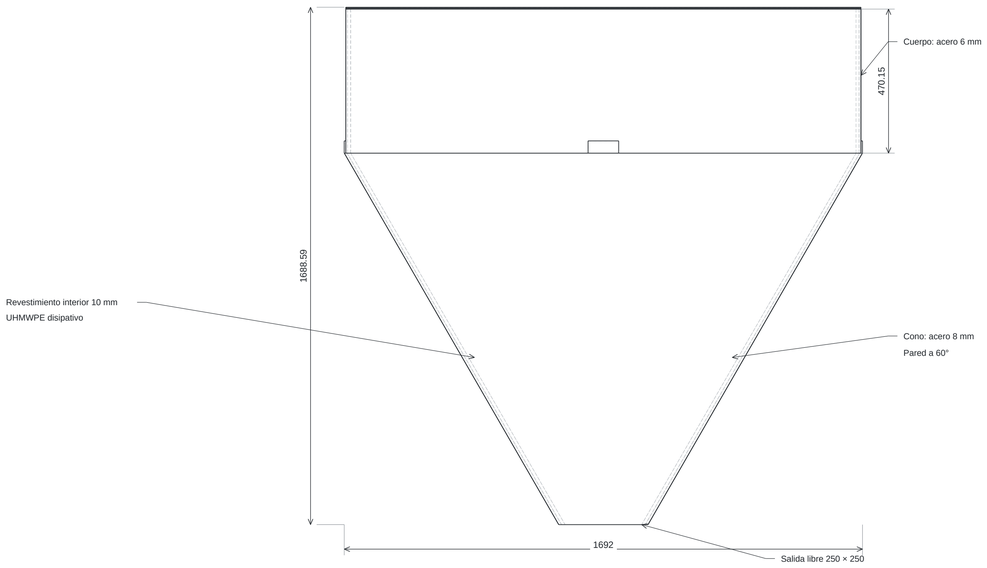


PLANTA ESCALA 1:15

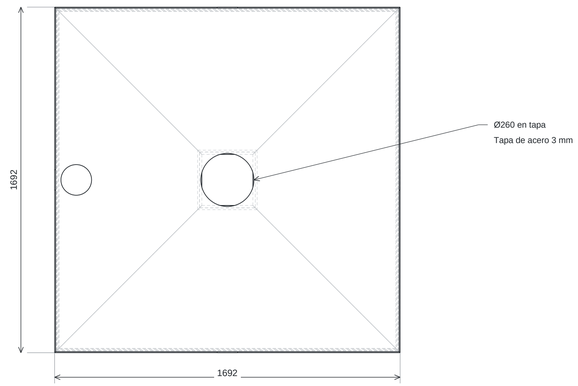

POS.	CANT.	PIEZA / MEDIDAS EN mm	MATERIAL / SUMINISTRO
17	4	Pared inclinada de tolva; Corte envolvente 1691.57×1404.62; espesor 8	ASTM A36 / Fabricar
18	3	Pared vertical de tolva; Corte envolvente 1682×470.15; espesor 6	ASTM A36 / Fabricar
19	1	Pared vertical con conexión de polvo; Corte envolvente 1682×470.15; espesor 6	ASTM A36 / Fabricar
20	1	Tapa de tolva; ancho 1682; alto 1682; espesor 3; taladros Ø150, Ø260	ASTM A36 / Fabricar
21	1	Empaque de tapa de tolva; ancho 1682; alto 1682; espesor 3	EPDM / Fabricar
57	4	Revestimiento interior de pared inclinada; Corte envolvente 1673.09×1405.77; espesor 10	PE-UHMW1000 disipativo / ASTM D4020 / Fabricar
58	3	Revestimiento interior de pared vertical; Corte envolvente 1670×470.15; espesor 10	PE-UHMW1000 disipativo / ASTM D4020 / Fabricar
59	1	Revestimiento vertical con conexión de polvo; Corte envolvente 1670×470.15; espesor 10	PE-UHMW1000 disipativo / ASTM D4020 / Fabricar
193	4	Placa de apoyo del marco de tolva; ancho 100; alto 40; espesor 5	ASTM A36 / Fabricar

ISOMÉTRICO A COLOR / REFERENCIA DE MONTAJE

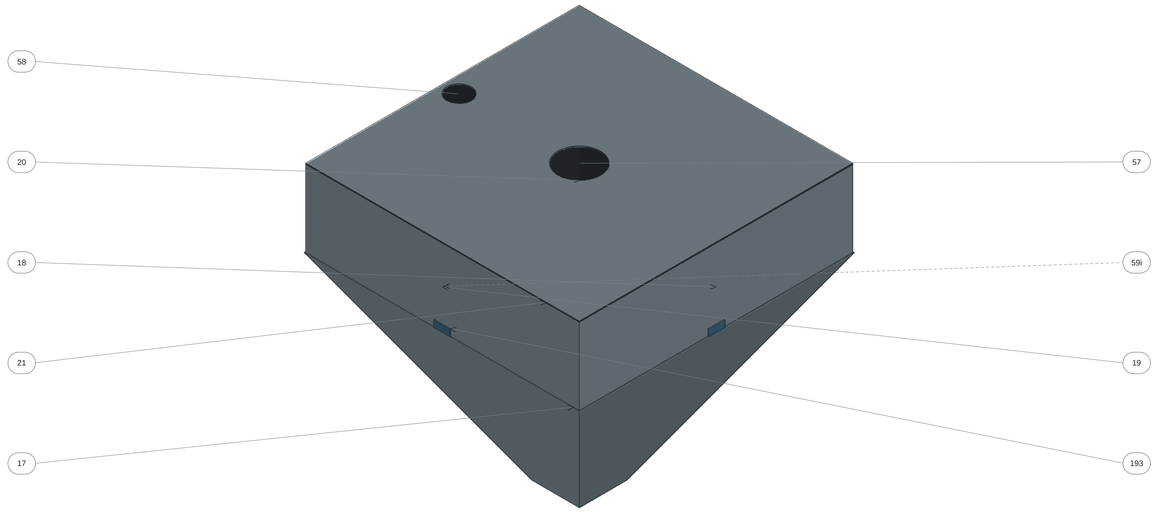

i = pieza interior; línea discontinua.


CONEXIÓN DE DESCARGA

ALZADO 1:2



Conexión a EB-10; materiales incluidos en EB-10.

PLANTA 1:3,33

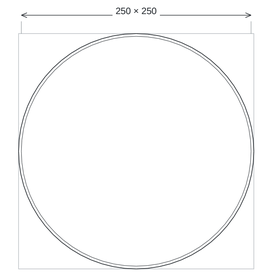

Paso de salida Ø250

NOTAS DE FABRICACIÓN Y MONTAJE

1. Boca interior libre 1 650; salida libre 250; paredes a 60 grados.
2. Tronco piramidal: altura interior1212,44. Cuerpo interior: altura470,15.
3. Chapa de cono: 8 mm; cuerpo: 6 mm. Esquinas del cono: CJP8 continuo.
4. Revestimiento UHMWPE disipativo de 10 mm; dimensiones interiores libres después del revestimiento.
5. Captación superior DN150 en tapa; cuerpo y revestimiento lateral sin perforación.
6. Volumen útil y ensayo de descarga por gravedad según memoria.
7. Cuerpo vertical470.15 mm. Volumen total2.572 m³; útil2.058 m³. Salida a1100 mm; apoyo de bolsa a3010 mm.

Cotas en mm. ISO2768-m. Soldaduras según cuadro JF. Contornos: CAD/DXF.

TALADROS DE PIEZAS DEL CONJUNTO / COORDENADAS LOCALES mm / ORIGEN LOCAL


P20 T1: Ø260; X0 Y0 Z0; eje Z

P20 T2: Ø150; X740 Y0 Z0; eje Z

				REBABAR Y ROMPER ARISTAS	NO CAMBIAR LA ESCALA	REVISIÓN
SESUVECA DEL PERÚ						
	NOMBRE	FIRMA	FECHA			TÍTULO: Tolva, anillos y revestimiento
DIBUJ.	Javier Acevedo		20/10/26			
VERIF.						
APROB.						
FABR.						
CALID.				MATERIAL: SEGÚN LISTA DE MATERIALES		N.º DE DIBUJO EB-07 / A1
PESO: SEGÚN CAD / lista de materiales				ESCALA: INDICADA		ESTACIÓN DE DESCARGA BIGBAG / HOJA 7 DE 16


Cortador y parrilla de apoyo de bolsa

ALZADO ESCALA 1:8

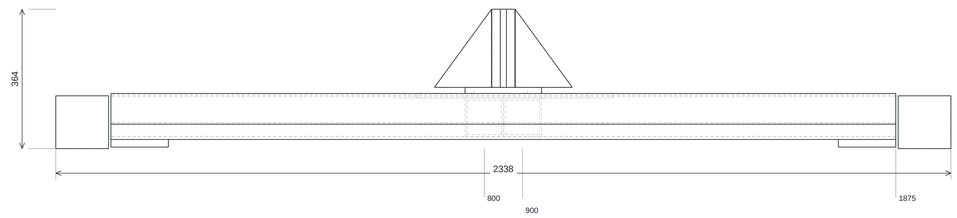


REFERENCIA X (mm)

PLANTA ESCALA 1:8

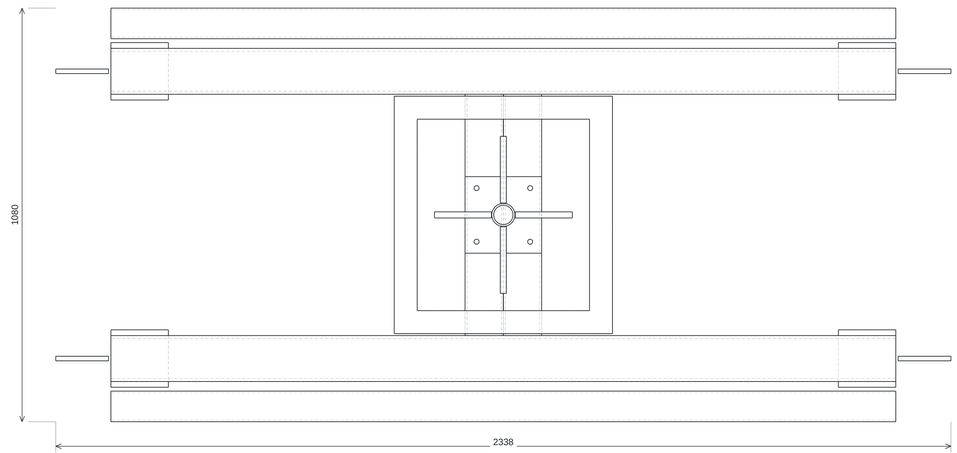

POS.	CANT.	PIEZA / MEDIDAS EN mm	MATERIAL / SUMINISTRO
13	2	Tramo de tubo cuadrado; ancho 80; alto 80; largo 2050; pared 4	ASTM A500 Gr.B / Fabricar
60-61	2	Cuchilla de apertura de bolsa; ancho 149; alto 204; espesor 16	AISI304 / ASTM A240 / Fabricar
62-63	2	Cuchilla de apertura de bolsa; ancho 174; alto 204; espesor 16	AISI304 / ASTM A240 / Fabricar
64	1	Tubo central del cortador; largo 204; pared 5; Ø exterior 60.3; Ø interior 50.3	AISI304 / ASTM A276 / Fabricar
65	1	Marco de apoyo del cortador; ancho 570; alto 620; espesor 12	ASTM A36 / Fabricar
66	1	Placa base del cortador; ancho 200; alto 200; espesor 16; taladros Ø13	ASTM A36 / Fabricar
137,140	2	Travesaño de apoyo de bolsa; ancho 120; alto 120; largo 2050; pared 8	ASTM A500 Gr.B / Fabricar
138	4	Placa de apoyo de travesaño; ancho 150; alto 150; espesor 20	ASTM A36 / Fabricar
139	4	Placa interior de refuerzo de travesaño; ancho 138; alto 138; espesor 12	ASTM A36 / Fabricar
141	2	Travesaño de apoyo del cortador; ancho 100; alto 100; largo 630; pared 5	ASTM A500 Gr.B / Fabricar
142	1	Placa separadora del cortador; ancho 200; alto 200; espesor 12	ASTM A36 / Fabricar

ISOMÉTRICO A COLOR / REFERENCIA DE MONTAJE

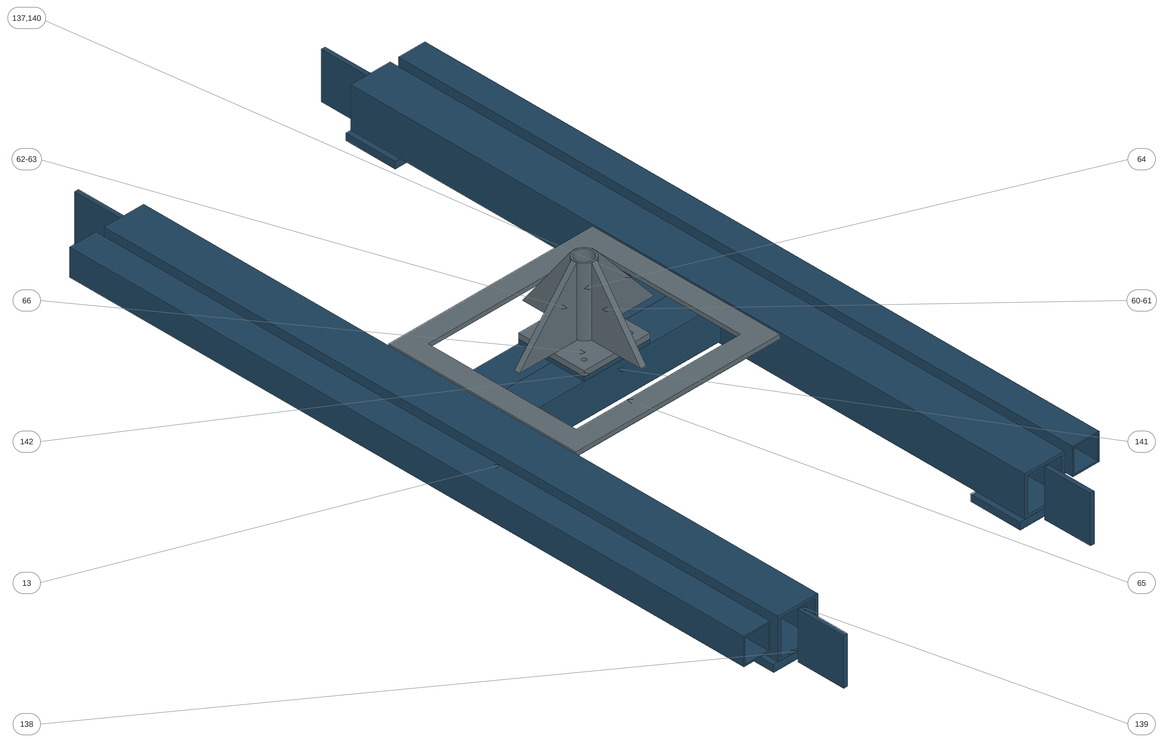

NOTAS DE FABRICACIÓN Y MONTAJE

1. Cuchilla piramidal fija de cuatro filos AISI304; chapas de filo t16 según lista de materiales.
2. Mástil, marco y travesaños forman un conjunto. Mantener posición centrada sobre salida.
3. Altura de punta Z = 3 230. El bigbag se desplaza con fondo a Z = 3 520.
4. Sustituir filos con equipo aislado, bolsa retirada y protección de acceso instalada.

Cotas en mm. ISO2768-m. Soldaduras según cuadro JF. Contornos: CAD/DXF.


TALADROS DE PIEZAS DEL CONJUNTO / COORDENADAS LOCALES mm / ORIGEN LOCAL

P66 T1: Ø13; X-70 Y-70 Z0; eje Z
P66 T2: Ø13; X70 Y-70 Z0; eje Z
P66 T3: Ø13; X-70 Y70 Z0; eje Z
P66 T4: Ø13; X70 Y70 Z0; eje Z


				REBABAR Y ROMPER ARISTAS	NO CAMBIAR LA ESCALA	REVISIÓN
SESUVECA DEL PERÚ						
	NOMBRE	FIRMA	FECHA			TÍTULO: Cortador y parrilla de apoyo de bolsa
DIBUJ.	Javier Acevedo		20/10/26			
VERIF.						
APROB.						
FABR.						
CALID.				MATERIAL: SEGÚN LISTA DE MATERIALES		N.º DE DIBUJO EB-08 / A1
PESO: SEGÚN CAD / lista de materiales				ESCALA: INDICADA		ESTACIÓN DE DESCARGA BIGBAG / HOJA 8 DE 16

Compuerta de descarga ensamblada

PLANTA ESCALA 1:5

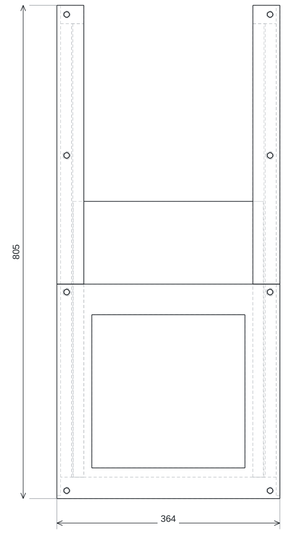


ALZADO ESCALA 1:2

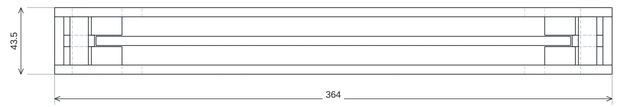


POS.	CANT.	PIEZA / MEDIDAS EN mm	MATERIAL / SUMINISTRO
72	1	Marco superior de compuerta; ancho 364; alto 350; espesor 6; taladros Ø9	ASTM A36 / Fabricar
73	1	Marco inferior de compuerta; ancho 364; alto 350; espesor 6; taladros Ø9	ASTM A36 / Fabricar
74	1	Placa deslizante de compuerta; ancho 310; alto 450; espesor 6	ASTM A36 / Fabricar
75	1	Guía superior de compuerta; ancho 44; alto 455; espesor 6; taladros Ø9	ASTM A36 / Fabricar
76	1	Guía superior de compuerta; ancho 44; alto 455; espesor 6; taladros Ø9	ASTM A36 / Fabricar
77	1	Guía inferior de compuerta; ancho 44; alto 455; espesor 6; taladros Ø9	ASTM A36 / Fabricar
78	1	Guía inferior de compuerta; ancho 44; alto 455; espesor 6; taladros Ø9	ASTM A36 / Fabricar
79-80	2	Barra separadora de compuerta; ancho 31.5; alto 800; espesor 6	ASTM A36 / Fabricar
81-82	2	Tira plástica de guía superior; ancho 20; alto 740; espesor 12	PE-UHMW1000 / ASTM D4020 / Fabricar
83-84	2	Tira plástica de guía inferior; ancho 20; alto 740; espesor 12	PE-UHMW1000 / ASTM D4020 / Fabricar
85-86	2	Tira plástica de guía lateral; ancho 20; alto 740; espesor 7.5; taladros Ø13	PE-UHMW1000 / ASTM D4020 / Fabricar
87	8	Separador tubular para perno; largo 31.5; pared 1.5; Ø exterior 12; Ø interior 9	ASTM A36 / Fabricar

ISOMÉTRICO A COLOR / REFERENCIA DE MONTAJE

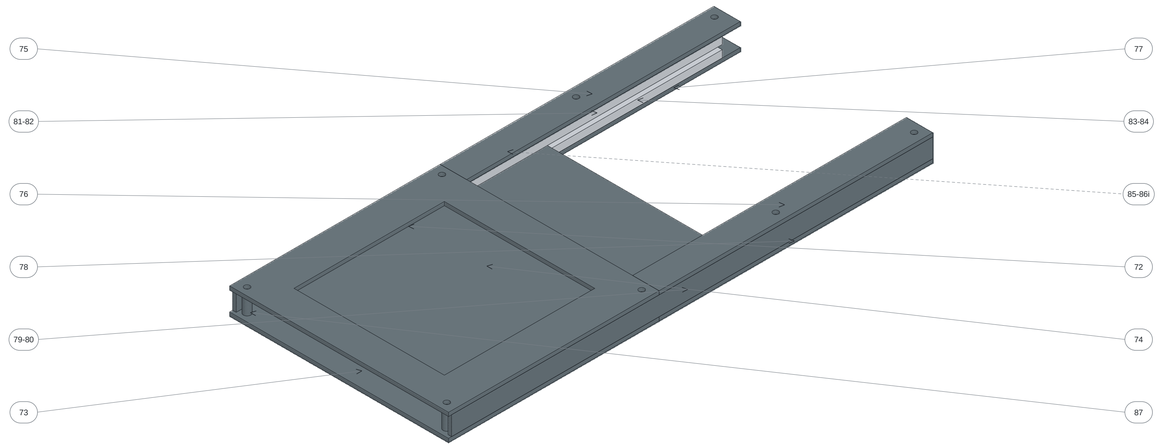

i = pieza interior; línea discontinua.

PLACAS DE COMPUERTA / POS. 72 / 73

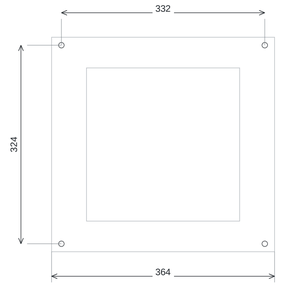

Planchas de acero 6 mm

Abertura 250 × 250

4 agujeros Ø9

Entre centros 332 × 324

Exterior 364 × 350

Medidas en mm. Vista ampliada de las placas; sin elementos de fijación.

NOTAS DE FABRICACIÓN Y MONTAJE

1. Hoja de cierre, guías y revestimientos se muestran en posición cerrada de referencia.
2. Accionamiento: cremallera y piñón con reducción manual; pasador cautivo de bloqueo.
3. Ajustar paralelismo de guías y comprobar recorrido completo antes del montaje de la guarda.
4. Conservar espesores de casquillos y UHMWPE del CAD; ajustar fijaciones manteniendo libre la corredera.

Cotas en mm. ISO2768-m. Soldaduras según cuadro JF. Contornos: CAD/DXF.

TALADROS DE PIEZAS DEL CONJUNTO / COORDENADAS LOCALES mm / ORIGEN LOCAL


P72 T1: Ø9; X-166 Y-162 Z0; eje Z
P72 T2: Ø9; X166 Y-162 Z0; eje Z
P72 T3: Ø9; X-166 Y162 Z0; eje Z
P72 T4: Ø9; X166 Y162 Z0; eje Z
P73 T1: Ø9; X-166 Y-162 Z0; eje Z
P73 T2: Ø9; X166 Y-162 Z0; eje Z
P73 T3: Ø9; X-166 Y162 Z0; eje Z
P73 T4: Ø9; X166 Y162 Z0; eje Z

P75 T1: Ø9; X6 Y-17.5 Z0; eje Z
P75 T2: Ø9; X6 Y212.5 Z0; eje Z
P76 T1: Ø9; X-6 Y-17.5 Z0; eje Z
P76 T2: Ø9; X-6 Y212.5 Z0; eje Z
P77 T1: Ø9; X6 Y-17.5 Z0; eje Z
P77 T2: Ø9; X6 Y212.5 Z0; eje Z
P78 T1: Ø9; X-6 Y-17.5 Z0; eje Z
P78 T2: Ø9; X-6 Y212.5 Z0; eje Z


				REBABAR Y ROMPER ARISTAS	NO CAMBIAR LA ESCALA	REVISIÓN
SESUVECA DEL PERÚ						
	NOMBRE	FIRMA	FECHA			TÍTULO: Compuerta de descarga ensamblada
DIBUJ.	Javier Acevedo		20/10/26			
VERIF.						
APROB.						
FABR.						
CALID.				MATERIAL: SEGÚN LISTA DE MATERIALES		N.° DE DIBUJO EB-09 / A1
PESO: SEGÚN CAD / lista de materiales				ESCALA: INDICADA		ESTACIÓN DE DESCARGA BIGBAG / HOJA 9 DE 16

Guarda, ensacado y captación

ALZADO ESCALA 1:20

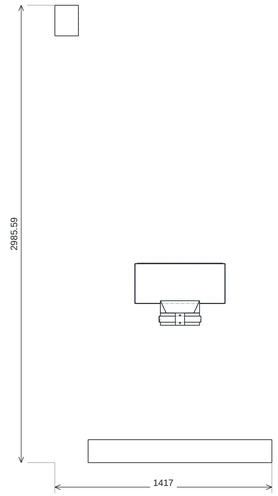


PLANTA ESCALA 1:10

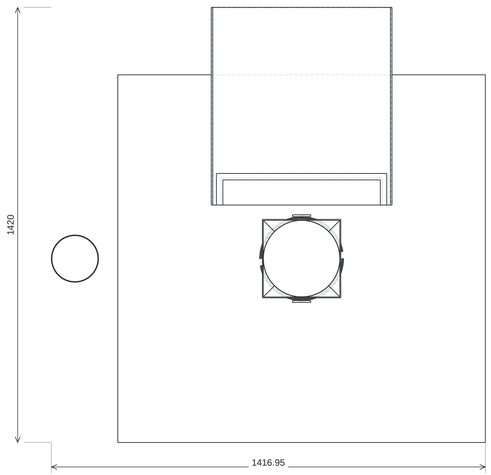


POS.	CANT.	PIEZA / MEDIDAS EN mm	MATERIAL / SUMINISTRO
88	1	Adaptador de salida cuadrada a redonda; alto 80; espesor 3; Ø interior 250; boca cuadrada 250	ASTM A36 / Fabricar
89	1	Tubo de salida de producto; largo 80; pared 3; Ø exterior 256; Ø interior 250	ASTM A36 / Fabricar
90	2	Abrazadera curva de sujeción del saco; ancho 402.3; alto 40; espesor 3; Ø exterior 274; Ø interior 268; R interior 134; R exterior 137; arco 170°	ASTM A36 / Fabricar
91	2	Banda de goma de abrazadera; ancho 268; alto 40; espesor 3; Ø exterior 268; Ø interior 262; R interior 131; R exterior 134; arco 170°	EPDM / Fabricar
92	2	Placa de soporte de abrazadera; ancho 60; alto 80; espesor 6; taladros Ø9	ASTM A36 / Fabricar
93	1	Saco de ensacado de 25–50 kg; ancho 380; alto 220; largo 766.5	Polipropileno tejido / Comprar
94	1	Balanza de plataforma 1200×1200, capacidad 2 t; ancho 1200; alto 1200; largo 150	Plataforma de pesaje completa / Comprar
95	1	Cubierta doblada de protección de compuerta; ancho 590; alto 262; largo 645; espesor 2; R interior 3	ASTM A36 / Fabricar
96	1	Tapa inferior de protección de compuerta; ancho 590; alto 645; espesor 2	ASTM A36 / Fabricar
97	1	Tapa de extremo de protección de compuerta; ancho 586; alto 258; espesor 2; R esquinas 3	ASTM A36 / Fabricar
98	1	Empaque flexible de protección de compuerta; ancho 556; alto 103; espesor 2	EPDM disipativo / Fabricar
158	1	Cuello de extracción superior Ø150; Ø interior150; Ø exterior154; espesor2; largo200	AISI 304 / Fabricar

ISOMÉTRICO A COLOR / REFERENCIA DE MONTAJE

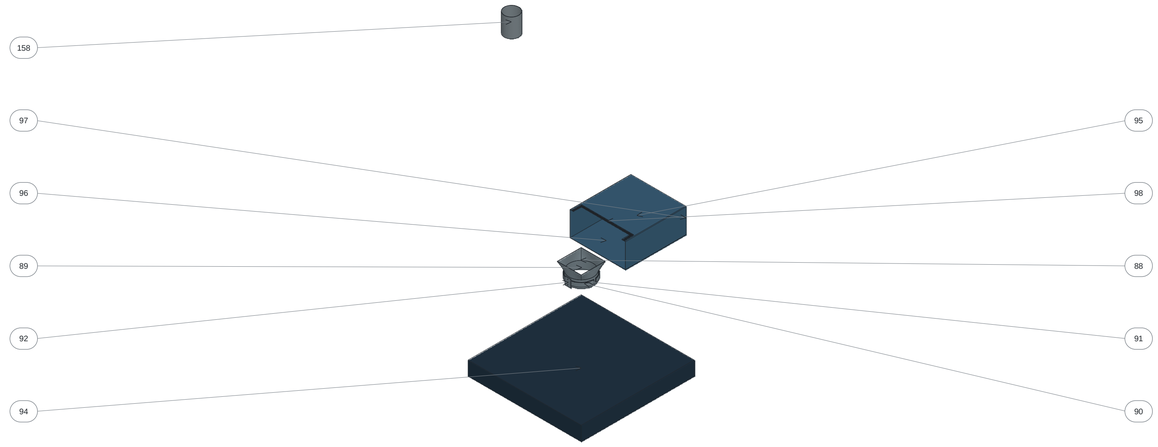

ABRAZADERA Y CAUCHO

POS.90 / 91

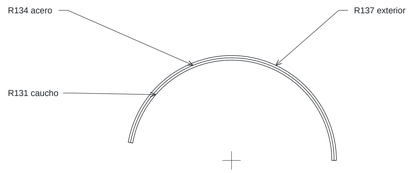


Arco 170°; ancho 40

Acero 3 mm; caucho 3 mm

Dos piezas de cada tipo. Radios en mm.

R3 interior

GUARDA ESCALA 1:5

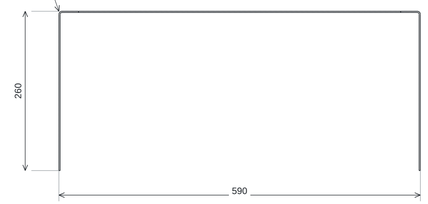

Radio interior de doblado R3

Plancha 2 mm

NOTAS DE FABRICACIÓN Y MONTAJE

1. Guarda cerrada de compuerta: envolvente final 590 x 645 x 262.
2. Cota superior de recinto protegido Z = 3 430; despeje nominal de traslado: 90.
3. Salida libre DN250; interfaz de saco y balanza de plataforma 1 200 x 1 200 / 2 t.
4. Captación DN150: 800 m3/h a 1 500 Pa en colector; balance de presión según memoria.
5. Conexiones desmontables para limpieza y mantenimiento. Protección contra polvo combustible según análisis del proyecto.

Cotas en mm. ISO2768-m. Soldaduras según cuadro JF. Contornos: CAD/DXF.

TALADROS DE PIEZAS DEL CONJUNTO / COORDENADAS LOCALES mm / ORIGEN LOCAL


P92 T1: Ø9; X0 Y-25 Z0; eje Z

P92 T2: Ø9; X0 Y25 Z0; eje Z

				REBABAR Y ROMPER ARISTAS	NO CAMBIAR LA ESCALA	REVISIÓN
SESUVECA DEL PERÚ						
	NOMBRE	FIRMA	FECHA			TÍTULO: Guarda, ensacado y captación
DIBUJ.	Javier Acevedo		20/10/26			
VERIF.						
APROB.						
FABR.						
CALID.				MATERIAL: SEGÚN LISTA DE MATERIALES		N.º DE DIBUJO EB-10 / A1
PESO: SEGÚN CAD / lista de materiales				ESCALA: INDICADA		ESTACIÓN DE DESCARGA BIGBAG / HOJA 10 DE 16


Carro, suspensión y traba de posición

ALZADO ESCALA 1:5

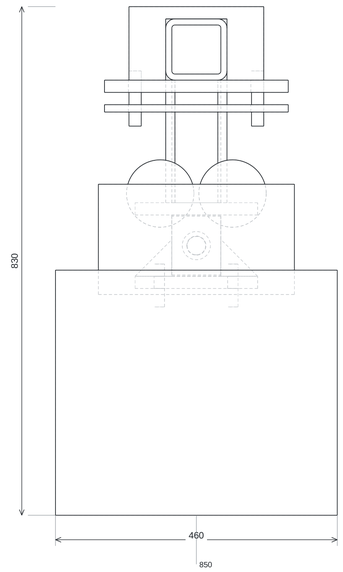


REFERENCIA X (mm)

PERFIL ESCALA 1:8

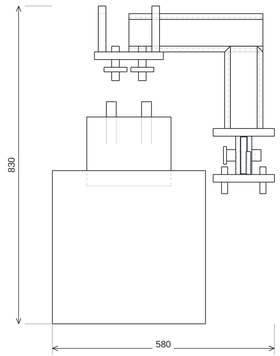

POS.	CANT.	PIEZA / MEDIDAS EN mm	MATERIAL / SUMINISTRO
67	1	Tecle eléctrico KITO SHER2M020IS-IS de 2 t; Conjunto KITO SHER2M020IS-IS, capacidad 2 t	Conjunto KITO SHER2M020IS-IS / Comprar
68	1	Carro motorizado del tecle KITO; Conjunto KITO SHER2M020IS-IS, capacidad 2 t	Conjunto KITO SHER2M020IS-IS / Comprar
69	1	Cadena de carga del tecle KITO; Repuesto original del conjunto KITO SHER2M020IS-IS de 2 t	Conjunto KITO SHER2M020IS-IS / Comprar
70	1	Bolsa bigbag de 1 t; ancho 1000; alto 1000; largo 1000	Polipropileno tejido / Comprar
71	4	Asa de bolsa bigbag; Asas integrales de la bolsa bigbag de 1 t	Polipropileno tejido / Comprar
101	8	Arandela M16; largo 3; pared 6; Ø exterior 30; Ø interior 18	Acero 200HV / ISO7089 / Comprar
102	8	Tuerca M16; Rosca M16; clase 8	Acero clase 8 / ISO898-2 / Comprar
104	1	Placa de apoyo de traba del carro; ancho 300; alto 180; espesor 20; taladros Ø22	ASTM A36 / Fabricar
105	2	Placa de refuerzo del ala de viga; ancho 300; alto 60; espesor 12; taladros Ø22	ASTM A36 / Fabricar
106	1	Brazo de traba del carro; ancho 100; alto 100; largo 350; pared 10	S355NH / EN10210-1 / Fabricar
107	1	Poste de traba del carro; ancho 100; alto 100; largo 215; pared 10	S355NH / EN10210-1 / Fabricar
108	1	Placa de apoyo del pasador; ancho 200; alto 160; espesor 20	ASTM A36 / Fabricar
109	2	Placa exterior de traba del carro; ancho 80; alto 100; espesor 12; taladros Ø31	ASTM A36 / Fabricar
110	1	Placa central de traba del carro; ancho 80; alto 96; espesor 16; taladros Ø31	ASTM A36 / Fabricar
111	1	Placa de unión al carro; ancho 200; alto 160; espesor 20; taladros Ø18	ASTM A36 / Fabricar
112	2	Placa de apoyo del brazo; ancho 220; alto 120; espesor 20	ASTM A36 / Fabricar
113	2	Refuerzo triangular de traba; ancho 60; alto 60; espesor 12	ASTM A36 / Fabricar
114	1	Pasador de bloqueo del carro; largo 90; Ø exterior 30; taladros Ø4.5	C45E+QT / EN ISO683-1 / Fabricar
115	1	Cabeza del pasador; largo 8; Ø exterior 46	ASTM A36 / Fabricar
116	1	Seguro tipo R del pasador; largo 38; Ø exterior 3	Acero para resorte / EN10270-1 / Comprar
117	1	Placa para sujetar cable del pasador; ancho 40; alto 12; espesor 3; taladros Ø4	ASTM A36 / Fabricar
118-120	3	Cable de retención del pasador; Cable Ø3; largo total mínimo 350; una sola pieza	AISI316 / EN12385-4 / Fabricar
121	4	Perno M20 de traba del carro; M20 × 90; clase 8.8	Acero clase 8.8 / ISO898-1 / Comprar
122	8	Arandela M20; largo 3; pared 7.5; Ø exterior 37; Ø interior 22	Acero 200HV / ISO7089 / Comprar
123	8	Tuerca M20; Rosca M20; clase 8	Acero clase 8 / ISO898-2 / Comprar
124	4	Espárrago M16 de unión al carro; M16 × 70; clase 8.8	Acero clase 8.8 / ISO898-1 / Comprar
125	4	Rueda del carro KITO; Repuesto original del conjunto KITO SHER2M020IS-IS de 2 t	Conjunto KITO SHER2M020IS-IS / Comprar

ISOMÉTRICO A COLOR / REFERENCIA DE MONTAJE

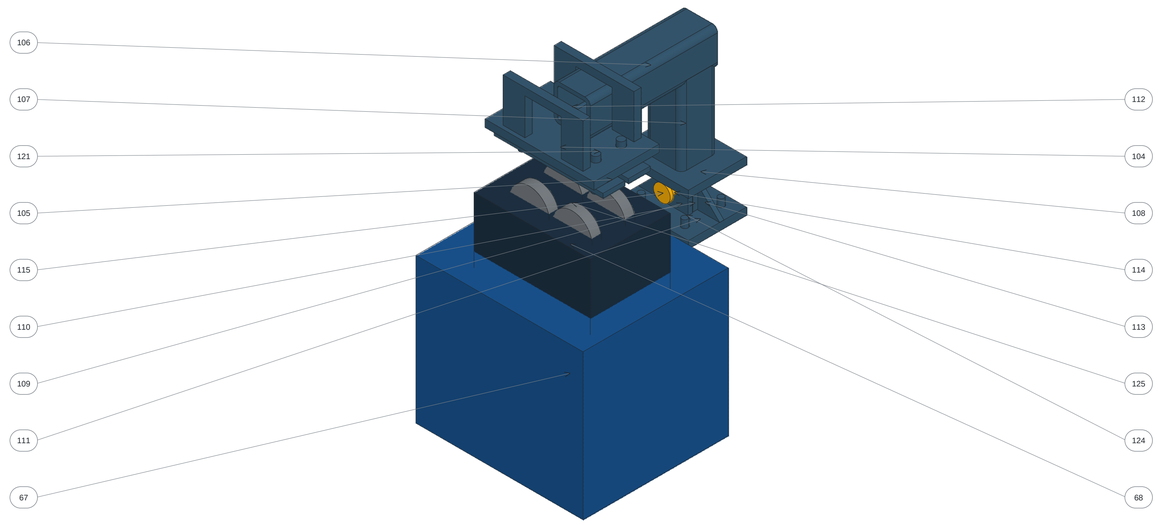

NOTAS DE FABRICACIÓN Y MONTAJE

1. Referencia comercial KITO SHER2M020IS-IS / 2 t; C de catálogo = 475.
2. Mantener el conjunto comercial de tecle y carro según especificación de compra.
3. Pasador cautivo D30 Fy >=355 MPa; dos orejas t12 y placa receptora t16; taladros D31.
4. Inserción únicamente con carro detenido. Inhibir traslación con pasador insertado.
5. Patrones de fijación TC y tolerancias de montaje según detalle / CAD.
6. Brazo y poste de traba100×100×10 S355NH: extremos a placas20 y encuentro brazo/poste con penetración completa10 mm; garganta efectiva mínima9 mm.
7. Brazo350 mm. Poste: reserva215 mm; contornear extremo al radio del brazo. Altura nominal200 mm; eje de poste y pasador Y300.

Cotas en mm. ISO2768-m. Soldaduras según cuadro JF. Contornos: CAD/DXF.


TALADROS DE PIEZAS DEL CONJUNTO / COORDENADAS LOCALES mm / ORIGEN LOCAL

P104 T1: Ø22; X-100 Y-35 Z0; eje Z
P104 T2: Ø22; X-100 Y35 Z0; eje Z
P104 T3: Ø22; X100 Y-35 Z0; eje Z
P104 T4: Ø22; X100 Y35 Z0; eje Z
P105 T1: Ø22; X-100 Y0 Z0; eje Z
P105 T2: Ø22; X100 Y0 Z0; eje Z
P109 T1: Ø31; X0 Y0 Z0; eje Z
P110 T1: Ø31; X0 Y0 Z0; eje Z
P111 T1: Ø18; X-60 Y-50 Z0; eje Z
P111 T2: Ø18; X-60 Y50 Z0; eje Z
P111 T3: Ø18; X60 Y-50 Z0; eje Z
P111 T4: Ø18; X60 Y50 Z0; eje Z
P114 B1: Ø4.5; X0 Y16 Z78; eje Y
P117 T1: Ø4; X12 Y0 Z0; eje Z

				REBABAR Y ROMPER ARISTAS	NO CAMBIAR LA ESCALA	REVISIÓN
SESUVECA DEL PERÚ						
	NOMBRE	FIRMA	FECHA			TÍTULO: Carro, suspensión y traba de posición
DIBUJ.	Javier Acevedo		20/10/26			
VERIF.						
APROB.						
FABR.						
CALID.				MATERIAL: SEGÚN LISTA DE MATERIALES		N.º DE DIBUJO EB-11 / A1
PESO: SEGÚN CAD / lista de materiales				ESCALA: INDICADA		ESTACIÓN DE DESCARGA BIGBAG / HOJA 11 DE 16


Plataforma de acceso ensamblada

PLANTA ESCALA 1:8

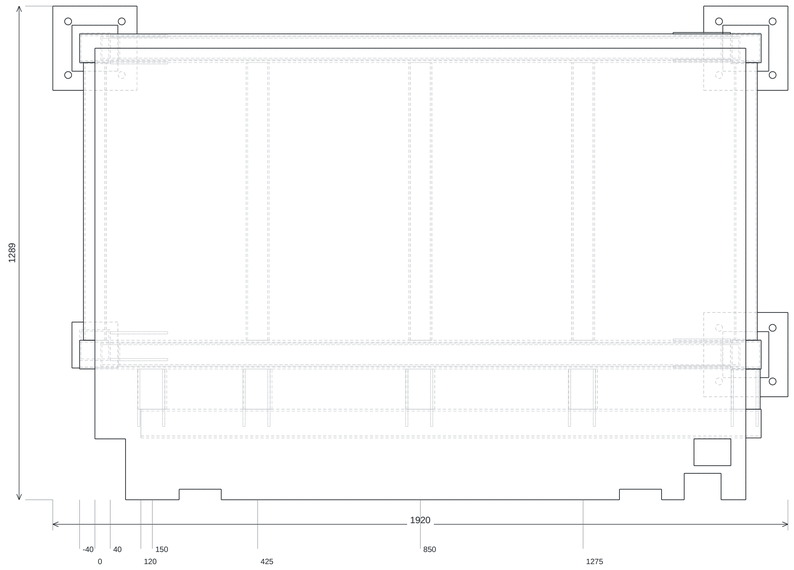


REFERENCIA X (mm)

ALZADO ESCALA 1:20

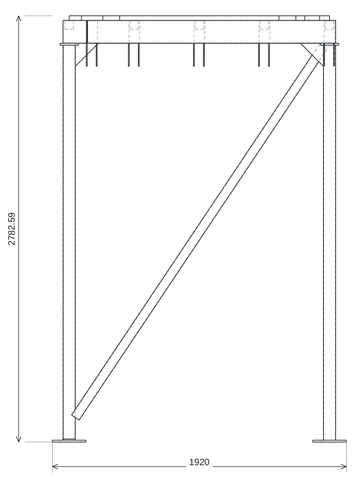

POS.	CANT.	PIEZA / MEDIDAS EN mm	MATERIAL / SUMINISTRO
159	4	Tapa de columna de acceso; ancho 120; alto 120; espesor 12	ASTM A36 / Fabricar
160	18	Refuerzo triangular de acceso; ancho 150; alto 150; espesor 6	ASTM A36 / Fabricar
161	3	Tramo de tubo cuadrado; ancho 80; alto 80; largo 2578.59; pared 4	ASTM A500 Gr.B / Fabricar
162	1	Tramo de tubo cuadrado; ancho 80; alto 80; largo 2570.59; pared 4	ASTM A500 Gr.B / Fabricar
163	2	Tramo de tubo rectangular; ancho 75; alto 150; largo 1780; pared 5	ASTM A500 Gr.B / Fabricar
164	1	Tramo de tubo rectangular; ancho 75; alto 150; largo 1620; pared 5	ASTM A500 Gr.B / Fabricar
165	5	Tramo de tubo cuadrado; ancho 60; alto 60; largo 725; pared 4	ASTM A500 Gr.B / Fabricar
166	5	Tramo de tubo rectangular; ancho 75; alto 150; largo 105; pared 5	ASTM A500 Gr.B / Fabricar
167	2	Tramo de tubo cuadrado; ancho 60; alto 60; largo 2914.33; pared 4	ASTM A500 Gr.B / Fabricar
168	1	Piso de rejilla de plataforma; ancho 1700; alto 1190; espesor 30	ASTM A36 galvanizado / Comprar
201	3	Placa base de acceso; ancho 220; alto 220; espesor 12; taladros Ø18	ASTM A36 / Fabricar

ISOMÉTRICO A COLOR / REFERENCIA DE MONTAJE

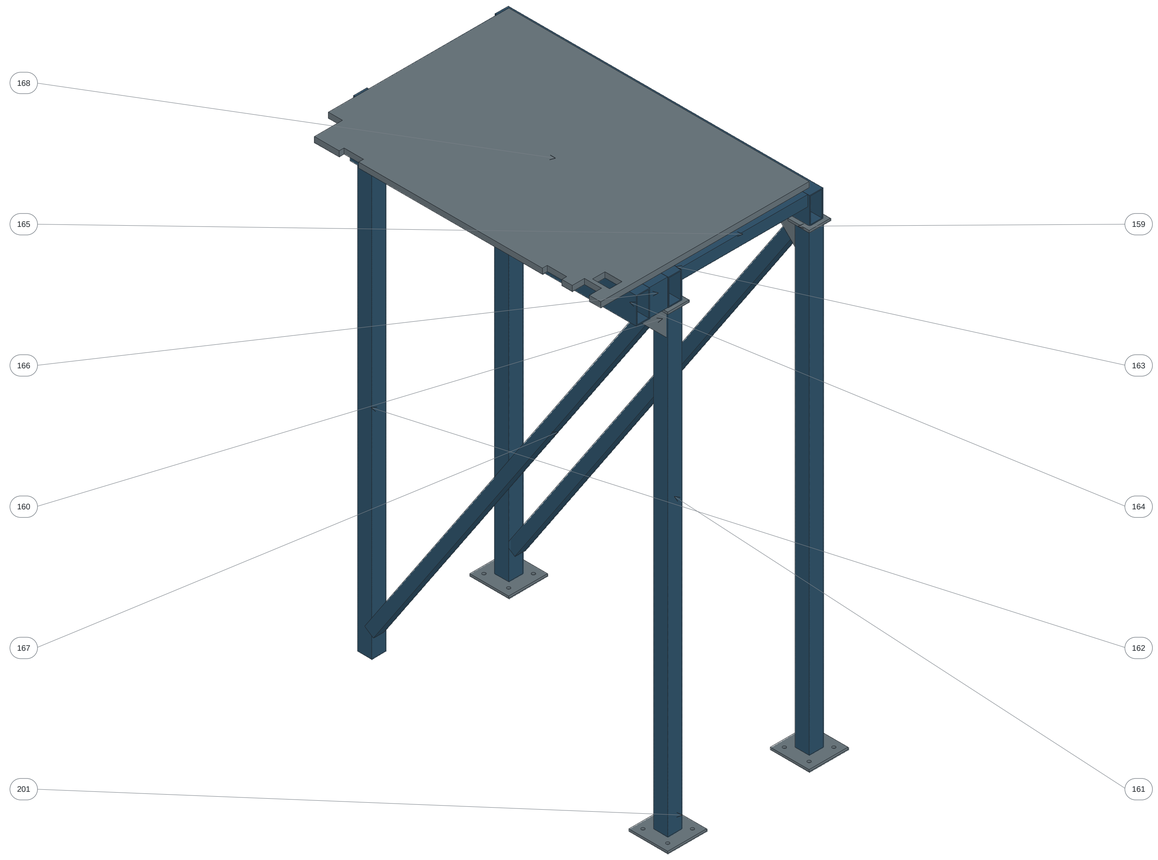

NOTAS DE FABRICACIÓN Y MONTAJE

1. Piso Z = 2 782,59; plataforma posterior de un lado con paso libre 800 y aproximación independiente.
2. No soldar la rejilla comercial a través de superficies de drenaje; fijaciones según compra.
3. Puerta corredera de intervención 800; bloqueo, autocierre y protección inferior fija.
4. Brazos RHS a marco: filete5 continuo en ambos extremos; viguetasSHS60 a marco: filete4 continuo.
5. ColumnasSHS80 a placas120x120x12: filete4 continuo. Cartelas: dos cordones filete4x100 por union.

Cotas en mm. ISO2768-m. Soldaduras según cuadro JF. Contornos: CAD/DXF.


TALADROS DE PIEZAS DEL CONJUNTO / COORDENADAS LOCALES mm / ORIGEN LOCAL

P201 T1: Ø18; X-70 Y-70 Z0; eje Z
P201 T2: Ø18; X70 Y-70 Z0; eje Z
P201 T3: Ø18; X70 Y70 Z0; eje Z
P201 T4: Ø18; X-70 Y70 Z0; eje Z


				REBABAR Y ROMPER ARISTAS	NO CAMBIAR LA ESCALA	REVISIÓN
SESUVECA DEL PERÚ						
	NOMBRE	FIRMA	FECHA			TÍTULO: Plataforma de acceso ensamblada
DIBUJ.	Javier Acevedo		20/10/26			
VERIF.						
APROB.						
FABR.						
CALID.				MATERIAL: SEGÚN LISTA DE MATERIALES		N.º DE DIBUJO EB-12 / A1
PESO: SEGÚN CAD / lista de materiales				ESCALA: INDICADA		ESTACIÓN DE DESCARGA BIGBAG / HOJA 12 DE 16

Escalera y desembarco ensamblados

ALZADO ESCALA 1:15

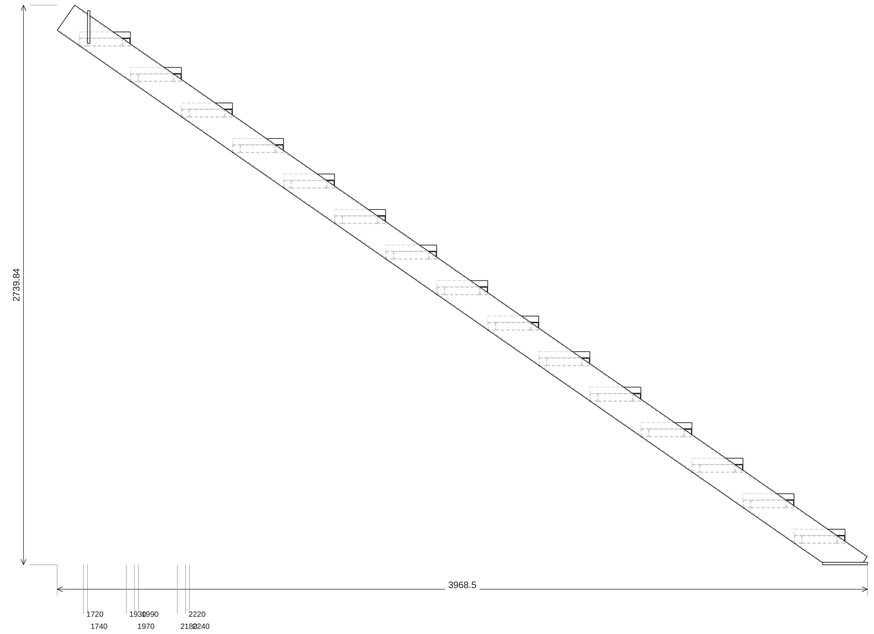


PLANTA ESCALA 1:15

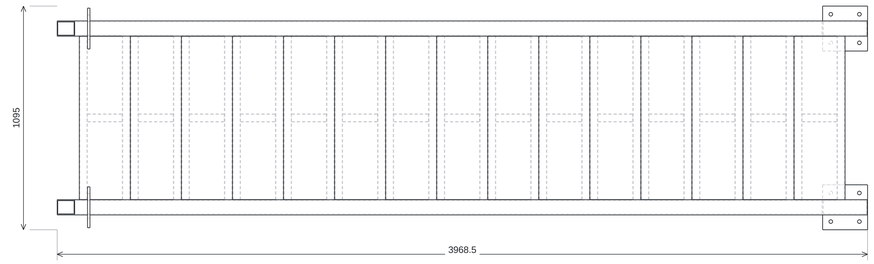

POS.	CANT.	PIEZA / MEDIDAS EN mm	MATERIAL / SUMINISTRO
169	15	Peldaño de rejilla; ancho 250; alto 800; espesor 30	ASTM A36 galvanizado / Comprar
170	2	Tramo de tubo rectangular; ancho 75; alto 150; largo 4568.12; pared 5	ASTM A500 Gr.B / Fabricar
171	2	Placa de unión de escalera a plataforma; ancho 200; alto 160; espesor 12; taladros Ø13	ASTM A36 / Fabricar
172	30	Tramo de tubo cuadrado; ancho 40; alto 40; largo 800; pared 3	ASTM A500 Gr.B / Fabricar
194	15	Tramo de tubo cuadrado; ancho 40; alto 40; largo 170; pared 3	ASTM A500 Gr.B / Fabricar
201	2	Placa base de acceso; ancho 220; alto 220; espesor 12; taladros Ø18	ASTM A36 / Fabricar

ISOMÉTRICO A COLOR / REFERENCIA DE MONTAJE

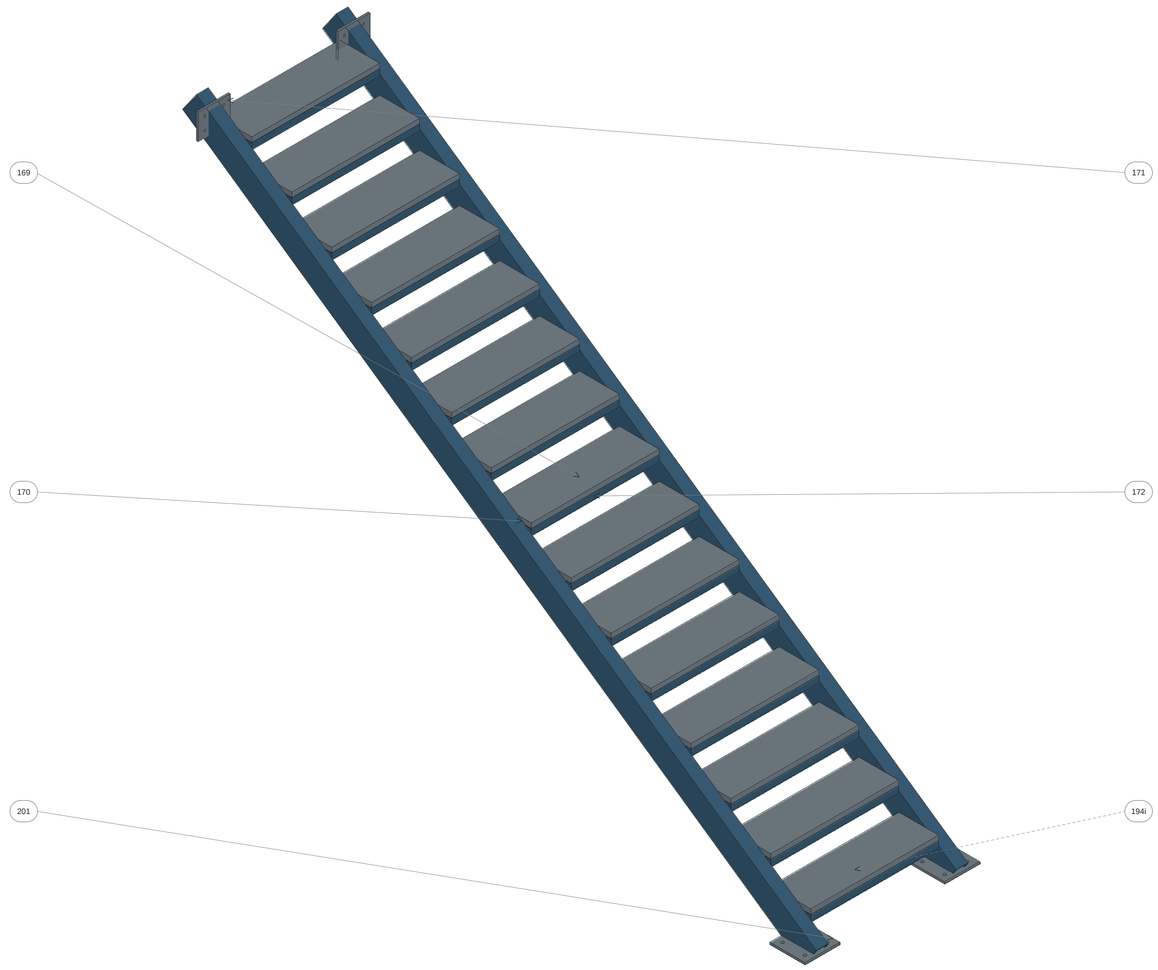

i = pieza interior; línea discontinua.

NOTAS DE FABRICACIÓN Y MONTAJE

1. Dos zancas RHS150x75x5 con recorte final de desembarco; peldaños según lista de materiales.
2. Cortar según lista y ensamblar en útil sobre los ejes indicados.
3. 16 contrahuellas de 173,91; 15 huellas de 250; desarrollo 3 750; paso libre 800.
4. Zanca a placa de extremo: filete5 continuo en contorno75x150. Peldaño a soporte: filete4 continuo.
5. Cada extremo de zanca: cuatro pernosM16 8.8 segun patrón CAD; placas y cartelas segun lista.

Cotas en mm. ISO2768-m. Soldaduras según cuadro JF. Contornos: CAD/DXF.

TALADROS DE PIEZAS DEL CONJUNTO / COORDENADAS LOCALES mm / ORIGEN LOCAL


P171 T1: Ø13; X-60 Y-40 Z0; eje Z
P171 T2: Ø13; X60 Y-40 Z0; eje Z
P171 T3: Ø13; X60 Y40 Z0; eje Z
P171 T4: Ø13; X-60 Y40 Z0; eje Z

P201 T1: Ø18; X-70 Y-70 Z0; eje Z
P201 T2: Ø18; X70 Y-70 Z0; eje Z
P201 T3: Ø18; X70 Y70 Z0; eje Z
P201 T4: Ø18; X-70 Y70 Z0; eje Z


				REBABAR Y ROMPER ARISTAS	NO CAMBIAR LA ESCALA		REVISIÓN
SESUVECA DEL PERÚ							
	NOMBRE	FIRMA	FECHA			TÍTULO: Escalera y desembarco ensamblados	
DIBUJ.	Javier Acevedo		20/10/26				
VERIF.							
APROB.							
FABR.							
CALID.				MATERIAL: SEGÚN LISTA DE MATERIALES		N.º DE DIBUJO EB-13	A1
PESO: SEGÚN CAD / lista de materiales				ESCALA: INDICADA		ESTACIÓN DE DESCARGA BIGBAG	HOJA 13 DE 16

Barandas, pasamanos y rodapiés

ALZADO ESCALA 1:25

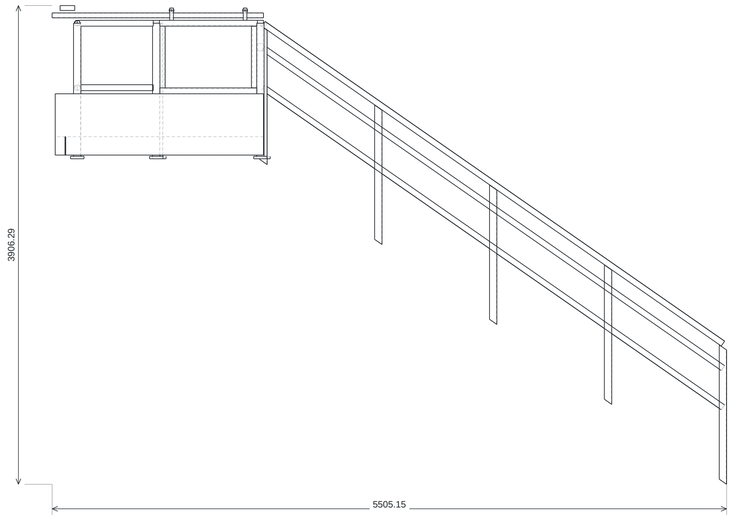


PLANTA ESCALA 1:20

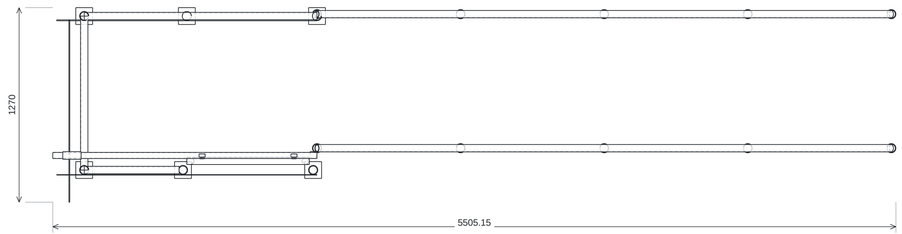

POS.	CANT.	PIEZA / MEDIDAS EN mm	MATERIAL / SUMINISTRO
173	6	Placa base de acceso; ancho 110; alto 110; espesor 20	ASTM A36 / Fabricar
174	6	Poste circular de baranda; largo 1085.85; pared 3.91; Ø exterior 60.3; Ø interior 52.48	ASTM A53 Gr B / Fabricar
175	2	Pasamanos o travesaño circular de baranda; largo 1520; pared 3.68; Ø exterior 48.3; Ø interior 40.94	ASTM A53 Gr B / Fabricar
176	2	Pasamanos o travesaño circular de baranda; largo 1005; pared 3.68; Ø exterior 48.3; Ø interior 40.94	ASTM A53 Gr B / Fabricar
177	2	Pasamanos o travesaño circular de baranda; largo 620; pared 3.68; Ø exterior 48.3; Ø interior 40.94	ASTM A53 Gr B / Fabricar
178	1	Protección fija frente a tolva; ancho 1700; alto 500; espesor 3	ASTM A36 / Fabricar
179	1	Banda de borde de plataforma; ancho 1700; alto 150; espesor 6	ASTM A36 / Fabricar
180	1	Banda de borde de plataforma; ancho 1190; alto 150; espesor 6	ASTM A36 / Fabricar
181	2	Pasamanos o travesaño circular de baranda; largo 800; pared 3.68; Ø exterior 48.3; Ø interior 40.94	ASTM A53 Gr B / Fabricar
182	2	Pasamanos o travesaño circular de baranda; largo 503.4; pared 3.68; Ø exterior 48.3; Ø interior 40.94	ASTM A53 Gr B / Fabricar
183	1	Panel de puerta corredera; ancho 720; alto 520; espesor 3	ASTM A36 / Fabricar
184	1	Tramo de tubo cuadrado; ancho 40; alto 40; largo 1725; pared 3	ASTM A500 Gr.B / Fabricar
185	2	Rodillo de guía de puerta corredera; Ø40; ancho20; conjunto con eje y rodamiento	Rodillo de acero galvanizado con rodamiento sellado / Comprar
186	2	Ac puerta colgador; ancho 30; alto 100; espesor 6; taladros Ø12	ASTM A36 / Fabricar
187	1	Cierre automático de puerta corredera; Conjunto de cierre automático para puerta corredera	Conjunto comercial de cierre / Comprar
188	1	Interruptor con bloqueo de puerta; 24 VDC; bloqueo supervisado de puerta	Interruptor de seguridad completo / Comprar
189-191	10	Poste circular de baranda; largo 1095.8; pared 3.91; Ø exterior 60.3; Ø interior 52.48	ASTM A53 Gr B / Fabricar
192	6	Pasamanos o travesaño circular de baranda; largo 4568.12; pared 3.68; Ø exterior 48.3; Ø interior 40.94	ASTM A53 Gr B / Fabricar

ISOMÉTRICO A COLOR / REFERENCIA DE MONTAJE

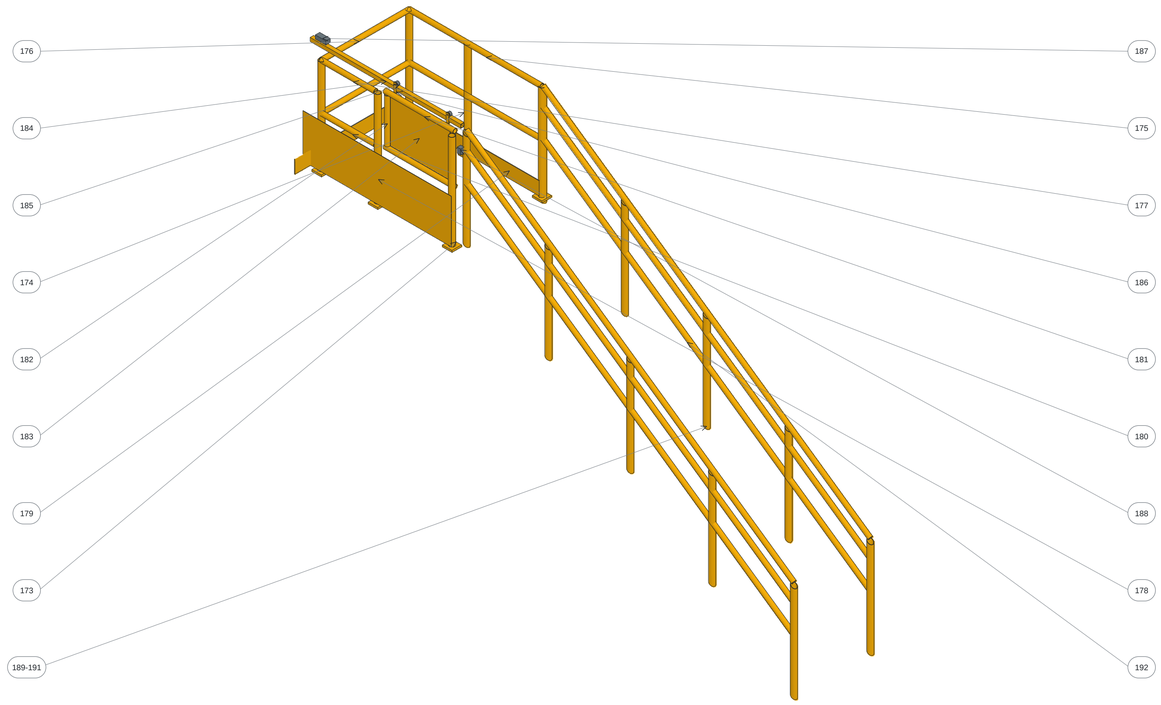

NOTAS DE FABRICACIÓN Y MONTAJE

1. Baranda 1 100 sobre piso; protección intermedia; rodapié 150. Materiales según lista.
2. Conservar ingletes reales y tapas de transición 60x70x8 en extremos superiores.
3. Uniones a pared de 3 mm: PJP a2 según preparación y cuadro de juntas.
4. Soldar en taller según cuadro; eliminar bordes cortantes y asegurar continuidad del pasamanos.
5. Poste a base110x110x20: filete4 continuo. Base al RHS: filete5 continuo.
6. Guías y cierre de puerta: cuatroM10 8.8. Mantener brazo resistente400 mínimo entre fijaciones.

Cotas en mm. ISO2768-m. Soldaduras según cuadro JF. Contornos: CAD/DXF.


TALADROS DE PIEZAS DEL CONJUNTO / COORDENADAS LOCALES mm / ORIGEN LOCAL

P186 T1: Ø12; X0 Y30 Z0; eje Z

				REBABAR Y ROMPER ARISTAS	NO CAMBIAR LA ESCALA	REVISIÓN
SESUVECA DEL PERÚ						
	NOMBRE	FIRMA	FECHA			TÍTULO: Barandas, pasamanos y rodapiés
DIBUJ.	Javier Acevedo		20/10/26			
VERIF.						
APROB.						
FABR.						
CALID.				MATERIAL: SEGÚN LISTA DE MATERIALES		N.° DE DIBUJO EB-14 / A1
PESO: SEGÚN CAD / lista de materiales				ESCALA: INDICADA		ESTACIÓN DE DESCARGA BIGBAG / HOJA 14 DE 16


Cruceta de izaje 2 t ensamblada

PLANTA ESCALA 1:8

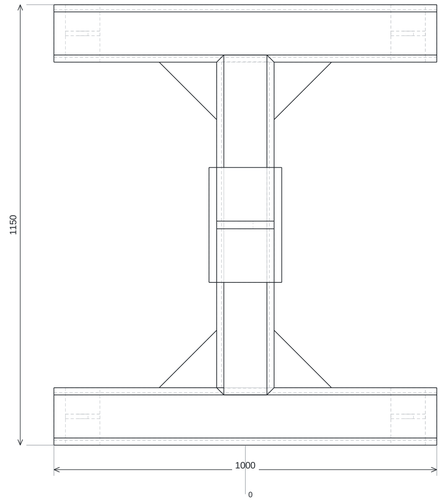


REFERENCIA X (mm)

ALZADO ESCALA 1:4

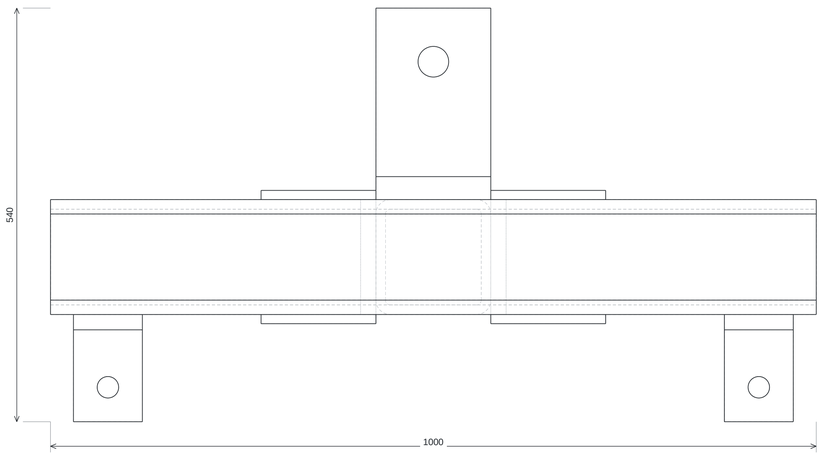

POS.	CANT.	PIEZA / MEDIDAS EN mm	MATERIAL / SUMINISTRO
14	2	Tramo de tubo cuadrado; ancho 150; alto 150; largo 1000; pared 12.5	S355NH / EN10210-1 / Fabricar
15	1	Tramo de tubo cuadrado; ancho 150; alto 150; largo 850; pared 12.5	S355NH / EN10210-1 / Fabricar
51	1	Placa central para levantar cruceta; ancho 150; alto 220; espesor 20; taladros Ø40	ASTM A36 / Fabricar
52	4	Placa extrema para sujetar asa; ancho 90; alto 120; espesor 12; taladros Ø28	ASTM A36 / Fabricar
53	4	Placa de refuerzo de enganche; ancho 90; alto 150; espesor 20	ASTM A36 / Fabricar
54	8	Refuerzo triangular de cruceta; ancho 150; alto 150; espesor 12	ASTM A36 / Fabricar
55	1	Placa superior de cruceta; ancho 150; alto 300; espesor 30	ASTM A36 / Fabricar
56	2	Placa lateral de cruceta; ancho 300; alto 150; espesor 20	ASTM A36 / Fabricar

ISOMÉTRICO A COLOR / REFERENCIA DE MONTAJE

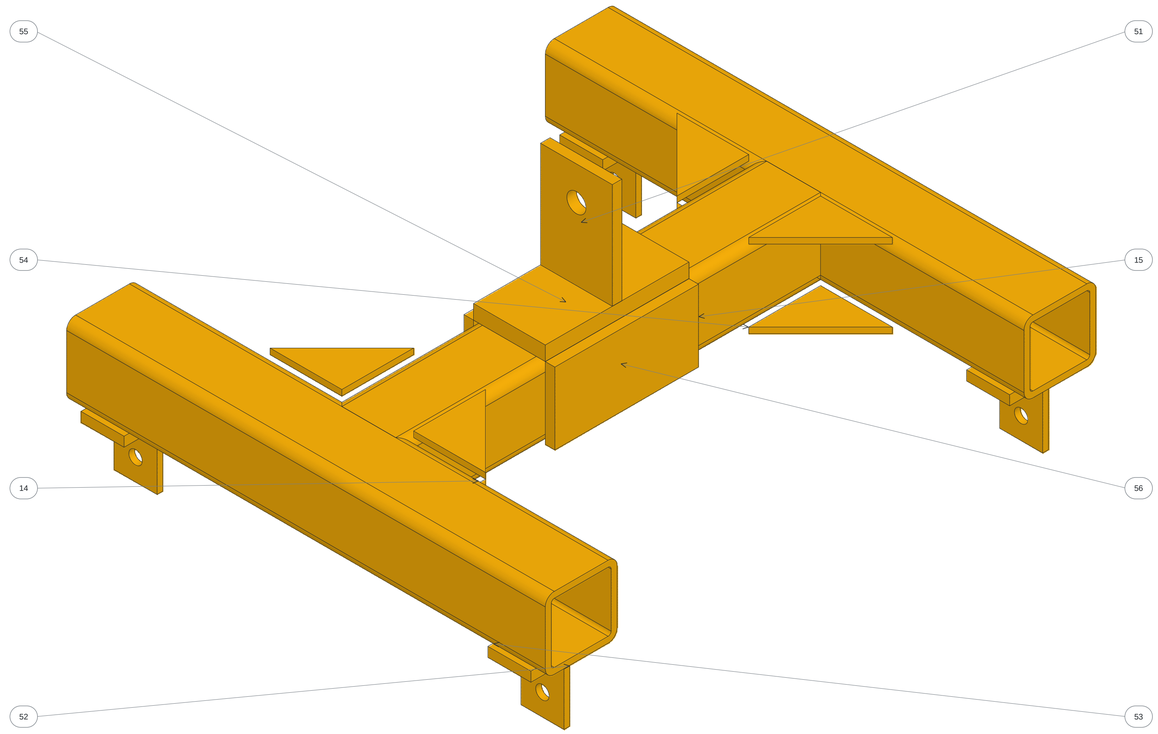

NOTAS DE FABRICACIÓN Y MONTAJE

1. Capacidad nominal 2 000 kg; 125 000 ciclos; Categoría B / Servicio Clase 2.
2. Tubos comerciales Celsius150×150×12.5 S355NH; placas y herrajes según lista.
3. Mantener reparto y geometría de toma del cálculo; identificación indeleble de capacidad y trazabilidad.
4. Ejecutar inspección y prueba de carga según protocolo antes de la puesta en servicio.
5. Tubo central: reserva de corte887.5 mm; luz entre caras850 mm. Contornear ambos extremos al radio real del tubo transversal; soldar todo el perímetro con filete6 mm.
6. Radios nominales R18.75 exterior y R6.25 interior. Acero S355NH con certificado3.1; conservar garganta y contorno de soldaduras indicados.
7. Placas laterales300×150 y respaldos90×150: dos cordones verticales de filete6×98.5 efectivos, centrados en altura, en sus bordes reales. Terminar antes de los radios; sin cordones horizontales sobre las esquinas.

Cotas en mm. ISO2768-m. Soldaduras según cuadro JF. Contornos: CAD/DXF.

TALADROS DE PIEZAS DEL CONJUNTO / COORDENADAS LOCALES mm / ORIGEN LOCAL

P51 T1: Ø40; X0 Y150 Z0; eje Z

P52 T1: Ø28; X0 Y75 Z0; eje Z

				REBABAR Y ROMPER ARISTAS	NO CAMBIAR LA ESCALA		REVISIÓN
SESUVECA DEL PERÚ							
	NOMBRE	FIRMA	FECHA			TÍTULO: Cruceta de izaje 2 t ensamblada	
DIBUJ.	Javier Acevedo		20/10/26				
VERIF.							
APROB.							
FABR.							
CALID.				MATERIAL: SEGÚN LISTA DE MATERIALES		N.º DE DIBUJO EB-15	A1
PESO: SEGÚN CAD / lista de materiales				ESCALA: INDICADA		ESTACIÓN DE DESCARGA BIGBAG	HOJA 15 DE 16

REVISION P05 - REDISENO20/10/2026 - ALCANCE VERIFICADO EN MEMORIA - SIN LIBERACION INTEGRAL

Uniones de fabricación / Cuadro 1

ID	MIEMBRO	SOPORTE	TIPO	a mm	L mm	CENTRO GLOBAL X/Y/Z mm	EJECUCIÓN
JF-001	BRL-A--1	COL-0--1	LUZ	-	-	POR MIEMBRO / SOPORTE	NO SOLDAR / LUZ 2
JF-002	BRL-A--1	COL-3.2--1	LUZ	-	-	POR MIEMBRO / SOPORTE	NO SOLDAR / LUZ 2
JF-003	BRL-B--1	COL-0--1	LUZ	-	-	POR MIEMBRO / SOPORTE	NO SOLDAR / LUZ 2
JF-004	BRL-B--1	COL-3.2--1	LUZ	-	-	POR MIEMBRO / SOPORTE	NO SOLDAR / LUZ 2
JF-005	KNE--1	COL-0--1	LUZ	-	-	POR MIEMBRO / SOPORTE	NO SOLDAR / LUZ 2
JF-006	BRL-A-1	COL-0-1	LUZ	-	-	POR MIEMBRO / SOPORTE	NO SOLDAR / LUZ 2
JF-007	BRL-A-1	COL-3.2-1	LUZ	-	-	POR MIEMBRO / SOPORTE	NO SOLDAR / LUZ 2
JF-008	BRL-B-1	COL-0-1	LUZ	-	-	POR MIEMBRO / SOPORTE	NO SOLDAR / LUZ 2
JF-009	BRL-B-1	COL-3.2-1	LUZ	-	-	POR MIEMBRO / SOPORTE	NO SOLDAR / LUZ 2
JF-010	KNE-1	COL-0-1	LUZ	-	-	POR MIEMBRO / SOPORTE	NO SOLDAR / LUZ 2
JF-019	KNE--1	TRA-0	CJP	3.72	147.61	-0 / -380.2 / 5498	TALLER / WPS
JF-020	KNE-1	TRA-0	CJP	3.72	147.61	0 / 380.2 / 5498	TALLER / WPS
JF-021	BRL-A--1	TIE--1-0.15	LUZ	-	-	POR MIEMBRO / SOPORTE	NO SOLDAR / LUZ 2
JF-022	BRL-B--1	TIE--1-0.15	LUZ	-	-	POR MIEMBRO / SOPORTE	NO SOLDAR / LUZ 2
JF-023	TIE--1-0.15	U02_COLLARX_0_1	CJP	3.72	224	89 / -1000 / 150	TALLER / WPS
JF-024	TIE--1-0.15	BRT_COLLARX_-1_0.15_-1	CJP	3.72	224	3111 / -1000 / 150	TALLER / WPS
JF-025	BRL-A--1	TIE--1-4.79	LUZ	-	-	POR MIEMBRO / SOPORTE	NO SOLDAR / LUZ 2
JF-026	BRL-B--1	TIE--1-4.79	LUZ	-	-	POR MIEMBRO / SOPORTE	NO SOLDAR / LUZ 2
JF-027	TIE--1-4.79	BRT_COLLARX_-1_5.338_-1	CJP	3.72	224	3111 / -1000 / 5430	TALLER / WPS
JF-028	BRL-A--1	U02_COLLARX_0_1	LUZ	-	-	POR MIEMBRO / SOPORTE	NO SOLDAR / LUZ 2
JF-029	BRL-A--1	BRT_COLLARX_-1_5.338_-1	LUZ	-	-	POR MIEMBRO / SOPORTE	NO SOLDAR / LUZ 2
JF-030	BRL-B--1	BRT_COLLARX_-1_0.15_-1	LUZ	-	-	POR MIEMBRO / SOPORTE	NO SOLDAR / LUZ 2
JF-031	KNE--1	U02_COLLARY_8_1	LUZ	-	-	POR MIEMBRO / SOPORTE	NO SOLDAR / LUZ 2
JF-032	BRL-A-1	TIE-1-0.15	LUZ	-	-	POR MIEMBRO / SOPORTE	NO SOLDAR / LUZ 2
JF-033	BRL-B-1	TIE-1-0.15	LUZ	-	-	POR MIEMBRO / SOPORTE	NO SOLDAR / LUZ 2
JF-034	TIE-1-0.15	U02_COLLARX_2_1	CJP	3.72	224	89 / 1000 / 150	TALLER / WPS
JF-035	TIE-1-0.15	BRT_COLLARX_1_0.15_-1	CJP	3.72	224	3111 / 1000 / 150	TALLER / WPS
JF-036	BRL-A-1	TIE-1-4.79	LUZ	-	-	POR MIEMBRO / SOPORTE	NO SOLDAR / LUZ 2
JF-037	BRL-B-1	TIE-1-4.79	LUZ	-	-	POR MIEMBRO / SOPORTE	NO SOLDAR / LUZ 2
JF-038	TIE-1-4.79	BRT_COLLARX_1_5.338_-1	CJP	3.72	224	3111 / 1000 / 5430	TALLER / WPS
JF-039	BRL-A-1	U02_COLLARX_2_1	LUZ	-	-	POR MIEMBRO / SOPORTE	NO SOLDAR / LUZ 2
JF-040	BRL-A-1	BRT_COLLARX_1_5.338_-1	LUZ	-	-	POR MIEMBRO / SOPORTE	NO SOLDAR / LUZ 2
JF-041	BRL-B-1	BRT_COLLARX_1_0.15_-1	LUZ	-	-	POR MIEMBRO / SOPORTE	NO SOLDAR / LUZ 2
JF-042	KNE-1	U02_COLLARY_9_-1	LUZ	-	-	POR MIEMBRO / SOPORTE	NO SOLDAR / LUZ 2

a = garganta efectiva de cálculo; L = longitud efectiva. CJP atraviesa la pared menor; PJP según preparación indicada.

LUZ = holgura de 2 mm libre de soldadura. Transferencia de carga por conexión primaria según memoria.

CJP / V60 / RAÍZ 2



PJP a2 / 2 x 45



FILETE / a SEGÚN CÁLCULO



NOTAS DE FABRICACIÓN Y MONTAJE


1. Soldadura conforme a AWS D1.1; verificación AISC360 según memoria.
2. Material de aporte compatible con metal base. CJP/PJP: procedimiento WPS calificado y aceptación según especificación.
3. Juntas primarias U01 / U02 / BRT / TC y anclajes: ver detalles y memoria. Interfaces JF según este cuadro.
4. Montaje en campo mediante uniones desmontables; conservar piezas KITO sin mecanizado ni soldaduras.

Cotas en mm. ISO2768-m. Soldaduras según cuadro JF. Contornos: CAD/DXF.

				REBABAR Y ROMPER ARISTAS	NO CAMBIAR LA ESCALA		REVISIÓN
SESUVECA DEL PERÚ							
	NOMBRE	FIRMA	FECHA			TÍTULO: Uniones de fabricación / Cuadro 1	
DIBUJ.	Javier Acevedo		20/10/26				
VERIF.							
APROB.							
FABR.							
CALID.				MATERIAL: SEGÚN LISTA DE MATERIALES		N.º DE DIBUJO EB-16	A1
PESO: SEGÚN CAD / lista de materiales				ESCALA: INDICADA		ESTACIÓN DE DESCARGA BIGBAG	HOJA 16 DE 16

P05 / PASANTES M16 / DETALLE DE CAD ACTUAL

A36 t18 inferior; arandela50x50x10; tuerca brida lisa ISO4161 clase10. No soldar perno.

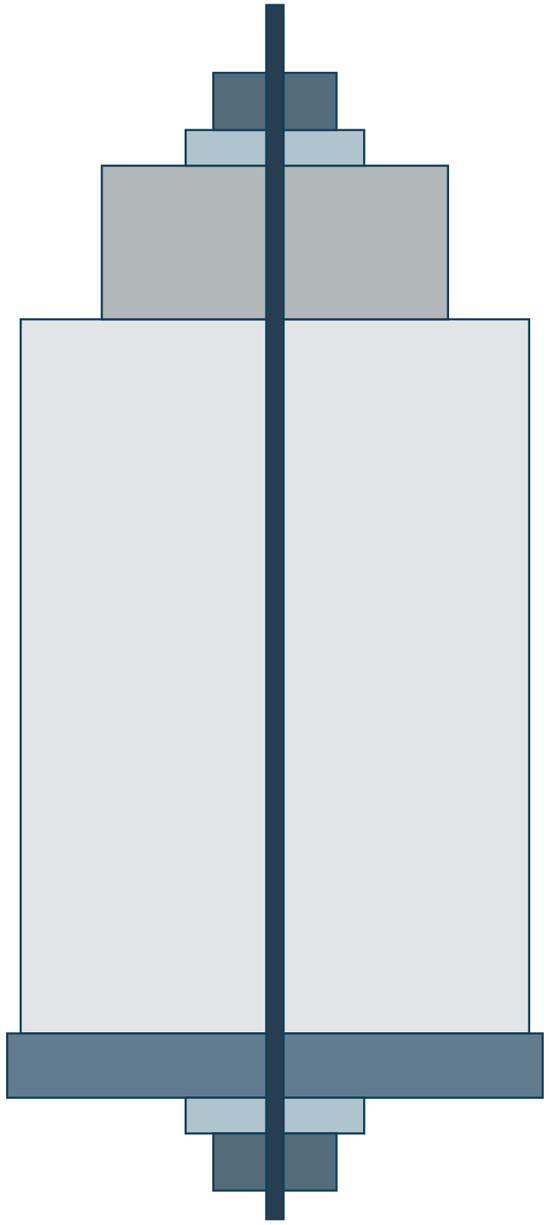

PernoZ+45

Arandela superiorZ0/+10

Cara losaZ-43

Losa200 / dobleD10@150

Cara losaZ-243

Contraplaca t18 Z-261/-243

Tuerca inferiorZ-287/-271

Perno extremoZ-295; proyeccion minima7mm

33 CONTRAPLACAS /52 PERNOS

26 simples150x150x18

2 comunes175x360x18, tres taladros

5 comunes290x290x18, cuatro taladros

Contorno comun = union de cuadrados150

TaladrosD18; arandela superior a5

Apoyo continuo y plano, sin vacios

Perno8.8 sin soldar; brida lisa dw>=31.9

Base de acceso superior+12mm; base/calce220x220. Otras bases segun CAD. Replantear bordes reales.

Las cotas geometricas no acreditan capacidad global de losa. Planos/DXF actuales prevalecen sobre antecedentes.

ALIMENTACIÓN Y MANDO ELÉCTRICO

ESTACIÓN BIGBAG · CONEXIONES Y SECUENCIA DE MANDO

POTENCIA · 380 V / 3F / 60 Hz + PE · TABLERO IP65

X1:1-2-3 / PE
Red de alimentación

Q0 / QF0 / ID0
C60N 25A curva C
ID30mA,60Hz,VFD

QF1 → K1 → K2
Protección según placa/cable

X2 → KITO SHER2M · 2 t
PE continuo a motores, gabinete, estructura y ductos conductores

QF2 → KM3
Protección según placa/cable

X3 → COLECTOR · 2,2 kW
PE continuo a motores, gabinete, estructura y ductos conductores

QF3 → T1 → PS1
Protección según placa/cable

380/230 VAC → 24 VDC PELV
PE continuo a motores, gabinete, estructura y ductos conductores

SEGURIDAD Y ÓRDENES · 24 VDC

X4 / X7 · Entradas dobles
S10 E-stop / S3 recinto
S16 puerta / S17 cerrojo
S18 aislamiento / S19 parada
S20 retención mecánica de carga

SR1 · Control de seguridad
Entradas con prueba y diagnóstico
S21 solicitud por llave / S23 diagnóstico
S22 rearme por flanco, mandos sueltos
EDM K1/K2/freno y llave cautiva KS1

K1 / K2 · Corte de potencia de movimiento
Dos salidas de seguridad independientes → bobinas K1 y K2
Contactos espejo NC en EDM; freno aplicado sin energía
GL1/KACC: energía para liberar puerta; resorte para bloquear
Circuito específico del freno según esquema KITO

PLC1 / SR1 · Permisos de proceso y seguridad
X5:S1…S23 monitorización; X4/X7: canales reales hacia SR1.
S2/S14 excluyentes; S13 confirma parada antes de mover pasador.
S5: fondo ≥ 3.520 mm para traslación y retirada de traba.
S4 detiene descenso; S9 bolsa vacía / S12 retorno / S8 captación.
Movimiento exige S16 y S17, sin solicitud de acceso ni aislamiento.
Abrir: carro trabado, bolsa apoyada/asegurada y energía aislada.
Cerrar no reinicia: nuevo rearme y nuevo mando de movimiento.

X6 · Relés de interfaz, contactos secos aislados
1 KTR → permitir traslación KITO
2 KDN → permitir descenso bajo / 3 KUP → subida de retorno
4 KMG → liberar compuerta / 5 KPIN → liberar retenedor
6 Y0 → aire mesa / 7 Y1 → bajar / 8 Y2 → liberar bloqueo
9 KACC → GL1, cerrojo de puerta superior; retorno a 0 V
GL1: EUCHNER084820,24V,IP67,FZh1500N; escape interior
Común 0 V: X6:0. Bobinas con protección de sobretensión.
No alimentar entradas KITO sin cotejar tensión y bornes.

CONEXIÓN E INSTALACIÓN

Indeco RZ1-K4x4mm² +PE4mm²,canalizacion metalica IP65; L1-L2-L3,cuarta vena reserva; sin neutro.

QF0 Schneider M9F11325; ID0 30mA apto para variador y60Hz; PE fuera del diferencial. Prueba sinN segun fabricante.

QF1/QF2/QF3:coordinar placa,arranque,Icu y cable; Ib<=25A<=Iz corregida; verificar caida de tension.

Comprobar PE,aislamiento,E-stop,puertas,sensores y ausencia de rearranque; mantener SR1 yEDM.

IP65 no acredita ATEX. Ubicar tablero segun zona; purga y paro de extraccion segun proteccion del colector.

Diseño de conexión. Ajustes eléctricos y tamaño del actuador según equipo suministrado.

Rearme manual. Sin arranque automático al recuperar energía.


SESUVECA DEL PERÚ
EL-01 | A3 | Unidades: V / bar / mm

SESUVECA DEL PERÚ

MESA ELEVADORA · CIRCUITO NEUMÁTICO

ESTACIÓN BIGBAG · CONEXIONES Y SECUENCIA DE MANDO

ALIMENTACIÓN Y DISTRIBUCIÓN · TRAZO CONTINUO: AIRE / DISCONTINUO: PILOTO

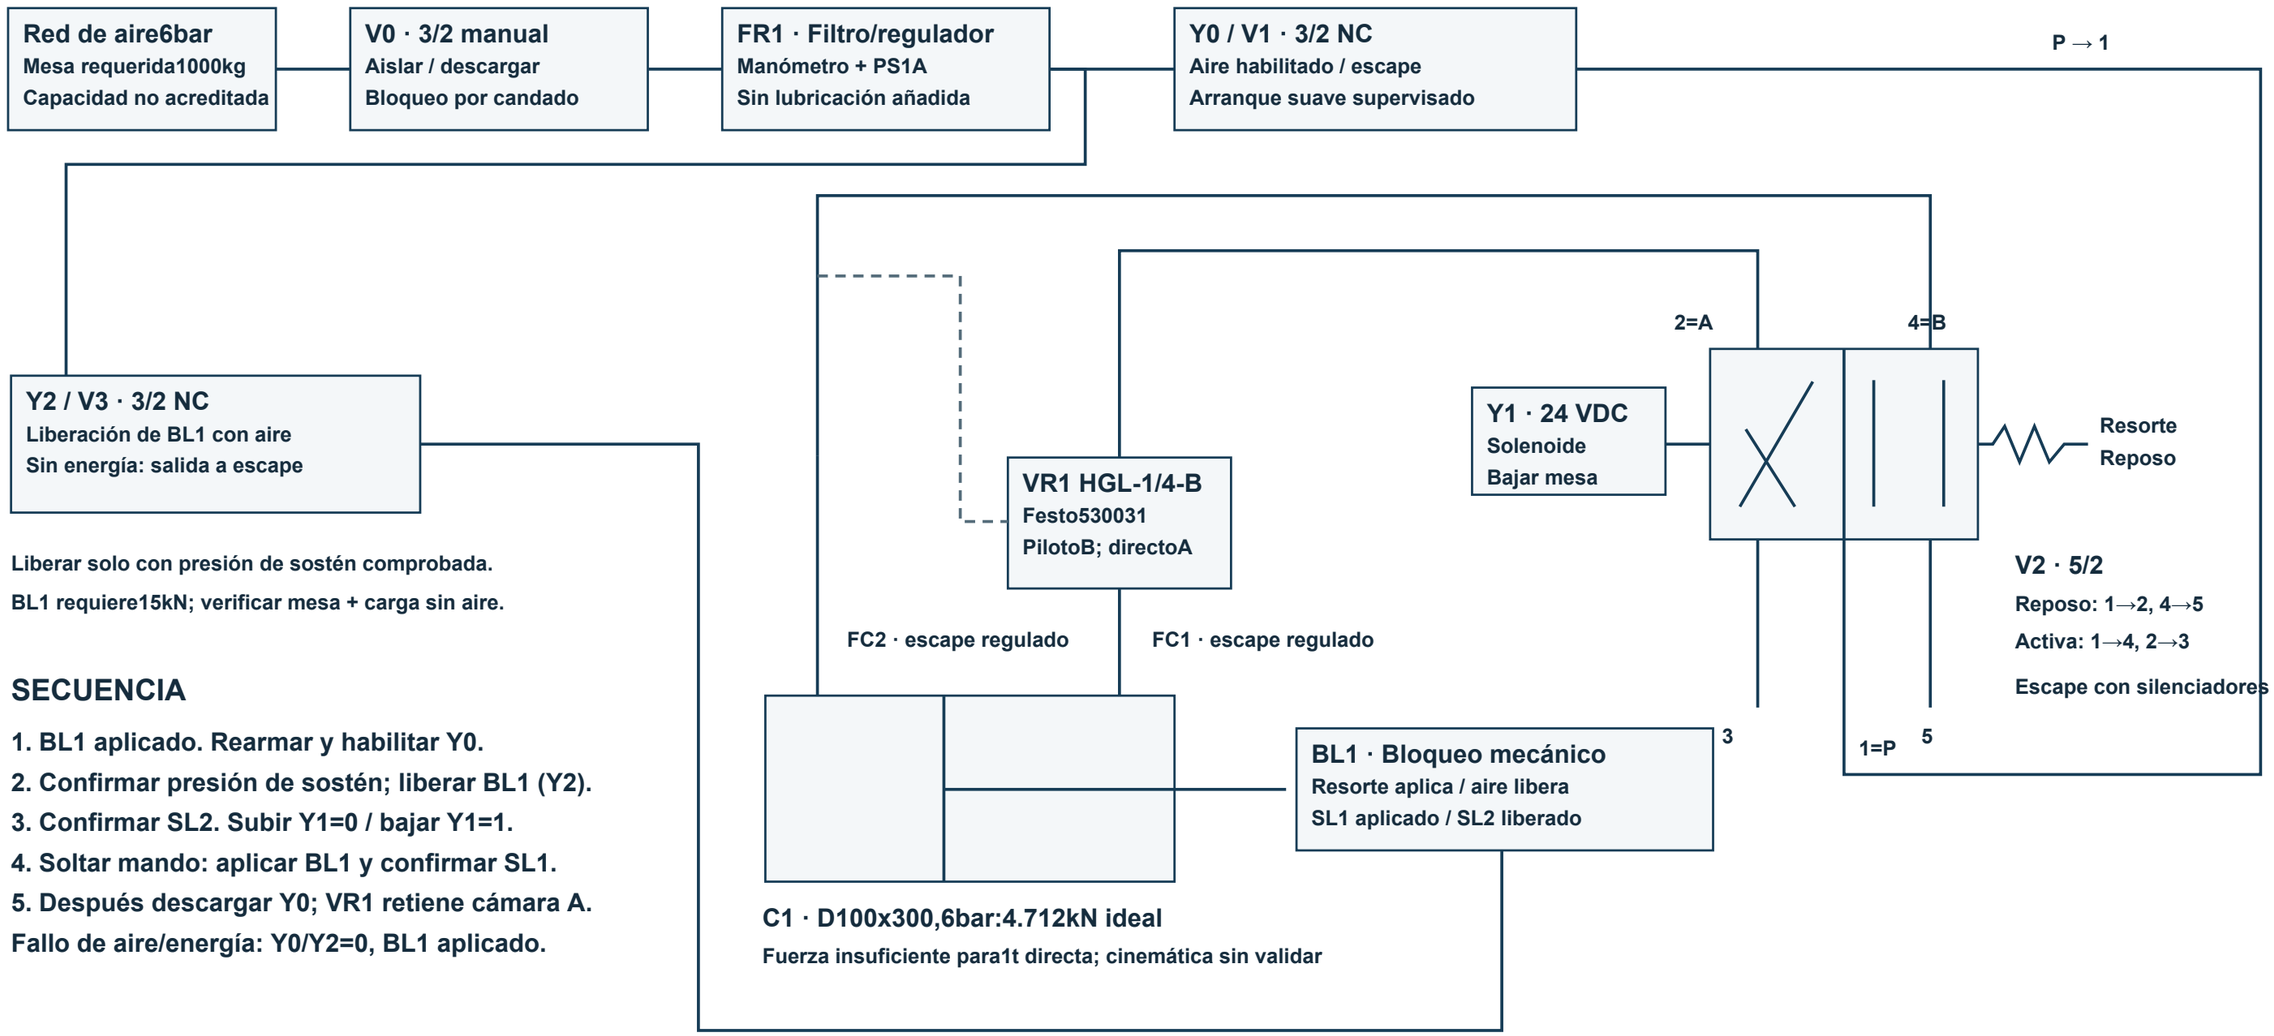

Liberar solo con presión de sostén comprobada.

BL1 requiere15kN; verificar mesa + carga sin aire.

SECUENCIA

1. BL1 aplicado. Rearmar y habilitar Y0.
2. Confirmar presión de sostén; liberar BL1 (Y2).
3. Confirmar SL2. Subir Y1=0 / bajar Y1=1.
4. Soltar mando: aplicar BL1 y confirmar SL1.
5. Después descargar Y0; VR1 retiene cámara A.

Fallo de aire/energía: Y0/Y2=0, BL1 aplicado.

DATOS DE SELECCIÓN Y COMPROBACIÓN

V2 Festo575511 / VUVS-L25-M52-MD-G14-F8-1C1:5/2,24VDC,muelle mecanico,G1/4,2.5..10bar.
Mesa requerida1000kg; cilindroD100x300 a6bar: capacidad de elevacion no acreditada.
Dimensionar VR1,FC1/FC2,tuberias yBL1 con cilindro,relacion de tijera,carga,velocidad y capacidad de detencion.
Una5/2 con resorte no retiene carga al perder aire. VR1 yBL1 conservan funciones independientes.
Antes de intervenir:apoyo rigido,V0 con candado y presion cero en ambas camaras; VR1 puede atrapar aire.

Diseño de conexión. Ajustes eléctricos y tamaño del actuador según equipo suministrado.

Rearme manual. Sin arranque automático al recuperar energía.

SESUVECA DEL PERÚ

NE-01 | A3 | Unidades: V / bar / mm

DESPIECE DE FABRICACIÓN / COTAS LOCALES


Detalles 1..4 de 175 componentes fabricados. Proyecciones exactas de la geometría final.

P001 | CANT. 4


SHS150x150x6_L5488000_P05

ASTM A500 Gr.B | ENVOLVENTE LOCAL X/Y/Z: 150 x 150 x 5488


XY / escala 1:4

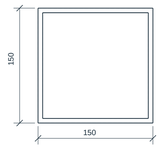

XZ / escala 1:10 / INTERRUMPIDA

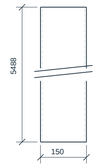

YZ / escala 1:10 / INTERRUMPIDA

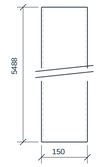


PERFIL SHS150x150x6; longitud nominal 5488. Preparaciones y recortes finales en vistas/DXF.
Sin taladros parametrizados adicionales. Contornos circulares en vistas y DXF.

P002 | CANT. 2

IPE200_L2000000_P05

ASTM A36 | ENVOLVENTE LOCAL X/Y/Z: 100 x 200 x 2000


XY / escala 1:4

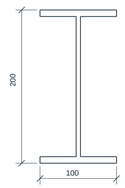

XZ / escala 1:10 / INTERRUMPIDA



YZ / escala 1:10 / INTERRUMPIDA

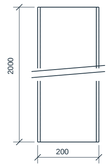


PERFIL IPE200; longitud nominal 2000. Preparaciones y recortes finales en vistas/DXF.
Sin taladros parametrizados adicionales. Contornos circulares en vistas y DXF.

P003 | CANT. 1


I_A240x140x8x20_L3600000_P05

ASTM A36 | ENVOLVENTE LOCAL X/Y/Z: 140 x 240 x 3600


XY / escala 1:4

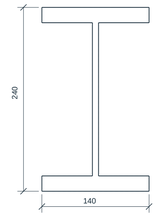

XZ / escala 1:10 / INTERRUMPIDA

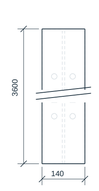

YZ / escala 1:10 / INTERRUMPIDA

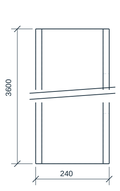

PERFIL I_A240x140x8x20; longitud nominal 3600. Preparaciones y recortes finales en vistas/DXF.

TALADROS / EJES: ID - Ø - X - Y - Z - DIRECCIÓN (mm)


B1 / 18 / -30 / 95 / 155 / Y
B2 / 18 / 30 / 95 / 155 / Y
B3 / 18 / -30 / 95 / 245 / Y
B4 / 18 / 30 / 95 / 245 / Y
B5 / 18 / -30 / 95 / 3355 / Y
B6 / 18 / 30 / 95 / 3355 / Y
B7 / 18 / -30 / 95 / 3445 / Y
B8 / 18 / 30 / 95 / 3445 / Y
B9 / 22 / -35 / 99 / 2450 / Y
B10 / 22 / 35 / 99 / 2450 / Y
B11 / 22 / -35 / 99 / 2650 / Y
B12 / 22 / 35 / 99 / 2650 / Y

P004 | CANT. 4


SHS100x100x5_L2848000_P05

ASTM A500 Gr.B | ENVOLVENTE LOCAL X/Y/Z: 100 x 100 x 2848


XY / escala 1:2

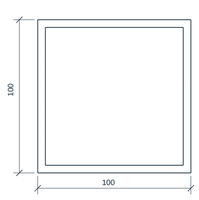

XZ / escala 1:10 / INTERRUMPIDA

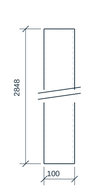

YZ / escala 1:10 / INTERRUMPIDA

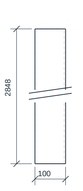

PERFIL SHS100x100x5; longitud nominal 2848. Preparaciones y recortes finales en vistas/DXF.
Sin taladros parametrizados adicionales. Contornos circulares en vistas y DXF.

Cotas en mm. Unidades y referencias locales X/Y/Z. Las vistas de detalle y DXF son proyecciones del CAD exacto OpenCascade; no se atribuye exportación nativa de SolidWorks a estas láminas.

Tolerancias ISO 2768-1 clase m en cotas lineales/angulares de piezas mecanizadas sin tolerancia individual. No se aplica a ajustes, soldaduras, equipos comerciales ni dimensiones de montaje críticas.

No escalar el PDF. Taladrar/escariar y desbarbar; eliminar aristas cortantes. Las preparaciones con luz 2 mm conservan geometría CAD; ejecutar soldadura únicamente según cuadro de juntas y WPS aplicable.

Acabados, ajustes y aceptación de uniones: según memoria, detalle específico y programa de inspección. Los espacios de verificación/aprobación permanecen sin firma.

Fuente: native_manifest.json + solidworks_model.bas; geometría y coordenadas íntegramente trazadas.

P05 - PLANOS DE DETALLE PARA REVISIÓN TÉCNICA

ESTACIÓN BIGBAG							**P05**
SESUVECA DEL PERÚ				SESUVECA DEL PERÚ			
DIBUJ.	PROYECTO P05		16/10/2026			**DESPIECE DE FABRICACIÓN / COTAS LOCALES**	
VERIF.							
APROB.							
FABR.							
CALID.				MATERIAL: SEGÚN DESPIECE		**ESTACIÓN DE DESCARGA BIGBAG**	**A1**
PESO: BOM / CAD				ESCALA: INDICADA		**P05-T-001**	HOJA 1/51

DESPIECE DE FABRICACIÓN / COTAS LOCALES


Detalles 5..8 de 175 componentes fabricados. Proyecciones exactas de la geometría final.

P005 | CANT. 2

SHS150x150x6_L2200000_CUTda1945_P05

ASTM A500 Gr.B | ENVOLVENTE LOCAL X/Y/Z: 150 x 150 x 2350


XY / escala 1:4

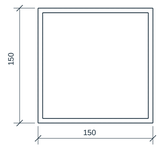

XZ / escala 1:10 / INTERRUMPIDA



YZ / escala 1:10 / INTERRUMPIDA

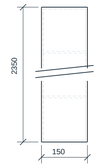


PERFIL SHS150x150x6; longitud nominal 2200. Preparaciones y recortes finales en vistas/DXF.
Sin taladros parametrizados adicionales. Contornos circulares en vistas y DXF.

P006 | CANT. 2


SHS150x150x6_L1650000_CUT8f76b3_P05

ASTM A500 Gr.B | ENVOLVENTE LOCAL X/Y/Z: 150 x 150 x 1800


XY / escala 1:4

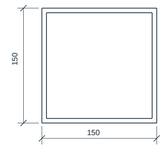

XZ / escala 1:10 / INTERRUMPIDA

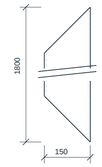

YZ / escala 1:10 / INTERRUMPIDA

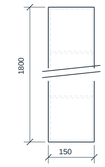


PERFIL SHS150x150x6; longitud nominal 1650. Preparaciones y recortes finales en vistas/DXF.
Sin taladros parametrizados adicionales. Contornos circulares en vistas y DXF.

P007 | CANT. 2


SHS60x60x4_L2100000_P05

ASTM A500 Gr.B | ENVOLVENTE LOCAL X/Y/Z: 60 x 60 x 2100

XY / escala 1:1

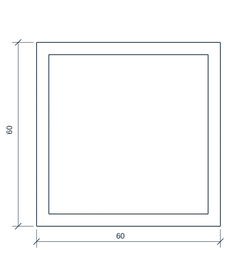

XZ / escala 1:10 / INTERRUMPIDA

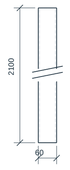

YZ / escala 1:10 / INTERRUMPIDA




PERFIL SHS60x60x4; longitud nominal 2100. Preparaciones y recortes finales en vistas/DXF.
Sin taladros parametrizados adicionales. Contornos circulares en vistas y DXF.

P008 | CANT. 2

SHS60x60x4_L1550000_P05

ASTM A500 Gr.B | ENVOLVENTE LOCAL X/Y/Z: 60 x 60 x 1550

XY / escala 1:1

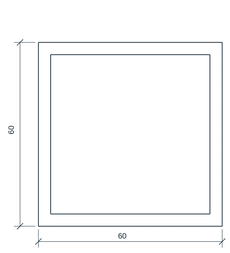

XZ / escala 1:10 / INTERRUMPIDA



YZ / escala 1:10 / INTERRUMPIDA



PERFIL SHS60x60x4; longitud nominal 1550. Preparaciones y recortes finales en vistas/DXF.
Sin taladros parametrizados adicionales. Contornos circulares en vistas y DXF.

Cotas en mm. Unidades y referencias locales X/Y/Z. Las vistas de detalle y DXF son proyecciones del CAD exacto OpenCascade; no se atribuye exportación nativa de SolidWorks a estas láminas.

Tolerancias ISO 2768-1 clase m en cotas lineales/angulares de piezas mecanizadas sin tolerancia individual. No se aplica a ajustes, soldaduras, equipos comerciales ni dimensiones de montaje críticas.

No escalar el PDF. Taladrar/escariar y desbarbar; eliminar aristas cortantes. Las preparaciones con luz 2 mm conservan geometría CAD; ejecutar soldadura únicamente según cuadro de juntas y WPS aplicable.

Acabados, ajustes y aceptación de uniones: según memoria, detalle específico y programa de inspección. Los espacios de verificación/aprobación permanecen sin firma.

Fuente: native_manifest.json + solidworks_model.bas; geometría y coordenadas íntegramente trazadas.

ESTACIÓN BIGBAG							**P05**
SESUVECA DEL PERÚ							
						DESPIECE DE FABRICACIÓN / COTAS LOCALES	
DIBUJ.	PROYECTO P05		16/10/2026				
VERIF.							
APROB.							
FABR.							
CALID.				MATERIAL: SEGÚN DESPIECE		**ESTACIÓN DE DESCARGA BIGBAG**	**A1**
PESO: BOM / CAD				ESCALA: INDICADA		**P05-T-002**	HOJA 2/51

DESPIECE DE FABRICACIÓN / COTAS LOCALES


Detalles 9..12 de 175 componentes fabricados. Proyecciones exactas de la geometría final.

P009 | CANT. 4


SHS100x100x5_L1499304_TOLVA

ASTM A500 Gr.B | ENVOLVENTE LOCAL X/Y/Z: 100 x 100 x 1599.3


XY / escala 1:2

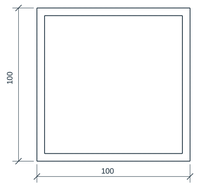

XZ / escala 1:10 / INTERRUMPIDA

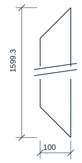

YZ / escala 1:10 / INTERRUMPIDA

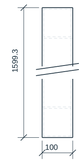


PERFIL SHS100x100x5; longitud nominal 1499.3. Preparaciones y recortes finales en vistas/DXF.
Sin taladros parametrizados adicionales. Contornos circulares en vistas y DXF.

P010 | CANT. 2


RHS150x75x5_L1757000_CUT394f60_P05

ASTM A500 Gr.B | ENVOLVENTE LOCAL X/Y/Z: 75 x 150 x 1832


XY / escala 1:4

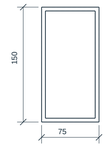

XZ / escala 1:10 / INTERRUMPIDA

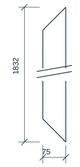

YZ / escala 1:10 / INTERRUMPIDA

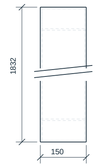


PERFIL RHS150x75x5; longitud nominal 1757. Preparaciones y recortes finales en vistas/DXF.
Sin taladros parametrizados adicionales. Contornos circulares en vistas y DXF.

P011 | CANT. 2

RHS150x75x5_L1757000_CUT3ec3f6_P05

ASTM A500 Gr.B | ENVOLVENTE LOCAL X/Y/Z: 75 x 150 x 1832


XY / escala 1:4

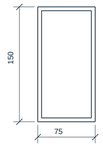

XZ / escala 1:10 / INTERRUMPIDA



YZ / escala 1:10 / INTERRUMPIDA

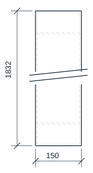


PERFIL RHS150x75x5; longitud nominal 1757. Preparaciones y recortes finales en vistas/DXF.
Sin taladros parametrizados adicionales. Contornos circulares en vistas y DXF.

P012 | CANT. 2

SHS60x60x4_L2882256_CUTf8e6e9_P05

ASTM A500 Gr.B | ENVOLVENTE LOCAL X/Y/Z: 60 x 60 x 2976.32


XY / escala 1:1

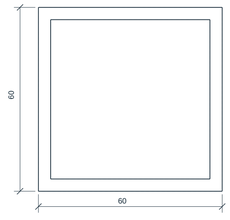

XZ / escala 1:10 / INTERRUMPIDA



YZ / escala 1:10 / INTERRUMPIDA

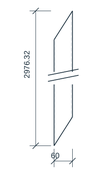

PERFIL SHS60x60x4; longitud nominal 2882.26. Preparaciones y recortes finales en vistas/DXF.
Sin taladros parametrizados adicionales. Contornos circulares en vistas y DXF.

Cotas en mm. Unidades y referencias locales X/Y/Z. Las vistas de detalle y DXF son proyecciones del CAD exacto OpenCascade; no se atribuye exportación nativa de SolidWorks a estas láminas.

Tolerancias ISO 2768-1 clase m en cotas lineales/angulares de piezas mecanizadas sin tolerancia individual. No se aplica a ajustes, soldaduras, equipos comerciales ni dimensiones de montaje críticas.

No escalar el PDF. Taladrar/escariar y desbarbar; eliminar aristas cortantes. Las preparaciones con luz 2 mm conservan geometría CAD; ejecutar soldadura únicamente según cuadro de juntas y WPS aplicable.

Acabados, ajustes y aceptación de uniones: según memoria, detalle específico y programa de inspección. Los espacios de verificación/aprobación permanecen sin firma.

Fuente: native_manifest.json + solidworks_model.bas; geometría y coordenadas íntegramente trazadas.

P05 - PLANOS DE DETALLE PARA REVISIÓN TÉCNICA

ESTACIÓN BIGBAG							**P05**
SESUVECA DEL PERÚ							
DIBUJ.	PROYECTO P05		16/10/2026			**DESPIECE DE FABRICACIÓN / COTAS LOCALES**	
VERIF.							
APROB.							
FABR.							
CALID.				MATERIAL: SEGÚN DESPIECE		**ESTACIÓN DE DESCARGA BIGBAG**	**A1**
PESO: BOM / CAD				ESCALA: INDICADA		**P05-T-003**	HOJA 3/51

DESPIECE DE FABRICACIÓN / COTAS LOCALES


Detalles 13..16 de 175 componentes fabricados. Proyecciones exactas de la geometría final.

P013 | CANT. 2

SHS80x80x4_L2050000_P05

ASTM A500 Gr.B | ENVOLVENTE LOCAL X/Y/Z: 80 x 80 x 2050

XY / escala 1:2

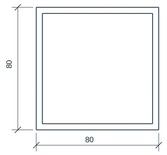

XZ / escala 1:10 / INTERRUMPIDA



YZ / escala 1:10 / INTERRUMPIDA




PERFIL SHS80x80x4; longitud nominal 2050. Preparaciones y recortes finales en vistas/DXF.
Sin taladros parametrizados adicionales. Contornos circulares en vistas y DXF.

P014 | CANT. 2


SHS150x150x12p5_L1000000_P05

S355NH / EN10210-1 | ENVOLVENTE LOCAL X/Y/Z: 150 x 150 x 1000


XY / escala 1:4

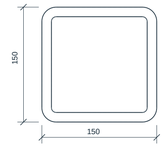

XZ / escala 1:4 / INTERRUMPIDA

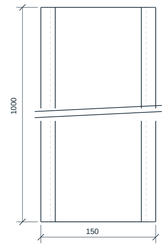

YZ / escala 1:4 / INTERRUMPIDA

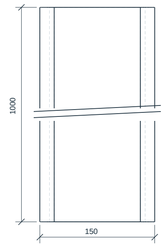


PERFIL SHS150x150x12.5; longitud nominal 1000. Preparaciones y recortes finales en vistas/DXF.
Sin taladros parametrizados adicionales. Contornos circulares en vistas y DXF.

P015 | CANT. 1


SHS150x150x12p5_L850000_P05

S355NH / EN10210-1 | ENVOLVENTE LOCAL X/Y/Z: 150 x 150 x 887.5


XY / escala 1:4

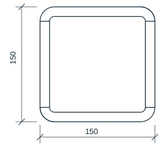

XZ / escala 1:4 / INTERRUMPIDA

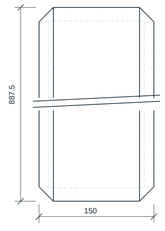

YZ / escala 1:4 / INTERRUMPIDA

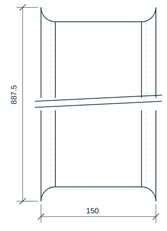


PERFIL SHS150x150x12.5; longitud nominal 850. Preparaciones y recortes finales en vistas/DXF.
Sin taladros parametrizados adicionales. Contornos circulares en vistas y DXF.

P016 | CANT. 4


SHS60x60x4_L62410_P05

ASTM A500 Gr.B | ENVOLVENTE LOCAL X/Y/Z: 60 x 60 x 62.41


XY / escala 1:1

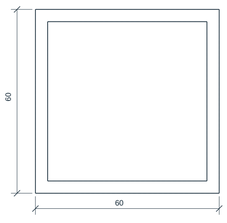

XZ / escala 1:1

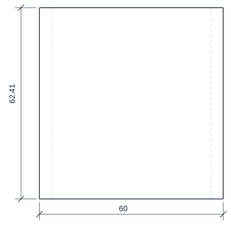

YZ / escala 1:1

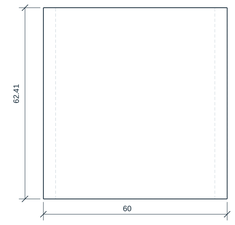

PERFIL SHS60x60x4; longitud nominal 62.41. Preparaciones y recortes finales en vistas/DXF.
Sin taladros parametrizados adicionales. Contornos circulares en vistas y DXF.

Cotas en mm. Unidades y referencias locales X/Y/Z. Las vistas de detalle y DXF son proyecciones del CAD exacto OpenCascade; no se atribuye exportación nativa de SolidWorks a estas láminas.

Tolerancias ISO 2768-1 clase m en cotas lineales/angulares de piezas mecanizadas sin tolerancia individual. No se aplica a ajustes, soldaduras, equipos comerciales ni dimensiones de montaje críticas.

No escalar el PDF. Taladrar/escariar y desbarbar; eliminar aristas cortantes. Las preparaciones con luz 2 mm conservan geometría CAD; ejecutar soldadura únicamente según cuadro de juntas y WPS aplicable.

Acabados, ajustes y aceptación de uniones: según memoria, detalle específico y programa de inspección. Los espacios de verificación/aprobación permanecen sin firma.

Fuente: native_manifest.json + solidworks_model.bas; geometría y coordenadas íntegramente trazadas.

ESTACIÓN BIGBAG						**P05**
SESUVECA DEL PERÚ						
						DESPIECE DE FABRICACIÓN / COTAS LOCALES
DIBUJ.	PROYECTO P05		16/10/2026			
VERIF.						
APROB.						
FABR.						
CALID.				MATERIAL: SEGÚN DESPIECE		**ESTACIÓN DE DESCARGA BIGBAG**
PESO: BOM / CAD				ESCALA: INDICADA		**P05-T-004**

DESPIECE DE FABRICACIÓN / COTAS LOCALES


Detalles 17..20 de 175 componentes fabricados. Proyecciones exactas de la geometría final.

P017 | CANT. 4

TOL_PANEL_CONO_8mm

ASTM A36 | ENVOLVENTE LOCAL X/Y/Z: 1691.57 x 1404.62 x 8

XY / escala 1:20

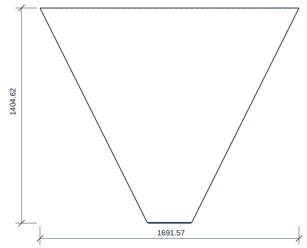

XZ / escala 1:5 / INTERRUMPIDA



YZ / escala 1:4 / INTERRUMPIDA




CHAPA: espesor 8. Contorno nominal CAD; corte y taladros se identifican por coordenadas locales.
Sin taladros parametrizados adicionales. Contornos circulares en vistas y DXF.

P018 | CANT. 3

TOL_PANEL_CUERPO_6mm_P05

ASTM A36 | ENVOLVENTE LOCAL X/Y/Z: 1682 x 470.15 x 6

XY / escala 1:20

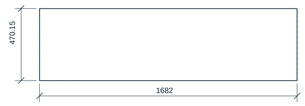

XZ / escala 1:5 / INTERRUMPIDA



YZ / escala 1:2 / INTERRUMPIDA




CHAPA: espesor 6. Contorno nominal CAD; corte y taladros se identifican por coordenadas locales.
Sin taladros parametrizados adicionales. Contornos circulares en vistas y DXF.

P019 | CANT. 1

TOL_PANEL_CUERPO_DN150_6mm_P05

ASTM A36 | ENVOLVENTE LOCAL X/Y/Z: 1682 x 470.15 x 6

XY / escala 1:20

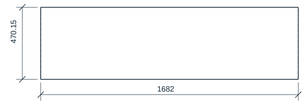

XZ / escala 1:5 / INTERRUMPIDA



YZ / escala 1:2 / INTERRUMPIDA




CHAPA: espesor 6. Contorno nominal CAD; corte y taladros se identifican por coordenadas locales.
Sin taladros parametrizados adicionales. Contornos circulares en vistas y DXF.

P020 | CANT. 1

TOL_TAPA_POLVO_1662x1662x3_P05

ASTM A36 | ENVOLVENTE LOCAL X/Y/Z: 1682 x 1682 x 3

XY / escala 1:40

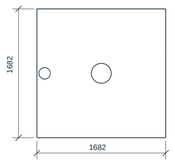

XZ / escala 1:5 / INTERRUMPIDA



YZ / escala 1:5 / INTERRUMPIDA



CHAPA: espesor 3. Contorno nominal CAD; corte y taladros se identifican por coordenadas locales.
TALADROS / EJES: ID - Ø - X - Y - Z - DIRECCIÓN (mm)
T1 / 260 / 0 / 0 / 0 / Z
T2 / 150 / 740 / 0 / 0 / Z

Cotas en mm. Unidades y referencias locales X/Y/Z. Las vistas de detalle y DXF son proyecciones del CAD exacto OpenCascade; no se atribuye exportación nativa de SolidWorks a estas láminas.

Tolerancias ISO 2768-1 clase m en cotas lineales/angulares de piezas mecanizadas sin tolerancia individual. No se aplica a ajustes, soldaduras, equipos comerciales ni dimensiones de montaje críticas.

No escalar el PDF. Taladrar/escariar y desbarbar; eliminar aristas cortantes. Las preparaciones con luz 2 mm conservan geometría CAD; ejecutar soldadura únicamente según cuadro de juntas y WPS aplicable.

Acabados, ajustes y aceptación de uniones: según memoria, detalle específico y programa de inspección. Los espacios de verificación/aprobación permanecen sin firma.

Fuente: native_manifest.json + solidworks_model.bas; geometría y coordenadas íntegramente trazadas.

ESTACIÓN BIGBAG						P05
SESUVECA DEL PERÚ						
						DESPIECE DE FABRICACIÓN / COTAS LOCALES
DIBUJ.	PROYECTO P05		16/10/2026			
VERIF.						
APROB.						
FABR.						
CALID.				MATERIAL: SEGÚN DESPIECE		ESTACIÓN DE DESCARGA BIGBAG / A1
PESO: BOM / CAD				ESCALA: INDICADA		P05-T-005 / HOJA 5/51

DESPIECE DE FABRICACIÓN / COTAS LOCALES


Detalles 21..24 de 175 componentes fabricados. Proyecciones exactas de la geometría final.

P022 | CANT. 2


BASE_PORTICO_360x360x35

ASTM A36 | ENVOLVENTE LOCAL X/Y/Z: 360 x 360 x 35


XY / escala 1:5

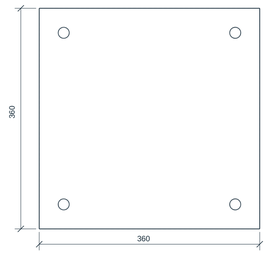

XZ / escala 1:2 / INTERRUMPIDA

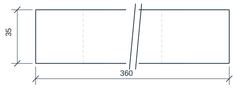

YZ / escala 1:2 / INTERRUMPIDA

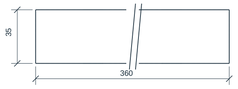


CHAPA: espesor 35. Contorno nominal CAD; corte y taladros se identifican por coordenadas locales.
TALADROS / EJES: ID - Ø - X - Y - Z - DIRECCIÓN (mm)
T1 / 18 / -140 / -140 / 0 / Z
T2 / 18 / -140 / 140 / 0 / Z
T3 / 18 / 140 / -140 / 0 / Z
T4 / 18 / 140 / 140 / 0 / Z

P023 | CANT. 2


BASE_TOLVA_250x250x25

ASTM A36 | ENVOLVENTE LOCAL X/Y/Z: 250 x 250 x 25


XY / escala 1:4

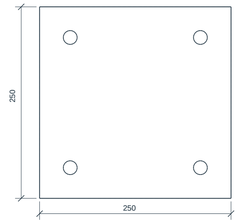

XZ / escala 1:2 / INTERRUMPIDA

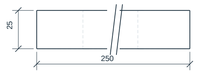

YZ / escala 1:2 / INTERRUMPIDA

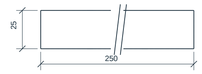


CHAPA: espesor 25. Contorno nominal CAD; corte y taladros se identifican por coordenadas locales.
TALADROS / EJES: ID - Ø - X - Y - Z - DIRECCIÓN (mm)
T1 / 18 / -85 / -85 / 0 / Z
T2 / 18 / -85 / 85 / 0 / Z
T3 / 18 / 85 / -85 / 0 / Z
T4 / 18 / 85 / 85 / 0 / Z

P024 | CANT. 2


U01_CAP_200x200x12_P05

ASTM A36 | ENVOLVENTE LOCAL X/Y/Z: 200 x 200 x 12


XY / escala 1:4

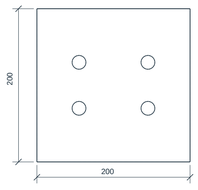

XZ / escala 1:1 / INTERRUMPIDA

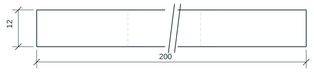

YZ / escala 1:1 / INTERRUMPIDA

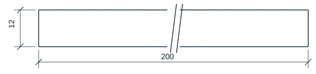


CHAPA: espesor 12. Contorno nominal CAD; corte y taladros se identifican por coordenadas locales.
TALADROS / EJES: ID - Ø - X - Y - Z - DIRECCIÓN (mm)
T1 / 18 / -45 / -30 / 0 / Z
T2 / 18 / -45 / 30 / 0 / Z
T3 / 18 / 45 / -30 / 0 / Z
T4 / 18 / 45 / 30 / 0 / Z

P025 | CANT. 4


U01_LATERAL_200x240x12_P05

ASTM A36 | ENVOLVENTE LOCAL X/Y/Z: 200 x 240 x 12

XY / escala 1:4

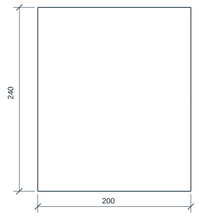

XZ / escala 1:1 / INTERRUMPIDA

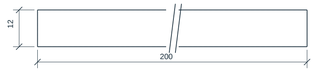

YZ / escala 1:1 / INTERRUMPIDA



CHAPA: espesor 12. Contorno nominal CAD; corte y taladros se identifican por coordenadas locales.
Sin taladros parametrizados adicionales. Contornos circulares en vistas y DXF.

Cotas en mm. Unidades y referencias locales X/Y/Z. Las vistas de detalle y DXF son proyecciones del CAD exacto OpenCascade; no se atribuye exportación nativa de SolidWorks a estas láminas.

Tolerancias ISO 2768-1 clase m en cotas lineales/angulares de piezas mecanizadas sin tolerancia individual. No se aplica a ajustes, soldaduras, equipos comerciales ni dimensiones de montaje críticas.

No escalar el PDF. Taladrar/escariar y desbarbar; eliminar aristas cortantes. Las preparaciones con luz 2 mm conservan geometría CAD; ejecutar soldadura únicamente según cuadro de juntas y WPS aplicable.

Acabados, ajustes y aceptación de uniones: según memoria, detalle específico y programa de inspección. Los espacios de verificación/aprobación permanecen sin firma.

Fuente: native_manifest.json + solidworks_model.bas; geometría y coordenadas íntegramente trazadas.

P05 - PLANOS DE DETALLE PARA REVISIÓN TÉCNICA

ESTACIÓN BIGBAG							**P05**
SESUVECA DEL PERÚ							
						DESPIECE DE FABRICACIÓN / COTAS LOCALES	
DIBUJ.	PROYECTO P05		16/10/2026				
VERIF.							
APROB.							
FABR.							
CALID.				MATERIAL: SEGÚN DESPIECE		**ESTACIÓN DE DESCARGA BIGBAG**	**A1**
PESO: BOM / CAD				ESCALA: INDICADA		**P05-T-006**	HOJA 6/51

DESPIECE DE FABRICACIÓN / COTAS LOCALES


Detalles 25..28 de 175 componentes fabricados. Proyecciones exactas de la geometría final.

P026 | CANT. 8


U01_CALCE_200x20x6_P05

ASTM A36 | ENVOLVENTE LOCAL X/Y/Z: 200 x 20 x 6

XY / escala 1:1 / INTERRUMPIDA

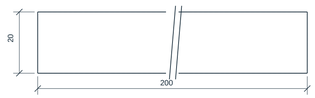

XZ / escala 1:1 / INTERRUMPIDA

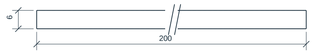

YZ / escala 2:1



CHAPA: espesor 6. Contorno nominal CAD; corte y taladros se identifican por coordenadas locales.
Sin taladros parametrizados adicionales. Contornos circulares en vistas y DXF.

P027 | CANT. 24

U01_RIGIDIZADOR_44x175x6_P05

ASTM A36 | ENVOLVENTE LOCAL X/Y/Z: 44 x 175 x 6

XY / escala 1:4



XZ / escala 2:1



YZ / escala 1:1 / INTERRUMPIDA



CHAPA: espesor 6. Contorno nominal CAD; corte y taladros se identifican por coordenadas locales.
Sin taladros parametrizados adicionales. Contornos circulares en vistas y DXF.

P028 | CANT. 8


U01_CARTELA_100x240x12_P05

ASTM A36 | ENVOLVENTE LOCAL X/Y/Z: 100 x 240 x 12


XY / escala 1:4



XZ / escala 1:1 / INTERRUMPIDA

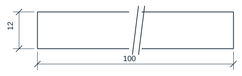

YZ / escala 1:1 / INTERRUMPIDA

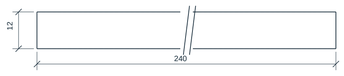


CHAPA: espesor 12. Contorno nominal CAD; corte y taladros se identifican por coordenadas locales.
Sin taladros parametrizados adicionales. Contornos circulares en vistas y DXF.

P029 | CANT. 4

P01_CAP_COLUMNA_200x200x12_P05

ASTM A36 | ENVOLVENTE LOCAL X/Y/Z: 200 x 200 x 12

XY / escala 1:4

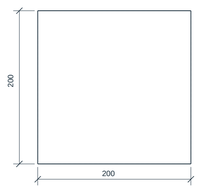

XZ / escala 1:1 / INTERRUMPIDA



YZ / escala 1:1 / INTERRUMPIDA



CHAPA: espesor 12. Contorno nominal CAD; corte y taladros se identifican por coordenadas locales.
Sin taladros parametrizados adicionales. Contornos circulares en vistas y DXF.

Cotas en mm. Unidades y referencias locales X/Y/Z. Las vistas de detalle y DXF son proyecciones del CAD exacto OpenCascade; no se atribuye exportación nativa de SolidWorks a estas láminas.

Tolerancias ISO 2768-1 clase m en cotas lineales/angulares de piezas mecanizadas sin tolerancia individual. No se aplica a ajustes, soldaduras, equipos comerciales ni dimensiones de montaje críticas.

No escalar el PDF. Taladrar/escariar y desbarbar; eliminar aristas cortantes. Las preparaciones con luz 2 mm conservan geometría CAD; ejecutar soldadura únicamente según cuadro de juntas y WPS aplicable.

Acabados, ajustes y aceptación de uniones: según memoria, detalle específico y programa de inspección. Los espacios de verificación/aprobación permanecen sin firma.

Fuente: native_manifest.json + solidworks_model.bas; geometría y coordenadas íntegramente trazadas.

P05 - PLANOS DE DETALLE PARA REVISIÓN TÉCNICA

ESTACIÓN BIGBAG							**P05**
SESUVECA DEL PERÚ							
						DESPIECE DE FABRICACIÓN / COTAS LOCALES	
DIBUJ.	PROYECTO P05		16/10/2026				
VERIF.							
APROB.							
FABR.							
CALID.				MATERIAL: SEGÚN DESPIECE		**ESTACIÓN DE DESCARGA BIGBAG**	**A1**
PESO: BOM / CAD				ESCALA: INDICADA		**P05-T-007**	HOJA 7/51

DESPIECE DE FABRICACIÓN / COTAS LOCALES


Detalles 29..32 de 175 componentes fabricados. Proyecciones exactas de la geometría final.

P030 | CANT. 8


U02_COLLAR_150x200x12_P05

ASTM A36 | ENVOLVENTE LOCAL X/Y/Z: 150 x 200 x 12


XY / escala 1:4

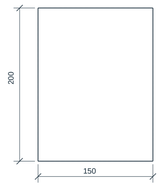

XZ / escala 1:1 / INTERRUMPIDA

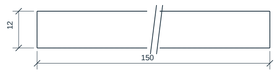

YZ / escala 1:1 / INTERRUMPIDA

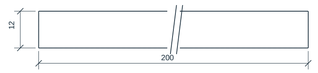


CHAPA: espesor 12. Contorno nominal CAD; corte y taladros se identifican por coordenadas locales.
Sin taladros parametrizados adicionales. Contornos circulares en vistas y DXF.

P031 | CANT. 8

U02_COLLAR_174x200x12_P05

ASTM A36 | ENVOLVENTE LOCAL X/Y/Z: 174 x 200 x 12


XY / escala 1:4

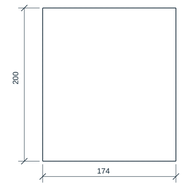

XZ / escala 1:1 / INTERRUMPIDA



YZ / escala 1:1 / INTERRUMPIDA

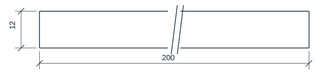


CHAPA: espesor 12. Contorno nominal CAD; corte y taladros se identifican por coordenadas locales.
Sin taladros parametrizados adicionales. Contornos circulares en vistas y DXF.

P032 | CANT. 4

U02_COLLAR_150x158x12_P05

ASTM A36 | ENVOLVENTE LOCAL X/Y/Z: 150 x 158 x 12

XY / escala 1:4

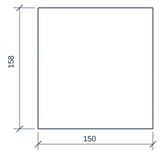

XZ / escala 1:1 / INTERRUMPIDA



YZ / escala 1:1 / INTERRUMPIDA




CHAPA: espesor 12. Contorno nominal CAD; corte y taladros se identifican por coordenadas locales.
Sin taladros parametrizados adicionales. Contornos circulares en vistas y DXF.

P033 | CANT. 4

U02_COLLAR_174x158x12_P05

ASTM A36 | ENVOLVENTE LOCAL X/Y/Z: 174 x 158 x 12

XY / escala 1:4

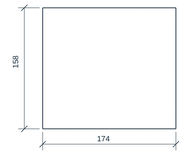

XZ / escala 1:1 / INTERRUMPIDA



YZ / escala 1:1 / INTERRUMPIDA



CHAPA: espesor 12. Contorno nominal CAD; corte y taladros se identifican por coordenadas locales.
Sin taladros parametrizados adicionales. Contornos circulares en vistas y DXF.

Cotas en mm. Unidades y referencias locales X/Y/Z. Las vistas de detalle y DXF son proyecciones del CAD exacto OpenCascade; no se atribuye exportación nativa de SolidWorks a estas láminas.

Tolerancias ISO 2768-1 clase m en cotas lineales/angulares de piezas mecanizadas sin tolerancia individual. No se aplica a ajustes, soldaduras, equipos comerciales ni dimensiones de montaje críticas.

No escalar el PDF. Taladrar/escariar y desbarbar; eliminar aristas cortantes. Las preparaciones con luz 2 mm conservan geometría CAD; ejecutar soldadura únicamente según cuadro de juntas y WPS aplicable.

Acabados, ajustes y aceptación de uniones: según memoria, detalle específico y programa de inspección. Los espacios de verificación/aprobación permanecen sin firma.

Fuente: native_manifest.json + solidworks_model.bas; geometría y coordenadas íntegramente trazadas.

ESTACIÓN BIGBAG							**P05**
SESUVECA DEL PERÚ							
						DESPIECE DE FABRICACIÓN / COTAS LOCALES	
DIBUJ.	PROYECTO P05		16/10/2026				
VERIF.							
APROB.							
FABR.							
CALID.				MATERIAL: SEGÚN DESPIECE		**ESTACIÓN DE DESCARGA BIGBAG**	**A1**
PESO: BOM / CAD				ESCALA: INDICADA		**P05-T-008**	HOJA 8/51

DESPIECE DE FABRICACIÓN / COTAS LOCALES


Detalles 33..36 de 175 componentes fabricados. Proyecciones exactas de la geometría final.

P034 | CANT. 1


U02_CARTELA_BRL-A--1_0_P05

ASTM A36 Fy250 | ENVOLVENTE LOCAL X/Y/Z: 250 x 250 x 18

XY / escala 1:4

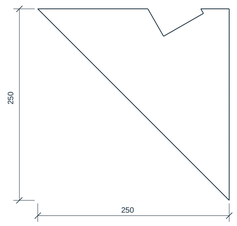

XZ / escala 1:2 / INTERRUMPIDA

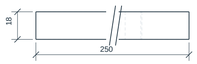

YZ / escala 1:2 / INTERRUMPIDA




CHAPA: espesor 18. Contorno nominal CAD; corte y taladros se identifican por coordenadas locales.
Sin taladros parametrizados adicionales. Contornos circulares en vistas y DXF.

P035 | CANT. 1


U02_CARTELA_BRL-A--1_1_P05

ASTM A36 Fy250 | ENVOLVENTE LOCAL X/Y/Z: 250 x 183 x 18


XY / escala 1:4

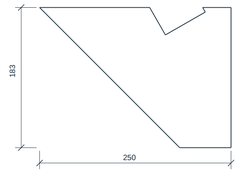

XZ / escala 1:2 / INTERRUMPIDA

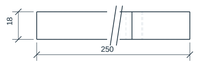

YZ / escala 1:1 / INTERRUMPIDA

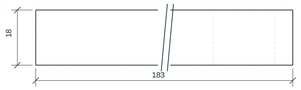


CHAPA: espesor 18. Contorno nominal CAD; corte y taladros se identifican por coordenadas locales.
Sin taladros parametrizados adicionales. Contornos circulares en vistas y DXF.

P036 | CANT. 1


U02_CARTELA_BRL-B--1_0_P05

ASTM A36 Fy250 | ENVOLVENTE LOCAL X/Y/Z: 250 x 183 x 18


XY / escala 1:4

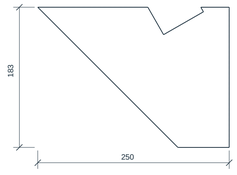

XZ / escala 1:2 / INTERRUMPIDA

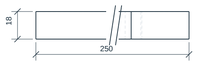

YZ / escala 1:1 / INTERRUMPIDA

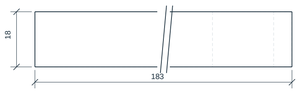


CHAPA: espesor 18. Contorno nominal CAD; corte y taladros se identifican por coordenadas locales.
Sin taladros parametrizados adicionales. Contornos circulares en vistas y DXF.

P037 | CANT. 1


U02_CARTELA_BRL-B--1_1_P05

ASTM A36 Fy250 | ENVOLVENTE LOCAL X/Y/Z: 250 x 250 x 18


XY / escala 1:4

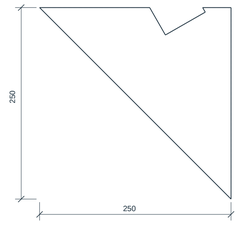

XZ / escala 1:2 / INTERRUMPIDA

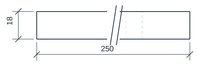

YZ / escala 1:2 / INTERRUMPIDA

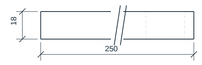

CHAPA: espesor 18. Contorno nominal CAD; corte y taladros se identifican por coordenadas locales.
Sin taladros parametrizados adicionales. Contornos circulares en vistas y DXF.

Cotas en mm. Unidades y referencias locales X/Y/Z. Las vistas de detalle y DXF son proyecciones del CAD exacto OpenCascade; no se atribuye exportación nativa de SolidWorks a estas láminas.

Tolerancias ISO 2768-1 clase m en cotas lineales/angulares de piezas mecanizadas sin tolerancia individual. No se aplica a ajustes, soldaduras, equipos comerciales ni dimensiones de montaje críticas.

No escalar el PDF. Taladrar/escariar y desbarbar; eliminar aristas cortantes. Las preparaciones con luz 2 mm conservan geometría CAD; ejecutar soldadura únicamente según cuadro de juntas y WPS aplicable.

Acabados, ajustes y aceptación de uniones: según memoria, detalle específico y programa de inspección. Los espacios de verificación/aprobación permanecen sin firma.

Fuente: native_manifest.json + solidworks_model.bas; geometría y coordenadas íntegramente trazadas.

P05 - PLANOS DE DETALLE PARA REVISIÓN TÉCNICA

ESTACIÓN BIGBAG							**P05**
SESUVECA DEL PERÚ							
						DESPIECE DE FABRICACIÓN / COTAS LOCALES	
DIBUJ.	PROYECTO P05		16/10/2026				
VERIF.							
APROB.							
FABR.							
CALID.				MATERIAL: SEGÚN DESPIECE		**ESTACIÓN DE DESCARGA BIGBAG**	**A1**
PESO: BOM / CAD				ESCALA: INDICADA		**P05-T-009**	HOJA 9/51

DESPIECE DE FABRICACIÓN / COTAS LOCALES


Detalles 37..40 de 175 componentes fabricados. Proyecciones exactas de la geometría final.

P038 | CANT. 1

U02_CARTELA_KNE--1_0_P05

ASTM A36 Fy250 | ENVOLVENTE LOCAL X/Y/Z: 250 x 250 x 18

XY / escala 1:4

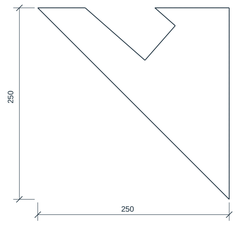

XZ / escala 1:2 / INTERRUMPIDA



YZ / escala 1:2 / INTERRUMPIDA




CHAPA: espesor 18. Contorno nominal CAD; corte y taladros se identifican por coordenadas locales.
Sin taladros parametrizados adicionales. Contornos circulares en vistas y DXF.

P039 | CANT. 1

U02_CARTELA_KNE--1_1_P05

ASTM A36 Fy250 | ENVOLVENTE LOCAL X/Y/Z: 250 x 250 x 18


XY / escala 1:4

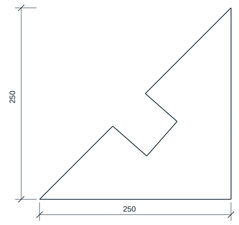

XZ / escala 1:2 / INTERRUMPIDA



YZ / escala 1:2 / INTERRUMPIDA

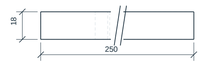


CHAPA: espesor 18. Contorno nominal CAD; corte y taladros se identifican por coordenadas locales.
Sin taladros parametrizados adicionales. Contornos circulares en vistas y DXF.

P040 | CANT. 1


U02_CARTELA_BRL-A-1_0_P05

ASTM A36 Fy250 | ENVOLVENTE LOCAL X/Y/Z: 250 x 250 x 18

XY / escala 1:4

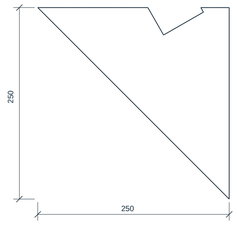

XZ / escala 1:2 / INTERRUMPIDA

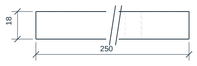

YZ / escala 1:2 / INTERRUMPIDA




CHAPA: espesor 18. Contorno nominal CAD; corte y taladros se identifican por coordenadas locales.
Sin taladros parametrizados adicionales. Contornos circulares en vistas y DXF.

P041 | CANT. 1


U02_CARTELA_BRL-A-1_1_P05

ASTM A36 Fy250 | ENVOLVENTE LOCAL X/Y/Z: 250 x 183 x 18


XY / escala 1:4

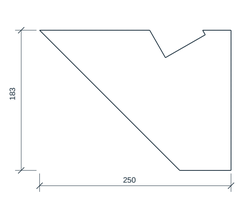

XZ / escala 1:2 / INTERRUMPIDA

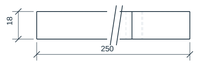

YZ / escala 1:1 / INTERRUMPIDA

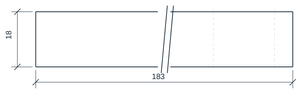

CHAPA: espesor 18. Contorno nominal CAD; corte y taladros se identifican por coordenadas locales.
Sin taladros parametrizados adicionales. Contornos circulares en vistas y DXF.

Cotas en mm. Unidades y referencias locales X/Y/Z. Las vistas de detalle y DXF son proyecciones del CAD exacto OpenCascade; no se atribuye exportación nativa de SolidWorks a estas láminas.

Tolerancias ISO 2768-1 clase m en cotas lineales/angulares de piezas mecanizadas sin tolerancia individual. No se aplica a ajustes, soldaduras, equipos comerciales ni dimensiones de montaje críticas.

No escalar el PDF. Taladrar/escariar y desbarbar; eliminar aristas cortantes. Las preparaciones con luz 2 mm conservan geometría CAD; ejecutar soldadura únicamente según cuadro de juntas y WPS aplicable.

Acabados, ajustes y aceptación de uniones: según memoria, detalle específico y programa de inspección. Los espacios de verificación/aprobación permanecen sin firma.

Fuente: native_manifest.json + solidworks_model.bas; geometría y coordenadas íntegramente trazadas.

P05 - PLANOS DE DETALLE PARA REVISIÓN TÉCNICA

ESTACIÓN BIGBAG							**P05**
SESUVECA DEL PERÚ							
						DESPIECE DE FABRICACIÓN / COTAS LOCALES	
DIBUJ.	PROYECTO P05		16/10/2026				
VERIF.							
APROB.							
FABR.							
CALID.				MATERIAL: SEGÚN DESPIECE		**ESTACIÓN DE DESCARGA BIGBAG**	**A1**
PESO: BOM / CAD				ESCALA: INDICADA		**P05-T-010**	HOJA 10/51

DESPIECE DE FABRICACIÓN / COTAS LOCALES


Detalles 41..44 de 175 componentes fabricados. Proyecciones exactas de la geometría final.

P042 | CANT. 1


U02_CARTELA_BRL-B-1_0_P05

ASTM A36 Fy250 | ENVOLVENTE LOCAL X/Y/Z: 250 x 183 x 18


XY / escala 1:4

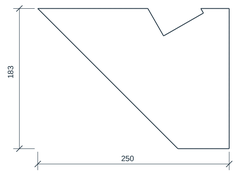

XZ / escala 1:2 / INTERRUMPIDA

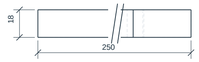

YZ / escala 1:1 / INTERRUMPIDA

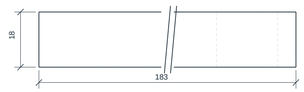


CHAPA: espesor 18. Contorno nominal CAD; corte y taladros se identifican por coordenadas locales.
Sin taladros parametrizados adicionales. Contornos circulares en vistas y DXF.

P043 | CANT. 1


U02_CARTELA_BRL-B-1_1_P05

ASTM A36 Fy250 | ENVOLVENTE LOCAL X/Y/Z: 250 x 250 x 18


XY / escala 1:4

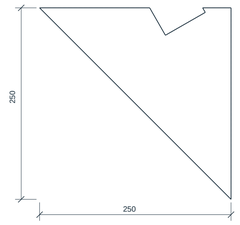

XZ / escala 1:2 / INTERRUMPIDA

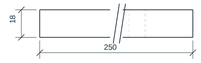

YZ / escala 1:2 / INTERRUMPIDA

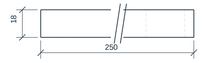


CHAPA: espesor 18. Contorno nominal CAD; corte y taladros se identifican por coordenadas locales.
Sin taladros parametrizados adicionales. Contornos circulares en vistas y DXF.

P044 | CANT. 1


U02_CARTELA_KNE-1_0_P05

ASTM A36 Fy250 | ENVOLVENTE LOCAL X/Y/Z: 250 x 250 x 18


XY / escala 1:4

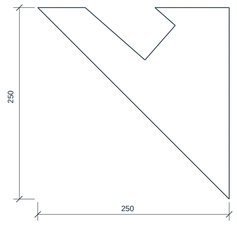

XZ / escala 1:2 / INTERRUMPIDA

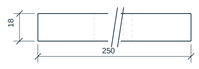

YZ / escala 1:2 / INTERRUMPIDA

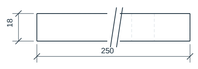


CHAPA: espesor 18. Contorno nominal CAD; corte y taladros se identifican por coordenadas locales.
Sin taladros parametrizados adicionales. Contornos circulares en vistas y DXF.

P045 | CANT. 1

U02_CARTELA_KNE-1_1_P05

ASTM A36 Fy250 | ENVOLVENTE LOCAL X/Y/Z: 250 x 250 x 18


XY / escala 1:4

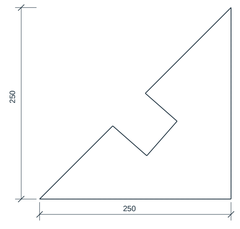

XZ / escala 1:2 / INTERRUMPIDA



YZ / escala 1:2 / INTERRUMPIDA

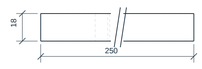

CHAPA: espesor 18. Contorno nominal CAD; corte y taladros se identifican por coordenadas locales.
Sin taladros parametrizados adicionales. Contornos circulares en vistas y DXF.

Cotas en mm. Unidades y referencias locales X/Y/Z. Las vistas de detalle y DXF son proyecciones del CAD exacto OpenCascade; no se atribuye exportación nativa de SolidWorks a estas láminas.

Tolerancias ISO 2768-1 clase m en cotas lineales/angulares de piezas mecanizadas sin tolerancia individual. No se aplica a ajustes, soldaduras, equipos comerciales ni dimensiones de montaje críticas.

No escalar el PDF. Taladrar/escariar y desbarbar; eliminar aristas cortantes. Las preparaciones con luz 2 mm conservan geometría CAD; ejecutar soldadura únicamente según cuadro de juntas y WPS aplicable.

Acabados, ajustes y aceptación de uniones: según memoria, detalle específico y programa de inspección. Los espacios de verificación/aprobación permanecen sin firma.

Fuente: native_manifest.json + solidworks_model.bas; geometría y coordenadas íntegramente trazadas.

P05 - PLANOS DE DETALLE PARA REVISIÓN TÉCNICA

ESTACIÓN BIGBAG							**P05**
SESUVECA DEL PERÚ							
						DESPIECE DE FABRICACIÓN / COTAS LOCALES	
DIBUJ.	PROYECTO P05		16/10/2026				
VERIF.							
APROB.							
FABR.							
CALID.				MATERIAL: SEGÚN DESPIECE		**ESTACIÓN DE DESCARGA BIGBAG**	**A1**
PESO: BOM / CAD				ESCALA: INDICADA		**P05-T-011**	HOJA 11/51

DESPIECE DE FABRICACIÓN / COTAS LOCALES


Detalles 45..48 de 175 componentes fabricados. Proyecciones exactas de la geometría final.

P046 | CANT. 4


U04_CAP_PATA_150x150x12_P05

ASTM A36 | ENVOLVENTE LOCAL X/Y/Z: 150 x 150 x 12


XY / escala 1:4

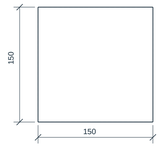

XZ / escala 1:1 / INTERRUMPIDA

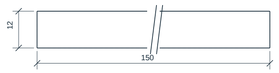

YZ / escala 1:1 / INTERRUMPIDA

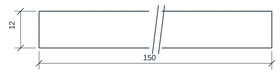


CHAPA: espesor 12. Contorno nominal CAD; corte y taladros se identifican por coordenadas locales.
Sin taladros parametrizados adicionales. Contornos circulares en vistas y DXF.

P047 | CANT. 8


U04_CARTELA_125x150x12_P05

ASTM A36 | ENVOLVENTE LOCAL X/Y/Z: 125 x 150 x 12

XY / escala 1:4

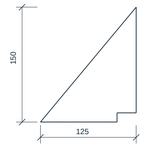

XZ / escala 1:1 / INTERRUMPIDA

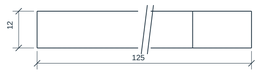

YZ / escala 1:1 / INTERRUMPIDA




CHAPA: espesor 12. Contorno nominal CAD; corte y taladros se identifican por coordenadas locales.
Sin taladros parametrizados adicionales. Contornos circulares en vistas y DXF.

P048 | CANT. 4

T01_ASIENTO_100x100x6_P05

ASTM A36 | ENVOLVENTE LOCAL X/Y/Z: 100 x 100 x 6

XY / escala 1:2

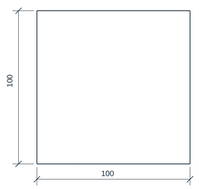

XZ / escala 1:1 / INTERRUMPIDA



YZ / escala 1:1 / INTERRUMPIDA




CHAPA: espesor 6. Contorno nominal CAD; corte y taladros se identifican por coordenadas locales.
Sin taladros parametrizados adicionales. Contornos circulares en vistas y DXF.

P049 | CANT. 4

T02_ASIENTO_INFERIOR_100x100x20_P05

ASTM A36 | ENVOLVENTE LOCAL X/Y/Z: 100 x 100 x 20

XY / escala 1:2

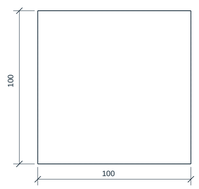

XZ / escala 1:2



YZ / escala 1:2



CHAPA: espesor 20. Contorno nominal CAD; corte y taladros se identifican por coordenadas locales.
Sin taladros parametrizados adicionales. Contornos circulares en vistas y DXF.

Cotas en mm. Unidades y referencias locales X/Y/Z. Las vistas de detalle y DXF son proyecciones del CAD exacto OpenCascade; no se atribuye exportación nativa de SolidWorks a estas láminas.

Tolerancias ISO 2768-1 clase m en cotas lineales/angulares de piezas mecanizadas sin tolerancia individual. No se aplica a ajustes, soldaduras, equipos comerciales ni dimensiones de montaje críticas.

No escalar el PDF. Taladrar/escariar y desbarbar; eliminar aristas cortantes. Las preparaciones con luz 2 mm conservan geometría CAD; ejecutar soldadura únicamente según cuadro de juntas y WPS aplicable.

Acabados, ajustes y aceptación de uniones: según memoria, detalle específico y programa de inspección. Los espacios de verificación/aprobación permanecen sin firma.

Fuente: native_manifest.json + solidworks_model.bas; geometría y coordenadas íntegramente trazadas.

P05 - PLANOS DE DETALLE PARA REVISIÓN TÉCNICA

ESTACIÓN BIGBAG							**P05**
SESUVECA DEL PERÚ							
						DESPIECE DE FABRICACIÓN / COTAS LOCALES	
DIBUJ.	PROYECTO P05		16/10/2026				
VERIF.							
APROB.							
FABR.							
CALID.				MATERIAL: SEGÚN DESPIECE		**ESTACIÓN DE DESCARGA BIGBAG**	**A1**
PESO: BOM / CAD				ESCALA: INDICADA		**P05-T-012**	HOJA 12/51

DESPIECE DE FABRICACIÓN / COTAS LOCALES


Detalles 49..52 de 175 componentes fabricados. Proyecciones exactas de la geometría final.

P050 | CANT. 4


T02_ASIENTO_SUPERIOR_200x214x20_P05

ASTM A36 | ENVOLVENTE LOCAL X/Y/Z: 200 x 214 x 20


XY / escala 1:4

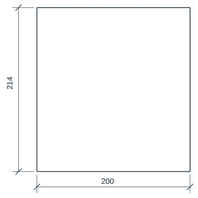

XZ / escala 1:1 / INTERRUMPIDA

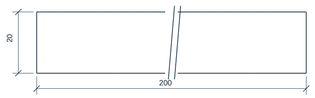

YZ / escala 1:1 / INTERRUMPIDA

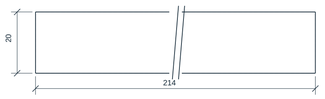


CHAPA: espesor 20. Contorno nominal CAD; corte y taladros se identifican por coordenadas locales.
Sin taladros parametrizados adicionales. Contornos circulares en vistas y DXF.

P051 | CANT. 1


OREJA_CENTRAL_150x220x20

ASTM A36 | ENVOLVENTE LOCAL X/Y/Z: 150 x 220 x 20


XY / escala 1:4

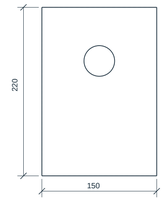

XZ / escala 1:1 / INTERRUMPIDA

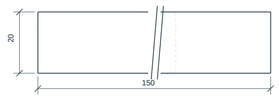

YZ / escala 1:1 / INTERRUMPIDA

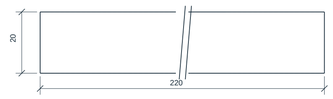


CHAPA: espesor 20. Contorno nominal CAD; corte y taladros se identifican por coordenadas locales.
TALADROS / EJES: ID - Ø - X - Y - Z - DIRECCIÓN (mm)
T1 / 40 / 0 / 150 / 0 / Z

P052 | CANT. 4


OREJA_EXTREMA_90x120x12

ASTM A36 | ENVOLVENTE LOCAL X/Y/Z: 90 x 120 x 12

XY / escala 1:2

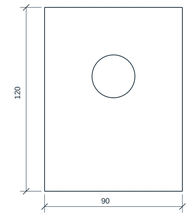

XZ / escala 1:1 / INTERRUMPIDA

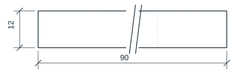

YZ / escala 1:1 / INTERRUMPIDA




CHAPA: espesor 12. Contorno nominal CAD; corte y taladros se identifican por coordenadas locales.
TALADROS / EJES: ID - Ø - X - Y - Z - DIRECCIÓN (mm)
T1 / 28 / 0 / 75 / 0 / Z

P053 | CANT. 4

CR_RESPALDO_EXTREMA_90x150x20_P05

ASTM A36 | ENVOLVENTE LOCAL X/Y/Z: 90 x 150 x 20


XY / escala 1:4

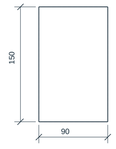

XZ / escala 1:1



YZ / escala 1:1 / INTERRUMPIDA

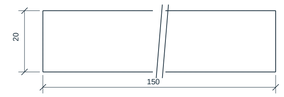

CHAPA: espesor 20. Contorno nominal CAD; corte y taladros se identifican por coordenadas locales.
Sin taladros parametrizados adicionales. Contornos circulares en vistas y DXF.

Cotas en mm. Unidades y referencias locales X/Y/Z. Las vistas de detalle y DXF son proyecciones del CAD exacto OpenCascade; no se atribuye exportación nativa de SolidWorks a estas láminas.

Tolerancias ISO 2768-1 clase m en cotas lineales/angulares de piezas mecanizadas sin tolerancia individual. No se aplica a ajustes, soldaduras, equipos comerciales ni dimensiones de montaje críticas.

No escalar el PDF. Taladrar/escariar y desbarbar; eliminar aristas cortantes. Las preparaciones con luz 2 mm conservan geometría CAD; ejecutar soldadura únicamente según cuadro de juntas y WPS aplicable.

Acabados, ajustes y aceptación de uniones: según memoria, detalle específico y programa de inspección. Los espacios de verificación/aprobación permanecen sin firma.

Fuente: native_manifest.json + solidworks_model.bas; geometría y coordenadas íntegramente trazadas.

P05 - PLANOS DE DETALLE PARA REVISIÓN TÉCNICA

ESTACIÓN BIGBAG							**P05**
SESUVECA DEL PERÚ				SESUVECA DEL PERÚ			
						DESPIECE DE FABRICACIÓN / COTAS LOCALES	
DIBUJ.	PROYECTO P05		16/10/2026				
VERIF.							
APROB.							
FABR.							
CALID.				MATERIAL: SEGÚN DESPIECE		**ESTACIÓN DE DESCARGA BIGBAG**	**A1**
PESO: BOM / CAD				ESCALA: INDICADA		**P05-T-013**	HOJA 13/51

DESPIECE DE FABRICACIÓN / COTAS LOCALES


Detalles 53..56 de 175 componentes fabricados. Proyecciones exactas de la geometría final.

P054 | CANT. 8


CR_CARTELA_TRIANGULAR_150x150x12_P05

ASTM A36 | ENVOLVENTE LOCAL X/Y/Z: 150 x 150 x 12


XY / escala 1:4

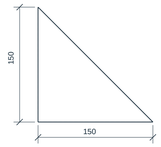

XZ / escala 1:1 / INTERRUMPIDA

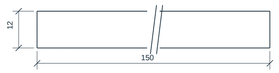

YZ / escala 1:1 / INTERRUMPIDA

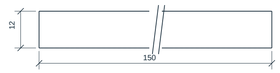

CHAPA: espesor 12. Contorno nominal CAD; corte y taladros se identifican por coordenadas locales.
Sin taladros parametrizados adicionales. Contornos circulares en vistas y DXF.

P055 | CANT. 1

CR_CAP_CENTRAL_150x300x30_P05

ASTM A36 | ENVOLVENTE LOCAL X/Y/Z: 150 x 300 x 30


XY / escala 1:5



XZ / escala 1:2



YZ / escala 1:2 / INTERRUMPIDA

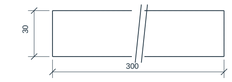

CHAPA: espesor 30. Contorno nominal CAD; corte y taladros se identifican por coordenadas locales.
Sin taladros parametrizados adicionales. Contornos circulares en vistas y DXF.

P056 | CANT. 2

CR_CHEEK_300x150x20_P05

ASTM A36 | ENVOLVENTE LOCAL X/Y/Z: 300 x 150 x 20


XY / escala 1:4



XZ / escala 1:2 / INTERRUMPIDA



YZ / escala 1:1 / INTERRUMPIDA

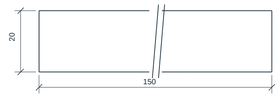


CHAPA: espesor 20. Contorno nominal CAD; corte y taladros se identifican por coordenadas locales.
Sin taladros parametrizados adicionales. Contornos circulares en vistas y DXF.

P057 | CANT. 4

LINER_CONO_UHMW10_P05

UHMWPE disipativo | ENVOLVENTE LOCAL X/Y/Z: 1673.09 x 1405.77 x 10

XY / escala 1:20

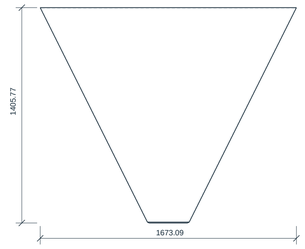

XZ / escala 1:5 / INTERRUMPIDA



YZ / escala 1:4 / INTERRUMPIDA



CHAPA: espesor 10. Contorno nominal CAD; corte y taladros se identifican por coordenadas locales.
Sin taladros parametrizados adicionales. Contornos circulares en vistas y DXF.

Cotas en mm. Unidades y referencias locales X/Y/Z. Las vistas de detalle y DXF son proyecciones del CAD exacto OpenCascade; no se atribuye exportación nativa de SolidWorks a estas láminas.

Tolerancias ISO 2768-1 clase m en cotas lineales/angulares de piezas mecanizadas sin tolerancia individual. No se aplica a ajustes, soldaduras, equipos comerciales ni dimensiones de montaje críticas.

No escalar el PDF. Taladrar/escariar y desbarbar; eliminar aristas cortantes. Las preparaciones con luz 2 mm conservan geometría CAD; ejecutar soldadura únicamente según cuadro de juntas y WPS aplicable.

Acabados, ajustes y aceptación de uniones: según memoria, detalle específico y programa de inspección. Los espacios de verificación/aprobación permanecen sin firma.

Fuente: native_manifest.json + solidworks_model.bas; geometría y coordenadas íntegramente trazadas.

P05 - PLANOS DE DETALLE PARA REVISIÓN TÉCNICA

ESTACIÓN BIGBAG							**P05**
SESUVECA DEL PERÚ							
						DESPIECE DE FABRICACIÓN / COTAS LOCALES	
DIBUJ.	PROYECTO P05		16/10/2026				
VERIF.							
APROB.							
FABR.							
CALID.				MATERIAL: SEGÚN DESPIECE		**ESTACIÓN DE DESCARGA BIGBAG**	**A1**
PESO: BOM / CAD				ESCALA: INDICADA		**P05-T-014**	HOJA 14/51

DESPIECE DE FABRICACIÓN / COTAS LOCALES

Detalles 57..60 de 175 componentes fabricados. Proyecciones exactas de la geometría final.

P058 | CANT. 3

LINER_CUERPO_UHMW10_P05

UHMWPE disipativo | ENVOLVENTE LOCAL X/Y/Z: 1670 x 470.15 x 10

XY / escala 1:20



XZ / escala 1:5 / INTERRUMPIDA



YZ / escala 1:2 / INTERRUMPIDA



CHAPA: espesor 10. Contorno nominal CAD; corte y taladros se identifican por coordenadas locales.
Sin taladros parametrizados adicionales. Contornos circulares en vistas y DXF.

P059 | CANT. 1

LINER_CUERPO_UHMW10_DN150_P05

UHMWPE disipativo | ENVOLVENTE LOCAL X/Y/Z: 1670 x 470.15 x 10

XY / escala 1:20



XZ / escala 1:5 / INTERRUMPIDA



YZ / escala 1:2 / INTERRUMPIDA




CHAPA: espesor 10. Contorno nominal CAD; corte y taladros se identifican por coordenadas locales.
Sin taladros parametrizados adicionales. Contornos circulares en vistas y DXF.

P060 | CANT. 1


CORTE_ALETA_1_304_t16_P05

AISI304 | ENVOLVENTE LOCAL X/Y/Z: 149 x 204 x 16


XY / escala 1:4

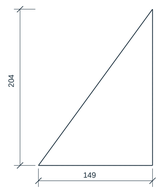

XZ / escala 1:1 / INTERRUMPIDA

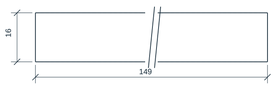

YZ / escala 1:1 / INTERRUMPIDA

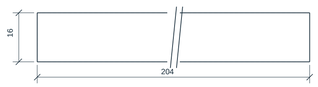


CHAPA: espesor 16. Contorno nominal CAD; corte y taladros se identifican por coordenadas locales.
Sin taladros parametrizados adicionales. Contornos circulares en vistas y DXF.

P061 | CANT. 1


CORTE_ALETA_2_304_t16_P05

AISI304 | ENVOLVENTE LOCAL X/Y/Z: 149 x 204 x 16

XY / escala 1:4

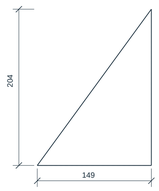

XZ / escala 1:1 / INTERRUMPIDA

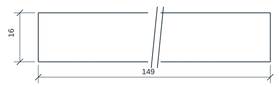

YZ / escala 1:1 / INTERRUMPIDA



CHAPA: espesor 16. Contorno nominal CAD; corte y taladros se identifican por coordenadas locales.
Sin taladros parametrizados adicionales. Contornos circulares en vistas y DXF.

Cotas en mm. Unidades y referencias locales X/Y/Z. Las vistas de detalle y DXF son proyecciones del CAD exacto OpenCascade; no se atribuye exportación nativa de SolidWorks a estas láminas.

Tolerancias ISO 2768-1 clase m en cotas lineales/angulares de piezas mecanizadas sin tolerancia individual. No se aplica a ajustes, soldaduras, equipos comerciales ni dimensiones de montaje críticas.

No escalar el PDF. Taladrar/escariar y desbarbar; eliminar aristas cortantes. Las preparaciones con luz 2 mm conservan geometría CAD; ejecutar soldadura únicamente según cuadro de juntas y WPS aplicable.

Acabados, ajustes y aceptación de uniones: según memoria, detalle específico y programa de inspección. Los espacios de verificación/aprobación permanecen sin firma.

Fuente: native_manifest.json + solidworks_model.bas; geometría y coordenadas íntegramente trazadas.

ESTACIÓN BIGBAG							P05
SESUVECA DEL PERÚ							
						DESPIECE DE FABRICACIÓN / COTAS LOCALES	
DIBUJ.	PROYECTO P05		16/10/2026				
VERIF.							
APROB.							
FABR.							
CALID.				MATERIAL: SEGÚN DESPIECE		ESTACIÓN DE DESCARGA BIGBAG	A1
PESO: BOM / CAD				ESCALA: INDICADA		P05-T-015	HOJA 15/51

DESPIECE DE FABRICACIÓN / COTAS LOCALES


Detalles 61..64 de 175 componentes fabricados. Proyecciones exactas de la geometría final.

P062 | CANT. 1


CORTE_ALETA_3_304_t16_P05

AISI304 | ENVOLVENTE LOCAL X/Y/Z: 174 x 204 x 16


XY / escala 1:4

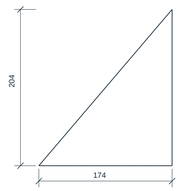

XZ / escala 1:1 / INTERRUMPIDA

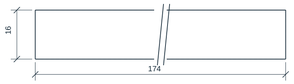

YZ / escala 1:1 / INTERRUMPIDA

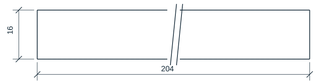


CHAPA: espesor 16. Contorno nominal CAD; corte y taladros se identifican por coordenadas locales.
Sin taladros parametrizados adicionales. Contornos circulares en vistas y DXF.

P063 | CANT. 1

CORTE_ALETA_4_304_t16_P05

AISI304 | ENVOLVENTE LOCAL X/Y/Z: 174 x 204 x 16

XY / escala 1:4

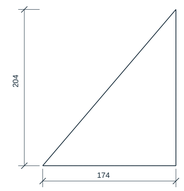

XZ / escala 1:1 / INTERRUMPIDA



YZ / escala 1:1 / INTERRUMPIDA




CHAPA: espesor 16. Contorno nominal CAD; corte y taladros se identifican por coordenadas locales.
Sin taladros parametrizados adicionales. Contornos circulares en vistas y DXF.

P064 | CANT. 1


CORTE_MASTIL_60p3x5_P05

AISI304 | ENVOLVENTE LOCAL X/Y/Z: 60.3 x 60.3 x 204


XY / escala 1:1

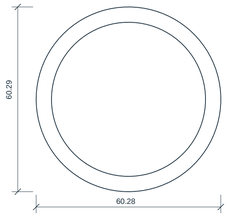

XZ / escala 1:4

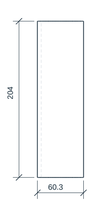

YZ / escala 1:4

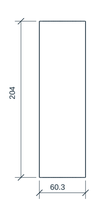


TORNEADO / TUBO: exterior Ø60.3, pared 5, longitud 204.
Sin taladros parametrizados adicionales. Contornos circulares en vistas y DXF.

P065 | CANT. 1

CORTE_MARCO_570x620x12_P05

AISI 304 | ENVOLVENTE LOCAL X/Y/Z: 570 x 620 x 12

XY / escala 1:10

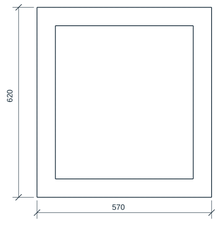

XZ / escala 1:2 / INTERRUMPIDA



YZ / escala 1:2 / INTERRUMPIDA



CHAPA: espesor 12. Contorno nominal CAD; corte y taladros se identifican por coordenadas locales.
Sin taladros parametrizados adicionales. Contornos circulares en vistas y DXF.

Cotas en mm. Unidades y referencias locales X/Y/Z. Las vistas de detalle y DXF son proyecciones del CAD exacto OpenCascade; no se atribuye exportación nativa de SolidWorks a estas láminas.

Tolerancias ISO 2768-1 clase m en cotas lineales/angulares de piezas mecanizadas sin tolerancia individual. No se aplica a ajustes, soldaduras, equipos comerciales ni dimensiones de montaje críticas.

No escalar el PDF. Taladrar/escariar y desbarbar; eliminar aristas cortantes. Las preparaciones con luz 2 mm conservan geometría CAD; ejecutar soldadura únicamente según cuadro de juntas y WPS aplicable.

Acabados, ajustes y aceptación de uniones: según memoria, detalle específico y programa de inspección. Los espacios de verificación/aprobación permanecen sin firma.

Fuente: native_manifest.json + solidworks_model.bas; geometría y coordenadas íntegramente trazadas.

P05 - PLANOS DE DETALLE PARA REVISIÓN TÉCNICA

ESTACIÓN BIGBAG						**P05**
SESUVECA DEL PERÚ						
						DESPIECE DE FABRICACIÓN / COTAS LOCALES
DIBUJ.	PROYECTO P05		16/10/2026			
VERIF.						
APROB.						
FABR.						
CALID.				MATERIAL: SEGÚN DESPIECE		**ESTACIÓN DE DESCARGA BIGBAG** / **A1**
PESO: BOM / CAD				ESCALA: INDICADA		**P05-T-016** / HOJA 16/51

DESPIECE DE FABRICACIÓN / COTAS LOCALES


Detalles 65..68 de 175 componentes fabricados. Proyecciones exactas de la geometría final.

P066 | CANT. 1


CORTE_BASE_200x200x16_P05

AISI 304 | ENVOLVENTE LOCAL X/Y/Z: 200 x 200 x 16


XY / escala 1:4

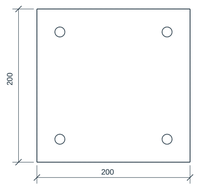

XZ / escala 1:1 / INTERRUMPIDA

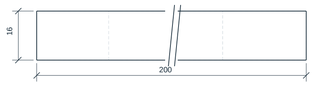

YZ / escala 1:1 / INTERRUMPIDA

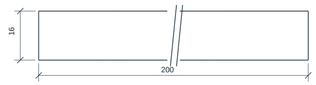


CHAPA: espesor 16. Contorno nominal CAD; corte y taladros se identifican por coordenadas locales.
TALADROS / EJES: ID - Ø - X - Y - Z - DIRECCIÓN (mm)
T1 / 13 / -70 / -70 / 0 / Z
T2 / 13 / 70 / -70 / 0 / Z
T3 / 13 / -70 / 70 / 0 / Z
T4 / 13 / 70 / 70 / 0 / Z

P072 | CANT. 1

MG02_FLANGE_364x350x6_P05

ASTM A36 | ENVOLVENTE LOCAL X/Y/Z: 364 x 350 x 6

XY / escala 1:5

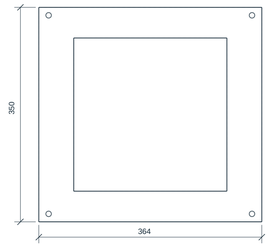

XZ / escala 1:2 / INTERRUMPIDA



YZ / escala 1:2 / INTERRUMPIDA




CHAPA: espesor 6. Contorno nominal CAD; corte y taladros se identifican por coordenadas locales.
TALADROS / EJES: ID - Ø - X - Y - Z - DIRECCIÓN (mm)
T1 / 9 / -166 / -162 / 0 / Z
T2 / 9 / 166 / -162 / 0 / Z
T3 / 9 / -166 / 162 / 0 / Z
T4 / 9 / 166 / 162 / 0 / Z

P073 | CANT. 1

MG03_FLANGE_364x350x6_P05

ASTM A36 | ENVOLVENTE LOCAL X/Y/Z: 364 x 350 x 6

XY / escala 1:5

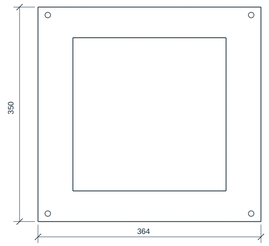

XZ / escala 1:2 / INTERRUMPIDA



YZ / escala 1:2 / INTERRUMPIDA




CHAPA: espesor 6. Contorno nominal CAD; corte y taladros se identifican por coordenadas locales.
TALADROS / EJES: ID - Ø - X - Y - Z - DIRECCIÓN (mm)
T1 / 9 / -166 / -162 / 0 / Z
T2 / 9 / 166 / -162 / 0 / Z
T3 / 9 / -166 / 162 / 0 / Z
T4 / 9 / 166 / 162 / 0 / Z

P074 | CANT. 1

MG01_HOJA_310x450x6_P05

ASTM A36 | ENVOLVENTE LOCAL X/Y/Z: 310 x 450 x 6

XY / escala 1:10

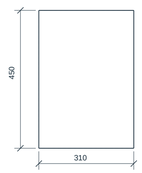

XZ / escala 1:2 / INTERRUMPIDA



YZ / escala 1:2 / INTERRUMPIDA



CHAPA: espesor 6. Contorno nominal CAD; corte y taladros se identifican por coordenadas locales.
Sin taladros parametrizados adicionales. Contornos circulares en vistas y DXF.

Cotas en mm. Unidades y referencias locales X/Y/Z. Las vistas de detalle y DXF son proyecciones del CAD exacto OpenCascade; no se atribuye exportación nativa de SolidWorks a estas láminas.

Tolerancias ISO 2768-1 clase m en cotas lineales/angulares de piezas mecanizadas sin tolerancia individual. No se aplica a ajustes, soldaduras, equipos comerciales ni dimensiones de montaje críticas.

No escalar el PDF. Taladrar/escariar y desbarbar; eliminar aristas cortantes. Las preparaciones con luz 2 mm conservan geometría CAD; ejecutar soldadura únicamente según cuadro de juntas y WPS aplicable.

Acabados, ajustes y aceptación de uniones: según memoria, detalle específico y programa de inspección. Los espacios de verificación/aprobación permanecen sin firma.

Fuente: native_manifest.json + solidworks_model.bas; geometría y coordenadas íntegramente trazadas.

P05 - PLANOS DE DETALLE PARA REVISIÓN TÉCNICA

ESTACIÓN BIGBAG						**P05**
SESUVECA DEL PERÚ				SESUVECA DEL PERÚ		
						DESPIECE DE FABRICACIÓN / COTAS LOCALES
DIBUJ.	PROYECTO P05		16/10/2026			
VERIF.						
APROB.						
FABR.						
CALID.				MATERIAL: SEGÚN DESPIECE		**ESTACIÓN DE DESCARGA BIGBAG** — **A1**
PESO: BOM / CAD				ESCALA: INDICADA		**P05-T-017** — HOJA 17/51

DESPIECE DE FABRICACIÓN / COTAS LOCALES

Detalles 69..72 de 175 componentes fabricados. Proyecciones exactas de la geometría final.

P075 | CANT. 1

MG04_SUP_1_P05

ASTM A36 | ENVOLVENTE LOCAL X/Y/Z: 44 x 455 x 6

XY / escala 1:4 / INTERRUMPIDA



XZ / escala 2:1



YZ / escala 1:2 / INTERRUMPIDA



CHAPA: espesor 6. Contorno nominal CAD; corte y taladros se identifican por coordenadas locales.
TALADROS / EJES: ID - Ø - X - Y - Z - DIRECCIÓN (mm)
T1 / 9 / 6 / -17.5 / 0 / Z
T2 / 9 / 6 / 212.5 / 0 / Z

P076 | CANT. 1

MG04_SUP_2_P05

ASTM A36 | ENVOLVENTE LOCAL X/Y/Z: 44 x 455 x 6

XY / escala 1:4 / INTERRUMPIDA



XZ / escala 2:1



YZ / escala 1:2 / INTERRUMPIDA



CHAPA: espesor 6. Contorno nominal CAD; corte y taladros se identifican por coordenadas locales.
TALADROS / EJES: ID - Ø - X - Y - Z - DIRECCIÓN (mm)
T1 / 9 / -6 / -17.5 / 0 / Z
T2 / 9 / -6 / 212.5 / 0 / Z

P077 | CANT. 1

MG05_INF_1_P05

ASTM A36 | ENVOLVENTE LOCAL X/Y/Z: 44 x 455 x 6

XY / escala 1:4 / INTERRUMPIDA



XZ / escala 2:1



YZ / escala 1:2 / INTERRUMPIDA



CHAPA: espesor 6. Contorno nominal CAD; corte y taladros se identifican por coordenadas locales.
TALADROS / EJES: ID - Ø - X - Y - Z - DIRECCIÓN (mm)
T1 / 9 / 6 / -17.5 / 0 / Z
T2 / 9 / 6 / 212.5 / 0 / Z

P078 | CANT. 1

MG05_INF_2_P05

ASTM A36 | ENVOLVENTE LOCAL X/Y/Z: 44 x 455 x 6

XY / escala 1:4 / INTERRUMPIDA



XZ / escala 2:1



YZ / escala 1:2 / INTERRUMPIDA



CHAPA: espesor 6. Contorno nominal CAD; corte y taladros se identifican por coordenadas locales.
TALADROS / EJES: ID - Ø - X - Y - Z - DIRECCIÓN (mm)
T1 / 9 / -6 / -17.5 / 0 / Z
T2 / 9 / -6 / 212.5 / 0 / Z

Cotas en mm. Unidades y referencias locales X/Y/Z. Las vistas de detalle y DXF son proyecciones del CAD exacto OpenCascade; no se atribuye exportación nativa de SolidWorks a estas láminas.

Tolerancias ISO 2768-1 clase m en cotas lineales/angulares de piezas mecanizadas sin tolerancia individual. No se aplica a ajustes, soldaduras, equipos comerciales ni dimensiones de montaje críticas.

No escalar el PDF. Taladrar/escariar y desbarbar; eliminar aristas cortantes. Las preparaciones con luz 2 mm conservan geometría CAD; ejecutar soldadura únicamente según cuadro de juntas y WPS aplicable.

Acabados, ajustes y aceptación de uniones: según memoria, detalle específico y programa de inspección. Los espacios de verificación/aprobación permanecen sin firma.

Fuente: native_manifest.json + solidworks_model.bas; geometría y coordenadas íntegramente trazadas.

P05 - PLANOS DE DETALLE PARA REVISIÓN TÉCNICA

ESTACIÓN BIGBAG						**P05**
SESUVECA DEL PERÚ						
						DESPIECE DE FABRICACIÓN / COTAS LOCALES
DIBUJ.	PROYECTO P05		16/10/2026			
VERIF.						
APROB.						
FABR.						
CALID.				MATERIAL: SEGÚN DESPIECE		**ESTACIÓN DE DESCARGA BIGBAG** / **A1**
PESO: BOM / CAD				ESCALA: INDICADA		**P05-T-018** / HOJA 18/51

DESPIECE DE FABRICACIÓN / COTAS LOCALES

Detalles 73..76 de 175 componentes fabricados. Proyecciones exactas de la geometría final.

P079 | CANT. 1

MG06_ESP_1_P05

ASTM A36 | ENVOLVENTE LOCAL X/Y/Z: 6 x 800 x 31.5


XY / escala 1:4 / INTERRUMPIDA



XZ / escala 2:1



YZ / escala 1:4 / INTERRUMPIDA

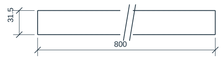

CHAPA: espesor 31.5. Contorno nominal CAD; corte y taladros se identifican por coordenadas locales.
Sin taladros parametrizados adicionales. Contornos circulares en vistas y DXF.

P080 | CANT. 1

MG06_ESP_2_P05

ASTM A36 | ENVOLVENTE LOCAL X/Y/Z: 6 x 800 x 31.5


XY / escala 1:4 / INTERRUMPIDA



XZ / escala 2:1



YZ / escala 1:4 / INTERRUMPIDA

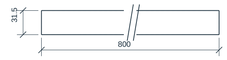


CHAPA: espesor 31.5. Contorno nominal CAD; corte y taladros se identifican por coordenadas locales.
Sin taladros parametrizados adicionales. Contornos circulares en vistas y DXF.

P087 | CANT. 8

MG10_CASQUILLO_12x9_L31p5_P05

ACERO | ENVOLVENTE LOCAL X/Y/Z: 12 x 12 x 31.5

XY / escala 5:1

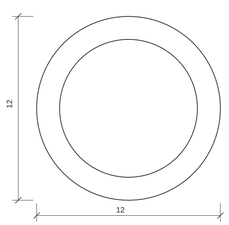

XZ / escala 2:1



YZ / escala 2:1




TORNEADO / TUBO: exterior Ø12, pared 1.5, longitud 31.5.
Sin taladros parametrizados adicionales. Contornos circulares en vistas y DXF.

P088 | CANT. 1


MS01_TRANSICION_CUADRADO_REDONDO_3_P05

ASTM A36 | ENVOLVENTE LOCAL X/Y/Z: 256 x 256 x 80

XY / escala 1:4

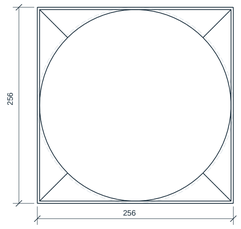

XZ / escala 1:4

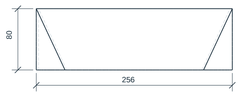

YZ / escala 1:4



CHAPA: espesor 3. Contorno nominal CAD; corte y taladros se identifican por coordenadas locales.
Sin taladros parametrizados adicionales. Contornos circulares en vistas y DXF.

Cotas en mm. Unidades y referencias locales X/Y/Z. Las vistas de detalle y DXF son proyecciones del CAD exacto OpenCascade; no se atribuye exportación nativa de SolidWorks a estas láminas.

Tolerancias ISO 2768-1 clase m en cotas lineales/angulares de piezas mecanizadas sin tolerancia individual. No se aplica a ajustes, soldaduras, equipos comerciales ni dimensiones de montaje críticas.

No escalar el PDF. Taladrar/escariar y desbarbar; eliminar aristas cortantes. Las preparaciones con luz 2 mm conservan geometría CAD; ejecutar soldadura únicamente según cuadro de juntas y WPS aplicable.

Acabados, ajustes y aceptación de uniones: según memoria, detalle específico y programa de inspección. Los espacios de verificación/aprobación permanecen sin firma.

Fuente: native_manifest.json + solidworks_model.bas; geometría y coordenadas íntegramente trazadas.

P05 - PLANOS DE DETALLE PARA REVISIÓN TÉCNICA

ESTACIÓN BIGBAG						**P05**
SESUVECA DEL PERÚ						
						DESPIECE DE FABRICACIÓN / COTAS LOCALES
DIBUJ.	PROYECTO P05		16/10/2026			
VERIF.						
APROB.						
FABR.						
CALID.				MATERIAL: SEGÚN DESPIECE		**ESTACIÓN DE DESCARGA BIGBAG** / **A1**
PESO: BOM / CAD				ESCALA: INDICADA		**P05-T-019** / HOJA 19/51

DESPIECE DE FABRICACIÓN / COTAS LOCALES


Detalles 77..80 de 175 componentes fabricados. Proyecciones exactas de la geometría final.

P089 | CANT. 1

MS02_CUELLO_ID250_OD256_L80_P05

ACERO | ENVOLVENTE LOCAL X/Y/Z: 256 x 256 x 80

XY / escala 1:4

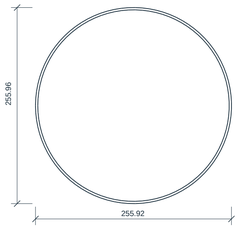

XZ / escala 1:4



YZ / escala 1:4




TORNEADO / TUBO: exterior Ø256, pared 3, longitud 80.
Sin taladros parametrizados adicionales. Contornos circulares en vistas y DXF.

P090 | CANT. 2


MS03_SECTOR_170deg_ID268_t3_H40_P05

ASTM A36 | ENVOLVENTE LOCAL X/Y/Z: 271.92 x 137 x 40

XY / escala 1:4

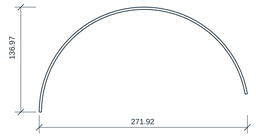

XZ / escala 1:2 / INTERRUMPIDA

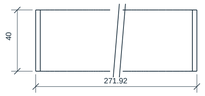

YZ / escala 1:2




CHAPA: espesor 3. Contorno nominal CAD; corte y taladros se identifican por coordenadas locales.
Sin taladros parametrizados adicionales. Contornos circulares en vistas y DXF.

P092 | CANT. 2


MS05_SOPORTE_60x80x6_P05

ASTM A36 | ENVOLVENTE LOCAL X/Y/Z: 60 x 80 x 6


XY / escala 1:2

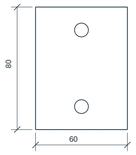

XZ / escala 1:1 / INTERRUMPIDA

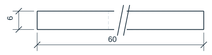

YZ / escala 1:1 / INTERRUMPIDA

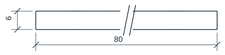

CHAPA: espesor 6. Contorno nominal CAD; corte y taladros se identifican por coordenadas locales.
TALADROS / EJES: ID - Ø - X - Y - Z - DIRECCIÓN (mm)
T1 / 9 / 0 / -25 / 0 / Z
T2 / 9 / 0 / 25 / 0 / Z

P095 | CANT. 1


MG11_GUARDA_U_590x645x260_R3_t2_P05

ASTM A36 | ENVOLVENTE LOCAL X/Y/Z: 590 x 260 x 645

XY / escala 1:10



XZ / escala 1:10

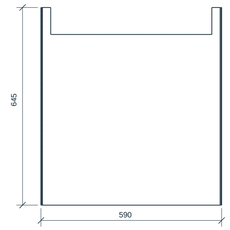

YZ / escala 1:10



CHAPA: espesor 2. Contorno nominal CAD; corte y taladros se identifican por coordenadas locales.
Sin taladros parametrizados adicionales. Contornos circulares en vistas y DXF.

Cotas en mm. Unidades y referencias locales X/Y/Z. Las vistas de detalle y DXF son proyecciones del CAD exacto OpenCascade; no se atribuye exportación nativa de SolidWorks a estas láminas.

Tolerancias ISO 2768-1 clase m en cotas lineales/angulares de piezas mecanizadas sin tolerancia individual. No se aplica a ajustes, soldaduras, equipos comerciales ni dimensiones de montaje críticas.

No escalar el PDF. Taladrar/escariar y desbarbar; eliminar aristas cortantes. Las preparaciones con luz 2 mm conservan geometría CAD; ejecutar soldadura únicamente según cuadro de juntas y WPS aplicable.

Acabados, ajustes y aceptación de uniones: según memoria, detalle específico y programa de inspección. Los espacios de verificación/aprobación permanecen sin firma.

Fuente: native_manifest.json + solidworks_model.bas; geometría y coordenadas íntegramente trazadas.

ESTACIÓN BIGBAG						**P05**
SESUVECA DEL PERÚ						
						DESPIECE DE FABRICACIÓN / COTAS LOCALES
DIBUJ.	PROYECTO P05		16/10/2026			
VERIF.						
APROB.						
FABR.						
CALID.				MATERIAL: SEGÚN DESPIECE		**ESTACIÓN DE DESCARGA BIGBAG**
PESO: BOM / CAD				ESCALA: INDICADA		**P05-T-020**
						HOJA 20/51

DESPIECE DE FABRICACIÓN / COTAS LOCALES


Detalles 81..84 de 175 componentes fabricados. Proyecciones exactas de la geometría final.

P096 | CANT. 1

MG12_GUARDA_FONDO_590x645x2_P05

ASTM A36 | ENVOLVENTE LOCAL X/Y/Z: 590 x 645 x 2

XY / escala 1:10

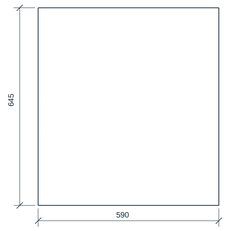

XZ / escala 1:2 / INTERRUMPIDA



YZ / escala 1:2 / INTERRUMPIDA



CHAPA: espesor 2. Contorno nominal CAD; corte y taladros se identifican por coordenadas locales.
Sin taladros parametrizados adicionales. Contornos circulares en vistas y DXF.

P097 | CANT. 1

MG13_GUARDA_TESTERO_586x258x2_P05

ASTM A36 | ENVOLVENTE LOCAL X/Y/Z: 586 x 258 x 2

XY / escala 1:10



XZ / escala 1:2 / INTERRUMPIDA



YZ / escala 1:2 / INTERRUMPIDA




CHAPA: espesor 2. Contorno nominal CAD; corte y taladros se identifican por coordenadas locales.
Sin taladros parametrizados adicionales. Contornos circulares en vistas y DXF.

P099 | CANT. 1


BASE_COMBINADA_PORTICO_TOLVA_SUR_t35_P05

A36 | ENVOLVENTE LOCAL X/Y/Z: 555 x 480 x 35


XY / escala 1:10

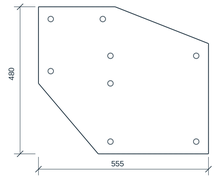

XZ / escala 1:2 / INTERRUMPIDA

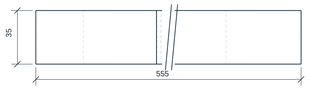

YZ / escala 1:2 / INTERRUMPIDA

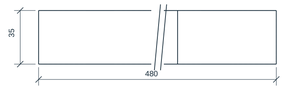


CHAPA: espesor 35. Contorno nominal CAD; corte y taladros se identifican por coordenadas locales.
TALADROS / EJES: ID - Ø - X - Y - Z - DIRECCIÓN (mm)
T1 / 18 / -140 / -140 / 0 / Z
T2 / 18 / -140 / 140 / 0 / Z
T3 / 18 / 140 / -140 / 0 / Z
T4 / 18 / 140 / 140 / 0 / Z
T5 / 18 / 140 / 50 / 0 / Z
T6 / 18 / 165 / 260 / 0 / Z
T7 / 18 / 335 / 90 / 0 / Z
T8 / 18 / 335 / 260 / 0 / Z

P100 | CANT. 1


BASE_COMBINADA_PORTICO_TOLVA_NORTE_t35_P05

A36 | ENVOLVENTE LOCAL X/Y/Z: 555 x 690 x 35

XY / escala 1:10

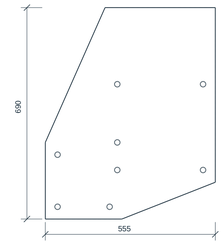

XZ / escala 1:2 / INTERRUMPIDA

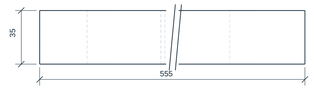

YZ / escala 1:4 / INTERRUMPIDA



CHAPA: espesor 35. Contorno nominal CAD; corte y taladros se identifican por coordenadas locales.
TALADROS / EJES: ID - Ø - X - Y - Z - DIRECCIÓN (mm)
T1 / 18 / -140 / -140 / 0 / Z
T2 / 18 / -140 / 140 / 0 / Z
T3 / 18 / 140 / -140 / 0 / Z
T4 / 18 / 140 / 140 / 0 / Z
T5 / 18 / 165 / -260 / 0 / Z
T6 / 18 / 140 / -50 / 0 / Z
T7 / 18 / 335 / -260 / 0 / Z
T8 / 18 / 335 / -90 / 0 / Z

Cotas en mm. Unidades y referencias locales X/Y/Z. Las vistas de detalle y DXF son proyecciones del CAD exacto OpenCascade; no se atribuye exportación nativa de SolidWorks a estas láminas.

Tolerancias ISO 2768-1 clase m en cotas lineales/angulares de piezas mecanizadas sin tolerancia individual. No se aplica a ajustes, soldaduras, equipos comerciales ni dimensiones de montaje críticas.

No escalar el PDF. Taladrar/escariar y desbarbar; eliminar aristas cortantes. Las preparaciones con luz 2 mm conservan geometría CAD; ejecutar soldadura únicamente según cuadro de juntas y WPS aplicable.

Acabados, ajustes y aceptación de uniones: según memoria, detalle específico y programa de inspección. Los espacios de verificación/aprobación permanecen sin firma.

Fuente: native_manifest.json + solidworks_model.bas; geometría y coordenadas íntegramente trazadas.

P05 - PLANOS DE DETALLE PARA REVISIÓN TÉCNICA

ESTACIÓN BIGBAG						**P05**
SESUVECA DEL PERÚ				SESUVECA DEL PERÚ		
						DESPIECE DE FABRICACIÓN / COTAS LOCALES
DIBUJ.	PROYECTO P05		16/10/2026			
VERIF.						
APROB.						
FABR.						
CALID.				MATERIAL: SEGÚN DESPIECE		**ESTACIÓN DE DESCARGA BIGBAG** — **A1**
PESO: BOM / CAD				ESCALA: INDICADA		**P05-T-021** — HOJA 21/51

DESPIECE DE FABRICACIÓN / COTAS LOCALES


Detalles 85..88 de 175 componentes fabricados. Proyecciones exactas de la geometría final.

P103 | CANT. 4

PORTICO_CIERRE_IPE200_2000x200x8_P05

A36 | ENVOLVENTE LOCAL X/Y/Z: 2000 x 200 x 8


XY / escala 1:5 / INTERRUMPIDA

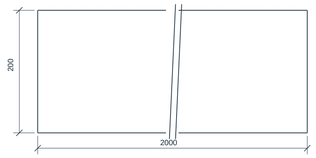

XZ / escala 1:5 / INTERRUMPIDA



YZ / escala 1:1 / INTERRUMPIDA

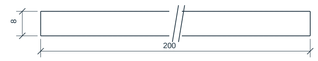


CHAPA: espesor 8. Contorno nominal CAD; corte y taladros se identifican por coordenadas locales.
Sin taladros parametrizados adicionales. Contornos circulares en vistas y DXF.

P104 | CANT. 1


TC01_SADDLE_300x180x20_P05

ASTM A36 | ENVOLVENTE LOCAL X/Y/Z: 300 x 180 x 20


XY / escala 1:4

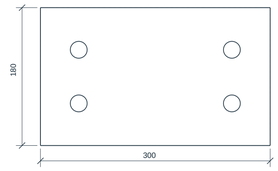

XZ / escala 1:2 / INTERRUMPIDA

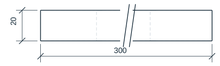

YZ / escala 1:1 / INTERRUMPIDA

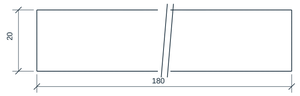

CHAPA: espesor 20. Contorno nominal CAD; corte y taladros se identifican por coordenadas locales.
TALADROS / EJES: ID - Ø - X - Y - Z - DIRECCIÓN (mm)
T1 / 22 / -100 / -35 / 0 / Z
T2 / 22 / -100 / 35 / 0 / Z
T3 / 22 / 100 / -35 / 0 / Z
T4 / 22 / 100 / 35 / 0 / Z

P105 | CANT. 2


TC02_DUPLICADOR_ALA_300x60x12_P05

ASTM A36 Fy250 | ENVOLVENTE LOCAL X/Y/Z: 300 x 60 x 12

XY / escala 1:4



XZ / escala 1:2 / INTERRUMPIDA

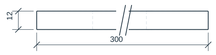

YZ / escala 1:1




CHAPA: espesor 12. Contorno nominal CAD; corte y taladros se identifican por coordenadas locales.
TALADROS / EJES: ID - Ø - X - Y - Z - DIRECCIÓN (mm)
T1 / 22 / -100 / 0 / 0 / Z
T2 / 22 / 100 / 0 / 0 / Z

P106 | CANT. 1

TC03_BRAZO_SHS100x100x10_S355_L300_P05

S355NH / EN10210-1 | ENVOLVENTE LOCAL X/Y/Z: 100 x 100 x 350

XY / escala 1:2

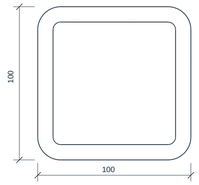

XZ / escala 1:5



YZ / escala 1:5



CHAPA: espesor 0. Contorno nominal CAD; corte y taladros se identifican por coordenadas locales.
Sin taladros parametrizados adicionales. Contornos circulares en vistas y DXF.

Cotas en mm. Unidades y referencias locales X/Y/Z. Las vistas de detalle y DXF son proyecciones del CAD exacto OpenCascade; no se atribuye exportación nativa de SolidWorks a estas láminas.

Tolerancias ISO 2768-1 clase m en cotas lineales/angulares de piezas mecanizadas sin tolerancia individual. No se aplica a ajustes, soldaduras, equipos comerciales ni dimensiones de montaje críticas.

No escalar el PDF. Taladrar/escariar y desbarbar; eliminar aristas cortantes. Las preparaciones con luz 2 mm conservan geometría CAD; ejecutar soldadura únicamente según cuadro de juntas y WPS aplicable.

Acabados, ajustes y aceptación de uniones: según memoria, detalle específico y programa de inspección. Los espacios de verificación/aprobación permanecen sin firma.

Fuente: native_manifest.json + solidworks_model.bas; geometría y coordenadas íntegramente trazadas.

P05 - PLANOS DE DETALLE PARA REVISIÓN TÉCNICA

ESTACIÓN BIGBAG						**P05**
SESUVECA DEL PERÚ						
						DESPIECE DE FABRICACIÓN / COTAS LOCALES
DIBUJ.	PROYECTO P05		16/10/2026			
VERIF.						
APROB.						
FABR.						
CALID.				MATERIAL: SEGÚN DESPIECE		**ESTACIÓN DE DESCARGA BIGBAG** / **A1**
PESO: BOM / CAD				ESCALA: INDICADA		**P05-T-022** / HOJA 22/51

DESPIECE DE FABRICACIÓN / COTAS LOCALES


Detalles 89..92 de 175 componentes fabricados. Proyecciones exactas de la geometría final.

P107 | CANT. 1


TC04_POSTE_SHS100x100x10_S355_L200_P05

S355NH / EN10210-1 | ENVOLVENTE LOCAL X/Y/Z: 100 x 100 x 215


XY / escala 1:2

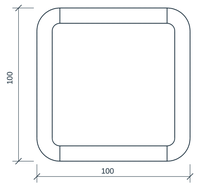

XZ / escala 1:4

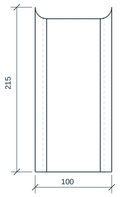

YZ / escala 1:4

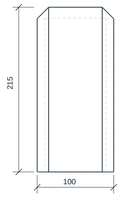


CHAPA: espesor 0. Contorno nominal CAD; corte y taladros se identifican por coordenadas locales.
Sin taladros parametrizados adicionales. Contornos circulares en vistas y DXF.

P108 | CANT. 1


TC05_PLACA_HORQUILLA_200x160x20_P05

ASTM A36 | ENVOLVENTE LOCAL X/Y/Z: 200 x 160 x 20


XY / escala 1:4

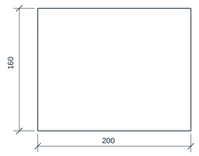

XZ / escala 1:1 / INTERRUMPIDA

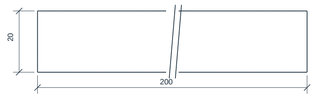

YZ / escala 1:1 / INTERRUMPIDA

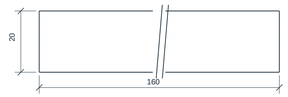


CHAPA: espesor 20. Contorno nominal CAD; corte y taladros se identifican por coordenadas locales.
Sin taladros parametrizados adicionales. Contornos circulares en vistas y DXF.

P109 | CANT. 2


TC06_OREJA_80x100x12_D31_P05

ASTM A36 | ENVOLVENTE LOCAL X/Y/Z: 80 x 100 x 12

XY / escala 1:2

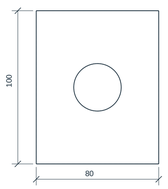

XZ / escala 1:1 / INTERRUMPIDA

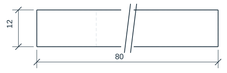

YZ / escala 1:1 / INTERRUMPIDA




CHAPA: espesor 12. Contorno nominal CAD; corte y taladros se identifican por coordenadas locales.
TALADROS / EJES: ID - Ø - X - Y - Z - DIRECCIÓN (mm)
T1 / 31 / 0 / 0 / 0 / Z

P110 | CANT. 1

TC07_RECEPTOR_80x96x16_D31_P05

A36 | ENVOLVENTE LOCAL X/Y/Z: 80 x 96 x 16


XY / escala 1:2

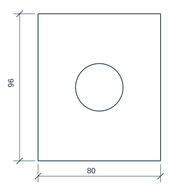

XZ / escala 1:1



YZ / escala 1:1 / INTERRUMPIDA

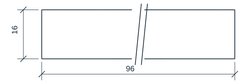

CHAPA: espesor 16. Contorno nominal CAD; corte y taladros se identifican por coordenadas locales.
TALADROS / EJES: ID - Ø - X - Y - Z - DIRECCIÓN (mm)
T1 / 31 / 0 / 0 / 0 / Z

Cotas en mm. Unidades y referencias locales X/Y/Z. Las vistas de detalle y DXF son proyecciones del CAD exacto OpenCascade; no se atribuye exportación nativa de SolidWorks a estas láminas.

Tolerancias ISO 2768-1 clase m en cotas lineales/angulares de piezas mecanizadas sin tolerancia individual. No se aplica a ajustes, soldaduras, equipos comerciales ni dimensiones de montaje críticas.

No escalar el PDF. Taladrar/escariar y desbarbar; eliminar aristas cortantes. Las preparaciones con luz 2 mm conservan geometría CAD; ejecutar soldadura únicamente según cuadro de juntas y WPS aplicable.

Acabados, ajustes y aceptación de uniones: según memoria, detalle específico y programa de inspección. Los espacios de verificación/aprobación permanecen sin firma.

Fuente: native_manifest.json + solidworks_model.bas; geometría y coordenadas íntegramente trazadas.

P05 - PLANOS DE DETALLE PARA REVISIÓN TÉCNICA

ESTACIÓN BIGBAG							**P05**
SESUVECA DEL PERÚ							
						DESPIECE DE FABRICACIÓN / COTAS LOCALES	
DIBUJ.	PROYECTO P05		16/10/2026				
VERIF.							
APROB.							
FABR.							
CALID.				MATERIAL: SEGÚN DESPIECE		**ESTACIÓN DE DESCARGA BIGBAG**	**A1**
PESO: BOM / CAD				ESCALA: INDICADA		**P05-T-023**	HOJA 23/51

DESPIECE DE FABRICACIÓN / COTAS LOCALES


Detalles 93..96 de 175 componentes fabricados. Proyecciones exactas de la geometría final.

P111 | CANT. 1


TC08_ADAPTADOR_200x160x20_4D18_P05

A36 | ENVOLVENTE LOCAL X/Y/Z: 200 x 160 x 20


XY / escala 1:4

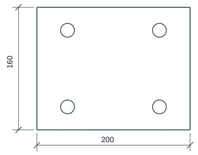

XZ / escala 1:1 / INTERRUMPIDA

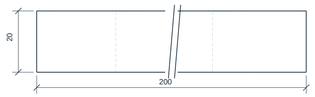

YZ / escala 1:1 / INTERRUMPIDA

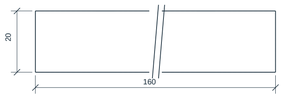


CHAPA: espesor 20. Contorno nominal CAD; corte y taladros se identifican por coordenadas locales.
TALADROS / EJES: ID - Ø - X - Y - Z - DIRECCIÓN (mm)
T1 / 18 / -60 / -50 / 0 / Z
T2 / 18 / -60 / 50 / 0 / Z
T3 / 18 / 60 / -50 / 0 / Z
T4 / 18 / 60 / 50 / 0 / Z

P112 | CANT. 2


TC09_CARTABON_SADDLE_220x120x20_P05

ASTM A36 | ENVOLVENTE LOCAL X/Y/Z: 220 x 120 x 20


XY / escala 1:4

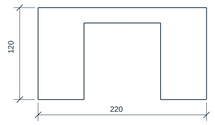

XZ / escala 1:1 / INTERRUMPIDA

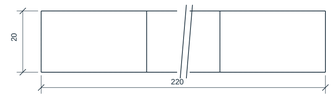

YZ / escala 1:1 / INTERRUMPIDA

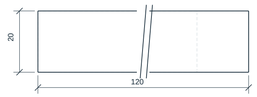


CHAPA: espesor 20. Contorno nominal CAD; corte y taladros se identifican por coordenadas locales.
Sin taladros parametrizados adicionales. Contornos circulares en vistas y DXF.

P113 | CANT. 2


TC10_CARTABON_RECEPTOR_60x60x12_P05

ASTM A36 | ENVOLVENTE LOCAL X/Y/Z: 60 x 60 x 12


XY / escala 1:1

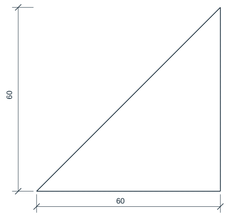

XZ / escala 1:1 / INTERRUMPIDA

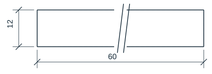

YZ / escala 1:1 / INTERRUMPIDA

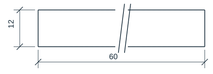


CHAPA: espesor 12. Contorno nominal CAD; corte y taladros se identifican por coordenadas locales.
Sin taladros parametrizados adicionales. Contornos circulares en vistas y DXF.

P114 | CANT. 1

TC11_PASADOR_D30_L90_FY355_P05

Acero certificado Fy>=355MPa | ENVOLVENTE LOCAL X/Y/Z: 30 x 30 x 90

XY / escala 2:1

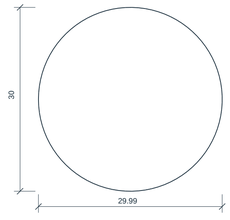

XZ / escala 1:2



YZ / escala 1:2



TORNEADO / TUBO: exterior Ø30, pared 0, longitud 90.
TALADROS / EJES: ID - Ø - X - Y - Z - DIRECCIÓN (mm)
B1 / 4.5 / 0 / 16 / 78 / Y

Cotas en mm. Unidades y referencias locales X/Y/Z. Las vistas de detalle y DXF son proyecciones del CAD exacto OpenCascade; no se atribuye exportación nativa de SolidWorks a estas láminas.

Tolerancias ISO 2768-1 clase m en cotas lineales/angulares de piezas mecanizadas sin tolerancia individual. No se aplica a ajustes, soldaduras, equipos comerciales ni dimensiones de montaje críticas.

No escalar el PDF. Taladrar/escariar y desbarbar; eliminar aristas cortantes. Las preparaciones con luz 2 mm conservan geometría CAD; ejecutar soldadura únicamente según cuadro de juntas y WPS aplicable.

Acabados, ajustes y aceptación de uniones: según memoria, detalle específico y programa de inspección. Los espacios de verificación/aprobación permanecen sin firma.

Fuente: native_manifest.json + solidworks_model.bas; geometría y coordenadas íntegramente trazadas.

P05 - PLANOS DE DETALLE PARA REVISIÓN TÉCNICA

ESTACIÓN BIGBAG							**P05**
SESUVECA DEL PERÚ							
DIBUJ.	PROYECTO P05		16/10/2026			**DESPIECE DE FABRICACIÓN / COTAS LOCALES**	
VERIF.							
APROB.							
FABR.							
CALID.				MATERIAL: SEGÚN DESPIECE		**ESTACIÓN DE DESCARGA BIGBAG**	**A1**
PESO: BOM / CAD				ESCALA: INDICADA		**P05-T-024**	HOJA 24/51

DESPIECE DE FABRICACIÓN / COTAS LOCALES


Detalles 97..100 de 175 componentes fabricados. Proyecciones exactas de la geometría final.

P115 | CANT. 1

TC12_CABEZA_D46_L8_P05

ASTM A36 / SEGÚN MEMORIA | ENVOLVENTE LOCAL X/Y/Z: 46 x 46 x 8

XY / escala 1:1

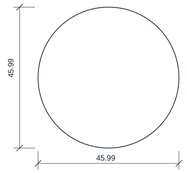

XZ / escala 2:1



YZ / escala 2:1



TORNEADO / TUBO: exterior Ø46, pared 0, longitud 8.
Sin taladros parametrizados adicionales. Contornos circulares en vistas y DXF.

P117 | CANT. 1

TC17_OJAL_CABLE_40x12x3_P05

ASTM A36 | ENVOLVENTE LOCAL X/Y/Z: 40 x 12 x 3

XY / escala 2:1



XZ / escala 2:1



YZ / escala 5:1




CHAPA: espesor 3. Contorno nominal CAD; corte y taladros se identifican por coordenadas locales.
TALADROS / EJES: ID - Ø - X - Y - Z - DIRECCIÓN (mm)
T1 / 4 / 12 / 0 / 0 / Z

P126 | CANT. 1

BRT_A_FINAL_P05

A36 | ENVOLVENTE LOCAL X/Y/Z: 60 x 60 x 5499.97

XY / escala 1:1

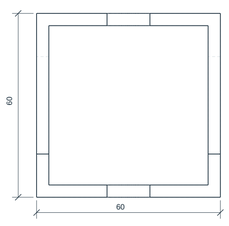

XZ / escala 1:10 / INTERRUMPIDA



YZ / escala 1:10 / INTERRUMPIDA



CHAPA: espesor 0. Contorno nominal CAD; corte y taladros se identifican por coordenadas locales.
Sin taladros parametrizados adicionales. Contornos circulares en vistas y DXF.


RANURAS: ancho 14; tramo recto 120; R7; ambos extremos según CAD.

P127 | CANT. 1


BRT_LENGUETA_BRT-A_0_250x250x12_P05

ASTM A36 | ENVOLVENTE LOCAL X/Y/Z: 250 x 250 x 12

XY / escala 1:4

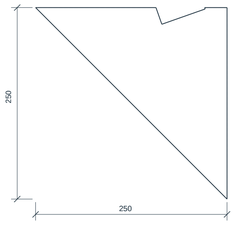

XZ / escala 1:2 / INTERRUMPIDA

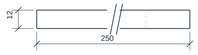

YZ / escala 1:2 / INTERRUMPIDA



CHAPA: espesor 12. Contorno nominal CAD; corte y taladros se identifican por coordenadas locales.
Sin taladros parametrizados adicionales. Contornos circulares en vistas y DXF.

Cotas en mm. Unidades y referencias locales X/Y/Z. Las vistas de detalle y DXF son proyecciones del CAD exacto OpenCascade; no se atribuye exportación nativa de SolidWorks a estas láminas.

Tolerancias ISO 2768-1 clase m en cotas lineales/angulares de piezas mecanizadas sin tolerancia individual. No se aplica a ajustes, soldaduras, equipos comerciales ni dimensiones de montaje críticas.

No escalar el PDF. Taladrar/escariar y desbarbar; eliminar aristas cortantes. Las preparaciones con luz 2 mm conservan geometría CAD; ejecutar soldadura únicamente según cuadro de juntas y WPS aplicable.

Acabados, ajustes y aceptación de uniones: según memoria, detalle específico y programa de inspección. Los espacios de verificación/aprobación permanecen sin firma.

Fuente: native_manifest.json + solidworks_model.bas; geometría y coordenadas íntegramente trazadas.

P05 - PLANOS DE DETALLE PARA REVISIÓN TÉCNICA

ESTACIÓN BIGBAG							**P05**
SESUVECA DEL PERÚ							
						DESPIECE DE FABRICACIÓN / COTAS LOCALES	
DIBUJ.	PROYECTO P05		16/10/2026				
VERIF.							
APROB.							
FABR.							
CALID.				MATERIAL: SEGÚN DESPIECE		**ESTACIÓN DE DESCARGA BIGBAG**	**A1**
PESO: BOM / CAD				ESCALA: INDICADA		**P05-T-025**	HOJA 25/51

DESPIECE DE FABRICACIÓN / COTAS LOCALES


Detalles 101..104 de 175 componentes fabricados. Proyecciones exactas de la geometría final.

P128 | CANT. 1

BRT_LENGUETA_BRT-A_1_250x250x12_P05

ASTM A36 | ENVOLVENTE LOCAL X/Y/Z: 250 x 250 x 12

XY / escala 1:4

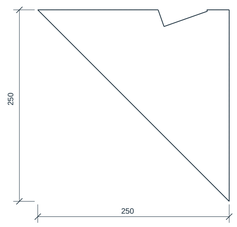

XZ / escala 1:2 / INTERRUMPIDA



YZ / escala 1:2 / INTERRUMPIDA




CHAPA: espesor 12. Contorno nominal CAD; corte y taladros se identifican por coordenadas locales.
Sin taladros parametrizados adicionales. Contornos circulares en vistas y DXF.

P129 | CANT. 1


BRT_B_FINAL_P05

A36 | ENVOLVENTE LOCAL X/Y/Z: 60 x 60 x 5499.97

XY / escala 1:1

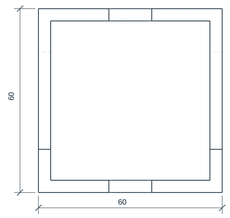

XZ / escala 1:10 / INTERRUMPIDA

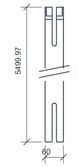

YZ / escala 1:10 / INTERRUMPIDA



CHAPA: espesor 0. Contorno nominal CAD; corte y taladros se identifican por coordenadas locales.
Sin taladros parametrizados adicionales. Contornos circulares en vistas y DXF.


RANURAS: ancho 14; tramo recto 120; R7; ambos extremos según CAD.

P130 | CANT. 1

BRT_LENGUETA_BRT-B_0_250x250x12_P05

ASTM A36 | ENVOLVENTE LOCAL X/Y/Z: 250 x 250 x 12

XY / escala 1:4

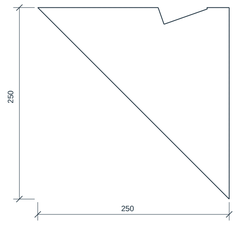

XZ / escala 1:2 / INTERRUMPIDA



YZ / escala 1:2 / INTERRUMPIDA




CHAPA: espesor 12. Contorno nominal CAD; corte y taladros se identifican por coordenadas locales.
Sin taladros parametrizados adicionales. Contornos circulares en vistas y DXF.

P131 | CANT. 1

BRT_LENGUETA_BRT-B_1_250x250x12_P05

ASTM A36 | ENVOLVENTE LOCAL X/Y/Z: 250 x 250 x 12

XY / escala 1:4

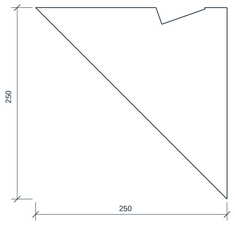

XZ / escala 1:2 / INTERRUMPIDA



YZ / escala 1:2 / INTERRUMPIDA



CHAPA: espesor 12. Contorno nominal CAD; corte y taladros se identifican por coordenadas locales.
Sin taladros parametrizados adicionales. Contornos circulares en vistas y DXF.

Cotas en mm. Unidades y referencias locales X/Y/Z. Las vistas de detalle y DXF son proyecciones del CAD exacto OpenCascade; no se atribuye exportación nativa de SolidWorks a estas láminas.

Tolerancias ISO 2768-1 clase m en cotas lineales/angulares de piezas mecanizadas sin tolerancia individual. No se aplica a ajustes, soldaduras, equipos comerciales ni dimensiones de montaje críticas.

No escalar el PDF. Taladrar/escariar y desbarbar; eliminar aristas cortantes. Las preparaciones con luz 2 mm conservan geometría CAD; ejecutar soldadura únicamente según cuadro de juntas y WPS aplicable.

Acabados, ajustes y aceptación de uniones: según memoria, detalle específico y programa de inspección. Los espacios de verificación/aprobación permanecen sin firma.

Fuente: native_manifest.json + solidworks_model.bas; geometría y coordenadas íntegramente trazadas.

P05 - PLANOS DE DETALLE PARA REVISIÓN TÉCNICA

ESTACIÓN BIGBAG						**P05**
SESUVECA DEL PERÚ	SESUVECA DEL PERÚ					
						DESPIECE DE FABRICACIÓN / COTAS LOCALES
DIBUJ.	PROYECTO P05		16/10/2026			
VERIF.						
APROB.						
FABR.						
CALID.				MATERIAL: SEGÚN DESPIECE		**ESTACIÓN DE DESCARGA BIGBAG** — **A1**
PESO: BOM / CAD				ESCALA: INDICADA		**P05-T-026** — HOJA 26/51

DESPIECE DE FABRICACIÓN / COTAS LOCALES

Detalles 105..108 de 175 componentes fabricados. Proyecciones exactas de la geometría final.

P132 | CANT. 8


BRT_COLLAR_150x300x12_P05

ASTM A36 | ENVOLVENTE LOCAL X/Y/Z: 150 x 300 x 12


XY / escala 1:5



XZ / escala 1:1 / INTERRUMPIDA

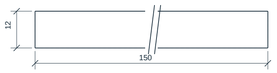

YZ / escala 1:2 / INTERRUMPIDA

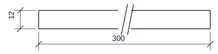


CHAPA: espesor 12. Contorno nominal CAD; corte y taladros se identifican por coordenadas locales.
Sin taladros parametrizados adicionales. Contornos circulares en vistas y DXF.

P133 | CANT. 8

BRT_COLLAR_174x300x12_P05

ASTM A36 | ENVOLVENTE LOCAL X/Y/Z: 174 x 300 x 12


XY / escala 1:5

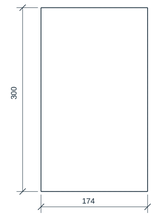

XZ / escala 1:1 / INTERRUMPIDA



YZ / escala 1:2 / INTERRUMPIDA

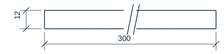


CHAPA: espesor 12. Contorno nominal CAD; corte y taladros se identifican por coordenadas locales.
Sin taladros parametrizados adicionales. Contornos circulares en vistas y DXF.

P134 | CANT. 4


BRT_RESPALDO_174x300x20_P05

ASTM A36 | ENVOLVENTE LOCAL X/Y/Z: 174 x 300 x 20

XY / escala 1:5

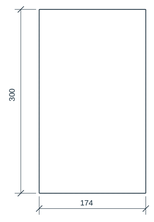

XZ / escala 1:1 / INTERRUMPIDA

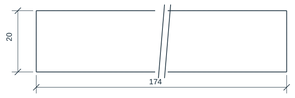

YZ / escala 1:2 / INTERRUMPIDA




CHAPA: espesor 20. Contorno nominal CAD; corte y taladros se identifican por coordenadas locales.
Sin taladros parametrizados adicionales. Contornos circulares en vistas y DXF.

P135 | CANT. 4

BRT_OUTRIGGER_SHS100x100x10_S355_L468_P05

S355NH / EN10210-1 | ENVOLVENTE LOCAL X/Y/Z: 100 x 100 x 468

XY / escala 1:2

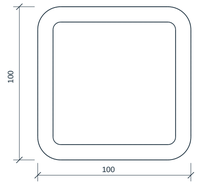

XZ / escala 1:10



YZ / escala 1:10



CHAPA: espesor 0. Contorno nominal CAD; corte y taladros se identifican por coordenadas locales.
Sin taladros parametrizados adicionales. Contornos circulares en vistas y DXF.

Cotas en mm. Unidades y referencias locales X/Y/Z. Las vistas de detalle y DXF son proyecciones del CAD exacto OpenCascade; no se atribuye exportación nativa de SolidWorks a estas láminas.

Tolerancias ISO 2768-1 clase m en cotas lineales/angulares de piezas mecanizadas sin tolerancia individual. No se aplica a ajustes, soldaduras, equipos comerciales ni dimensiones de montaje críticas.

No escalar el PDF. Taladrar/escariar y desbarbar; eliminar aristas cortantes. Las preparaciones con luz 2 mm conservan geometría CAD; ejecutar soldadura únicamente según cuadro de juntas y WPS aplicable.

Acabados, ajustes y aceptación de uniones: según memoria, detalle específico y programa de inspección. Los espacios de verificación/aprobación permanecen sin firma.

Fuente: native_manifest.json + solidworks_model.bas; geometría y coordenadas íntegramente trazadas.

P05 - PLANOS DE DETALLE PARA REVISIÓN TÉCNICA

ESTACIÓN BIGBAG							**P05**
SESUVECA DEL PERÚ							
						DESPIECE DE FABRICACIÓN / COTAS LOCALES	
DIBUJ.	PROYECTO P05		16/10/2026				
VERIF.							
APROB.							
FABR.							
CALID.				MATERIAL: SEGÚN DESPIECE		**ESTACIÓN DE DESCARGA BIGBAG**	**A1**
PESO: BOM / CAD				ESCALA: INDICADA		**P05-T-027**	HOJA 27/51

DESPIECE DE FABRICACIÓN / COTAS LOCALES


Detalles 109..112 de 175 componentes fabricados. Proyecciones exactas de la geometría final.

P136 | CANT. 4

BRT_CONTRACARA_250x250x20_P05

ASTM A36 | ENVOLVENTE LOCAL X/Y/Z: 250 x 250 x 20

XY / escala 1:4

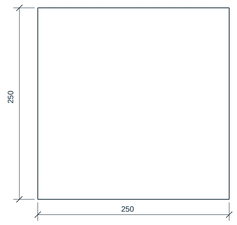

XZ / escala 1:2 / INTERRUMPIDA



YZ / escala 1:2 / INTERRUMPIDA




CHAPA: espesor 20. Contorno nominal CAD; corte y taladros se identifican por coordenadas locales.
Sin taladros parametrizados adicionales. Contornos circulares en vistas y DXF.

P137 | CANT. 1

GRID__0p25_FINAL_P05

A36 | ENVOLVENTE LOCAL X/Y/Z: 120 x 120 x 2050

XY / escala 1:2

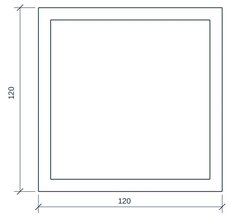

XZ / escala 1:10 / INTERRUMPIDA



YZ / escala 1:10 / INTERRUMPIDA




CHAPA: espesor 0. Contorno nominal CAD; corte y taladros se identifican por coordenadas locales.
Sin taladros parametrizados adicionales. Contornos circulares en vistas y DXF.

P138 | CANT. 4


GRID_ASIENTO_150x150x20_P05

ASTM A36 | ENVOLVENTE LOCAL X/Y/Z: 150 x 150 x 20


XY / escala 1:4

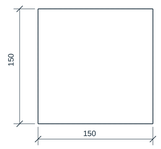

XZ / escala 1:1 / INTERRUMPIDA

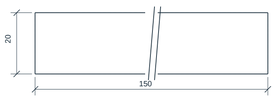

YZ / escala 1:1 / INTERRUMPIDA

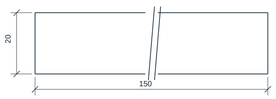


CHAPA: espesor 20. Contorno nominal CAD; corte y taladros se identifican por coordenadas locales.
Sin taladros parametrizados adicionales. Contornos circulares en vistas y DXF.

P139 | CANT. 4

GRID_DIAFRAGMA_HUP_138x138x12_P05

ASTM A36 | ENVOLVENTE LOCAL X/Y/Z: 138 x 138 x 12

XY / escala 1:2

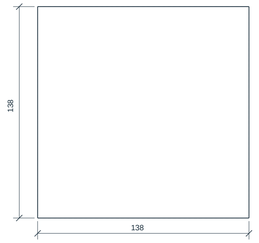

XZ / escala 1:1 / INTERRUMPIDA



YZ / escala 1:1 / INTERRUMPIDA



CHAPA: espesor 12. Contorno nominal CAD; corte y taladros se identifican por coordenadas locales.
Sin taladros parametrizados adicionales. Contornos circulares en vistas y DXF.

Cotas en mm. Unidades y referencias locales X/Y/Z. Las vistas de detalle y DXF son proyecciones del CAD exacto OpenCascade; no se atribuye exportación nativa de SolidWorks a estas láminas.

Tolerancias ISO 2768-1 clase m en cotas lineales/angulares de piezas mecanizadas sin tolerancia individual. No se aplica a ajustes, soldaduras, equipos comerciales ni dimensiones de montaje críticas.

No escalar el PDF. Taladrar/escariar y desbarbar; eliminar aristas cortantes. Las preparaciones con luz 2 mm conservan geometría CAD; ejecutar soldadura únicamente según cuadro de juntas y WPS aplicable.

Acabados, ajustes y aceptación de uniones: según memoria, detalle específico y programa de inspección. Los espacios de verificación/aprobación permanecen sin firma.

Fuente: native_manifest.json + solidworks_model.bas; geometría y coordenadas íntegramente trazadas.

P05 - PLANOS DE DETALLE PARA REVISIÓN TÉCNICA

ESTACIÓN BIGBAG						**P05**
SESUVECA DEL PERÚ				SESUVECA DEL PERÚ		
						DESPIECE DE FABRICACIÓN / COTAS LOCALES
DIBUJ.	PROYECTO P05		16/10/2026			
VERIF.						
APROB.						
FABR.						
CALID.				MATERIAL: SEGÚN DESPIECE		**ESTACIÓN DE DESCARGA BIGBAG** — **A1**
PESO: BOM / CAD				ESCALA: INDICADA		**P05-T-028** — HOJA 28/51

DESPIECE DE FABRICACIÓN / COTAS LOCALES


Detalles 113..116 de 175 componentes fabricados. Proyecciones exactas de la geometría final.

P140 | CANT. 1

GRID_0p25_FINAL_P05

A36 | ENVOLVENTE LOCAL X/Y/Z: 120 x 120 x 2050

XY / escala 1:2

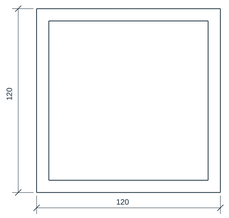

XZ / escala 1:10 / INTERRUMPIDA



YZ / escala 1:10 / INTERRUMPIDA




CHAPA: espesor 0. Contorno nominal CAD; corte y taladros se identifican por coordenadas locales.
Sin taladros parametrizados adicionales. Contornos circulares en vistas y DXF.

P141 | CANT. 2


CORTE_TRAVESANO100x100x5_L630_P05

A36 | ENVOLVENTE LOCAL X/Y/Z: 100 x 100 x 630


XY / escala 1:2

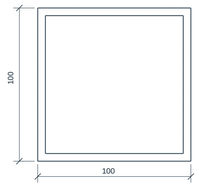

XZ / escala 1:4 / INTERRUMPIDA

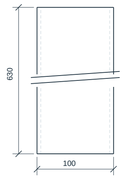

YZ / escala 1:4 / INTERRUMPIDA

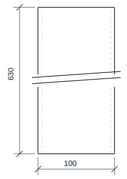


PERFIL SHS100x100x5; longitud nominal 630. Preparaciones y recortes finales en vistas/DXF.
Sin taladros parametrizados adicionales. Contornos circulares en vistas y DXF.

P142 | CANT. 1

CORTE_ESPACIADOR_CENTRAL_200x200x12_P05

AISI 304 | ENVOLVENTE LOCAL X/Y/Z: 200 x 200 x 12

XY / escala 1:4

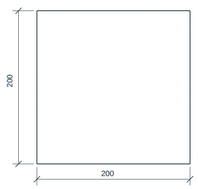

XZ / escala 1:1 / INTERRUMPIDA



YZ / escala 1:1 / INTERRUMPIDA




CHAPA: espesor 12. Contorno nominal CAD; corte y taladros se identifican por coordenadas locales.
Sin taladros parametrizados adicionales. Contornos circulares en vistas y DXF.

P143 | CANT. 1

HR_2p3124_1_FINAL_P05

S355NH / EN10210-1 | ENVOLVENTE LOCAL X/Y/Z: 60 x 100 x 1812


XY / escala 1:2

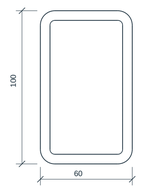

XZ / escala 1:10 / INTERRUMPIDA



YZ / escala 1:10 / INTERRUMPIDA

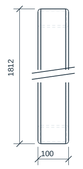

PERFIL RHS100x60x6.3; longitud nominal 1752. Preparaciones y recortes finales en vistas/DXF.
Sin taladros parametrizados adicionales. Contornos circulares en vistas y DXF.

Cotas en mm. Unidades y referencias locales X/Y/Z. Las vistas de detalle y DXF son proyecciones del CAD exacto OpenCascade; no se atribuye exportación nativa de SolidWorks a estas láminas.

Tolerancias ISO 2768-1 clase m en cotas lineales/angulares de piezas mecanizadas sin tolerancia individual. No se aplica a ajustes, soldaduras, equipos comerciales ni dimensiones de montaje críticas.

No escalar el PDF. Taladrar/escariar y desbarbar; eliminar aristas cortantes. Las preparaciones con luz 2 mm conservan geometría CAD; ejecutar soldadura únicamente según cuadro de juntas y WPS aplicable.

Acabados, ajustes y aceptación de uniones: según memoria, detalle específico y programa de inspección. Los espacios de verificación/aprobación permanecen sin firma.

Fuente: native_manifest.json + solidworks_model.bas; geometría y coordenadas íntegramente trazadas.

DESPIECE DE FABRICACIÓN / COTAS LOCALES


Detalles 117..120 de 175 componentes fabricados. Proyecciones exactas de la geometría final.

P144 | CANT. 1


HR_2p3124_2_FINAL_P05

S355NH / EN10210-1 | ENVOLVENTE LOCAL X/Y/Z: 60 x 100 x 1812


XY / escala 1:2

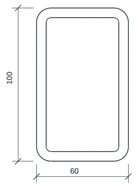

XZ / escala 1:10 / INTERRUMPIDA

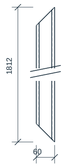

YZ / escala 1:10 / INTERRUMPIDA

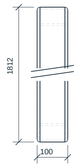


PERFIL RHS100x60x6.3; longitud nominal 1752. Preparaciones y recortes finales en vistas/DXF.
Sin taladros parametrizados adicionales. Contornos circulares en vistas y DXF.

P145 | CANT. 1

HR_2p3124_3_FINAL_P05

S355NH / EN10210-1 | ENVOLVENTE LOCAL X/Y/Z: 60 x 100 x 1812


XY / escala 1:2

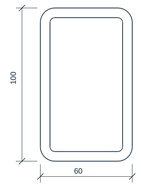

XZ / escala 1:10 / INTERRUMPIDA



YZ / escala 1:10 / INTERRUMPIDA

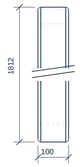


PERFIL RHS100x60x6.3; longitud nominal 1752. Preparaciones y recortes finales en vistas/DXF.
Sin taladros parametrizados adicionales. Contornos circulares en vistas y DXF.

P146 | CANT. 1

HR_2p3124_4_FINAL_P05

S355NH / EN10210-1 | ENVOLVENTE LOCAL X/Y/Z: 60 x 100 x 1812


XY / escala 1:2

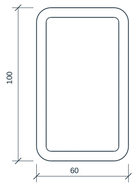

XZ / escala 1:10 / INTERRUMPIDA



YZ / escala 1:10 / INTERRUMPIDA

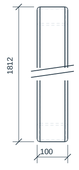


PERFIL RHS100x60x6.3; longitud nominal 1752. Preparaciones y recortes finales en vistas/DXF.
Sin taladros parametrizados adicionales. Contornos circulares en vistas y DXF.

P148 | CANT. 1

SHS60x60x4_L6085645_SLOT_P05_JUNTA_1

ASTM A500 Gr.B | ENVOLVENTE LOCAL X/Y/Z: 60 x 60 x 6085.65

XY / escala 1:1

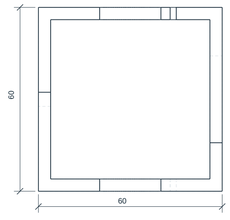

XZ / escala 1:10 / INTERRUMPIDA



YZ / escala 1:10 / INTERRUMPIDA



PERFIL SHS60x60x4; longitud nominal 6085.65. Preparaciones y recortes finales en vistas/DXF.
Sin taladros parametrizados adicionales. Contornos circulares en vistas y DXF.
Preparación final de unión incluida; luz nominal 2 mm. Ver registro JF y DXF.

RANURAS: ancho 20; tramo recto 120; R10; ambos extremos según CAD.

Cotas en mm. Unidades y referencias locales X/Y/Z. Las vistas de detalle y DXF son proyecciones del CAD exacto OpenCascade; no se atribuye exportación nativa de SolidWorks a estas láminas.

Tolerancias ISO 2768-1 clase m en cotas lineales/angulares de piezas mecanizadas sin tolerancia individual. No se aplica a ajustes, soldaduras, equipos comerciales ni dimensiones de montaje críticas.

No escalar el PDF. Taladrar/escariar y desbarbar; eliminar aristas cortantes. Las preparaciones con luz 2 mm conservan geometría CAD; ejecutar soldadura únicamente según cuadro de juntas y WPS aplicable.

Acabados, ajustes y aceptación de uniones: según memoria, detalle específico y programa de inspección. Los espacios de verificación/aprobación permanecen sin firma.

Fuente: native_manifest.json + solidworks_model.bas; geometría y coordenadas íntegramente trazadas.

P05 - PLANOS DE DETALLE PARA REVISIÓN TÉCNICA

ESTACIÓN BIGBAG							**P05**
SESUVECA DEL PERÚ							
						DESPIECE DE FABRICACIÓN / COTAS LOCALES	
DIBUJ.	PROYECTO P05		16/10/2026				
VERIF.							
APROB.							
FABR.							
CALID.				MATERIAL: SEGÚN DESPIECE		**ESTACIÓN DE DESCARGA BIGBAG**	**A1**
PESO: BOM / CAD				ESCALA: INDICADA		**P05-T-030**	HOJA 30/51

DESPIECE DE FABRICACIÓN / COTAS LOCALES


Detalles 121..124 de 175 componentes fabricados. Proyecciones exactas de la geometría final.

P149 | CANT. 1


SHS60x60x4_L6085645_SLOT_P05_JUNTA_2

ASTM A500 Gr.B | ENVOLVENTE LOCAL X/Y/Z: 60 x 60 x 6085.65

XY / escala 1:1

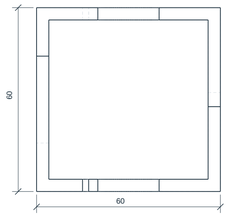

XZ / escala 1:10 / INTERRUMPIDA

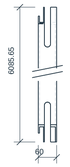

YZ / escala 1:10 / INTERRUMPIDA



PERFIL SHS60x60x4; longitud nominal 6085.65. Preparaciones y recortes finales en vistas/DXF.
Sin taladros parametrizados adicionales. Contornos circulares en vistas y DXF.
Preparación final de unión incluida; luz nominal 2 mm. Ver registro JF y DXF.


RANURAS: ancho 20; tramo recto 120; R10; ambos extremos según CAD.

P150 | CANT. 1

SHS60x60x4_L748810_SLOT_P05_JUNTA_3

ASTM A500 Gr.B | ENVOLVENTE LOCAL X/Y/Z: 60 x 60 x 748.81


XY / escala 1:1

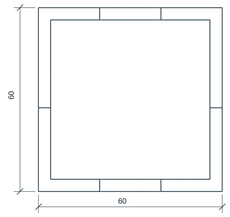

XZ / escala 1:4 / INTERRUMPIDA



YZ / escala 1:4 / INTERRUMPIDA

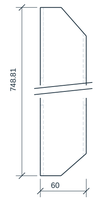

PERFIL SHS60x60x4; longitud nominal 748.81. Preparaciones y recortes finales en vistas/DXF.
Sin taladros parametrizados adicionales. Contornos circulares en vistas y DXF.
Preparación final de unión incluida; luz nominal 2 mm. Ver registro JF y DXF.


RANURAS: ancho 20; tramo recto 120; R10; ambos extremos según CAD.

P151 | CANT. 1

SHS60x60x4_L6085645_SLOT_P05_JUNTA_4

ASTM A500 Gr.B | ENVOLVENTE LOCAL X/Y/Z: 60 x 60 x 6085.65

XY / escala 1:1

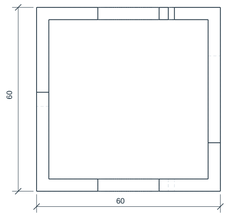

XZ / escala 1:10 / INTERRUMPIDA



YZ / escala 1:10 / INTERRUMPIDA



PERFIL SHS60x60x4; longitud nominal 6085.65. Preparaciones y recortes finales en vistas/DXF.
Sin taladros parametrizados adicionales. Contornos circulares en vistas y DXF.
Preparación final de unión incluida; luz nominal 2 mm. Ver registro JF y DXF.


RANURAS: ancho 20; tramo recto 120; R10; ambos extremos según CAD.

P152 | CANT. 1


SHS60x60x4_L6085645_SLOT_P05_JUNTA_5

ASTM A500 Gr.B | ENVOLVENTE LOCAL X/Y/Z: 60 x 60 x 6085.65


XY / escala 1:1

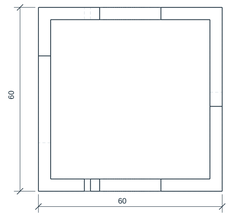

XZ / escala 1:10 / INTERRUMPIDA

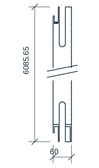

YZ / escala 1:10 / INTERRUMPIDA

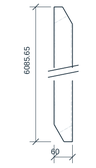

PERFIL SHS60x60x4; longitud nominal 6085.65. Preparaciones y recortes finales en vistas/DXF.
Sin taladros parametrizados adicionales. Contornos circulares en vistas y DXF.
Preparación final de unión incluida; luz nominal 2 mm. Ver registro JF y DXF.

RANURAS: ancho 20; tramo recto 120; R10; ambos extremos según CAD.

Cotas en mm. Unidades y referencias locales X/Y/Z. Las vistas de detalle y DXF son proyecciones del CAD exacto OpenCascade; no se atribuye exportación nativa de SolidWorks a estas láminas.

Tolerancias ISO 2768-1 clase m en cotas lineales/angulares de piezas mecanizadas sin tolerancia individual. No se aplica a ajustes, soldaduras, equipos comerciales ni dimensiones de montaje críticas.

No escalar el PDF. Taladrar/escariar y desbarbar; eliminar aristas cortantes. Las preparaciones con luz 2 mm conservan geometría CAD; ejecutar soldadura únicamente según cuadro de juntas y WPS aplicable.

Acabados, ajustes y aceptación de uniones: según memoria, detalle específico y programa de inspección. Los espacios de verificación/aprobación permanecen sin firma.

Fuente: native_manifest.json + solidworks_model.bas; geometría y coordenadas íntegramente trazadas.

P05 - PLANOS DE DETALLE PARA REVISIÓN TÉCNICA

ESTACIÓN BIGBAG							**P05**
SESUVECA DEL PERÚ							
DIBUJ.	PROYECTO P05		16/10/2026			**DESPIECE DE FABRICACIÓN / COTAS LOCALES**	
VERIF.							
APROB.							
FABR.							
CALID.				MATERIAL: SEGÚN DESPIECE		**ESTACIÓN DE DESCARGA BIGBAG**	**A1**
PESO: BOM / CAD				ESCALA: INDICADA		**P05-T-031**	HOJA 31/51

DESPIECE DE FABRICACIÓN / COTAS LOCALES


Detalles 125..128 de 175 componentes fabricados. Proyecciones exactas de la geometría final.

P153 | CANT. 1

SHS60x60x4_L748810_SLOT_P05_JUNTA_6

ASTM A500 Gr.B | ENVOLVENTE LOCAL X/Y/Z: 60 x 60 x 748.81

XY / escala 1:1

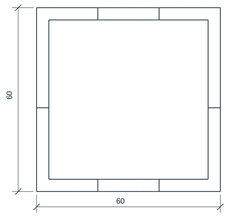

XZ / escala 1:4 / INTERRUMPIDA



YZ / escala 1:4 / INTERRUMPIDA



PERFIL SHS60x60x4; longitud nominal 748.81. Preparaciones y recortes finales en vistas/DXF.
Sin taladros parametrizados adicionales. Contornos circulares en vistas y DXF.
Preparación final de unión incluida; luz nominal 2 mm. Ver registro JF y DXF.


RANURAS: ancho 20; tramo recto 120; R10; ambos extremos según CAD.

P154 | CANT. 1


SHS60x60x4_L3050000_P05_JUNTA_14

ASTM A500 Gr.B | ENVOLVENTE LOCAL X/Y/Z: 60 x 60 x 3022

XY / escala 1:1

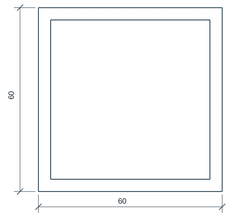

XZ / escala 1:10 / INTERRUMPIDA

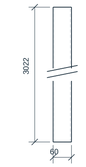

YZ / escala 1:10 / INTERRUMPIDA




PERFIL SHS60x60x4; longitud nominal 3050. Preparaciones y recortes finales en vistas/DXF.
Sin taladros parametrizados adicionales. Contornos circulares en vistas y DXF.
Preparación final de unión incluida; luz nominal 2 mm. Ver registro JF y DXF.

P155 | CANT. 1

SHS60x60x4_L3050000_P05_JUNTA_15

ASTM A500 Gr.B | ENVOLVENTE LOCAL X/Y/Z: 60 x 60 x 3022

XY / escala 1:1

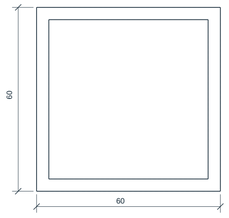

XZ / escala 1:10 / INTERRUMPIDA



YZ / escala 1:10 / INTERRUMPIDA




PERFIL SHS60x60x4; longitud nominal 3050. Preparaciones y recortes finales en vistas/DXF.
Sin taladros parametrizados adicionales. Contornos circulares en vistas y DXF.
Preparación final de unión incluida; luz nominal 2 mm. Ver registro JF y DXF.

P156 | CANT. 1


SHS60x60x4_L3050000_P05_JUNTA_16

ASTM A500 Gr.B | ENVOLVENTE LOCAL X/Y/Z: 60 x 60 x 3022

XY / escala 1:1

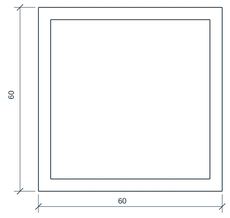

XZ / escala 1:10 / INTERRUMPIDA

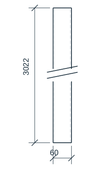

YZ / escala 1:10 / INTERRUMPIDA



PERFIL SHS60x60x4; longitud nominal 3050. Preparaciones y recortes finales en vistas/DXF.
Sin taladros parametrizados adicionales. Contornos circulares en vistas y DXF.
Preparación final de unión incluida; luz nominal 2 mm. Ver registro JF y DXF.

Cotas en mm. Unidades y referencias locales X/Y/Z. Las vistas de detalle y DXF son proyecciones del CAD exacto OpenCascade; no se atribuye exportación nativa de SolidWorks a estas láminas.

Tolerancias ISO 2768-1 clase m en cotas lineales/angulares de piezas mecanizadas sin tolerancia individual. No se aplica a ajustes, soldaduras, equipos comerciales ni dimensiones de montaje críticas.

No escalar el PDF. Taladrar/escariar y desbarbar; eliminar aristas cortantes. Las preparaciones con luz 2 mm conservan geometría CAD; ejecutar soldadura únicamente según cuadro de juntas y WPS aplicable.

Acabados, ajustes y aceptación de uniones: según memoria, detalle específico y programa de inspección. Los espacios de verificación/aprobación permanecen sin firma.

Fuente: native_manifest.json + solidworks_model.bas; geometría y coordenadas íntegramente trazadas.

ESTACIÓN BIGBAG							P05
SESUVECA DEL PERÚ							
						DESPIECE DE FABRICACIÓN / COTAS LOCALES	
DIBUJ.	PROYECTO P05		16/10/2026				
VERIF.							
APROB.							
FABR.							
CALID.				MATERIAL: SEGÚN DESPIECE		ESTACIÓN DE DESCARGA BIGBAG	A1
PESO: BOM / CAD				ESCALA: INDICADA		P05-T-032	HOJA 32/51

DESPIECE DE FABRICACIÓN / COTAS LOCALES


Detalles 129..132 de 175 componentes fabricados. Proyecciones exactas de la geometría final.

P157 | CANT. 1


SHS60x60x4_L3050000_P05_JUNTA_17

ASTM A500 Gr.B | ENVOLVENTE LOCAL X/Y/Z: 60 x 60 x 3022

XY / escala 1:1

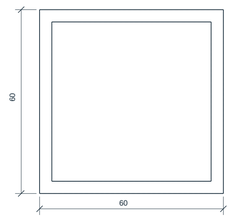

XZ / escala 1:10 / INTERRUMPIDA

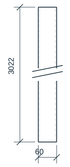

YZ / escala 1:10 / INTERRUMPIDA



PERFIL SHS60x60x4; longitud nominal 3050. Preparaciones y recortes finales en vistas/DXF.
Sin taladros parametrizados adicionales. Contornos circulares en vistas y DXF.


Preparación final de unión incluida; luz nominal 2 mm. Ver registro JF y DXF.

P158 | CANT. 1


CUELLO_CAPTACION_SUP_DN150_AISI304_L200

AISI 304 | ENVOLVENTE LOCAL X/Y/Z: 154 x 154 x 200


XY / escala 1:4

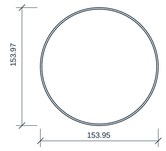

XZ / escala 1:4

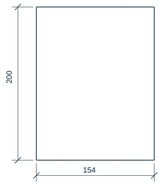

YZ / escala 1:4

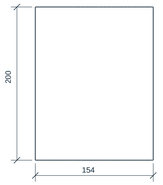


TORNEADO / TUBO: exterior Ø154, pared 2, longitud 200.
Sin taladros parametrizados adicionales. Contornos circulares en vistas y DXF.

P159 | CANT. 4

AC_CAP_120x120x12

ASTM A36 | ENVOLVENTE LOCAL X/Y/Z: 120 x 120 x 12


XY / escala 1:2

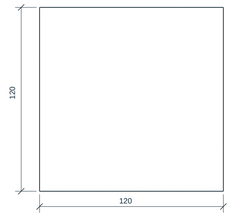

XZ / escala 1:1 / INTERRUMPIDA



YZ / escala 1:1 / INTERRUMPIDA

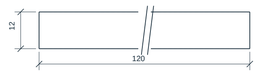


CHAPA: espesor 12. Contorno nominal CAD; corte y taladros se identifican por coordenadas locales.
Sin taladros parametrizados adicionales. Contornos circulares en vistas y DXF.

P160 | CANT. 18

AC_CARTELA_150x150x6

ASTM A36 | ENVOLVENTE LOCAL X/Y/Z: 150 x 150 x 6

XY / escala 1:4

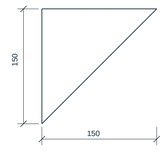

XZ / escala 1:1 / INTERRUMPIDA



YZ / escala 1:1 / INTERRUMPIDA



CHAPA: espesor 6. Contorno nominal CAD; corte y taladros se identifican por coordenadas locales.
Sin taladros parametrizados adicionales. Contornos circulares en vistas y DXF.

Cotas en mm. Unidades y referencias locales X/Y/Z. Las vistas de detalle y DXF son proyecciones del CAD exacto OpenCascade; no se atribuye exportación nativa de SolidWorks a estas láminas.

Tolerancias ISO 2768-1 clase m en cotas lineales/angulares de piezas mecanizadas sin tolerancia individual. No se aplica a ajustes, soldaduras, equipos comerciales ni dimensiones de montaje críticas.

No escalar el PDF. Taladrar/escariar y desbarbar; eliminar aristas cortantes. Las preparaciones con luz 2 mm conservan geometría CAD; ejecutar soldadura únicamente según cuadro de juntas y WPS aplicable.

Acabados, ajustes y aceptación de uniones: según memoria, detalle específico y programa de inspección. Los espacios de verificación/aprobación permanecen sin firma.

Fuente: native_manifest.json + solidworks_model.bas; geometría y coordenadas íntegramente trazadas.

P05 - PLANOS DE DETALLE PARA REVISIÓN TÉCNICA

ESTACIÓN BIGBAG							**P05**
SESUVECA DEL PERÚ							
						DESPIECE DE FABRICACIÓN / COTAS LOCALES	
DIBUJ.	PROYECTO P05		16/10/2026				
VERIF.							
APROB.							
FABR.							
CALID.				MATERIAL: SEGÚN DESPIECE		**ESTACIÓN DE DESCARGA BIGBAG**	**A1**
PESO: BOM / CAD				ESCALA: INDICADA		**P05-T-033**	HOJA 33/51

DESPIECE DE FABRICACIÓN / COTAS LOCALES


Detalles 133..136 de 175 componentes fabricados. Proyecciones exactas de la geometría final.

P161 | CANT. 3

AC_SHS80x80x4_L2578590

ASTM A500 Gr B | ENVOLVENTE LOCAL X/Y/Z: 80 x 80 x 2578.59

XY / escala 1:2

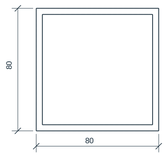

XZ / escala 1:10 / INTERRUMPIDA



YZ / escala 1:10 / INTERRUMPIDA




PERFIL SHS80x80x4; longitud nominal 2578.59. Preparaciones y recortes finales en vistas/DXF.
Sin taladros parametrizados adicionales. Contornos circulares en vistas y DXF.

P162 | CANT. 1

AC_SHS80x80x4_L2570590

ASTM A500 Gr B | ENVOLVENTE LOCAL X/Y/Z: 80 x 80 x 2570.59

XY / escala 1:2

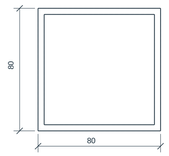

XZ / escala 1:10 / INTERRUMPIDA



YZ / escala 1:10 / INTERRUMPIDA




PERFIL SHS80x80x4; longitud nominal 2570.59. Preparaciones y recortes finales en vistas/DXF.
Sin taladros parametrizados adicionales. Contornos circulares en vistas y DXF.

P163 | CANT. 2

AC_RHS150x75x5_L1780000

ASTM A500 Gr B | ENVOLVENTE LOCAL X/Y/Z: 75 x 150 x 1780


XY / escala 1:4

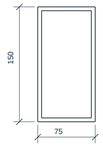

XZ / escala 1:10 / INTERRUMPIDA



YZ / escala 1:10 / INTERRUMPIDA

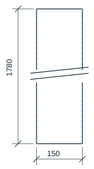


PERFIL RHS150x75x5; longitud nominal 1780. Preparaciones y recortes finales en vistas/DXF.
Sin taladros parametrizados adicionales. Contornos circulares en vistas y DXF.

P164 | CANT. 1


AC_RHS150x75x5_L1620000

ASTM A500 Gr B | ENVOLVENTE LOCAL X/Y/Z: 75 x 150 x 1620

XY / escala 1:4

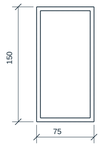

XZ / escala 1:10 / INTERRUMPIDA

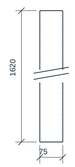

YZ / escala 1:10 / INTERRUMPIDA



PERFIL RHS150x75x5; longitud nominal 1620. Preparaciones y recortes finales en vistas/DXF.
Sin taladros parametrizados adicionales. Contornos circulares en vistas y DXF.

Cotas en mm. Unidades y referencias locales X/Y/Z. Las vistas de detalle y DXF son proyecciones del CAD exacto OpenCascade; no se atribuye exportación nativa de SolidWorks a estas láminas.

Tolerancias ISO 2768-1 clase m en cotas lineales/angulares de piezas mecanizadas sin tolerancia individual. No se aplica a ajustes, soldaduras, equipos comerciales ni dimensiones de montaje críticas.

No escalar el PDF. Taladrar/escariar y desbarbar; eliminar aristas cortantes. Las preparaciones con luz 2 mm conservan geometría CAD; ejecutar soldadura únicamente según cuadro de juntas y WPS aplicable.

Acabados, ajustes y aceptación de uniones: según memoria, detalle específico y programa de inspección. Los espacios de verificación/aprobación permanecen sin firma.

Fuente: native_manifest.json + solidworks_model.bas; geometría y coordenadas íntegramente trazadas.

P05 - PLANOS DE DETALLE PARA REVISIÓN TÉCNICA

ESTACIÓN BIGBAG							**P05**
SESUVECA DEL PERÚ							
						DESPIECE DE FABRICACIÓN / COTAS LOCALES	
DIBUJ.	PROYECTO P05		16/10/2026				
VERIF.							
APROB.							
FABR.							
CALID.				MATERIAL: SEGÚN DESPIECE		**ESTACIÓN DE DESCARGA BIGBAG**	**A1**
PESO: BOM / CAD				ESCALA: INDICADA		**P05-T-034**	HOJA 34/51

DESPIECE DE FABRICACIÓN / COTAS LOCALES


Detalles 137..140 de 175 componentes fabricados. Proyecciones exactas de la geometría final.

P165 | CANT. 5


AC_SHS60x60x4_L725000

ASTM A500 Gr B | ENVOLVENTE LOCAL X/Y/Z: 60 x 60 x 725


XY / escala 1:1

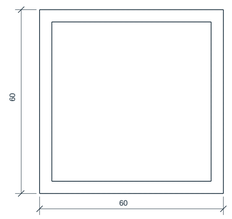

XZ / escala 1:4 / INTERRUMPIDA

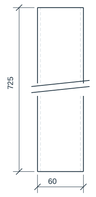

YZ / escala 1:4 / INTERRUMPIDA

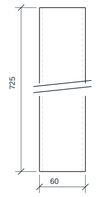


PERFIL SHS60x60x4; longitud nominal 725. Preparaciones y recortes finales en vistas/DXF.
Sin taladros parametrizados adicionales. Contornos circulares en vistas y DXF.

P166 | CANT. 5


AC_RHS150x75x5_L105000

ASTM A500 Gr B | ENVOLVENTE LOCAL X/Y/Z: 75 x 150 x 105


XY / escala 1:4

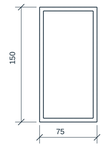

XZ / escala 1:2

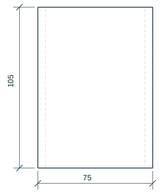

YZ / escala 1:2

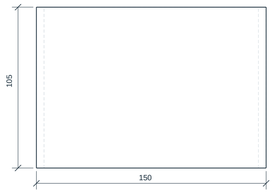


PERFIL RHS150x75x5; longitud nominal 105. Preparaciones y recortes finales en vistas/DXF.
Sin taladros parametrizados adicionales. Contornos circulares en vistas y DXF.

P167 | CANT. 2

AC_SHS60x60x4_L2914334

ASTM A500 Gr B | ENVOLVENTE LOCAL X/Y/Z: 60 x 60 x 2914.33


XY / escala 1:1

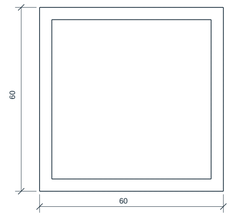

XZ / escala 1:10 / INTERRUMPIDA



YZ / escala 1:10 / INTERRUMPIDA

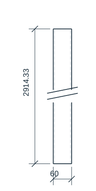


PERFIL SHS60x60x4; longitud nominal 2914.33. Preparaciones y recortes finales en vistas/DXF.
Sin taladros parametrizados adicionales. Contornos circulares en vistas y DXF.

P170 | CANT. 2


AC_RHS150x75x5_L4568118_17c97d

ASTM A500 Gr B | ENVOLVENTE LOCAL X/Y/Z: 75 x 150 x 4728.12


XY / escala 1:4

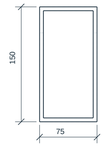

XZ / escala 1:10 / INTERRUMPIDA

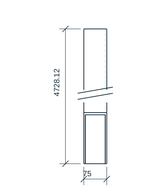

YZ / escala 1:10 / INTERRUMPIDA

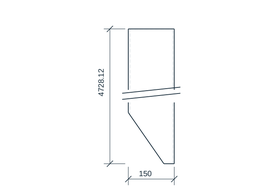

PERFIL RHS150x75x5; longitud nominal 4568.12. Preparaciones y recortes finales en vistas/DXF.
Sin taladros parametrizados adicionales. Contornos circulares en vistas y DXF.

Cotas en mm. Unidades y referencias locales X/Y/Z. Las vistas de detalle y DXF son proyecciones del CAD exacto OpenCascade; no se atribuye exportación nativa de SolidWorks a estas láminas.

Tolerancias ISO 2768-1 clase m en cotas lineales/angulares de piezas mecanizadas sin tolerancia individual. No se aplica a ajustes, soldaduras, equipos comerciales ni dimensiones de montaje críticas.

No escalar el PDF. Taladrar/escariar y desbarbar; eliminar aristas cortantes. Las preparaciones con luz 2 mm conservan geometría CAD; ejecutar soldadura únicamente según cuadro de juntas y WPS aplicable.

Acabados, ajustes y aceptación de uniones: según memoria, detalle específico y programa de inspección. Los espacios de verificación/aprobación permanecen sin firma.

Fuente: native_manifest.json + solidworks_model.bas; geometría y coordenadas íntegramente trazadas.

P05 - PLANOS DE DETALLE PARA REVISIÓN TÉCNICA

ESTACIÓN BIGBAG							**P05**
SESUVECA DEL PERÚ				SESUVECA DEL PERÚ			
						DESPIECE DE FABRICACIÓN / COTAS LOCALES	
DIBUJ.	PROYECTO P05		16/10/2026				
VERIF.							
APROB.							
FABR.							
CALID.				MATERIAL: SEGÚN DESPIECE		**ESTACIÓN DE DESCARGA BIGBAG**	**A1**
PESO: BOM / CAD				ESCALA: INDICADA		**P05-T-035**	HOJA 35/51

DESPIECE DE FABRICACIÓN / COTAS LOCALES


Detalles 141..144 de 175 componentes fabricados. Proyecciones exactas de la geometría final.

P171 | CANT. 2


AC_UNION_ZANCA_200x160x12

ASTM A36 | ENVOLVENTE LOCAL X/Y/Z: 200 x 160 x 12


XY / escala 1:4

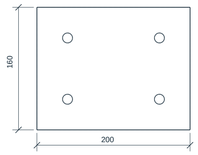

XZ / escala 1:1 / INTERRUMPIDA

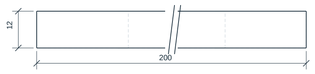

YZ / escala 1:1 / INTERRUMPIDA

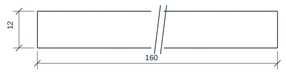


CHAPA: espesor 12. Contorno nominal CAD; corte y taladros se identifican por coordenadas locales.
TALADROS / EJES: ID - Ø - X - Y - Z - DIRECCIÓN (mm)
T1 / 13 / -60 / -40 / 0 / Z
T2 / 13 / 60 / -40 / 0 / Z
T3 / 13 / 60 / 40 / 0 / Z
T4 / 13 / -60 / 40 / 0 / Z

P172 | CANT. 30

AC_SHS40x40x3_L800000

ASTM A500 Gr B | ENVOLVENTE LOCAL X/Y/Z: 40 x 40 x 800

XY / escala 1:1

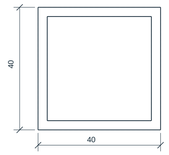

XZ / escala 1:4 / INTERRUMPIDA



YZ / escala 1:4 / INTERRUMPIDA




PERFIL SHS40x40x3; longitud nominal 800. Preparaciones y recortes finales en vistas/DXF.
Sin taladros parametrizados adicionales. Contornos circulares en vistas y DXF.

P173 | CANT. 6


AC_BASE_BARANDA_110x110x20

ASTM A36 | ENVOLVENTE LOCAL X/Y/Z: 110 x 110 x 20


XY / escala 1:2

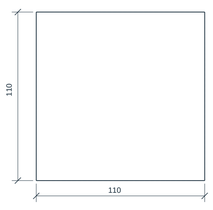

XZ / escala 1:1 / INTERRUMPIDA

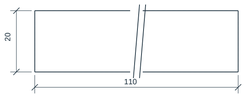

YZ / escala 1:1 / INTERRUMPIDA

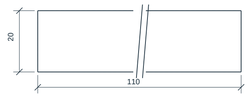


CHAPA: espesor 20. Contorno nominal CAD; corte y taladros se identifican por coordenadas locales.
Sin taladros parametrizados adicionales. Contornos circulares en vistas y DXF.

P174 | CANT. 6

AC_CHS60p3x3p91_L1085850

ASTM A53 Gr B | ENVOLVENTE LOCAL X/Y/Z: 60.3 x 60.3 x 1085.85

XY / escala 1:1

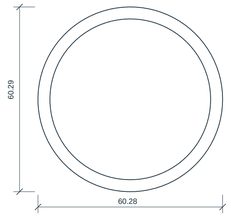

XZ / escala 1:5 / INTERRUMPIDA



YZ / escala 1:5 / INTERRUMPIDA



PERFIL CHS60p3x3p91; longitud nominal 1085.85. Preparaciones y recortes finales en vistas/DXF.
Sin taladros parametrizados adicionales. Contornos circulares en vistas y DXF.

Cotas en mm. Unidades y referencias locales X/Y/Z. Las vistas de detalle y DXF son proyecciones del CAD exacto OpenCascade; no se atribuye exportación nativa de SolidWorks a estas láminas.

Tolerancias ISO 2768-1 clase m en cotas lineales/angulares de piezas mecanizadas sin tolerancia individual. No se aplica a ajustes, soldaduras, equipos comerciales ni dimensiones de montaje críticas.

No escalar el PDF. Taladrar/escariar y desbarbar; eliminar aristas cortantes. Las preparaciones con luz 2 mm conservan geometría CAD; ejecutar soldadura únicamente según cuadro de juntas y WPS aplicable.

Acabados, ajustes y aceptación de uniones: según memoria, detalle específico y programa de inspección. Los espacios de verificación/aprobación permanecen sin firma.

Fuente: native_manifest.json + solidworks_model.bas; geometría y coordenadas íntegramente trazadas.

DESPIECE DE FABRICACIÓN / COTAS LOCALES


Detalles 145..148 de 175 componentes fabricados. Proyecciones exactas de la geometría final.

P175 | CANT. 2

AC_CHS48p3x3p68_L1520000

ASTM A53 Gr B | ENVOLVENTE LOCAL X/Y/Z: 48.3 x 48.3 x 1520

XY / escala 1:1

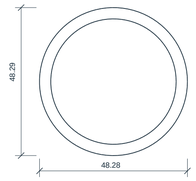

XZ / escala 1:10 / INTERRUMPIDA



YZ / escala 1:10 / INTERRUMPIDA




PERFIL CHS48p3x3p68; longitud nominal 1520. Preparaciones y recortes finales en vistas/DXF.
Sin taladros parametrizados adicionales. Contornos circulares en vistas y DXF.

P176 | CANT. 2

AC_CHS48p3x3p68_L1005000

ASTM A53 Gr B | ENVOLVENTE LOCAL X/Y/Z: 48.3 x 48.3 x 1005


XY / escala 1:1

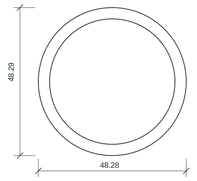

XZ / escala 1:4 / INTERRUMPIDA



YZ / escala 1:4 / INTERRUMPIDA

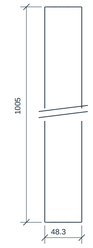


PERFIL CHS48p3x3p68; longitud nominal 1005. Preparaciones y recortes finales en vistas/DXF.
Sin taladros parametrizados adicionales. Contornos circulares en vistas y DXF.

P177 | CANT. 2

AC_CHS48p3x3p68_L620000

ASTM A53 Gr B | ENVOLVENTE LOCAL X/Y/Z: 48.3 x 48.3 x 620


XY / escala 1:1

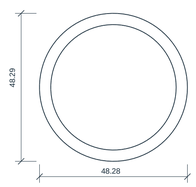

XZ / escala 1:4 / INTERRUMPIDA



YZ / escala 1:4 / INTERRUMPIDA

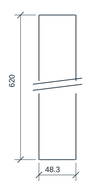

PERFIL CHS48p3x3p68; longitud nominal 620. Preparaciones y recortes finales en vistas/DXF.
Sin taladros parametrizados adicionales. Contornos circulares en vistas y DXF.

P178 | CANT. 1

AC_PROTECCION_INFERIOR_1700x500x3

ASTM A36 | ENVOLVENTE LOCAL X/Y/Z: 1700 x 500 x 3

XY / escala 1:20



XZ / escala 1:5 / INTERRUMPIDA



YZ / escala 1:2 / INTERRUMPIDA



CHAPA: espesor 3. Contorno nominal CAD; corte y taladros se identifican por coordenadas locales.
Sin taladros parametrizados adicionales. Contornos circulares en vistas y DXF.

Cotas en mm. Unidades y referencias locales X/Y/Z. Las vistas de detalle y DXF son proyecciones del CAD exacto OpenCascade; no se atribuye exportación nativa de SolidWorks a estas láminas.

Tolerancias ISO 2768-1 clase m en cotas lineales/angulares de piezas mecanizadas sin tolerancia individual. No se aplica a ajustes, soldaduras, equipos comerciales ni dimensiones de montaje críticas.

No escalar el PDF. Taladrar/escariar y desbarbar; eliminar aristas cortantes. Las preparaciones con luz 2 mm conservan geometría CAD; ejecutar soldadura únicamente según cuadro de juntas y WPS aplicable.

Acabados, ajustes y aceptación de uniones: según memoria, detalle específico y programa de inspección. Los espacios de verificación/aprobación permanecen sin firma.

Fuente: native_manifest.json + solidworks_model.bas; geometría y coordenadas íntegramente trazadas.

P05 - PLANOS DE DETALLE PARA REVISIÓN TÉCNICA

ESTACIÓN BIGBAG							**P05**
SESUVECA DEL PERÚ							
						DESPIECE DE FABRICACIÓN / COTAS LOCALES	
DIBUJ.	PROYECTO P05		16/10/2026				
VERIF.							
APROB.							
FABR.							
CALID.				MATERIAL: SEGÚN DESPIECE		**ESTACIÓN DE DESCARGA BIGBAG**	**A1**
PESO: BOM / CAD				ESCALA: INDICADA		**P05-T-037**	HOJA 37/51

DESPIECE DE FABRICACIÓN / COTAS LOCALES


Detalles 149..152 de 175 componentes fabricados. Proyecciones exactas de la geometría final.

P179 | CANT. 1

AC_RODAPIE_1700x150x6

ASTM A36 | ENVOLVENTE LOCAL X/Y/Z: 1700 x 150 x 6


XY / escala 1:5 / INTERRUMPIDA

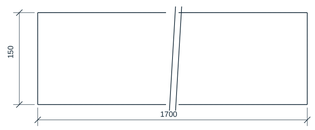

XZ / escala 1:5 / INTERRUMPIDA



YZ / escala 1:1 / INTERRUMPIDA

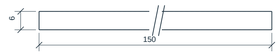


CHAPA: espesor 6. Contorno nominal CAD; corte y taladros se identifican por coordenadas locales.
Sin taladros parametrizados adicionales. Contornos circulares en vistas y DXF.

P180 | CANT. 1

AC_RODAPIE_1190x150x6

ASTM A36 | ENVOLVENTE LOCAL X/Y/Z: 1190 x 150 x 6

XY / escala 1:4 / INTERRUMPIDA

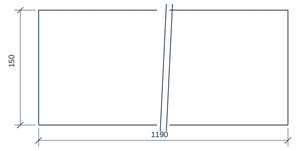

XZ / escala 1:4 / INTERRUMPIDA



YZ / escala 1:1 / INTERRUMPIDA




CHAPA: espesor 6. Contorno nominal CAD; corte y taladros se identifican por coordenadas locales.
Sin taladros parametrizados adicionales. Contornos circulares en vistas y DXF.

P181 | CANT. 2


AC_CHS48p3x3p68_L800000

ASTM A53 Gr B | ENVOLVENTE LOCAL X/Y/Z: 48.3 x 48.3 x 800


XY / escala 1:1

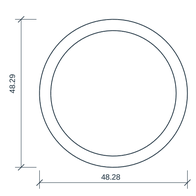

XZ / escala 1:4 / INTERRUMPIDA

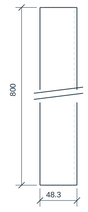

YZ / escala 1:4 / INTERRUMPIDA

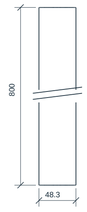


PERFIL CHS48p3x3p68; longitud nominal 800. Preparaciones y recortes finales en vistas/DXF.
Sin taladros parametrizados adicionales. Contornos circulares en vistas y DXF.

P182 | CANT. 2

AC_CHS48p3x3p68_L503400

ASTM A53 Gr B | ENVOLVENTE LOCAL X/Y/Z: 48.3 x 48.3 x 503.4

XY / escala 1:1

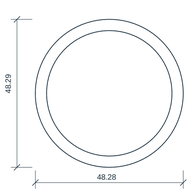

XZ / escala 1:4 / INTERRUMPIDA



YZ / escala 1:4 / INTERRUMPIDA



PERFIL CHS48p3x3p68; longitud nominal 503.4. Preparaciones y recortes finales en vistas/DXF.
Sin taladros parametrizados adicionales. Contornos circulares en vistas y DXF.

Cotas en mm. Unidades y referencias locales X/Y/Z. Las vistas de detalle y DXF son proyecciones del CAD exacto OpenCascade; no se atribuye exportación nativa de SolidWorks a estas láminas.

Tolerancias ISO 2768-1 clase m en cotas lineales/angulares de piezas mecanizadas sin tolerancia individual. No se aplica a ajustes, soldaduras, equipos comerciales ni dimensiones de montaje críticas.

No escalar el PDF. Taladrar/escariar y desbarbar; eliminar aristas cortantes. Las preparaciones con luz 2 mm conservan geometría CAD; ejecutar soldadura únicamente según cuadro de juntas y WPS aplicable.

Acabados, ajustes y aceptación de uniones: según memoria, detalle específico y programa de inspección. Los espacios de verificación/aprobación permanecen sin firma.

Fuente: native_manifest.json + solidworks_model.bas; geometría y coordenadas íntegramente trazadas.

P05 - PLANOS DE DETALLE PARA REVISIÓN TÉCNICA

ESTACIÓN BIGBAG							**P05**
SESUVECA DEL PERÚ							
						DESPIECE DE FABRICACIÓN / COTAS LOCALES	
DIBUJ.	PROYECTO P05		16/10/2026				
VERIF.							
APROB.							
FABR.							
CALID.				MATERIAL: SEGÚN DESPIECE		**ESTACIÓN DE DESCARGA BIGBAG**	**A1**
PESO: BOM / CAD				ESCALA: INDICADA		**P05-T-038**	HOJA 38/51

DESPIECE DE FABRICACIÓN / COTAS LOCALES

Detalles 153..156 de 175 componentes fabricados. Proyecciones exactas de la geometría final.

P183 | CANT. 1

AC_PUERTA_PANEL_720x520x3

ASTM A36 | ENVOLVENTE LOCAL X/Y/Z: 720 x 520 x 3

XY / escala 1:10



XZ / escala 1:4 / INTERRUMPIDA



YZ / escala 1:2 / INTERRUMPIDA




CHAPA: espesor 3. Contorno nominal CAD; corte y taladros se identifican por coordenadas locales.
Sin taladros parametrizados adicionales. Contornos circulares en vistas y DXF.

P184 | CANT. 1

AC_SHS40x40x3_L1725000

ASTM A500 Gr B | ENVOLVENTE LOCAL X/Y/Z: 40 x 40 x 1725

XY / escala 1:1

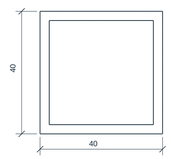

XZ / escala 1:10 / INTERRUMPIDA



YZ / escala 1:10 / INTERRUMPIDA



PERFIL SHS40x40x3; longitud nominal 1725. Preparaciones y recortes finales en vistas/DXF.
Sin taladros parametrizados adicionales. Contornos circulares en vistas y DXF.

P186 | CANT. 2

AC_PUERTA_COLGADOR_30x100x6

ASTM A36 | ENVOLVENTE LOCAL X/Y/Z: 30 x 100 x 6

XY / escala 1:2



XZ / escala 2:1



YZ / escala 1:1 / INTERRUMPIDA




CHAPA: espesor 6. Contorno nominal CAD; corte y taladros se identifican por coordenadas locales.
TALADROS / EJES: ID - Ø - X - Y - Z - DIRECCIÓN (mm)
T1 / 12 / 0 / 30 / 0 / Z

P189 | CANT. 4

AC_CHS60p3x3p91_L1095800_637020

ASTM A53 Gr B | ENVOLVENTE LOCAL X/Y/Z: 60.3 x 60.3 x 1137.75

XY / escala 1:1

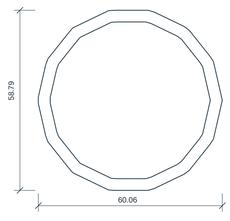

XZ / escala 1:5 / INTERRUMPIDA



YZ / escala 1:5 / INTERRUMPIDA



PERFIL CHS60p3x3p91; longitud nominal 1095.8. Preparaciones y recortes finales en vistas/DXF.
Sin taladros parametrizados adicionales. Contornos circulares en vistas y DXF.

Cotas en mm. Unidades y referencias locales X/Y/Z. Las vistas de detalle y DXF son proyecciones del CAD exacto OpenCascade; no se atribuye exportación nativa de SolidWorks a estas láminas.

Tolerancias ISO 2768-1 clase m en cotas lineales/angulares de piezas mecanizadas sin tolerancia individual. No se aplica a ajustes, soldaduras, equipos comerciales ni dimensiones de montaje críticas.

No escalar el PDF. Taladrar/escariar y desbarbar; eliminar aristas cortantes. Las preparaciones con luz 2 mm conservan geometría CAD; ejecutar soldadura únicamente según cuadro de juntas y WPS aplicable.

Acabados, ajustes y aceptación de uniones: según memoria, detalle específico y programa de inspección. Los espacios de verificación/aprobación permanecen sin firma.

Fuente: native_manifest.json + solidworks_model.bas; geometría y coordenadas íntegramente trazadas.

ESTACIÓN BIGBAG							**P05**
SESUVECA DEL PERÚ							
						DESPIECE DE FABRICACIÓN / COTAS LOCALES	
DIBUJ.	PROYECTO P05		16/10/2026				
VERIF.							
APROB.							
FABR.							
CALID.				MATERIAL: SEGÚN DESPIECE		**ESTACIÓN DE DESCARGA BIGBAG**	**A1**
PESO: BOM / CAD				ESCALA: INDICADA		**P05-T-039**	HOJA 39/51

DESPIECE DE FABRICACIÓN / COTAS LOCALES


Detalles 157..160 de 175 componentes fabricados. Proyecciones exactas de la geometría final.

P190 | CANT. 2

AC_CHS60p3x3p91_L1095800_df7763

ASTM A53 Gr B | ENVOLVENTE LOCAL X/Y/Z: 60.3 x 60.3 x 1137.75

XY / escala 1:1

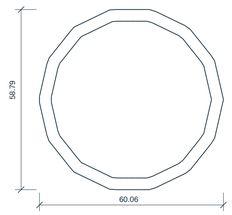

XZ / escala 1:5 / INTERRUMPIDA



YZ / escala 1:5 / INTERRUMPIDA




PERFIL CHS60p3x3p91; longitud nominal 1095.8. Preparaciones y recortes finales en vistas/DXF.
Sin taladros parametrizados adicionales. Contornos circulares en vistas y DXF.

P191 | CANT. 4

AC_CHS60p3x3p91_L1095800_0965d8

ASTM A53 Gr B | ENVOLVENTE LOCAL X/Y/Z: 60.3 x 60.3 x 1137.75


XY / escala 1:1

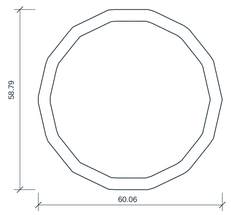

XZ / escala 1:5 / INTERRUMPIDA



YZ / escala 1:5 / INTERRUMPIDA

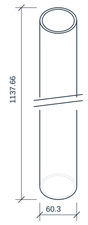


PERFIL CHS60p3x3p91; longitud nominal 1095.8. Preparaciones y recortes finales en vistas/DXF.
Sin taladros parametrizados adicionales. Contornos circulares en vistas y DXF.

P192 | CANT. 6

AC_CHS48p3x3p68_L4568118

ASTM A53 Gr B | ENVOLVENTE LOCAL X/Y/Z: 48.3 x 48.3 x 4568.12

XY / escala 1:1

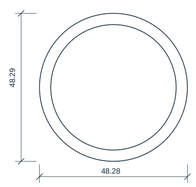

XZ / escala 1:10 / INTERRUMPIDA



YZ / escala 1:10 / INTERRUMPIDA



PERFIL CHS48p3x3p68; longitud nominal 4568.12. Preparaciones y recortes finales en vistas/DXF.
Sin taladros parametrizados adicionales. Contornos circulares en vistas y DXF.

P193 | CANT. 4

HR4_PAD_100x40x5_P05_EJE_POSITIVO

ASTM A36 | ENVOLVENTE LOCAL X/Y/Z: 100 x 40 x 5

XY / escala 1:2



XZ / escala 1:1 / INTERRUMPIDA



YZ / escala 2:1



CHAPA: espesor 5. Contorno nominal CAD; corte y taladros se identifican por coordenadas locales.
Sin taladros parametrizados adicionales. Contornos circulares en vistas y DXF.

Cotas en mm. Unidades y referencias locales X/Y/Z. Las vistas de detalle y DXF son proyecciones del CAD exacto OpenCascade; no se atribuye exportación nativa de SolidWorks a estas láminas.

Tolerancias ISO 2768-1 clase m en cotas lineales/angulares de piezas mecanizadas sin tolerancia individual. No se aplica a ajustes, soldaduras, equipos comerciales ni dimensiones de montaje críticas.

No escalar el PDF. Taladrar/escariar y desbarbar; eliminar aristas cortantes. Las preparaciones con luz 2 mm conservan geometría CAD; ejecutar soldadura únicamente según cuadro de juntas y WPS aplicable.

Acabados, ajustes y aceptación de uniones: según memoria, detalle específico y programa de inspección. Los espacios de verificación/aprobación permanecen sin firma.

Fuente: native_manifest.json + solidworks_model.bas; geometría y coordenadas íntegramente trazadas.

P05 - PLANOS DE DETALLE PARA REVISIÓN TÉCNICA

ESTACIÓN BIGBAG							**P05**
SESUVECA DEL PERÚ							
						DESPIECE DE FABRICACIÓN / COTAS LOCALES	
DIBUJ.	PROYECTO P05		16/10/2026				
VERIF.							
APROB.							
FABR.							
CALID.				MATERIAL: SEGÚN DESPIECE		**ESTACIÓN DE DESCARGA BIGBAG**	**A1**
PESO: BOM / CAD				ESCALA: INDICADA		**P05-T-040**	HOJA 40/51

DESPIECE DE FABRICACIÓN / COTAS LOCALES


Detalles 161..164 de 175 componentes fabricados. Proyecciones exactas de la geometría final.

P194 | CANT. 15

AC_PUENTE_REJILLA_SHS40x40x3_L170_P05

ASTM A500 Gr B | ENVOLVENTE LOCAL X/Y/Z: 40 x 40 x 170

XY / escala 1:1

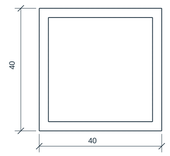

XZ / escala 1:4



YZ / escala 1:4




PERFIL SHS40x40x3; longitud nominal 170. Preparaciones y recortes finales en vistas/DXF.
Sin taladros parametrizados adicionales. Contornos circulares en vistas y DXF.

P196 | CANT. 2


CALCE_PASANTE_BASE_TOLVA_250x250x25_t10

ASTM A36 | ENVOLVENTE LOCAL X/Y/Z: 250 x 250 x 10

XY / escala 1:4

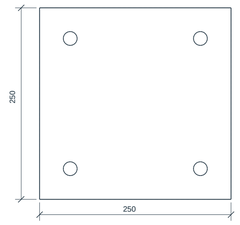

XZ / escala 1:2 / INTERRUMPIDA

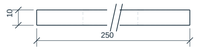

YZ / escala 1:2 / INTERRUMPIDA




CHAPA: espesor 10. Contorno nominal CAD; corte y taladros se identifican por coordenadas locales.
TALADROS / EJES: ID - Ø - X - Y - Z - DIRECCIÓN (mm)
T1 / 18 / -85 / -85 / 0 / Z
T2 / 18 / -85 / 85 / 0 / Z
T3 / 18 / 85 / -85 / 0 / Z
T4 / 18 / 85 / 85 / 0 / Z

P197 | CANT. 2


TOPE_PLACA_REACCION_640x360x45_P05

A36 | ENVOLVENTE LOCAL X/Y/Z: 640 x 360 x 45


XY / escala 1:10

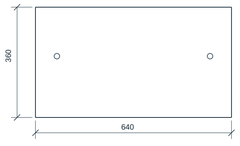

XZ / escala 1:2 / INTERRUMPIDA

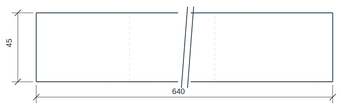

YZ / escala 1:2 / INTERRUMPIDA

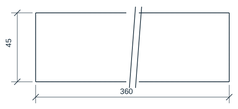

CHAPA: espesor 45. Contorno nominal CAD; corte y taladros se identifican por coordenadas locales.
TALADROS / EJES: ID - Ø - X - Y - Z - DIRECCIÓN (mm)
T1 / 18 / -250 / 20 / 0 / Z
T2 / 18 / 250 / 20 / 0 / Z

P198 | CANT. 4


TOPE_RIGIDIZADOR_TERMINAL_100x240x12_P05

ASTM A36 Fy250 | ENVOLVENTE LOCAL X/Y/Z: 100 x 240 x 12


XY / escala 1:4



XZ / escala 1:1 / INTERRUMPIDA

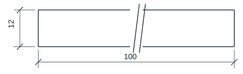

YZ / escala 1:1 / INTERRUMPIDA

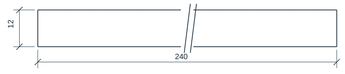

CHAPA: espesor 12. Contorno nominal CAD; corte y taladros se identifican por coordenadas locales.
Sin taladros parametrizados adicionales. Contornos circulares en vistas y DXF.

Cotas en mm. Unidades y referencias locales X/Y/Z. Las vistas de detalle y DXF son proyecciones del CAD exacto OpenCascade; no se atribuye exportación nativa de SolidWorks a estas láminas.

Tolerancias ISO 2768-1 clase m en cotas lineales/angulares de piezas mecanizadas sin tolerancia individual. No se aplica a ajustes, soldaduras, equipos comerciales ni dimensiones de montaje críticas.

No escalar el PDF. Taladrar/escariar y desbarbar; eliminar aristas cortantes. Las preparaciones con luz 2 mm conservan geometría CAD; ejecutar soldadura únicamente según cuadro de juntas y WPS aplicable.

Acabados, ajustes y aceptación de uniones: según memoria, detalle específico y programa de inspección. Los espacios de verificación/aprobación permanecen sin firma.

Fuente: native_manifest.json + solidworks_model.bas; geometría y coordenadas íntegramente trazadas.

P05 - PLANOS DE DETALLE PARA REVISIÓN TÉCNICA

ESTACIÓN BIGBAG							**P05**
SESUVECA DEL PERÚ							
						DESPIECE DE FABRICACIÓN / COTAS LOCALES	
DIBUJ.	PROYECTO P05		16/10/2026				
VERIF.							
APROB.							
FABR.							
CALID.				MATERIAL: SEGÚN DESPIECE		**ESTACIÓN DE DESCARGA BIGBAG**	**A1**
PESO: BOM / CAD				ESCALA: INDICADA		**P05-T-041**	HOJA 41/51

DESPIECE DE FABRICACIÓN / COTAS LOCALES


Detalles 165..168 de 175 componentes fabricados. Proyecciones exactas de la geometría final.

P199 | CANT. 104

PASANTE_ARANDELA_A36_50x50x10_D18_P05

ASTM A36 | ENVOLVENTE LOCAL X/Y/Z: 50 x 50 x 10

XY / escala 1:1

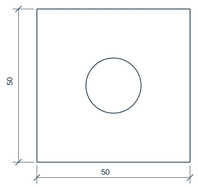

XZ / escala 1:1



YZ / escala 1:1




CHAPA: espesor 10. Contorno nominal CAD; corte y taladros se identifican por coordenadas locales.
TALADROS / EJES: ID - Ø - X - Y - Z - DIRECCIÓN (mm)
T1 / 18 / 0 / 0 / 0 / Z

P201 | CANT. 5


AC_BASE_220x220x12

ASTM A36 | ENVOLVENTE LOCAL X/Y/Z: 220 x 220 x 12

XY / escala 1:4

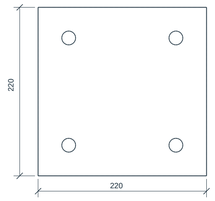

XZ / escala 1:1 / INTERRUMPIDA

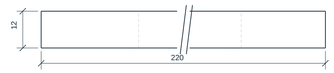

YZ / escala 1:1 / INTERRUMPIDA




CHAPA: espesor 12. Contorno nominal CAD; corte y taladros se identifican por coordenadas locales.
TALADROS / EJES: ID - Ø - X - Y - Z - DIRECCIÓN (mm)
T1 / 18 / -70 / -70 / 0 / Z
T2 / 18 / 70 / -70 / 0 / Z
T3 / 18 / 70 / 70 / 0 / Z
T4 / 18 / -70 / 70 / 0 / Z

P202 | CANT. 5


CALCE_PASANTE_AC_BASE_220x220x12_t35

ASTM A36 | ENVOLVENTE LOCAL X/Y/Z: 220 x 220 x 35


XY / escala 1:4

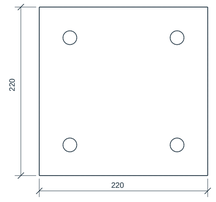

XZ / escala 1:1 / INTERRUMPIDA

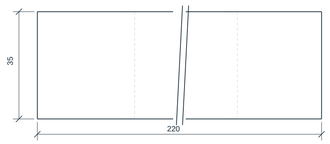

YZ / escala 1:1 / INTERRUMPIDA

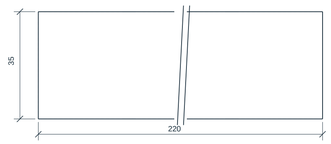


CHAPA: espesor 35. Contorno nominal CAD; corte y taladros se identifican por coordenadas locales.
TALADROS / EJES: ID - Ø - X - Y - Z - DIRECCIÓN (mm)
T1 / 18 / -70 / -70 / 0 / Z
T2 / 18 / 70 / -70 / 0 / Z
T3 / 18 / 70 / 70 / 0 / Z
T4 / 18 / -70 / 70 / 0 / Z

P203 | CANT. 1


CONTRAPLACA_COMUN_A36_290x290x18_G01_P05

ASTM A36 | ENVOLVENTE LOCAL X/Y/Z: 290 x 290 x 18


XY / escala 1:4

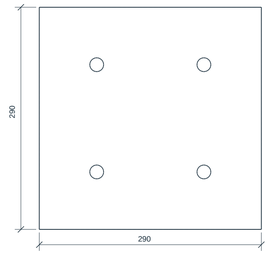

XZ / escala 1:2 / INTERRUMPIDA

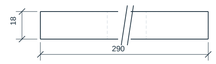

YZ / escala 1:2 / INTERRUMPIDA

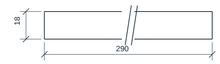

CHAPA: espesor 18. Contorno nominal CAD; corte y taladros se identifican por coordenadas locales.
TALADROS / EJES: ID - Ø - X - Y - Z - DIRECCIÓN (mm)
T1 / 18 / -70 / -70 / 0 / Z
T2 / 18 / -70 / 70 / 0 / Z
T3 / 18 / 70 / -70 / 0 / Z
T4 / 18 / 70 / 70 / 0 / Z

Cotas en mm. Unidades y referencias locales X/Y/Z. Las vistas de detalle y DXF son proyecciones del CAD exacto OpenCascade; no se atribuye exportación nativa de SolidWorks a estas láminas.

Tolerancias ISO 2768-1 clase m en cotas lineales/angulares de piezas mecanizadas sin tolerancia individual. No se aplica a ajustes, soldaduras, equipos comerciales ni dimensiones de montaje críticas.

No escalar el PDF. Taladrar/escariar y desbarbar; eliminar aristas cortantes. Las preparaciones con luz 2 mm conservan geometría CAD; ejecutar soldadura únicamente según cuadro de juntas y WPS aplicable.

Acabados, ajustes y aceptación de uniones: según memoria, detalle específico y programa de inspección. Los espacios de verificación/aprobación permanecen sin firma.

Fuente: native_manifest.json + solidworks_model.bas; geometría y coordenadas íntegramente trazadas.

P05 - PLANOS DE DETALLE PARA REVISIÓN TÉCNICA

ESTACIÓN BIGBAG							**P05**
SESUVECA DEL PERÚ							
						DESPIECE DE FABRICACIÓN / COTAS LOCALES	
DIBUJ.	PROYECTO P05		16/10/2026				
VERIF.							
APROB.							
FABR.							
CALID.				MATERIAL: SEGÚN DESPIECE		**ESTACIÓN DE DESCARGA BIGBAG**	**A1**
PESO: BOM / CAD				ESCALA: INDICADA		**P05-T-042**	HOJA 42/51

DESPIECE DE FABRICACIÓN / COTAS LOCALES


Detalles 169..172 de 175 componentes fabricados. Proyecciones exactas de la geometría final.

P204 | CANT. 1


CONTRAPLACA_COMUN_A36_290x290x18_G02_P05

ASTM A36 | ENVOLVENTE LOCAL X/Y/Z: 290 x 290 x 18


XY / escala 1:4

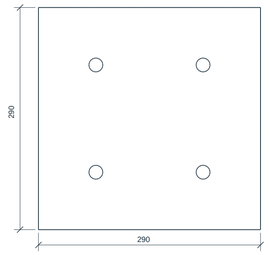

XZ / escala 1:2 / INTERRUMPIDA

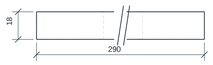

YZ / escala 1:2 / INTERRUMPIDA

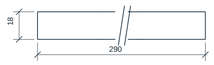


CHAPA: espesor 18. Contorno nominal CAD; corte y taladros se identifican por coordenadas locales.
TALADROS / EJES: ID - Ø - X - Y - Z - DIRECCIÓN (mm)
T1 / 18 / -70 / -70 / 0 / Z
T2 / 18 / -70 / 70 / 0 / Z
T3 / 18 / 70 / -70 / 0 / Z
T4 / 18 / 70 / 70 / 0 / Z

P205 | CANT. 1


CONTRAPLACA_COMUN_A36_290x290x18_G03_P05

ASTM A36 | ENVOLVENTE LOCAL X/Y/Z: 290 x 290 x 18


XY / escala 1:4

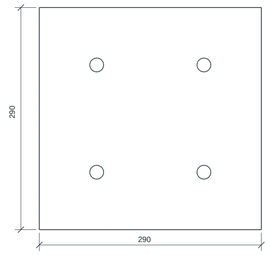

XZ / escala 1:2 / INTERRUMPIDA

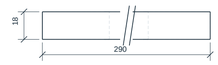

YZ / escala 1:2 / INTERRUMPIDA

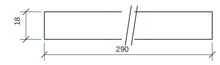


CHAPA: espesor 18. Contorno nominal CAD; corte y taladros se identifican por coordenadas locales.
TALADROS / EJES: ID - Ø - X - Y - Z - DIRECCIÓN (mm)
T1 / 18 / -70 / -70 / 0 / Z
T2 / 18 / -70 / 70 / 0 / Z
T3 / 18 / 70 / -70 / 0 / Z
T4 / 18 / 70 / 70 / 0 / Z

P206 | CANT. 1


CONTRAPLACA_COMUN_A36_290x290x18_G04_P05

ASTM A36 | ENVOLVENTE LOCAL X/Y/Z: 290 x 290 x 18


XY / escala 1:4

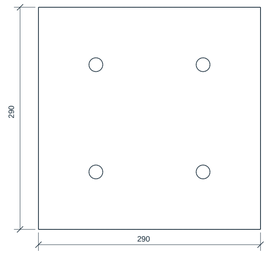

XZ / escala 1:2 / INTERRUMPIDA

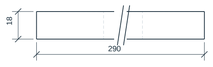

YZ / escala 1:2 / INTERRUMPIDA

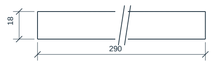


CHAPA: espesor 18. Contorno nominal CAD; corte y taladros se identifican por coordenadas locales.
TALADROS / EJES: ID - Ø - X - Y - Z - DIRECCIÓN (mm)
T1 / 18 / -70 / -70 / 0 / Z
T2 / 18 / -70 / 70 / 0 / Z
T3 / 18 / 70 / -70 / 0 / Z
T4 / 18 / 70 / 70 / 0 / Z

P207 | CANT. 1


CONTRAPLACA_COMUN_A36_290x290x18_G05_P05

ASTM A36 | ENVOLVENTE LOCAL X/Y/Z: 290 x 290 x 18


XY / escala 1:4

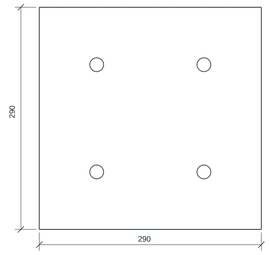

XZ / escala 1:2 / INTERRUMPIDA

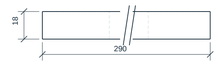

YZ / escala 1:2 / INTERRUMPIDA

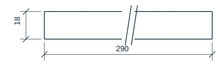

CHAPA: espesor 18. Contorno nominal CAD; corte y taladros se identifican por coordenadas locales.
TALADROS / EJES: ID - Ø - X - Y - Z - DIRECCIÓN (mm)
T1 / 18 / -70 / -70 / 0 / Z
T2 / 18 / -70 / 70 / 0 / Z
T3 / 18 / 70 / -70 / 0 / Z
T4 / 18 / 70 / 70 / 0 / Z

Cotas en mm. Unidades y referencias locales X/Y/Z. Las vistas de detalle y DXF son proyecciones del CAD exacto OpenCascade; no se atribuye exportación nativa de SolidWorks a estas láminas.

Tolerancias ISO 2768-1 clase m en cotas lineales/angulares de piezas mecanizadas sin tolerancia individual. No se aplica a ajustes, soldaduras, equipos comerciales ni dimensiones de montaje críticas.

No escalar el PDF. Taladrar/escariar y desbarbar; eliminar aristas cortantes. Las preparaciones con luz 2 mm conservan geometría CAD; ejecutar soldadura únicamente según cuadro de juntas y WPS aplicable.

Acabados, ajustes y aceptación de uniones: según memoria, detalle específico y programa de inspección. Los espacios de verificación/aprobación permanecen sin firma.

Fuente: native_manifest.json + solidworks_model.bas; geometría y coordenadas íntegramente trazadas.

P05 - PLANOS DE DETALLE PARA REVISIÓN TÉCNICA

ESTACIÓN BIGBAG							**P05**
SESUVECA DEL PERÚ							
						DESPIECE DE FABRICACIÓN / COTAS LOCALES	
DIBUJ.	PROYECTO P05		16/10/2026				
VERIF.							
APROB.							
FABR.							
CALID.				MATERIAL: SEGÚN DESPIECE		**ESTACIÓN DE DESCARGA BIGBAG**	**A1**
PESO: BOM / CAD				ESCALA: INDICADA		**P05-T-043**	HOJA 43/51

DESPIECE DE FABRICACIÓN / COTAS LOCALES


Detalles 173..175 de 175 componentes fabricados. Proyecciones exactas de la geometría final.

P208 | CANT. 26


CONTRAPLACA_A36_150x150x18_D18_P05

ASTM A36 | ENVOLVENTE LOCAL X/Y/Z: 150 x 150 x 18


XY / escala 1:4

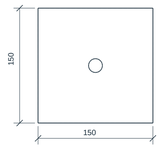

XZ / escala 1:1 / INTERRUMPIDA

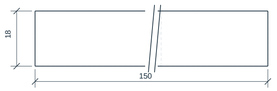

YZ / escala 1:1 / INTERRUMPIDA

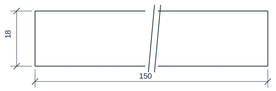


CHAPA: espesor 18. Contorno nominal CAD; corte y taladros se identifican por coordenadas locales.
TALADROS / EJES: ID - Ø - X - Y - Z - DIRECCIÓN (mm)
T1 / 18 / 0 / 0 / 0 / Z

P209 | CANT. 1


CONTRAPLACA_COMUN_A36_175x360x18_G25_P05

ASTM A36 | ENVOLVENTE LOCAL X/Y/Z: 175 x 360 x 18

XY / escala 1:5

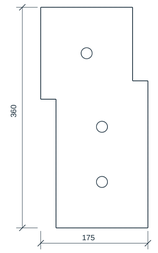

XZ / escala 1:1 / INTERRUMPIDA

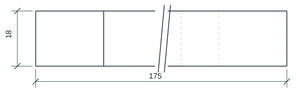

YZ / escala 1:2 / INTERRUMPIDA




CHAPA: espesor 18. Contorno nominal CAD; corte y taladros se identifican por coordenadas locales.
TALADROS / EJES: ID - Ø - X - Y - Z - DIRECCIÓN (mm)
T1 / 18 / 12.5 / -15 / 0 / Z
T2 / 18 / 12.5 / -105 / 0 / Z
T3 / 18 / -12.5 / 105 / 0 / Z

P210 | CANT. 1


CONTRAPLACA_COMUN_A36_175x360x18_G30_P05

ASTM A36 | ENVOLVENTE LOCAL X/Y/Z: 175 x 360 x 18


XY / escala 1:5

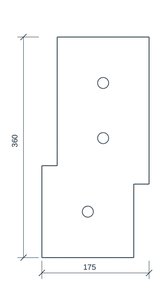

XZ / escala 1:1 / INTERRUMPIDA

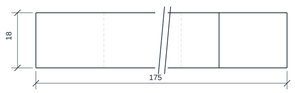

YZ / escala 1:2 / INTERRUMPIDA

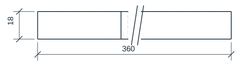

CHAPA: espesor 18. Contorno nominal CAD; corte y taladros se identifican por coordenadas locales.
TALADROS / EJES: ID - Ø - X - Y - Z - DIRECCIÓN (mm)
T1 / 18 / 12.5 / 15 / 0 / Z
T2 / 18 / -12.5 / -105 / 0 / Z
T3 / 18 / 12.5 / 105 / 0 / Z

Cotas en mm. Unidades y referencias locales X/Y/Z. Las vistas de detalle y DXF son proyecciones del CAD exacto OpenCascade; no se atribuye exportación nativa de SolidWorks a estas láminas.

Tolerancias ISO 2768-1 clase m en cotas lineales/angulares de piezas mecanizadas sin tolerancia individual. No se aplica a ajustes, soldaduras, equipos comerciales ni dimensiones de montaje críticas.

No escalar el PDF. Taladrar/escariar y desbarbar; eliminar aristas cortantes. Las preparaciones con luz 2 mm conservan geometría CAD; ejecutar soldadura únicamente según cuadro de juntas y WPS aplicable.

Acabados, ajustes y aceptación de uniones: según memoria, detalle específico y programa de inspección. Los espacios de verificación/aprobación permanecen sin firma.

Fuente: native_manifest.json + solidworks_model.bas; geometría y coordenadas íntegramente trazadas.

P05 - PLANOS DE DETALLE PARA REVISIÓN TÉCNICA

ESTACIÓN BIGBAG							**P05**
SESUVECA DEL PERÚ							
						DESPIECE DE FABRICACIÓN / COTAS LOCALES	
DIBUJ.	PROYECTO P05		16/10/2026				
VERIF.							
APROB.							
FABR.							
CALID.				MATERIAL: SEGÚN DESPIECE		**ESTACIÓN DE DESCARGA BIGBAG**	**A1**
PESO: BOM / CAD				ESCALA: INDICADA		**P05-T-044**	HOJA 44/51

LISTA INTEGRAL DE MATERIALES 1/5

Una fila por pieza instalada; cantidades de las 889 posiciones del manifiesto. Referencias comerciales identificadas.

ÍTEM	PIEZA / ARCHIVO SLDPRT	CANT.	MATERIAL	TIPO	ENVOLVENTE X/Y/Z mm	HOJA / REFERENCIA
P001	SHS150x150x6_L5488000_P05	4	ASTM A500 Gr.B	profile	150 x 150 x 5488	P05-T-001
P002	IPE200_L2000000_P05	2	ASTM A36	profile	100 x 200 x 2000	P05-T-001
P003	I_A240x140x8x20_L3600000_P05	1	ASTM A36	profile	140 x 240 x 3600	P05-T-001
P004	SHS100x100x5_L2848000_P05	4	ASTM A500 Gr.B	profile	100 x 100 x 2848	P05-T-001
P005	SHS150x150x6_L2200000_CUTda1945_P05	2	ASTM A500 Gr.B	profile	150 x 150 x 2350	P05-T-002
P006	SHS150x150x6_L1650000_CUT8f76b3_P05	2	ASTM A500 Gr.B	profile	150 x 150 x 1800	P05-T-002
P007	SHS60x60x4_L2100000_P05	2	ASTM A500 Gr.B	profile	60 x 60 x 2100	P05-T-002
P008	SHS60x60x4_L1550000_P05	2	ASTM A500 Gr.B	profile	60 x 60 x 1550	P05-T-002
P009	SHS100x100x5_L1499304_TOLVA	4	ASTM A500 Gr.B	profile	100 x 100 x 1599.3	P05-T-003
P010	RHS150x75x5_L1757000_CUT394f60_P05	2	ASTM A500 Gr.B	profile	75 x 150 x 1832	P05-T-003
P011	RHS150x75x5_L1757000_CUT3ec3f6_P05	2	ASTM A500 Gr.B	profile	75 x 150 x 1832	P05-T-003
P012	SHS60x60x4_L2882256_CUTf8e6e9_P05	2	ASTM A500 Gr.B	profile	60 x 60 x 2976.32	P05-T-003
P013	SHS80x80x4_L2050000_P05	2	ASTM A500 Gr.B	profile	80 x 80 x 2050	P05-T-004
P014	SHS150x150x12p5_L1000000_P05	2	S355NH / EN10210-1	profile	150 x 150 x 1000	P05-T-004
P015	SHS150x150x12p5_L850000_P05	1	S355NH / EN10210-1	profile	150 x 150 x 887.5	P05-T-004
P016	SHS60x60x4_L62410_P05	4	ASTM A500 Gr.B	profile	60 x 60 x 62.41	P05-T-004
P017	TOL_PANEL_CONO_8mm	4	ASTM A36	plate	1691.57 x 1404.62 x 8	P05-T-005
P018	TOL_PANEL_CUERPO_6mm_P05	3	ASTM A36	plate	1682 x 470.15 x 6	P05-T-005
P019	TOL_PANEL_CUERPO_DN150_6mm_P05	1	ASTM A36	plate	1682 x 470.15 x 6	P05-T-005
P020	TOL_TAPA_POLVO_1662x1662x3_P05	1	ASTM A36	plate	1682 x 1682 x 3	P05-T-005
P021	TOL_JUNTA_EPDM_1662x1662x3_P05	1	EPDM	COMERCIAL	1682 x 1682 x 3	CATÁLOGO / COMPRA
P022	BASE_PORTICO_360x360x35	2	ASTM A36	plate	360 x 360 x 35	P05-T-006
P023	BASE_TOLVA_250x250x25	2	ASTM A36	plate	250 x 250 x 25	P05-T-006
P024	U01_CAP_200x200x12_P05	2	ASTM A36	plate	200 x 200 x 12	P05-T-006
P025	U01_LATERAL_200x240x12_P05	4	ASTM A36	plate	200 x 240 x 12	P05-T-006
P026	U01_CALCE_200x20x6_P05	8	ASTM A36	plate	200 x 20 x 6	P05-T-007
P027	U01_RIGIDIZADOR_44x175x6_P05	24	ASTM A36	plate	44 x 175 x 6	P05-T-007
P028	U01_CARTELA_100x240x12_P05	8	ASTM A36	plate	100 x 240 x 12	P05-T-007
P029	P01_CAP_COLUMNA_200x200x12_P05	4	ASTM A36	plate	200 x 200 x 12	P05-T-007
P030	U02_COLLAR_150x200x12_P05	8	ASTM A36	plate	150 x 200 x 12	P05-T-008
P031	U02_COLLAR_174x200x12_P05	8	ASTM A36	plate	174 x 200 x 12	P05-T-008
P032	U02_COLLAR_150x158x12_P05	4	ASTM A36	plate	150 x 158 x 12	P05-T-008
P033	U02_COLLAR_174x158x12_P05	4	ASTM A36	plate	174 x 158 x 12	P05-T-008
P034	U02_CARTELA_BRL-A--1_0_P05	1	ASTM A36 Fy250	plate	250 x 250 x 18	P05-T-009
P035	U02_CARTELA_BRL-A--1_1_P05	1	ASTM A36 Fy250	plate	250 x 183 x 18	P05-T-009
P036	U02_CARTELA_BRL-B--1_0_P05	1	ASTM A36 Fy250	plate	250 x 183 x 18	P05-T-009
P037	U02_CARTELA_BRL-B--1_1_P05	1	ASTM A36 Fy250	plate	250 x 250 x 18	P05-T-009
P038	U02_CARTELA_KNE--1_0_P05	1	ASTM A36 Fy250	plate	250 x 250 x 18	P05-T-010
P039	U02_CARTELA_KNE--1_1_P05	1	ASTM A36 Fy250	plate	250 x 250 x 18	P05-T-010
P040	U02_CARTELA_BRL-A-1_0_P05	1	ASTM A36 Fy250	plate	250 x 250 x 18	P05-T-010
P041	U02_CARTELA_BRL-A-1_1_P05	1	ASTM A36 Fy250	plate	250 x 183 x 18	P05-T-010
P042	U02_CARTELA_BRL-B-1_0_P05	1	ASTM A36 Fy250	plate	250 x 183 x 18	P05-T-011
P043	U02_CARTELA_BRL-B-1_1_P05	1	ASTM A36 Fy250	plate	250 x 250 x 18	P05-T-011
P044	U02_CARTELA_KNE-1_0_P05	1	ASTM A36 Fy250	plate	250 x 250 x 18	P05-T-011

Filas 1..44 / 210. Cantidad acumulada total del BOM: 889 componentes.

Cotas en mm. Unidades y referencias locales X/Y/Z. Las vistas de detalle y DXF son proyecciones del CAD exacto OpenCascade; no se atribuye exportación nativa de SolidWorks a estas láminas.

Tolerancias ISO 2768-1 clase m en cotas lineales/angulares de piezas mecanizadas sin tolerancia individual. No se aplica a ajustes, soldaduras, equipos comerciales ni dimensiones de montaje críticas.

No escalar el PDF. Taladrar/escariar y desbarbar; eliminar aristas cortantes. Las preparaciones con luz 2 mm conservan geometría CAD; ejecutar soldadura únicamente según cuadro de juntas y WPS aplicable.

Acabados, ajustes y aceptación de uniones: según memoria, detalle específico y programa de inspección. Los espacios de verificación/aprobación permanecen sin firma.

Fuente: native_manifest.json + solidworks_model.bas; geometría y coordenadas íntegramente trazadas.

P05 - PLANOS DE DETALLE PARA REVISIÓN TÉCNICA

ESTACIÓN BIGBAG						**P05**
SESUVECA DEL PERÚ	SESUVECA DEL PERÚ					
DIBUJ.	PROYECTO P05		16/10/2026			**LISTA INTEGRAL DE MATERIALES 1/5**
VERIF.						
APROB.						
FABR.						
CALID.				MATERIAL: SEGÚN DESPIECE		**ESTACIÓN DE DESCARGA BIGBAG**
						A1
PESO: BOM / CAD				ESCALA: INDICADA		**P05-T-045** HOJA 45/51

LISTA INTEGRAL DE MATERIALES 2/5

Una fila por pieza instalada; cantidades de las 889 posiciones del manifiesto. Referencias comerciales identificadas.

ÍTEM	PIEZA / ARCHIVO SLDPRT	CANT.	MATERIAL	TIPO	ENVOLVENTE X/Y/Z mm	HOJA / REFERENCIA
P045	U02_CARTELA_KNE-1_1_P05	1	ASTM A36 Fy250	plate	250 x 250 x 18	P05-T-011
P046	U04_CAP_PATA_150x150x12_P05	4	ASTM A36	plate	150 x 150 x 12	P05-T-012
P047	U04_CARTELA_125x150x12_P05	8	ASTM A36	plate	125 x 150 x 12	P05-T-012
P048	T01_ASIENTO_100x100x6_P05	4	ASTM A36	plate	100 x 100 x 6	P05-T-012
P049	T02_ASIENTO_INFERIOR_100x100x20_P05	4	ASTM A36	plate	100 x 100 x 20	P05-T-012
P050	T02_ASIENTO_SUPERIOR_200x214x20_P05	4	ASTM A36	plate	200 x 214 x 20	P05-T-013
P051	OREJA_CENTRAL_150x220x20	1	ASTM A36	plate	150 x 220 x 20	P05-T-013
P052	OREJA_EXTREMA_90x120x12	4	ASTM A36	plate	90 x 120 x 12	P05-T-013
P053	CR_RESPALDO_EXTREMA_90x150x20_P05	4	ASTM A36	plate	90 x 150 x 20	P05-T-013
P054	CR_CARTELA_TRIANGULAR_150x150x12_P05	8	ASTM A36	plate	150 x 150 x 12	P05-T-014
P055	CR_CAP_CENTRAL_150x300x30_P05	1	ASTM A36	plate	150 x 300 x 30	P05-T-014
P056	CR_CHEEK_300x150x20_P05	2	ASTM A36	plate	300 x 150 x 20	P05-T-014
P057	LINER_CONO_UHMW10_P05	4	UHMWPE disipativo	plate	1673.09 x 1405.77 x 10	P05-T-014
P058	LINER_CUERPO_UHMW10_P05	3	UHMWPE disipativo	plate	1670 x 470.15 x 10	P05-T-015
P059	LINER_CUERPO_UHMW10_DN150_P05	1	UHMWPE disipativo	plate	1670 x 470.15 x 10	P05-T-015
P060	CORTE_ALETA_1_304_t16_P05	1	AISI304	plate	149 x 204 x 16	P05-T-015
P061	CORTE_ALETA_2_304_t16_P05	1	AISI304	plate	149 x 204 x 16	P05-T-015
P062	CORTE_ALETA_3_304_t16_P05	1	AISI304	plate	174 x 204 x 16	P05-T-016
P063	CORTE_ALETA_4_304_t16_P05	1	AISI304	plate	174 x 204 x 16	P05-T-016
P064	CORTE_MASTIL_60p3x5_P05	1	AISI304	tube	60.3 x 60.3 x 204	P05-T-016
P065	CORTE_MARCO_570x620x12_P05	1	AISI 304	plate	570 x 620 x 12	P05-T-016
P066	CORTE_BASE_200x200x16_P05	1	AISI 304	plate	200 x 200 x 16	P05-T-017
P067	TECLE_2t_REFERENCIA	1	SEGÚN CATÁLOGO / COMPRA	COMERCIAL	460 x 400 x 400	CATÁLOGO / COMPRA
P068	CARRO_MOTORIZADO_REFERENCIA	1	SEGÚN CATÁLOGO / COMPRA	COMERCIAL	320 x 220 x 180	CATÁLOGO / COMPRA
P069	CADENA_ENVELOPE	1	SEGÚN CATÁLOGO / COMPRA	COMERCIAL	24 x 24 x 250	CATÁLOGO / COMPRA
P070	BIGBAG_1000x1000x1000_REF	1	SEGÚN CATÁLOGO / COMPRA	COMERCIAL	1000 x 1000 x 1000	CATÁLOGO / COMPRA
P071	ASA_BIGBAG_REF	4	SEGÚN CATÁLOGO / COMPRA	COMERCIAL	45 x 18 x 150	CATÁLOGO / COMPRA
P072	MG02_FLANGE_364x350x6_P05	1	ASTM A36	plate	364 x 350 x 6	P05-T-017
P073	MG03_FLANGE_364x350x6_P05	1	ASTM A36	plate	364 x 350 x 6	P05-T-017
P074	MG01_HOJA_310x450x6_P05	1	ASTM A36	plate	310 x 450 x 6	P05-T-017
P075	MG04_SUP_1_P05	1	ASTM A36	plate	44 x 455 x 6	P05-T-018
P076	MG04_SUP_2_P05	1	ASTM A36	plate	44 x 455 x 6	P05-T-018
P077	MG05_INF_1_P05	1	ASTM A36	plate	44 x 455 x 6	P05-T-018
P078	MG05_INF_2_P05	1	ASTM A36	plate	44 x 455 x 6	P05-T-018
P079	MG06_ESP_1_P05	1	ASTM A36	plate	6 x 800 x 31.5	P05-T-019
P080	MG06_ESP_2_P05	1	ASTM A36	plate	6 x 800 x 31.5	P05-T-019
P081	MG07_UHMW_SUP_1_P05	1	UHMW-PE	COMERCIAL	20 x 740 x 12	CATÁLOGO / COMPRA
P082	MG07_UHMW_SUP_2_P05	1	UHMW-PE	COMERCIAL	20 x 740 x 12	CATÁLOGO / COMPRA
P083	MG08_UHMW_INF_1_P05	1	UHMW-PE	COMERCIAL	20 x 740 x 12	CATÁLOGO / COMPRA
P084	MG08_UHMW_INF_2_P05	1	UHMW-PE	COMERCIAL	20 x 740 x 12	CATÁLOGO / COMPRA
P085	MG09_UHMW_LADO_1_P05	1	UHMW-PE	COMERCIAL	20 x 740 x 7.5	CATÁLOGO / COMPRA
P086	MG09_UHMW_LADO_2_P05	1	UHMW-PE	COMERCIAL	20 x 740 x 7.5	CATÁLOGO / COMPRA
P087	MG10_CASQUILLO_12x9_L31p5_P05	8	ACERO	tube	12 x 12 x 31.5	P05-T-019
P088	MS01_TRANSICION_CUADRADO_REDONDO_3_P05	1	ASTM A36	plate	256 x 256 x 80	P05-T-019

Filas 45..88 / 210. Cantidad acumulada total del BOM: 889 componentes.

Cotas en mm. Unidades y referencias locales X/Y/Z. Las vistas de detalle y DXF son proyecciones del CAD exacto OpenCascade; no se atribuye exportación nativa de SolidWorks a estas láminas.

Tolerancias ISO 2768-1 clase m en cotas lineales/angulares de piezas mecanizadas sin tolerancia individual. No se aplica a ajustes, soldaduras, equipos comerciales ni dimensiones de montaje críticas.

No escalar el PDF. Taladrar/escariar y desbarbar; eliminar aristas cortantes. Las preparaciones con luz 2 mm conservan geometría CAD; ejecutar soldadura únicamente según cuadro de juntas y WPS aplicable.

Acabados, ajustes y aceptación de uniones: según memoria, detalle específico y programa de inspección. Los espacios de verificación/aprobación permanecen sin firma.

Fuente: native_manifest.json + solidworks_model.bas; geometría y coordenadas íntegramente trazadas.

ESTACIÓN BIGBAG						**P05**
SESUVECA DEL PERÚ						
						LISTA INTEGRAL DE MATERIALES 2/5
DIBUJ.	PROYECTO P05		16/10/2026			
VERIF.						
APROB.						
FABR.						
CALID.				MATERIAL: SEGÚN DESPIECE		**ESTACIÓN DE DESCARGA BIGBAG**
						A1
PESO: BOM / CAD				ESCALA: INDICADA		**P05-T-046** HOJA 46/51

LISTA INTEGRAL DE MATERIALES 3/5

Una fila por pieza instalada; cantidades de las 889 posiciones del manifiesto. Referencias comerciales identificadas.

ÍTEM	PIEZA / ARCHIVO SLDPRT	CANT.	MATERIAL	TIPO	ENVOLVENTE X/Y/Z mm	HOJA / REFERENCIA
P089	MS02_CUELLO_ID250_OD256_L80_P05	1	ACERO	tube	256 x 256 x 80	P05-T-020
P090	MS03_SECTOR_170deg_ID268_t3_H40_P05	2	ASTM A36	plate	271.92 x 137 x 40	P05-T-020
P091	MS04_LINER_EPDM3_SECTOR_170_P05	2	EPDM	COMERCIAL	265.96 x 134 x 40	CATÁLOGO / COMPRA
P092	MS05_SOPORTE_60x80x6_P05	2	ASTM A36	plate	60 x 80 x 6	P05-T-020
P093	SACO_25_50kg_REF	1	SEGÚN CATÁLOGO / COMPRA	COMERCIAL	380 x 220 x 766.5	CATÁLOGO / COMPRA
P094	BALANZA_2t_1200_REF	1	SEGÚN CATÁLOGO / COMPRA	COMERCIAL	1200 x 1200 x 150	CATÁLOGO / COMPRA
P095	MG11_GUARDA_U_590x645x260_R3_t2_P05	1	ASTM A36	plate	590 x 260 x 645	P05-T-020
P096	MG12_GUARDA_FONDO_590x645x2_P05	1	ASTM A36	plate	590 x 645 x 2	P05-T-021
P097	MG13_GUARDA_TESTERO_586x258x2_P05	1	ASTM A36	plate	586 x 258 x 2	P05-T-021
P098	MG14_JUNTA_SOLAPE_RECORTET2_REF	1	Junta flexible disipativa compatible con polvo; seleccion final conforme materiales del proyecto	COMERCIAL	556 x 103 x 2	CATÁLOGO / COMPRA
P099	BASE_COMBINADA_PORTICO_TOLVA_SUR_t35_P05	1	A36	plate	555 x 480 x 35	P05-T-021
P100	BASE_COMBINADA_PORTICO_TOLVA_NORTE_t35_P05	1	A36	plate	555 x 690 x 35	P05-T-021
P101	ANCLA_ARANDELA_D30_D18_t3_REF	28	SEGÚN CATÁLOGO / COMPRA	COMERCIAL	30 x 30 x 3	CATÁLOGO / COMPRA
P102	ANCLA_TUERCA_M16_AF24_H13_REF	28	Acero clase8	COMERCIAL	27.71 x 24 x 13	CATÁLOGO / COMPRA
P103	PORTICO_CIERRE_IPE200_2000x200x8_P05	4	A36	plate	2000 x 200 x 8	P05-T-022
P104	TC01_SADDLE_300x180x20_P05	1	ASTM A36	plate	300 x 180 x 20	P05-T-022
P105	TC02_DUPLICADOR_ALA_300x60x12_P05	2	ASTM A36 Fy250	plate	300 x 60 x 12	P05-T-022
P106	TC03_BRAZO_SHS100x100x10_S355_L300_P05	1	S355NH / EN10210-1	profile	100 x 100 x 350	P05-T-022
P107	TC04_POSTE_SHS100x100x10_S355_L200_P05	1	S355NH / EN10210-1	profile	100 x 100 x 215	P05-T-023
P108	TC05_PLACA_HORQUILLA_200x160x20_P05	1	ASTM A36	plate	200 x 160 x 20	P05-T-023
P109	TC06_OREJA_80x100x12_D31_P05	2	ASTM A36	plate	80 x 100 x 12	P05-T-023
P110	TC07_RECEPTOR_80x96x16_D31_P05	1	A36	plate	80 x 96 x 16	P05-T-023
P111	TC08_ADAPTADOR_200x160x20_4D18_P05	1	A36	plate	200 x 160 x 20	P05-T-024
P112	TC09_CARTABON_SADDLE_220x120x20_P05	2	ASTM A36	plate	220 x 120 x 20	P05-T-024
P113	TC10_CARTABON_RECEPTOR_60x60x12_P05	2	ASTM A36	plate	60 x 60 x 12	P05-T-024
P114	TC11_PASADOR_D30_L90_FY355_P05	1	Acero certificado Fy>=355MPa	tube	30 x 30 x 90	P05-T-024
P115	TC12_CABEZA_D46_L8_P05	1	ASTM A36 / SEGÚN MEMORIA	tube	46 x 46 x 8	P05-T-025
P116	TC13_CLIP_R_D3_L38_REF	1	SEGÚN CATÁLOGO / COMPRA	COMERCIAL	3 x 3 x 38	CATÁLOGO / COMPRA
P117	TC17_OJAL_CABLE_40x12x3_P05	1	ASTM A36	plate	40 x 12 x 3	P05-T-025
P118	TC18_CABLE_CAUTIVO_D3_SEG1_REF	1	Cable inoxidable cautivo flexible; longitud min350mm	COMERCIAL	3 x 3 x 118.53	CATÁLOGO / COMPRA
P119	TC18_CABLE_CAUTIVO_D3_SEG2_REF	1	Cable inoxidable cautivo flexible; longitud min350mm	COMERCIAL	3 x 3 x 171.54	CATÁLOGO / COMPRA
P120	TC18_CABLE_CAUTIVO_D3_SEG3_REF	1	Cable inoxidable cautivo flexible; longitud min350mm	COMERCIAL	3 x 3 x 14.76	CATÁLOGO / COMPRA
P121	TC14_PERNO_M20_L90_8p8_REF	4	Clase8.8	COMERCIAL	20 x 20 x 90	CATÁLOGO / COMPRA
P122	TC15_ARANDELA_D37_D22_t3_REF	8	SEGÚN CATÁLOGO / COMPRA	COMERCIAL	37 x 37 x 3	CATÁLOGO / COMPRA
P123	TC16_TUERCA_M20_D36_ID21_H16_REF	8	SEGÚN CATÁLOGO / COMPRA	COMERCIAL	36 x 36 x 16	CATÁLOGO / COMPRA
P124	TC19_ESPARRAGO_M16_L70_8p8_REF	4	Clase8.8	COMERCIAL	16 x 16 x 70	CATÁLOGO / COMPRA
P125	KITO_RUEDA_D110_PASO118_REF	4	SEGÚN CATÁLOGO / COMPRA	COMERCIAL	110 x 110 x 26	CATÁLOGO / COMPRA
P126	BRT_A_FINAL_P05	1	A36	profile	60 x 60 x 5499.97	P05-T-025
P127	BRT_LENGUETA_BRT-A_0_250x250x12_P05	1	ASTM A36	plate	250 x 250 x 12	P05-T-025
P128	BRT_LENGUETA_BRT-A_1_250x250x12_P05	1	ASTM A36	plate	250 x 250 x 12	P05-T-026
P129	BRT_B_FINAL_P05	1	A36	profile	60 x 60 x 5499.97	P05-T-026
P130	BRT_LENGUETA_BRT-B_0_250x250x12_P05	1	ASTM A36	plate	250 x 250 x 12	P05-T-026
P131	BRT_LENGUETA_BRT-B_1_250x250x12_P05	1	ASTM A36	plate	250 x 250 x 12	P05-T-026
P132	BRT_COLLAR_150x300x12_P05	8	ASTM A36	plate	150 x 300 x 12	P05-T-027

Filas 89..132 / 210. Cantidad acumulada total del BOM: 889 componentes.

Cotas en mm. Unidades y referencias locales X/Y/Z. Las vistas de detalle y DXF son proyecciones del CAD exacto OpenCascade; no se atribuye exportación nativa de SolidWorks a estas láminas.

Tolerancias ISO 2768-1 clase m en cotas lineales/angulares de piezas mecanizadas sin tolerancia individual. No se aplica a ajustes, soldaduras, equipos comerciales ni dimensiones de montaje críticas.

No escalar el PDF. Taladrar/escariar y desbarbar; eliminar aristas cortantes. Las preparaciones con luz 2 mm conservan geometría CAD; ejecutar soldadura únicamente según cuadro de juntas y WPS aplicable.

Acabados, ajustes y aceptación de uniones: según memoria, detalle específico y programa de inspección. Los espacios de verificación/aprobación permanecen sin firma.

Fuente: native_manifest.json + solidworks_model.bas; geometría y coordenadas íntegramente trazadas.

ESTACIÓN BIGBAG						**P05**
SESUVECA DEL PERÚ						
						LISTA INTEGRAL DE MATERIALES 3/5
DIBUJ.	PROYECTO P05		16/10/2026			
VERIF.						
APROB.						
FABR.						
CALID.				MATERIAL: SEGÚN DESPIECE		**ESTACIÓN DE DESCARGA BIGBAG**
						A1
PESO: BOM / CAD				ESCALA: INDICADA		**P05-T-047** HOJA 47/51

LISTA INTEGRAL DE MATERIALES 4/5

Una fila por pieza instalada; cantidades de las 889 posiciones del manifiesto. Referencias comerciales identificadas.

ÍTEM	PIEZA / ARCHIVO SLDPRT	CANT.	MATERIAL	TIPO	ENVOLVENTE X/Y/Z mm	HOJA / REFERENCIA
P133	BRT_COLLAR_174x300x12_P05	8	ASTM A36	plate	174 x 300 x 12	P05-T-027
P134	BRT_RESPALDO_174x300x20_P05	4	ASTM A36	plate	174 x 300 x 20	P05-T-027
P135	BRT_OUTRIGGER_SHS100x100x10_S355_L468_P05	4	S355NH / EN10210-1	profile	100 x 100 x 468	P05-T-027
P136	BRT_CONTRACARA_250x250x20_P05	4	ASTM A36	plate	250 x 250 x 20	P05-T-028
P137	GRID__0p25_FINAL_P05	1	A36	profile	120 x 120 x 2050	P05-T-028
P138	GRID_ASIENTO_150x150x20_P05	4	ASTM A36	plate	150 x 150 x 20	P05-T-028
P139	GRID_DIAFRAGMA_HUP_138x138x12_P05	4	ASTM A36	plate	138 x 138 x 12	P05-T-028
P140	GRID_0p25_FINAL_P05	1	A36	profile	120 x 120 x 2050	P05-T-029
P141	CORTE_TRAVESANO100x100x5_L630_P05	2	A36	profile	100 x 100 x 630	P05-T-029
P142	CORTE_ESPACIADOR_CENTRAL_200x200x12_P05	1	AISI 304	plate	200 x 200 x 12	P05-T-029
P143	HR_2p3124_1_FINAL_P05	1	S355NH / EN10210-1	profile	60 x 100 x 1812	P05-T-029
P144	HR_2p3124_2_FINAL_P05	1	S355NH / EN10210-1	profile	60 x 100 x 1812	P05-T-030
P145	HR_2p3124_3_FINAL_P05	1	S355NH / EN10210-1	profile	60 x 100 x 1812	P05-T-030
P146	HR_2p3124_4_FINAL_P05	1	S355NH / EN10210-1	profile	60 x 100 x 1812	P05-T-030
P147	TOPE_ACE_TR100_60_ENVOLVENTE_PRESELECCION_REF	4	Copoliester / envolvente de reserva	COMERCIAL	82 x 133 x 88	CATÁLOGO / COMPRA
P148	SHS60x60x4_L6085645_SLOT_P05_JUNTA_1	1	ASTM A500 Gr.B	profile	60 x 60 x 6085.65	P05-T-030
P149	SHS60x60x4_L6085645_SLOT_P05_JUNTA_2	1	ASTM A500 Gr.B	profile	60 x 60 x 6085.65	P05-T-031
P150	SHS60x60x4_L748810_SLOT_P05_JUNTA_3	1	ASTM A500 Gr.B	profile	60 x 60 x 748.81	P05-T-031
P151	SHS60x60x4_L6085645_SLOT_P05_JUNTA_4	1	ASTM A500 Gr.B	profile	60 x 60 x 6085.65	P05-T-031
P152	SHS60x60x4_L6085645_SLOT_P05_JUNTA_5	1	ASTM A500 Gr.B	profile	60 x 60 x 6085.65	P05-T-031
P153	SHS60x60x4_L748810_SLOT_P05_JUNTA_6	1	ASTM A500 Gr.B	profile	60 x 60 x 748.81	P05-T-032
P154	SHS60x60x4_L3050000_P05_JUNTA_14	1	ASTM A500 Gr.B	profile	60 x 60 x 3022	P05-T-032
P155	SHS60x60x4_L3050000_P05_JUNTA_15	1	ASTM A500 Gr.B	profile	60 x 60 x 3022	P05-T-032
P156	SHS60x60x4_L3050000_P05_JUNTA_16	1	ASTM A500 Gr.B	profile	60 x 60 x 3022	P05-T-032
P157	SHS60x60x4_L3050000_P05_JUNTA_17	1	ASTM A500 Gr.B	profile	60 x 60 x 3022	P05-T-033
P158	CUELLO_CAPTACION_SUP_DN150_AISI304_L200	1	AISI 304	tube	154 x 154 x 200	P05-T-033
P159	AC_CAP_120x120x12	4	ASTM A36	plate	120 x 120 x 12	P05-T-033
P160	AC_CARTELA_150x150x6	18	ASTM A36	plate	150 x 150 x 6	P05-T-033
P161	AC_SHS80x80x4_L2578590	3	ASTM A500 Gr B	profile	80 x 80 x 2578.59	P05-T-034
P162	AC_SHS80x80x4_L2570590	1	ASTM A500 Gr B	profile	80 x 80 x 2570.59	P05-T-034
P163	AC_RHS150x75x5_L1780000	2	ASTM A500 Gr B	profile	75 x 150 x 1780	P05-T-034
P164	AC_RHS150x75x5_L1620000	1	ASTM A500 Gr B	profile	75 x 150 x 1620	P05-T-034
P165	AC_SHS60x60x4_L725000	5	ASTM A500 Gr B	profile	60 x 60 x 725	P05-T-035
P166	AC_RHS150x75x5_L105000	5	ASTM A500 Gr B	profile	75 x 150 x 105	P05-T-035
P167	AC_SHS60x60x4_L2914334	2	ASTM A500 Gr B	profile	60 x 60 x 2914.33	P05-T-035
P168	PLATAFORMA_REJILLA_1700x1190x30_REF	1	ASTM A36 galvanizado	COMERCIAL	1700 x 1179 x 30	CATÁLOGO / COMPRA
P169	PELDAÑO_REJILLA_800x250x30_REF	15	ASTM A36 galvanizado	COMERCIAL	250 x 800 x 30	CATÁLOGO / COMPRA
P170	AC_RHS150x75x5_L4568118_17c97d	2	ASTM A500 Gr B	profile	75 x 150 x 4728.12	P05-T-035
P171	AC_UNION_ZANCA_200x160x12	2	ASTM A36	plate	200 x 160 x 12	P05-T-036
P172	AC_SHS40x40x3_L800000	30	ASTM A500 Gr B	profile	40 x 40 x 800	P05-T-036
P173	AC_BASE_BARANDA_110x110x20	6	ASTM A36	plate	110 x 110 x 20	P05-T-036
P174	AC_CHS60p3x3p91_L1085850	6	ASTM A53 Gr B	tube	60.3 x 60.3 x 1085.85	P05-T-036
P175	AC_CHS48p3x3p68_L1520000	2	ASTM A53 Gr B	tube	48.3 x 48.3 x 1520	P05-T-037
P176	AC_CHS48p3x3p68_L1005000	2	ASTM A53 Gr B	tube	48.3 x 48.3 x 1005	P05-T-037

Filas 133..176 / 210. Cantidad acumulada total del BOM: 889 componentes.

Cotas en mm. Unidades y referencias locales X/Y/Z. Las vistas de detalle y DXF son proyecciones del CAD exacto OpenCascade; no se atribuye exportación nativa de SolidWorks a estas láminas.

Tolerancias ISO 2768-1 clase m en cotas lineales/angulares de piezas mecanizadas sin tolerancia individual. No se aplica a ajustes, soldaduras, equipos comerciales ni dimensiones de montaje críticas.

No escalar el PDF. Taladrar/escariar y desbarbar; eliminar aristas cortantes. Las preparaciones con luz 2 mm conservan geometría CAD; ejecutar soldadura únicamente según cuadro de juntas y WPS aplicable.

Acabados, ajustes y aceptación de uniones: según memoria, detalle específico y programa de inspección. Los espacios de verificación/aprobación permanecen sin firma.

Fuente: native_manifest.json + solidworks_model.bas; geometría y coordenadas íntegramente trazadas.

P05 - PLANOS DE DETALLE PARA REVISIÓN TÉCNICA

ESTACIÓN BIGBAG						**P05**
SESUVECA DEL PERÚ						
						LISTA INTEGRAL DE MATERIALES 4/5
DIBUJ.	PROYECTO P05		16/10/2026			
VERIF.						
APROB.						
FABR.						
CALID.				MATERIAL: SEGÚN DESPIECE		**ESTACIÓN DE DESCARGA BIGBAG**
						A1
PESO: BOM / CAD				ESCALA: INDICADA		**P05-T-048** HOJA 48/51

LISTA INTEGRAL DE MATERIALES 5/5

Una fila por pieza instalada; cantidades de las 889 posiciones del manifiesto. Referencias comerciales identificadas.

ÍTEM	PIEZA / ARCHIVO SLDPRT	CANT.	MATERIAL	TIPO	ENVOLVENTE X/Y/Z mm	HOJA / REFERENCIA
P177	AC_CHS48p3x3p68_L620000	2	ASTM A53 Gr B	tube	48.3 x 48.3 x 620	P05-T-037
P178	AC_PROTECCION_INFERIOR_1700x500x3	1	ASTM A36	plate	1700 x 500 x 3	P05-T-037
P179	AC_RODAPIE_1700x150x6	1	ASTM A36	plate	1700 x 150 x 6	P05-T-038
P180	AC_RODAPIE_1190x150x6	1	ASTM A36	plate	1190 x 150 x 6	P05-T-038
P181	AC_CHS48p3x3p68_L800000	2	ASTM A53 Gr B	tube	48.3 x 48.3 x 800	P05-T-038
P182	AC_CHS48p3x3p68_L503400	2	ASTM A53 Gr B	tube	48.3 x 48.3 x 503.4	P05-T-038
P183	AC_PUERTA_PANEL_720x520x3	1	ASTM A36	plate	720 x 520 x 3	P05-T-039
P184	AC_SHS40x40x3_L1725000	1	ASTM A500 Gr B	profile	40 x 40 x 1725	P05-T-039
P185	AC_RODILLO_GUIA_D40_L20_REF	2	Acero galvanizado, rodamiento sellado	COMERCIAL	40 x 40 x 20	CATÁLOGO / COMPRA
P186	AC_PUERTA_COLGADOR_30x100x6	2	ASTM A36	plate	30 x 100 x 6	P05-T-039
P187	AC_CIERRE_AUTOMATICO_REF	1	Conjunto comercial cierre por resorte y bloqueo supervisado	COMERCIAL	120 x 50 x 40	CATÁLOGO / COMPRA
P188	AC_SENSOR_BLOQUEO_PUERTA_REF	1	Interruptor de seguridad con bloqueo y contactos supervisados	COMERCIAL	40 x 40 x 60	CATÁLOGO / COMPRA
P189	AC_CHS60p3x3p91_L1095800_637020	4	ASTM A53 Gr B	tube	60.3 x 60.3 x 1137.75	P05-T-039
P190	AC_CHS60p3x3p91_L1095800_df7763	2	ASTM A53 Gr B	tube	60.3 x 60.3 x 1137.75	P05-T-040
P191	AC_CHS60p3x3p91_L1095800_0965d8	4	ASTM A53 Gr B	tube	60.3 x 60.3 x 1137.75	P05-T-040
P192	AC_CHS48p3x3p68_L4568118	6	ASTM A53 Gr B	tube	48.3 x 48.3 x 4568.12	P05-T-040
P193	HR4_PAD_100x40x5_P05_EJE_POSITIVO	4	ASTM A36	plate	100 x 40 x 5	P05-T-040
P194	AC_PUENTE_REJILLA_SHS40x40x3_L170_P05	15	ASTM A500 Gr B	profile	40 x 40 x 170	P05-T-041
P195	PASANTE_M16_8p8_L340_P05	52	Acero ISO898-1 clase8.8 certificado	COMERCIAL	16 x 16 x 340	CATÁLOGO / COMPRA
P196	CALCE_PASANTE_BASE_TOLVA_250x250x25_t10	2	ASTM A36	plate	250 x 250 x 10	P05-T-041
P197	TOPE_PLACA_REACCION_640x360x45_P05	2	A36	plate	640 x 360 x 45	P05-T-041
P198	TOPE_RIGIDIZADOR_TERMINAL_100x240x12_P05	4	ASTM A36 Fy250	plate	100 x 240 x 12	P05-T-041
P199	PASANTE_ARANDELA_A36_50x50x10_D18_P05	104	ASTM A36	plate	50 x 50 x 10	P05-T-042
P200	PASANTE_TUERCA_BRIDA_M16_CL10_D34p5_H16_REF	104	ISO 898-2 clase10 certificada	COMERCIAL	34.5 x 34.5 x 16	CATÁLOGO / COMPRA
P201	AC_BASE_220x220x12	5	ASTM A36	plate	220 x 220 x 12	P05-T-042
P202	CALCE_PASANTE_AC_BASE_220x220x12_t35	5	ASTM A36	plate	220 x 220 x 35	P05-T-042
P203	CONTRAPLACA_COMUN_A36_290x290x18_G01_P05	1	ASTM A36	plate	290 x 290 x 18	P05-T-042
P204	CONTRAPLACA_COMUN_A36_290x290x18_G02_P05	1	ASTM A36	plate	290 x 290 x 18	P05-T-043
P205	CONTRAPLACA_COMUN_A36_290x290x18_G03_P05	1	ASTM A36	plate	290 x 290 x 18	P05-T-043
P206	CONTRAPLACA_COMUN_A36_290x290x18_G04_P05	1	ASTM A36	plate	290 x 290 x 18	P05-T-043
P207	CONTRAPLACA_COMUN_A36_290x290x18_G05_P05	1	ASTM A36	plate	290 x 290 x 18	P05-T-043
P208	CONTRAPLACA_A36_150x150x18_D18_P05	26	ASTM A36	plate	150 x 150 x 18	P05-T-044
P209	CONTRAPLACA_COMUN_A36_175x360x18_G25_P05	1	ASTM A36	plate	175 x 360 x 18	P05-T-044
P210	CONTRAPLACA_COMUN_A36_175x360x18_G30_P05	1	ASTM A36	plate	175 x 360 x 18	P05-T-044

Filas 177..210 / 210. Cantidad acumulada total del BOM: 889 componentes.

Cotas en mm. Unidades y referencias locales X/Y/Z. Las vistas de detalle y DXF son proyecciones del CAD exacto OpenCascade; no se atribuye exportación nativa de SolidWorks a estas láminas.

Tolerancias ISO 2768-1 clase m en cotas lineales/angulares de piezas mecanizadas sin tolerancia individual. No se aplica a ajustes, soldaduras, equipos comerciales ni dimensiones de montaje críticas.

No escalar el PDF. Taladrar/escariar y desbarbar; eliminar aristas cortantes. Las preparaciones con luz 2 mm conservan geometría CAD; ejecutar soldadura únicamente según cuadro de juntas y WPS aplicable.

Acabados, ajustes y aceptación de uniones: según memoria, detalle específico y programa de inspección. Los espacios de verificación/aprobación permanecen sin firma.

Fuente: native_manifest.json + solidworks_model.bas; geometría y coordenadas íntegramente trazadas.

P05 - PLANOS DE DETALLE PARA REVISIÓN TÉCNICA

ESTACIÓN BIGBAG						**P05**
SESUVECA DEL PERÚ	SESUVECA DEL PERÚ					
						LISTA INTEGRAL DE MATERIALES 5/5
DIBUJ.	PROYECTO P05		16/10/2026			
VERIF.						
APROB.						
FABR.						
CALID.				MATERIAL: SEGÚN DESPIECE		**ESTACIÓN DE DESCARGA BIGBAG** / **A1**
PESO: BOM / CAD				ESCALA: INDICADA		**P05-T-049** / HOJA 49/51

CUADRO DE JUNTAS Y PREPARACIONES 1/2

Cuadro trazado por ID de interfaz: no soldar las holguras que no transfieren carga. WPS y aceptación según memoria.

ID	MIEMBRO	SOPORTE	TIPO	a mm	L mm	INSTRUCCIÓN / UBICACIÓN
JF-001	BRL-A--1	COL-0--1	LUZ	-	-	DO NOT WELD THIS CLEARANCE; maintain2mm; primary connection specified separately
JF-002	BRL-A--1	COL-3.2--1	LUZ	-	-	DO NOT WELD THIS CLEARANCE; maintain2mm; primary connection specified separately
JF-003	BRL-B--1	COL-0--1	LUZ	-	-	DO NOT WELD THIS CLEARANCE; maintain2mm; primary connection specified separately
JF-004	BRL-B--1	COL-3.2--1	LUZ	-	-	DO NOT WELD THIS CLEARANCE; maintain2mm; primary connection specified separately
JF-005	KNE--1	COL-0--1	LUZ	-	-	DO NOT WELD THIS CLEARANCE; maintain2mm; primary connection specified separately
JF-006	BRL-A-1	COL-0-1	LUZ	-	-	DO NOT WELD THIS CLEARANCE; maintain2mm; primary connection specified separately
JF-007	BRL-A-1	COL-3.2-1	LUZ	-	-	DO NOT WELD THIS CLEARANCE; maintain2mm; primary connection specified separately
JF-008	BRL-B-1	COL-0-1	LUZ	-	-	DO NOT WELD THIS CLEARANCE; maintain2mm; primary connection specified separately
JF-009	BRL-B-1	COL-3.2-1	LUZ	-	-	DO NOT WELD THIS CLEARANCE; maintain2mm; primary connection specified separately
JF-010	KNE-1	COL-0-1	LUZ	-	-	DO NOT WELD THIS CLEARANCE; maintain2mm; primary connection specified separately
JF-019	KNE--1	TRA-0	CJP	3.72	147.61	CJP through thinner member; approved qualified WPS, backing/backgouging or qualified open root; do not infer prequalification
JF-020	KNE-1	TRA-0	CJP	3.72	147.61	CJP through thinner member; approved qualified WPS, backing/backgouging or qualified open root; do not infer prequalification
JF-021	BRL-A--1	TIE--1-0.15	LUZ	-	-	DO NOT WELD THIS CLEARANCE; maintain2mm; primary connection specified separately
JF-022	BRL-B--1	TIE--1-0.15	LUZ	-	-	DO NOT WELD THIS CLEARANCE; maintain2mm; primary connection specified separately
JF-023	TIE--1-0.15	U02_COLLARX_0_1	CJP	3.72	224	CJP through thinner member; approved qualified WPS, backing/backgouging or qualified open root; do not infer prequalification
JF-024	TIE--1-0.15	BRT_COLLARX_-1_0.15_-1	CJP	3.72	224	CJP through thinner member; approved qualified WPS, backing/backgouging or qualified open root; do not infer prequalification
JF-025	BRL-A--1	TIE--1-4.79	LUZ	-	-	DO NOT WELD THIS CLEARANCE; maintain2mm; primary connection specified separately
JF-026	BRL-B--1	TIE--1-4.79	LUZ	-	-	DO NOT WELD THIS CLEARANCE; maintain2mm; primary connection specified separately
JF-027	TIE--1-4.79	BRT_COLLARX_-1_5.338_-1	CJP	3.72	224	CJP through thinner member; approved qualified WPS, backing/backgouging or qualified open root; do not infer prequalification
JF-028	BRL-A--1	U02_COLLARX_0_1	LUZ	-	-	DO NOT WELD THIS CLEARANCE; maintain2mm; primary connection specified separately
JF-029	BRL-A--1	BRT_COLLARX_-1_5.338_-1	LUZ	-	-	DO NOT WELD THIS CLEARANCE; maintain2mm; primary connection specified separately
JF-030	BRL-B--1	BRT_COLLARX_-1_0.15_-1	LUZ	-	-	DO NOT WELD THIS CLEARANCE; maintain2mm; primary connection specified separately
JF-031	KNE--1	U02_COLLARY_8_1	LUZ	-	-	DO NOT WELD THIS CLEARANCE; maintain2mm; primary connection specified separately
JF-032	BRL-A-1	TIE-1-0.15	LUZ	-	-	DO NOT WELD THIS CLEARANCE; maintain2mm; primary connection specified separately
JF-033	BRL-B-1	TIE-1-0.15	LUZ	-	-	DO NOT WELD THIS CLEARANCE; maintain2mm; primary connection specified separately
JF-034	TIE-1-0.15	U02_COLLARX_2_1	CJP	3.72	224	CJP through thinner member; approved qualified WPS, backing/backgouging or qualified open root; do not infer prequalification
JF-035	TIE-1-0.15	BRT_COLLARX_1_0.15_-1	CJP	3.72	224	CJP through thinner member; approved qualified WPS, backing/backgouging or qualified open root; do not infer prequalification
JF-036	BRL-A-1	TIE-1-4.79	LUZ	-	-	DO NOT WELD THIS CLEARANCE; maintain2mm; primary connection specified separately
JF-037	BRL-B-1	TIE-1-4.79	LUZ	-	-	DO NOT WELD THIS CLEARANCE; maintain2mm; primary connection specified separately
JF-038	TIE-1-4.79	BRT_COLLARX_1_5.338_-1	CJP	3.72	224	CJP through thinner member; approved qualified WPS, backing/backgouging or qualified open root; do not infer prequalification

Cotas en mm. Unidades y referencias locales X/Y/Z. Las vistas de detalle y DXF son proyecciones del CAD exacto OpenCascade; no se atribuye exportación nativa de SolidWorks a estas láminas.

Tolerancias ISO 2768-1 clase m en cotas lineales/angulares de piezas mecanizadas sin tolerancia individual. No se aplica a ajustes, soldaduras, equipos comerciales ni dimensiones de montaje críticas.

No escalar el PDF. Taladrar/escariar y desbarbar; eliminar aristas cortantes. Las preparaciones con luz 2 mm conservan geometría CAD; ejecutar soldadura únicamente según cuadro de juntas y WPS aplicable.

Acabados, ajustes y aceptación de uniones: según memoria, detalle específico y programa de inspección. Los espacios de verificación/aprobación permanecen sin firma.

Fuente: native_manifest.json + solidworks_model.bas; geometría y coordenadas íntegramente trazadas.

P05 - PLANOS DE DETALLE PARA REVISIÓN TÉCNICA

ESTACIÓN BIGBAG							**P05**
SESUVECA DEL PERÚ							
						CUADRO DE JUNTAS Y PREPARACIONES 1/2	
DIBUJ.	PROYECTO P05		16/10/2026				
VERIF.							
APROB.							
FABR.							
CALID.				MATERIAL: SEGÚN DESPIECE		**ESTACIÓN DE DESCARGA BIGBAG**	**A1**
PESO: BOM / CAD				ESCALA: INDICADA		**P05-T-050**	HOJA 50/51

CUADRO DE JUNTAS Y PREPARACIONES 2/2

Cuadro trazado por ID de interfaz: no soldar las holguras que no transfieren carga. WPS y aceptación según memoria.

ID	MIEMBRO	SOPORTE	TIPO	a mm	L mm	INSTRUCCIÓN / UBICACIÓN
JF-039	BRL-A-1	U02_COLLARX_2_1	LUZ	-	-	DO NOT WELD THIS CLEARANCE; maintain2mm; primary connection specified separately
JF-040	BRL-A-1	BRT_COLLARX_1_5.338_-1	LUZ	-	-	DO NOT WELD THIS CLEARANCE; maintain2mm; primary connection specified separately
JF-041	BRL-B-1	BRT_COLLARX_1_0.15_-1	LUZ	-	-	DO NOT WELD THIS CLEARANCE; maintain2mm; primary connection specified separately
JF-042	KNE-1	U02_COLLARY_9_-1	LUZ	-	-	DO NOT WELD THIS CLEARANCE; maintain2mm; primary connection specified separately

CJP: V60 / RAIZ2 / ESPESOR MENOR



PJP: a2 / DOS CORDONES L45



FILETE: a SEGUN UNION PRIMARIA



Montaje en campo: uniones desmontables atornilladas. No soldar las holguras JF. a: garganta efectiva de calculo; CJP real atraviesa la pared completa.

Cotas en mm. Unidades y referencias locales X/Y/Z. Las vistas de detalle y DXF son proyecciones del CAD exacto OpenCascade; no se atribuye exportación nativa de SolidWorks a estas láminas.

Tolerancias ISO 2768-1 clase m en cotas lineales/angulares de piezas mecanizadas sin tolerancia individual. No se aplica a ajustes, soldaduras, equipos comerciales ni dimensiones de montaje críticas.

No escalar el PDF. Taladrar/escariar y desbarbar; eliminar aristas cortantes. Las preparaciones con luz 2 mm conservan geometría CAD; ejecutar soldadura únicamente según cuadro de juntas y WPS aplicable.

Acabados, ajustes y aceptación de uniones: según memoria, detalle específico y programa de inspección. Los espacios de verificación/aprobación permanecen sin firma.

Fuente: native_manifest.json + solidworks_model.bas; geometría y coordenadas íntegramente trazadas.

P05 - PLANOS DE DETALLE PARA REVISIÓN TÉCNICA

ESTACIÓN BIGBAG							**P05**
SESUVECA DEL PERÚ							
						CUADRO DE JUNTAS Y PREPARACIONES 2/2	
DIBUJ.	PROYECTO P05		16/10/2026				
VERIF.							
APROB.							
FABR.							
CALID.				MATERIAL: SEGÚN DESPIECE		**ESTACIÓN DE DESCARGA BIGBAG**	**A1**
PESO: BOM / CAD				ESCALA: INDICADA		**P05-T-051**	HOJA 51/51