

# Estación Bigbag P05 / Conjunto general

**ALZADO LONGITUDINAL  ESCALA 1:40**

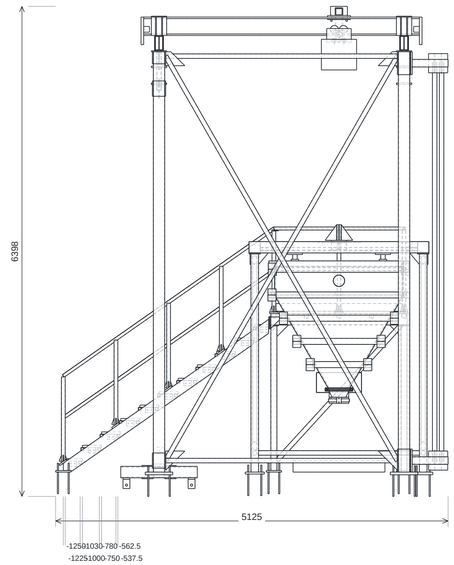


DATUM GLOBAL X (mm)


**ALZADO TRANSVERSAL  ESCALA 1:50**

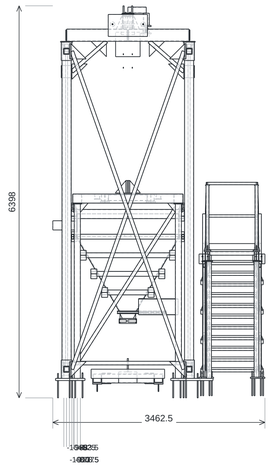


DATUM GLOBAL Y (mm)

| CONJUNTO | PLANO |
|---|---|
| Cimentación y placas base | P05-C-02 |
| Pórticos transversales ensamblados | P05-C-03 |
| Arriostramiento longitudinal y uniones | P05-C-04 |
| Viga carril y topes de fin de carrera | P05-C-05 |
| Bastidor de tolva ensamblado | P05-C-06 |
| Tolva, anillos y revestimiento | P05-C-07 |
| Cortador y parrilla de apoyo de bolsa | P05-C-08 |
| Compuerta de descarga ensamblada | P05-C-09 |
| Guarda, ensacado y captación | P05-C-10 |
| Carro, suspensión y traba de posición | P05-C-11 |
| Plataforma de acceso ensamblada | P05-C-12 |
| Escalera y desembarco ensamblados | P05-C-13 |
| Barandas, pasamanos y rodapiés | P05-C-14 |
| Cruceta de izaje 2 t ensamblada | P05-C-15 |

**ISOMÉTRICO A COLOR / REFERENCIA DE MONTAJE**

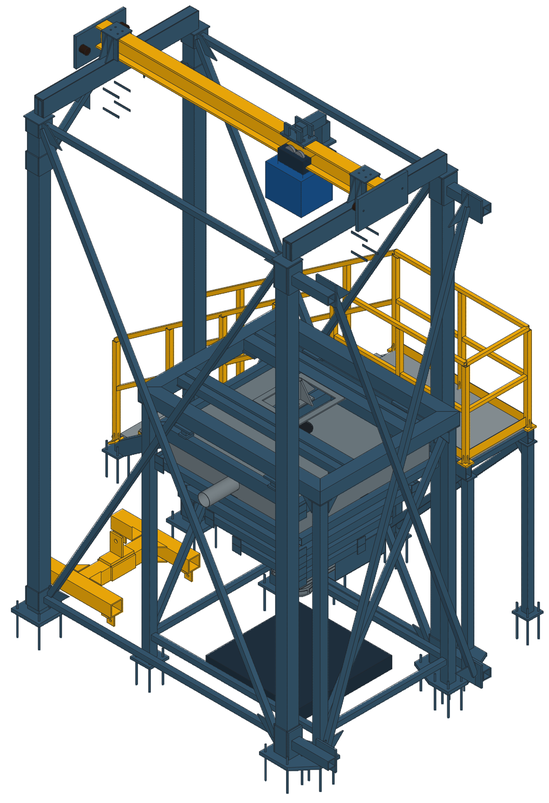

**NOTAS DE FABRICACIÓN Y MmontaJE**

1. Cruceta y tecle nominales 2 t; proceso de bolsas de 1 t.
2. Traslado con fondo de bolsa a Z = 3 520; guarda superior Z = 3 430; punta de cortador Z = 3 230.
3. Enclavamientos, prueba de carga y recepción según memoria.
4. POS.: número de pieza en el BOM de 253 piezas únicas.


Cotas en mm. ISO2768-m. Soldaduras según cuadro JF. Contornos: CAD/DXF.

**P05 - REVISIÓN TÉCNICA**


| | | | | | | |
|---|---|---|---|---|---|---|
| | | | | REBABAR Y ROMPER ARISTAS | NO CAMBIAR LA ESCALA | REVISIÓN P05 |
| SESUVECA DEL PERÚ | | | | | | |
| | NOMBRE | FIRMA | FECHA | | | TÍTULO: Estación Bigbag P05 / Conjunto general |
| DIBUJ. | PROYECTO P05 | | 16/10/26 | | | |
| VERIF. | | | | | | |
| APROB. | | | | | | |
| FABR. | | | | | | |
| CALID. | | | | MATERIAL: SEGÚN LISTA DE MATERIALES | | N.º DE DIBUJO P05-C-01 / A1 |
| PESO: SEGÚN CAD / BOM | | | | ESCALA: INDICADA | | ESTACIÓN DE DESCARGA BIGBAG / HOJA 1 DE 17 |

# Cimentación y placas base

**PLANTA ESCALA 1:20**

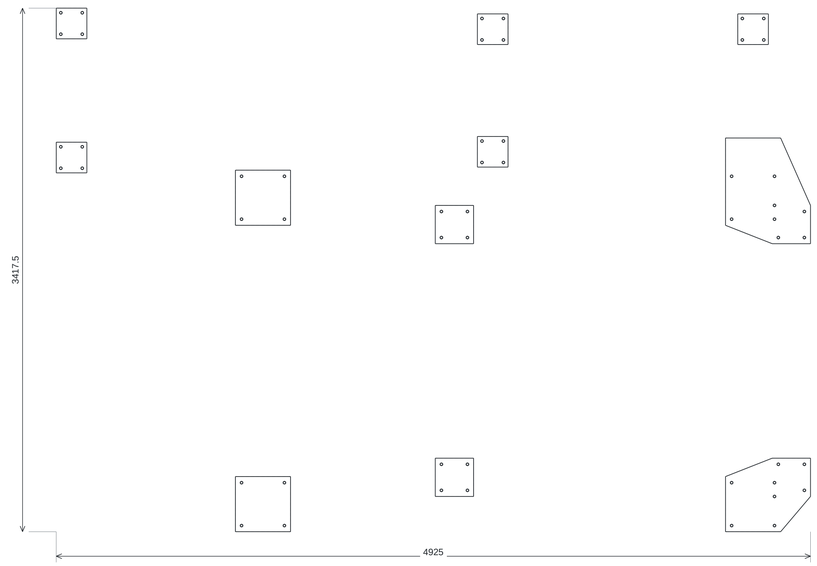



**ALZADO ESCALA 1:15**

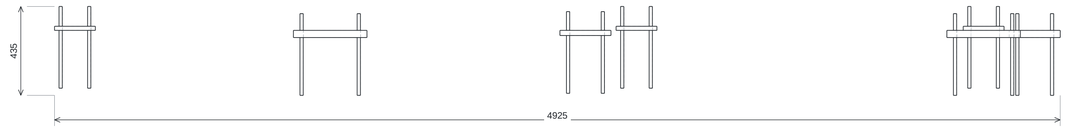


| POS. CAD | CANT. | DESCRIPCIÓN / CORTE NOMINAL mm | MATERIAL |
|---|---|---|---|
| 42 | 2 | BASE PORTICO 360x360x35 | ASTM A36 |
| 43 | 2 | BASE TOLVA 250x250x25 | ASTM A36 |
| 44 | 5 | P02 BASE ACCESO 200x200x12 | ASTM A36 |
| 130 | 1 | BASE COMBINADA PORTICO TOLVA SUR t35 | A36 |
| 131 | 1 | BASE COMBINADA PORTICO TOLVA NORTE t35 | A36 |
| 132 | 52 | ANCLA HASU 8p8 M16 L400 HEF275 | HAS-U8.8 |
| 133 | 52 | ANCLA ARANDELA D30 D18 t3 | SEGÚN CATÁLOGO / COMPRA |
| 134 | 52 | ANCLA TUERCA M16 AF24 H13 | Acero clase8 |

Cortes nominales agrupados; preparaciones finales identificadas por POS., JF y DXF.

**ISOMÉTRICO A COLOR / REFERENCIA DE MONTAJE**

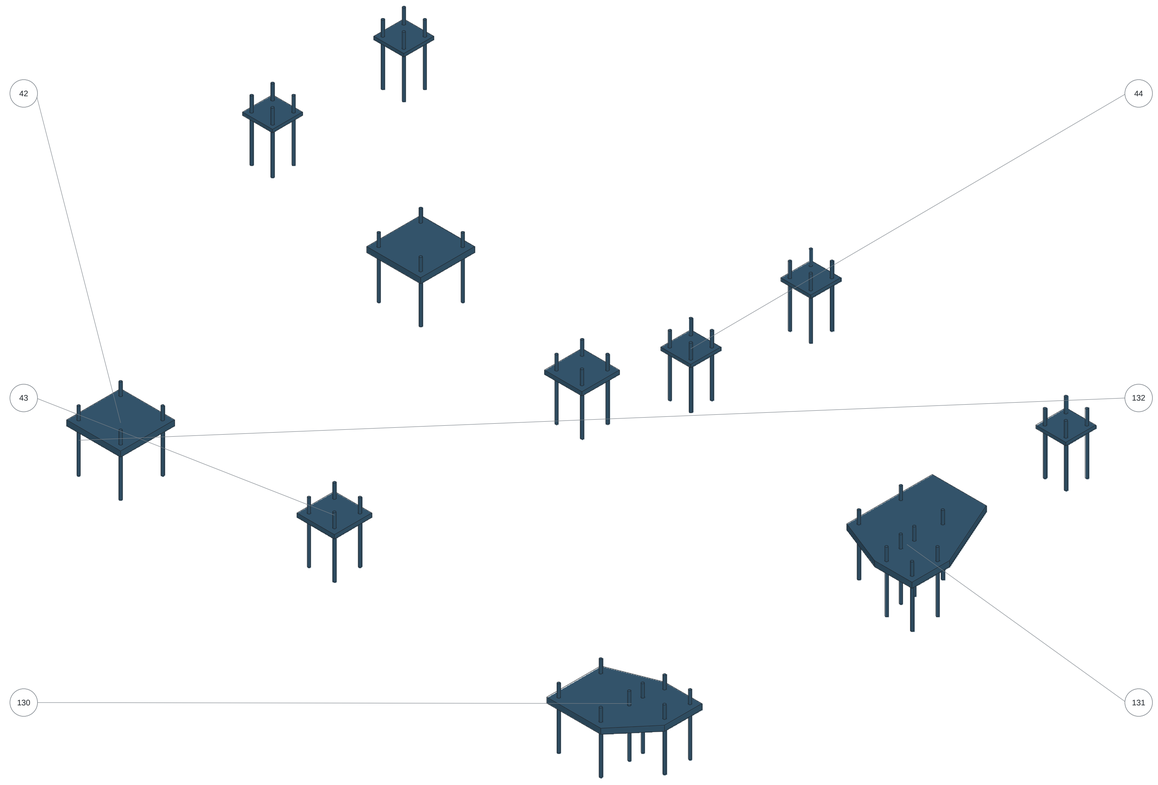


TALADROS PARAMETRIZADOS: 28 / coordenadas locales en Tabla_fabricacion_P05.csv

## NOTAS DE FABRICACIÓN Y MONTAJE

1. Losa: espesor 650 mm; f'c = 20,59 MPa (datos del cliente).
2. HAS-U 8.8 M16: longitud total 400; empotramiento efectivo 275; resina HIT-RE 500 V4.
3. Replanteo en coordenadas globales; cota Z0 = cara superior del concreto. Borde mínimo de proyecto: 500 mm.
4. Respetar patrón y diámetro de agujeros del CAD; instalación, limpieza y curado según fabricante.

Cotas en mm. ISO2768-m. Soldaduras según cuadro JF. Contornos: CAD/DXF.

**TALADROS DE PIEZAS DEL CONJUNTO / COORDENADAS LOCALES mm / ORIGEN CAD**


P42 T1: D18; X-140 Y-140 Z0; eje Z
P42 T2: D18; X-140 Y140 Z0; eje Z
P42 T3: D18; X140 Y-140 Z0; eje Z
P42 T4: D18; X140 Y140 Z0; eje Z
P43 T1: D18; X-85 Y-85 Z0; eje Z
P43 T2: D18; X-85 Y85 Z0; eje Z
P43 T3: D18; X85 Y-85 Z0; eje Z
P43 T4: D18; X85 Y85 Z0; eje Z
P44 T1: D18; X-70 Y-70 Z0; eje Z
P44 T2: D18; X-70 Y70 Z0; eje Z
P44 T3: D18; X70 Y-70 Z0; eje Z
P44 T4: D18; X70 Y70 Z0; eje Z
P130 T1: D18; X-140 Y-140 Z0; eje Z
P130 T2: D18; X-140 Y140 Z0; eje Z
P130 T3: D18; X140 Y-140 Z0; eje Z
P130 T4: D18; X140 Y140 Z0; eje Z
P130 T5: D18; X140 Y50 Z0; eje Z
P130 T6: D18; X165 Y260 Z0; eje Z
P130 T7: D18; X335 Y90 Z0; eje Z
P130 T8: D18; X335 Y260 Z0; eje Z
P131 T1: D18; X-140 Y-140 Z0; eje Z
P131 T2: D18; X-140 Y140 Z0; eje Z
P131 T3: D18; X140 Y-140 Z0; eje Z
P131 T4: D18; X140 Y140 Z0; eje Z
P131 T5: D18; X165 Y-260 Z0; eje Z
P131 T6: D18; X140 Y-50 Z0; eje Z
P131 T7: D18; X335 Y-260 Z0; eje Z
P131 T8: D18; X335 Y-90 Z0; eje Z

**P05 - REVISIÓN TÉCNICA**

| | | | | | | |
|---|---|---|---|---|---|---|
| | | | | REBABAR Y ROMPER ARISTAS | NO CAMBIAR LA ESCALA | REVISIÓN **P05** |
| SESUVECA DEL PERÚ | | | | | | |
| | NOMBRE | FIRMA | FECHA | | | TÍTULO: Cimentación y placas base |
| DIBUJ. | PROYECTO P05 | | 16/10/26 | | | |
| VERIF. | | | | | | |
| APROB. | | | | | | |
| FABR. | | | | | | |
| CALID. | | | | MATERIAL: SEGÚN LISTA DE MATERIALES | | N.º DE DIBUJO **P05-C-02** / **A1** |
| PESO: SEGÚN CAD / BOM | | | | ESCALA: INDICADA | | ESTACIÓN DE DESCARGA BIGBAG / HOJA 2 DE 17 |

# Pórticos transversales ensamblados

**PERFIL ESCALA 1:40**

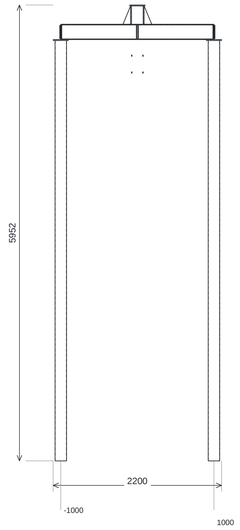


DATUM GLOBAL Y (mm)


**PLANTA ESCALA 1:15**




| POS. CAD | CANT. | DESCRIPCIÓN / CORTE NOMINAL mm | MATERIAL |
|---|---|---|---|
| 1 | 4 | SHS150x150x6 x 5488 | ASTM A500 Gr.B |
| 2 | 2 | IPE200 x 2000 | ASTM A36 |
| 45 | 2 | U01 CAP 200x200x12 | ASTM A36 |
| 46 | 4 | U01 LATERAL 200x240x12 | ASTM A36 |
| 47 | 8 | U01 CALCE 200x20x6 | ASTM A36 |
| 48 | 24 | U01 RIGIDIZADOR 44x175x6 | ASTM A36 |
| 49 | 8 | U01 CARTELA 100x240x12 | ASTM A36 |
| 50 | 4 | P01 CAP COLUMNA 200x200x12 | ASTM A36 |

Cortes nominales agrupados; preparaciones finales identificadas por POS., JF y DXF.

**ISOMÉTRICO A COLOR / REFERENCIA DE MONTAJE**

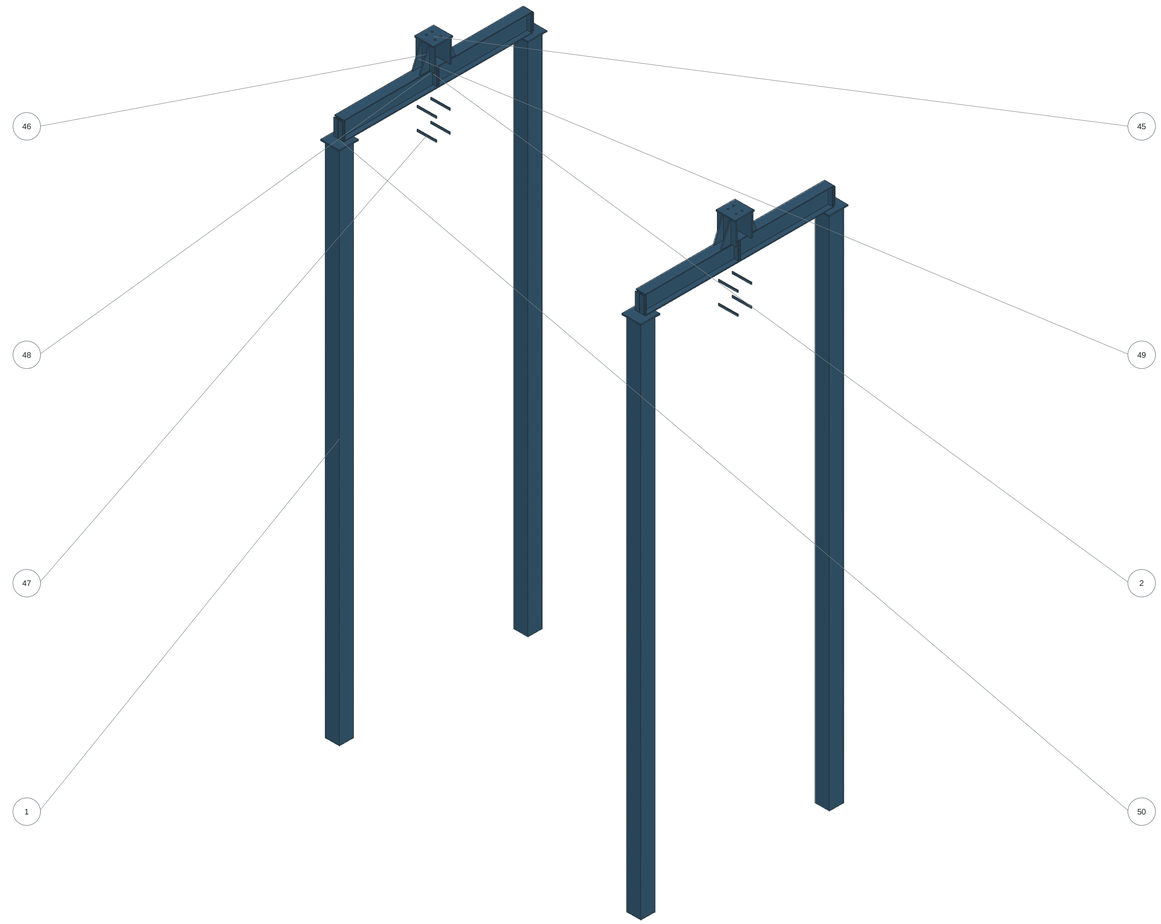


TALADROS PARAMETRIZADOS: 4 / coordenadas locales en Tabla_fabricacion_P05.csv

## NOTAS DE FABRICACIÓN Y MONTAJE

1. Dos pórticos, ejes X = 0 y 3 200; separación Y = 2 000 entre columnas.
2. Columnas SHS150x150x6; travesaños IPE200. Chapas de unión U01 / P01 según BOM.
3. Cotas referidas a la posición nominal montada. Soldadura de taller; montaje desmontable según detalle.

Cotas en mm. ISO2768-m. Soldaduras según cuadro JF. Contornos: CAD/DXF.

**TALADROS DE PIEZAS DEL CONJUNTO / COORDENADAS LOCALES mm / ORIGEN CAD**


P45 T1: D18; X-45 Y-30 Z0; eje Z
P45 T2: D18; X-45 Y30 Z0; eje Z
P45 T3: D18; X45 Y-30 Z0; eje Z
P45 T4: D18; X45 Y30 Z0; eje Z

**P05 - REVISIÓN TÉCNICA**

| | | | | | | |
|---|---|---|---|---|---|---|
| | | | | REBABAR Y ROMPER ARISTAS | NO CAMBIAR LA ESCALA | REVISIÓN **P05** |
| SESUVECA DEL PERÚ | | | | | | |
| | NOMBRE | FIRMA | FECHA | | | TÍTULO: Pórticos transversales ensamblados |
| DIBUJ. | PROYECTO P05 | | 16/10/26 | | | |
| VERIF. | | | | | | |
| APROB. | | | | | | |
| FABR. | | | | | | |
| CALID. | | | | MATERIAL: SEGÚN LISTA DE MATERIALES | | N.º DE DIBUJO **P05-C-03** — **A1** |
| PESO: SEGÚN CAD / BOM | | | | ESCALA: INDICADA | | ESTACIÓN DE DESCARGA BIGBAG — HOJA 3 DE 17 |


# Arriostramiento longitudinal y uniones

**ALZADO ESCALA 1:40**

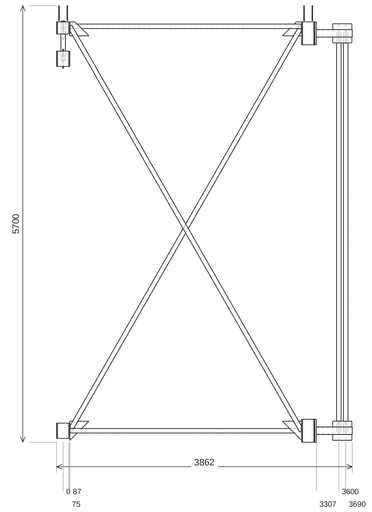


DATUM GLOBAL X (mm)


**PLANTA ESCALA 1:15**

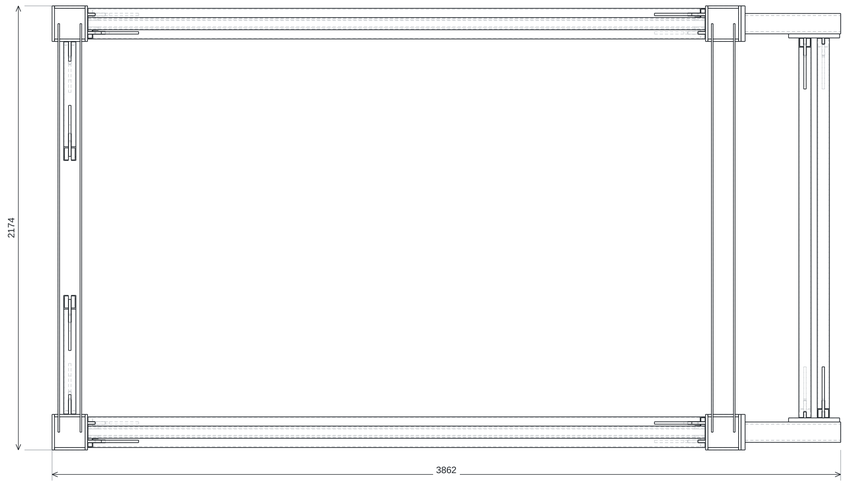


| POS. CAD | CANT. | DESCRIPCIÓN / CORTE NOMINAL mm | MATERIAL |
|---|---|---|---|
| 51 | 8 | U02 COLLAR 150x200x12 | ASTM A36 |
| 52 | 8 | U02 COLLAR 174x200x12 | ASTM A36 |
| 53 | 4 | U02 COLLAR 150x158x12 | ASTM A36 |
| 54 | 4 | U02 COLLAR 174x158x12 | ASTM A36 |
| 55 | 1 | U02 CARTELA BRL-A--1 0 | ASTM A36 |
| 56 | 1 | U02 CARTELA BRL-A--1 1 | ASTM A36 |
| 57 | 1 | U02 CARTELA BRL-B--1 0 | ASTM A36 |
| 58 | 1 | U02 CARTELA BRL-B--1 1 | ASTM A36 |
| 59 | 1 | U02 CARTELA KNE--1 0 | ASTM A36 |
| 60 | 1 | U02 CARTELA KNE--1 1 | ASTM A36 |
| 61 | 1 | U02 CARTELA BRL-A-1 0 | ASTM A36 |
| 62 | 1 | U02 CARTELA BRL-A-1 1 | ASTM A36 |
| 63 | 1 | U02 CARTELA BRL-B-1 0 | ASTM A36 |
| 64 | 1 | U02 CARTELA BRL-B-1 1 | ASTM A36 |
| 65 | 1 | U02 CARTELA KNE-1 0 | ASTM A36 |
| 66 | 1 | U02 CARTELA KNE-1 1 | ASTM A36 |
| 135 | 4 | PORTICO CIERRE IPE200 2000x200x8 | A36 |
| 158 | 1 | BRT A FINAL | A36 |
| 159 | 1 | BRT LENGUETA BRT-A 0 250x250x12 | ASTM A36 |
| 160 | 1 | BRT LENGUETA BRT-A 1 250x250x12 | ASTM A36 |
| 161 | 1 | BRT B FINAL | A36 |
| 162 | 1 | BRT LENGUETA BRT-B 0 250x250x12 | ASTM A36 |
| 163 | 1 | BRT LENGUETA BRT-B 1 250x250x12 | ASTM A36 |
| 164 | 8 | BRT COLLAR 150x300x12 | ASTM A36 |
| 165 | 8 | BRT COLLAR 174x300x12 | ASTM A36 |
| 166 | 4 | BRT RESPALDO 174x300x20 | ASTM A36 |
| 167 | 4 | BRT OUTRIGGER SHS100x100x10 S355 L468 | S355 certificado Fy>=355MPa |
| 168 | 4 | BRT CONTRACARA 250x250x20 | ASTM A36 |
| 187-188,190-191 | 4 | SHS60x60x4 x 6085.65 | ASTM A500 Gr.B |
| 189,192 | 2 | SHS60x60x4 x 748.81 | ASTM A500 Gr.B |
| 200-203 | 4 | SHS60x60x4 x 3050 | ASTM A500 Gr.B |

Cortes nominales agrupados; preparaciones finales identificadas por POS., JF y DXF.

**ISOMÉTRICO A COLOR / REFERENCIA DE MONTAJE**

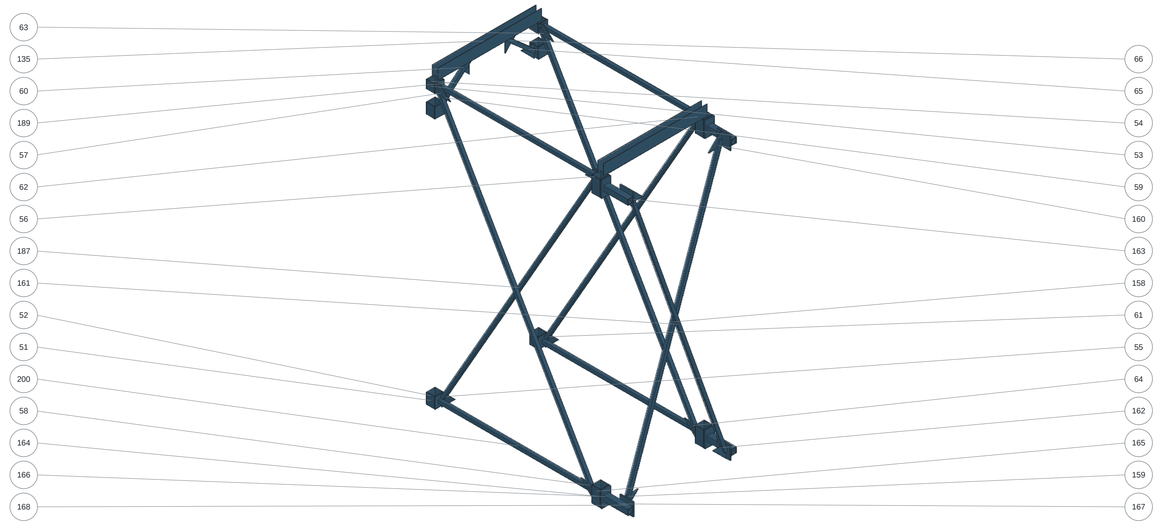


**NOTAS DE FABRICACIÓN Y MONTAJE**

1. Dos planos longitudinales Y = -1 000 y +1 000. Luz entre pórticos: 3 200.
2. Conservar ranuras y recortes de extremos; no soldar las holguras JF identificadas como LUZ.
3. Collares, lengüetas y diagonales: preparaciones según CAD; mantener holguras libres de soldadura.
4. Geometría BRT y posición de collares según CAD final; reacción longitudinal de diseño: 12 kN.


Cotas en mm. ISO2768-m. Soldaduras según cuadro JF. Contornos: CAD/DXF.

**P05 - REVISIÓN TÉCNICA**

| | | | | | | |
|---|---|---|---|---|---|---|
| | | | | REBABAR Y ROMPER ARISTAS | NO CAMBIAR LA ESCALA | REVISIÓN P05 |
| SESUVECA DEL PERÚ | | | | | | |
| | NOMBRE | FIRMA | FECHA | | | TÍTULO: Arriostramiento longitudinal y uniones |
| DIBUJ. | PROYECTO P05 | | 16/10/26 | | | |
| VERIF. | | | | | | |
| APROB. | | | | | | |
| FABR. | | | | | | |
| CALID. | | | | MATERIAL: SEGÚN LISTA DE MATERIALES | | N.º DE DIBUJO P05-C-04 / A1 |
| PESO: SEGÚN CAD / BOM | | | | ESCALA: INDICADA | | ESTACIÓN DE DESCARGA BIGBAG / HOJA 4 DE 17 |


# Viga carril y topes de fin de carrera

**ALZADO ESCALA 1:15**

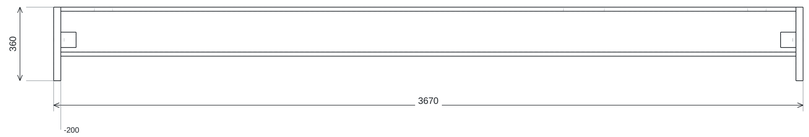


DATUM GLOBAL X (mm)


**PLANTA ESCALA 1:15**

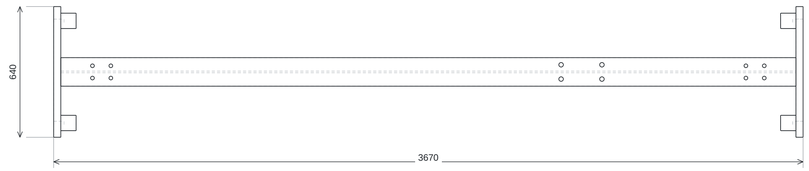


| POS. CAD | CANT. | DESCRIPCIÓN / CORTE NOMINAL mm | MATERIAL |
|---|---|---|---|
| 3 | 1 | I_A240x140x8x20 x 3600 | ASTM A36 |
| 180 | 2 | TOPE PLACA REACCION 640x360x35 | A36 |
| 181 | 4 | TOPE ACE TS75 39 D75 L75 | Elastomero copoliester Shore40D |
| 182 | 4 | TOPE ACE FIJACION M16 L51 ENVELOPE | Tornillo especial suministrado con ACE |

Cortes nominales agrupados; preparaciones finales identificadas por POS., JF y DXF.

**ISOMÉTRICO A COLOR / REFERENCIA DE MONTAJE**

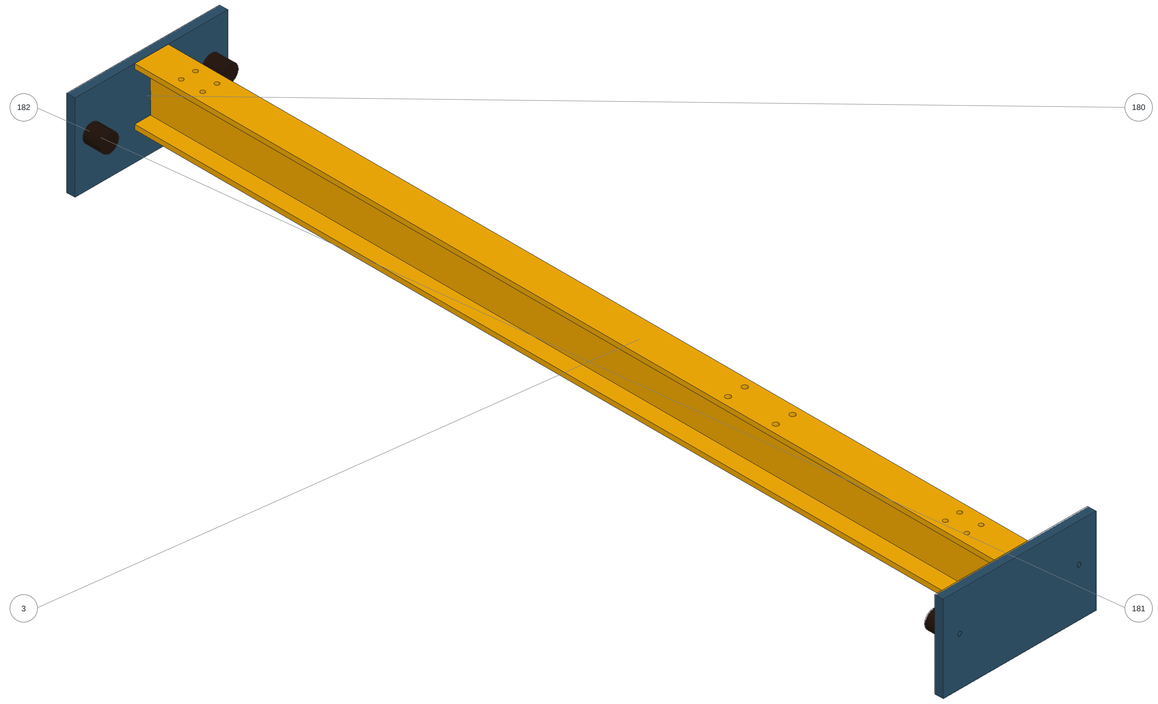


TALADROS PARAMETRIZADOS: 14 / coordenadas locales en Tabla_fabricacion_P05.csv

## NOTAS DE FABRICACIÓN Y MONTAJE

1. Viga fabricada I240x140x8x20; longitud 3 600; ala de rodadura 140 x 20.
2. Dos topes ACE TS75-39 por extremo; placas de reacción 640 x 360 x 35.
3. Carrera nominal del amortiguador 39; energía de proyecto 419,45 J; reacción estructural adoptada 12 kN.
4. Montaje KITO y topes: ver especificación y memoria.

Cotas en mm. ISO2768-m. Soldaduras según cuadro JF. Contornos: CAD/DXF.

**TALADROS DE PIEZAS DEL CONJUNTO / COORDENADAS LOCALES mm / ORIGEN CAD**


P3 B1: D18; X-30 Y95 Z155; eje Y
P3 B2: D18; X30 Y95 Z155; eje Y
P3 B3: D18; X-30 Y95 Z245; eje Y
P3 B4: D18; X30 Y95 Z245; eje Y
P3 B5: D18; X-30 Y95 Z3355; eje Y
P3 B6: D18; X30 Y95 Z3355; eje Y
P3 B7: D18; X-30 Y95 Z3445; eje Y
P3 B8: D18; X30 Y95 Z3445; eje Y
P3 B9: D22; X-35 Y99 Z2450; eje Y
P3 B10: D22; X35 Y99 Z2450; eje Y
P3 B11: D22; X-35 Y99 Z2650; eje Y
P3 B12: D22; X35 Y99 Z2650; eje Y
P180 T1: D18; X-250 Y20 Z0; eje Z
P180 T2: D18; X250 Y20 Z0; eje Z

**P05 - REVISIÓN TÉCNICA**

| | | | | | | |
|---|---|---|---|---|---|---|
| | | | | REBABAR Y ROMPER ARISTAS | NO CAMBIAR LA ESCALA | REVISIÓN **P05** |
| SESUVECA DEL PERÚ | | | | | | |
| | NOMBRE | FIRMA | FECHA | | | TÍTULO: Viga carril y topes de fin de carrera |
| DIBUJ. | PROYECTO P05 | | 16/10/26 | | | |
| VERIF. | | | | | | |
| APROB. | | | | | | |
| FABR. | | | | | | |
| CALID. | | | | MATERIAL: SEGÚN LISTA DE MATERIALES | | N.º DE DIBUJO **P05-C-05** — **A1** |
| PESO: SEGÚN CAD / BOM | | | | ESCALA: INDICADA | | ESTACIÓN DE DESCARGA BIGBAG — HOJA 5 DE 17 |


# Bastidor de tolva ensamblado

**ALZADO ESCALA 1:20**

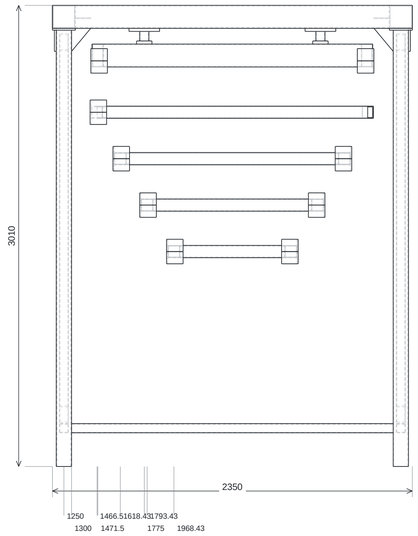


DATUM GLOBAL X (mm)


**PLANTA ESCALA 1:15**

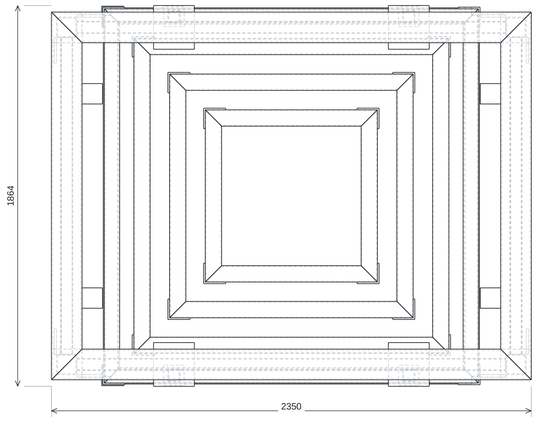


| POS. CAD | CANT. | DESCRIPCIÓN / CORTE NOMINAL mm | MATERIAL |
|---|---|---|---|
| 4 | 4 | SHS100x100x5 x 2848 | ASTM A500 Gr.B |
| 5 | 2 | SHS150x150x6 x 2200 | ASTM A500 Gr.B |
| 6 | 2 | SHS150x150x6 x 1650 | ASTM A500 Gr.B |
| 7 | 2 | SHS60x60x4 x 2100 | ASTM A500 Gr.B |
| 8 | 2 | SHS60x60x4 x 1550 | ASTM A500 Gr.B |
| 9-10 | 4 | SHS80x80x4 x 763.14 | ASTM A500 Gr.B |
| 11-12 | 4 | SHS80x80x4 x 1113.14 | ASTM A500 Gr.B |
| 13 | 4 | SHS80x80x4 x 1463.14 | ASTM A500 Gr.B |
| 14-15 | 4 | RHS150x75x5 x 1757 | ASTM A500 Gr.B |
| 16 | 2 | SHS60x60x4 x 2882.26 | ASTM A500 Gr.B |
| 36 | 4 | SHS60x60x4 x 62.41 | ASTM A500 Gr.B |
| 67 | 4 | U04 CAP PATA 150x150x12 | ASTM A36 |
| 70 | 8 | U04 CARTELA 125x150x12 | ASTM A36 |
| 71 | 36 | U04 ANGULO ARMADO 2x100x80x8 | ASTM A36 |
| 72 | 4 | T01 ASIENTO 100x100x6 | ASTM A36 |
| 73 | 4 | T02 ASIENTO INFERIOR 100x100x20 | ASTM A36 |
| 74 | 4 | T02 ASIENTO SUPERIOR 200x214x20 | ASTM A36 |
| 175 | 1 | HR 2p3124 1 FINAL | A36 |
| 176 | 1 | HR 2p3124 2 FINAL | A36 |
| 177 | 1 | HR 2p3124 3 FINAL | A36 |
| 178 | 1 | HR 2p3124 4 FINAL | A36 |

Cortes nominales agrupados; preparaciones finales identificadas por POS., JF y DXF.

**ISOMÉTRICO A COLOR / REFERENCIA DE MONTAJE**

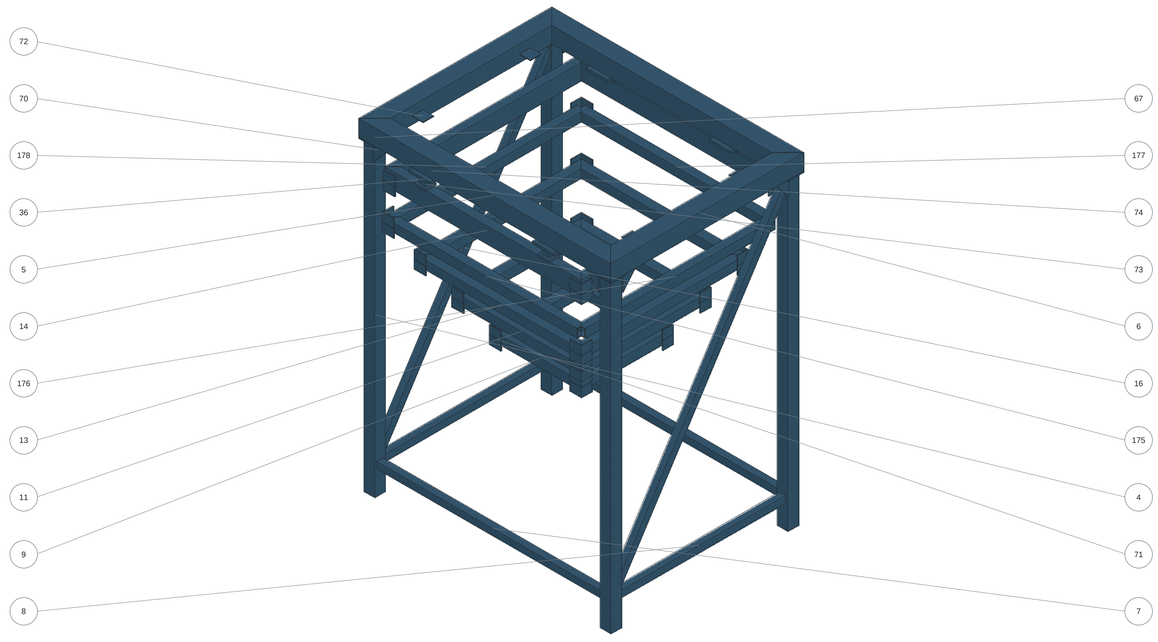


**NOTAS DE FABRICACIÓN Y MONTAJE**

1. Cuatro patas SHS100x100x5; marco superior SHS150x150x6. Longitudes y cantidades en BOM.
2. Ejes de patas X = 1 250 / 3 450; Y = -825 / +825.
3. Mantener posiciones de anillos y apoyos; cortes de encuentro incluidos en CAD / DXF.
4. Soldadura de taller según conjunto y espesores; mantener libres las superficies de apoyo y revestimiento.


Cotas en mm. ISO2768-m. Soldaduras según cuadro JF. Contornos: CAD/DXF.

**P05 - REVISIÓN TÉCNICA**


| | | | | | | |
|---|---|---|---|---|---|---|
| | | | | REBABAR Y ROMPER ARISTAS | NO CAMBIAR LA ESCALA | REVISIÓN **P05** |
| SESUVECA DEL PERÚ | | | | | | |
| | NOMBRE | FIRMA | FECHA | | | TÍTULO: Bastidor de tolva ensamblado |
| DIBUJ. | PROYECTO P05 | | 16/10/26 | | | |
| VERIF. | | | | | | |
| APROB. | | | | | | |
| FABR. | | | | | | |
| CALID. | | | | MATERIAL: SEGÚN LISTA DE MATERIALES | | N.º DE DIBUJO **P05-C-06** — **A1** |
| PESO: SEGÚN CAD / BOM | | | | ESCALA: INDICADA | | ESTACIÓN DE DESCARGA BIGBAG — HOJA 6 DE 17 |

# Tolva, anillos y revestimiento

**ALZADO ESCALA 1:10**

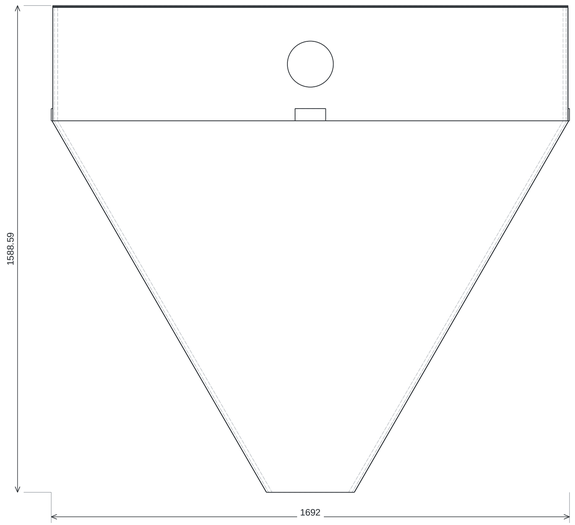



**PLANTA ESCALA 1:15**

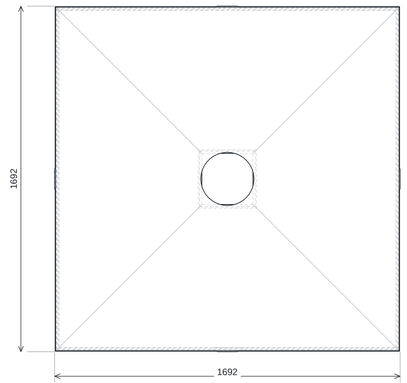


| POS. CAD | CANT. | DESCRIPCIÓN / CORTE NOMINAL mm | MATERIAL |
|---|---|---|---|
| 37 | 4 | TOL PANEL CONO 6mm | ASTM A36 |
| 38 | 3 | TOL PANEL CUERPO 6mm | ASTM A36 |
| 39 | 1 | TOL PANEL CUERPO DN150 6mm | ASTM A36 |
| 40 | 1 | TOL TAPA POLVO 1662x1662x3 | ASTM A36 |
| 41 | 1 | TOL | EPDM |
| 85 | 4 | LINER CONO UHMW10 | UHMWPE disipativo |
| 86 | 3 | LINER CUERPO UHMW10 | UHMWPE disipativo |
| 87 | 1 | LINER CUERPO UHMW10 DN150 | UHMWPE disipativo |
| 179 | 4 | HR4 PAD 100x40x5 | ASTM A36 |

Cortes nominales agrupados; preparaciones finales identificadas por POS., JF y DXF.

**ISOMÉTRICO A COLOR / REFERENCIA DE MONTAJE**

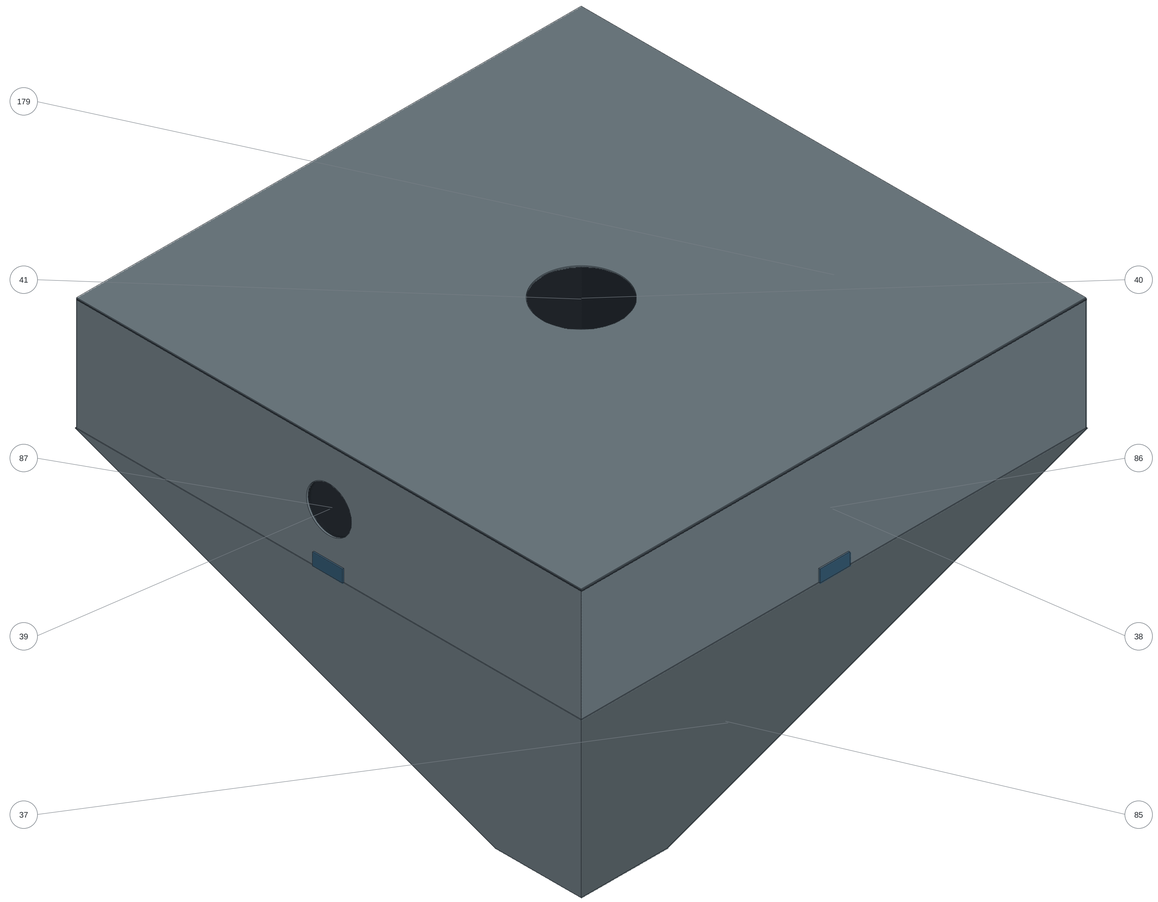


TALADROS PARAMETRIZADOS: 3 / coordenadas locales en Tabla_fabricacion_P05.csv

## NOTAS DE FABRICACIÓN Y MONTAJE

1. Boca interior libre 1 650; salida libre 250; paredes a 60 grados.
2. Tronco piramidal: altura interior 1 212,44. Cuerpo interior: altura 370,15.
3. Revestimiento UHMWPE disipativo de 10 mm; dimensiones interiores libres después del revestimiento.
4. Puerto DN150 con paso continuo a través de casco y liner; no obstruir el conducto.
5. Volumen útil y ensayo de descarga por gravedad según memoria.

Cotas en mm. ISO2768-m. Soldaduras según cuadro JF. Contornos: CAD/DXF.

**TALADROS DE PIEZAS DEL CONJUNTO / COORDENADAS LOCALES mm / ORIGEN CAD**

P39 B1: D150; X0 Y185.08 Z9; eje Z
P40 T1: D260; X0 Y0 Z0; eje Z


P87 B1: D150; X0 Y185.08 Z-1; eje Z

**P05 - REVISIÓN TÉCNICA**

| | | | | | | |
|---|---|---|---|---|---|---|
| | | | | REBABAR Y ROMPER ARISTAS | NO CAMBIAR LA ESCALA | REVISIÓN **P05** |
| SESUVECA DEL PERÚ | | | | | | |
| | NOMBRE | FIRMA | FECHA | | | TÍTULO: Tolva, anillos y revestimiento |
| DIBUJ. | PROYECTO P05 | | 16/10/26 | | | |
| VERIF. | | | | | | |
| APROB. | | | | | | |
| FABR. | | | | | | |
| CALID. | | | | MATERIAL: SEGÚN LISTA DE MATERIALES | | N.º DE DIBUJO **P05-C-07** / **A1** |
| PESO: SEGÚN CAD / BOM | | | | ESCALA: INDICADA | | ESTACIÓN DE DESCARGA BIGBAG / HOJA 7 DE 17 |


# Cortador y parrilla de apoyo de bolsa

**ALZADO ESCALA 1:8**

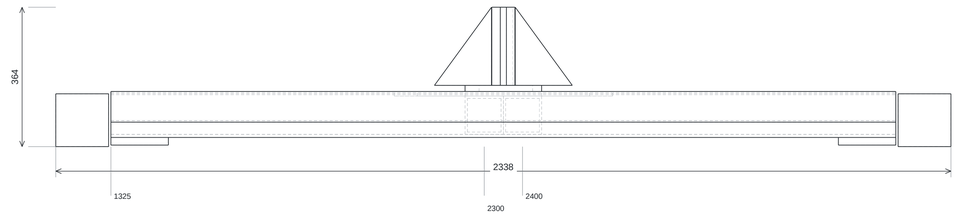


DATUM GLOBAL X (mm)


**PLANTA ESCALA 1:8**

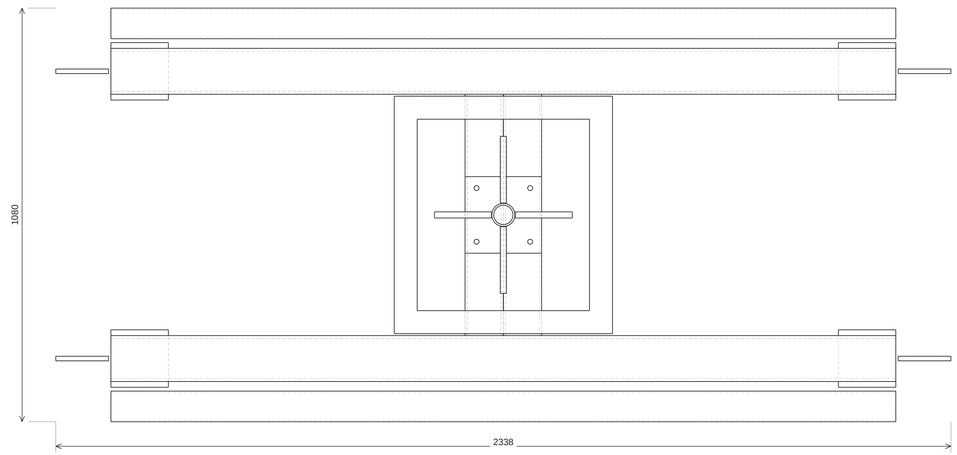


| POS. CAD | CANT. | DESCRIPCIÓN / CORTE NOMINAL mm | MATERIAL |
|---|---|---|---|
| 17 | 2 | SHS80x80x4 x 2050 | ASTM A500 Gr.B |
| 88 | 1 | CORTE ALETA 1 304 t16 | AISI304 |
| 89 | 1 | CORTE ALETA 2 304 t16 | AISI304 |
| 90 | 1 | CORTE ALETA 3 304 t16 | AISI304 |
| 91 | 1 | CORTE ALETA 4 304 t16 | AISI304 |
| 92 | 1 | CORTE MASTIL 60p3x5 | AISI304 |
| 93 | 1 | CORTE MARCO 570x620x12 | AISI 304 |
| 94 | 1 | CORTE BASE 200x200x16 | AISI 304 |
| 169 | 1 | GRID 0p25 FINAL | A36 |
| 170 | 4 | GRID ASIENTO 150x150x20 | ASTM A36 |
| 171 | 4 | GRID DIAFRAGMA HUP 138x138x12 | ASTM A36 |
| 172 | 1 | GRID 0p25 FINAL | A36 |
| 173 | 2 | CORTE TRAVESANO100x100x6 L630 | A36 |
| 174 | 1 | CORTE ESPACIADOR CENTRAL 200x200x12 | AISI 304 |

Cortes nominales agrupados; preparaciones finales identificadas por POS., JF y DXF.

**ISOMÉTRICO A COLOR / REFERENCIA DE MONTAJE**

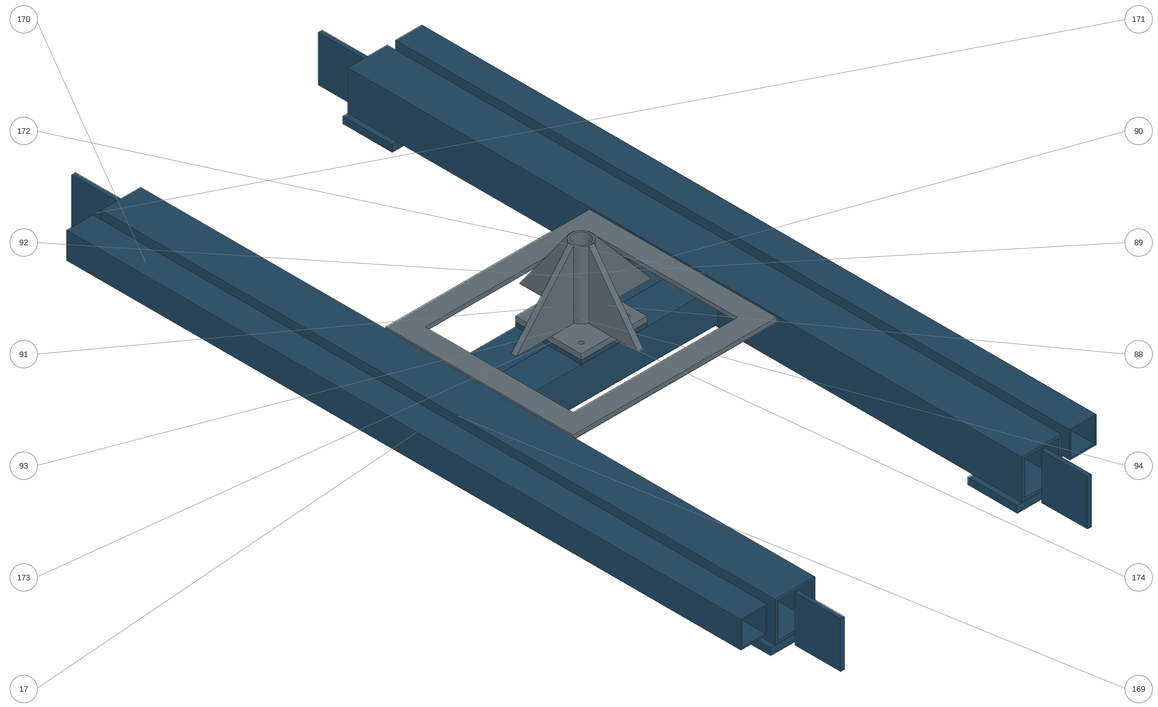


TALADROS PARAMETRIZADOS: 4 / coordenadas locales en Tabla_fabricacion_P05.csv

**NOTAS DE FABRICACIÓN Y MONTAJE**

1. Cuchilla piramidal fija de cuatro filos AISI304; chapas de filo t16 según BOM.
2. Mástil, marco y travesaños forman un conjunto. Mantener posición centrada sobre salida.
3. Altura de punta Z = 3 230. El bigbag se desplaza con fondo a Z = 3 520.
4. Sustituir filos con equipo aislado, bolsa retirada y protección de acceso instalada.

Cotas en mm. ISO2768-m. Soldaduras según cuadro JF. Contornos: CAD/DXF.

**TALADROS DE PIEZAS DEL CONJUNTO / COORDENADAS LOCALES mm / ORIGEN CAD**


P94 T1: D13; X-70 Y-70 Z0; eje Z
P94 T2: D13; X70 Y-70 Z0; eje Z
P94 T3: D13; X-70 Y70 Z0; eje Z
P94 T4: D13; X70 Y70 Z0; eje Z

**P05 - REVISIÓN TÉCNICA**


| | | | | | | |
|---|---|---|---|---|---|---|
| | | | | REBABAR Y ROMPER ARISTAS | NO CAMBIAR LA ESCALA | REVISIÓN **P05** |
| SESUVECA DEL PERÚ | | | | | | |
| | NOMBRE | FIRMA | FECHA | | | TÍTULO: Cortador y parrilla de apoyo de bolsa |
| DIBUJ. | PROYECTO P05 | | 16/10/26 | | | |
| VERIF. | | | | | | |
| APROB. | | | | | | |
| FABR. | | | | | | |
| CALID. | | | | MATERIAL: SEGÚN LISTA DE MATERIALES | | N.º DE DIBUJO **P05-C-08** — **A1** |
| PESO: SEGÚN CAD / BOM | | | | ESCALA: INDICADA | | ESTACIÓN DE DESCARGA BIGBAG — HOJA 8 DE 17 |

# Compuerta de descarga ensamblada

**PLANTA ESCALA 1:5**

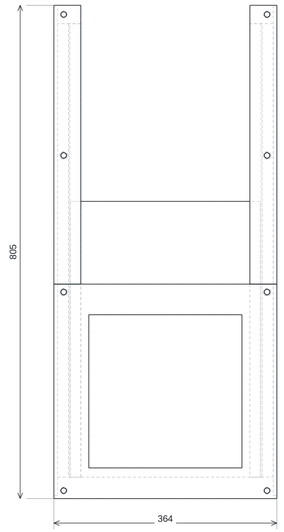



**ALZADO ESCALA 1:2**

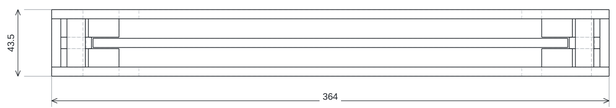


| POS. CAD | CANT. | DESCRIPCIÓN / CORTE NOMINAL mm | MATERIAL |
|---|---|---|---|
| 100 | 1 | MG02 FLANGE 364x350x6 | ASTM A36 |
| 101 | 1 | MG03 FLANGE 364x350x6 | ASTM A36 |
| 102 | 1 | MG01 HOJA 310x450x6 | ASTM A36 |
| 103 | 1 | MG04 SUP 1 | ASTM A36 |
| 104 | 1 | MG04 SUP 2 | ASTM A36 |
| 105 | 1 | MG05 INF 1 | ASTM A36 |
| 106 | 1 | MG05 INF 2 | ASTM A36 |
| 107 | 1 | MG06 ESP 1 | ASTM A36 |
| 108 | 1 | MG06 ESP 2 | ASTM A36 |
| 109 | 1 | MG07 UHMW SUP 1 | UHMW-PE |
| 110 | 1 | MG07 UHMW SUP 2 | UHMW-PE |
| 111 | 1 | MG08 UHMW INF 1 | UHMW-PE |
| 112 | 1 | MG08 UHMW INF 2 | UHMW-PE |
| 113 | 1 | MG09 UHMW LADO 1 | UHMW-PE |
| 114 | 1 | MG09 UHMW LADO 2 | UHMW-PE |
| 115 | 8 | MG10 CASQUILLO 12x9 L31p5 | ACERO |

Cortes nominales agrupados; preparaciones finales identificadas por POS., JF y DXF.

**ISOMÉTRICO A COLOR / REFERENCIA DE MONTAJE**

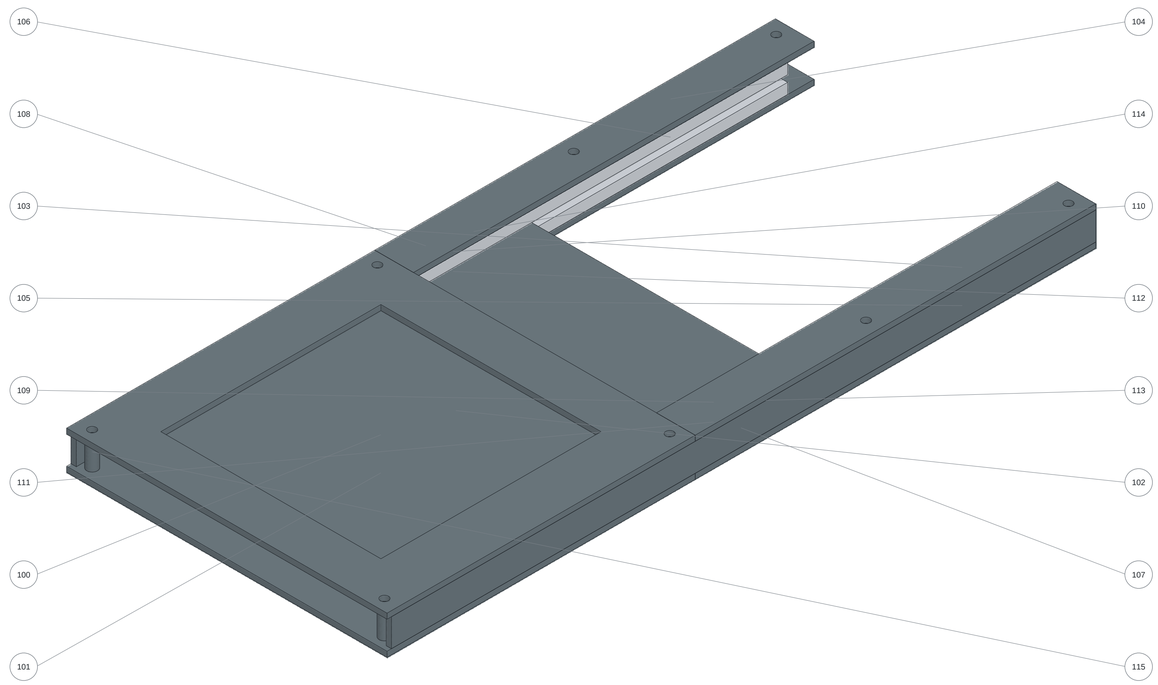


TALADROS PARAMETRIZADOS: 16 / coordenadas locales en Tabla_fabricacion_P05.csv

## NOTAS DE FABRICACIÓN Y MONTAJE

1. Hoja de cierre, guías y liners se muestran en posición cerrada de referencia.
2. Accionamiento: cremallera y piñón con reducción manual; pasador cautivo de bloqueo.
3. Ajustar paralelismo de guías y comprobar recorrido completo antes del montaje de la guarda.
4. Conservar espesores de casquillos y UHMWPE del CAD; ajustar fijaciones manteniendo libre la corredera.

Cotas en mm. ISO2768-m. Soldaduras según cuadro JF. Contornos: CAD/DXF.

**TALADROS DE PIEZAS DEL CONJUNTO / COORDENADAS LOCALES mm / ORIGEN CAD**


P100 T1: D9; X-166 Y-162 Z0; eje Z
P100 T2: D9; X166 Y-162 Z0; eje Z
P100 T3: D9; X-166 Y162 Z0; eje Z
P100 T4: D9; X166 Y162 Z0; eje Z
P101 T1: D9; X-166 Y-162 Z0; eje Z
P101 T2: D9; X166 Y-162 Z0; eje Z
P101 T3: D9; X-166 Y162 Z0; eje Z
P101 T4: D9; X166 Y162 Z0; eje Z
P103 T1: D9; X6 Y-17.5 Z0; eje Z
P103 T2: D9; X6 Y212.5 Z0; eje Z
P104 T1: D9; X-6 Y-17.5 Z0; eje Z
P104 T2: D9; X-6 Y212.5 Z0; eje Z
P105 T1: D9; X6 Y-17.5 Z0; eje Z
P105 T2: D9; X6 Y212.5 Z0; eje Z
P106 T1: D9; X-6 Y-17.5 Z0; eje Z
P106 T2: D9; X-6 Y212.5 Z0; eje Z

**P05 - REVISIÓN TÉCNICA**


| | | | | | | |
|---|---|---|---|---|---|---|
| | | | | REBABAR Y ROMPER ARISTAS | NO CAMBIAR LA ESCALA | REVISIÓN P05 |
| SESUVECA DEL PERÚ | | | | | | |
| | NOMBRE | FIRMA | FECHA | | | TÍTULO: Compuerta de descarga ensamblada |
| DIBUJ. | PROYECTO P05 | | 16/10/26 | | | |
| VERIF. | | | | | | |
| APROB. | | | | | | |
| FABR. | | | | | | |
| CALID. | | | | MATERIAL: SEGÚN LISTA DE MATERIALES | | N.º DE DIBUJO P05-C-09 — A1 |
| PESO: SEGÚN CAD / BOM | | | | ESCALA: INDICADA | | ESTACIÓN DE DESCARGA BIGBAG — HOJA 9 DE 17 |

# Guarda, ensacado y captación

**ALZADO ESCALA 1:15**

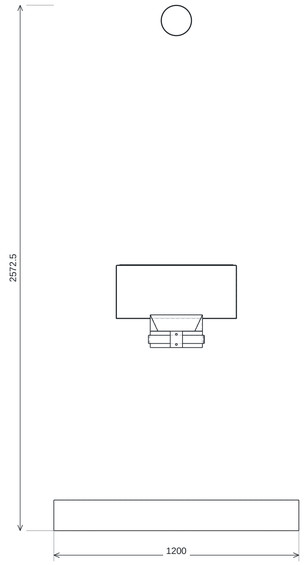



**PLANTA ESCALA 1:15**

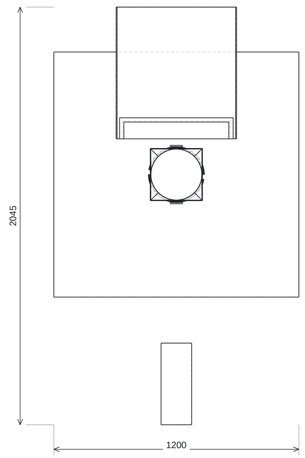


| POS. CAD | CANT. | DESCRIPCIÓN / CORTE NOMINAL mm | MATERIAL |
|---|---|---|---|
| 116 | 1 | MS01 TRANSICION CUADRADO REDONDO 3 | ASTM A36 |
| 117 | 1 | MS02 CUELLO ID250 OD256 L80 | ACERO |
| 118 | 2 | MS03 SECTOR 170deg ID268 t3 H40 | ASTM A36 |
| 119 | 2 | MS04 LINER EPDM3 SECTOR 170 | EPDM |
| 120 | 2 | MS05 SOPORTE 60x80x6 | ASTM A36 |
| 121 | 1 | SACO 25 50kg | SEGÚN CATÁLOGO / COMPRA |
| 122 | 1 | BALANZA 2t 1200 | SEGÚN CATÁLOGO / COMPRA |
| 125 | 1 | CAPTACION POLVO DN150 | SEGÚN CATÁLOGO / COMPRA |
| 126 | 1 | MG11 GUARDA U 590x645x260 R3 t2 | ASTM A36 |
| 127 | 1 | MG12 GUARDA FONDO 590x645x2 | ASTM A36 |
| 128 | 1 | MG13 GUARDA TESTERO 586x258x2 | ASTM A36 |
| 129 | 1 | MG14 | Junta flexible disipativa compatible con polvo; seleccion final conforme materiales del proyecto |

Cortes nominales agrupados; preparaciones finales identificadas por POS., JF y DXF.

**ISOMÉTRICO A COLOR / REFERENCIA DE MONTAJE**

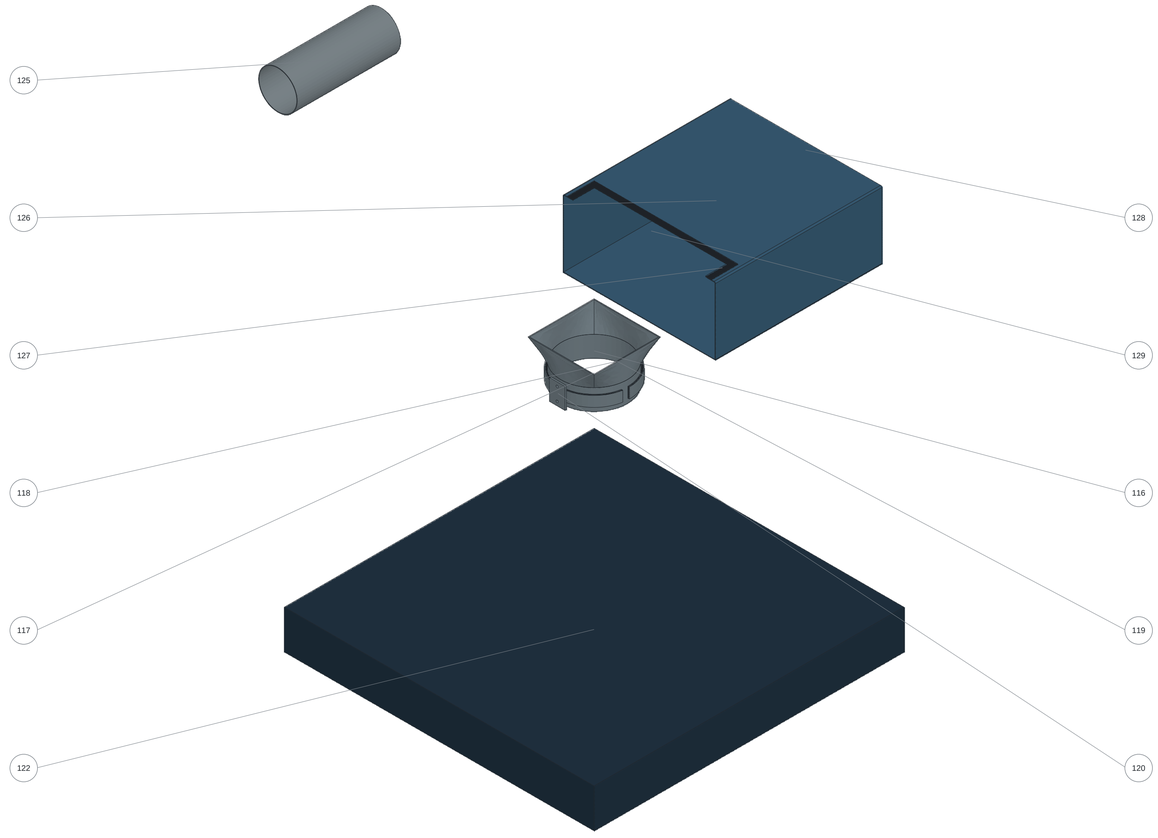


TALADROS PARAMETRIZADOS: 2 / coordenadas locales en Tabla_fabricacion_P05.csv

## NOTAS DE FABRICACIÓN Y MONTAJE

1. Guarda cerrada de compuerta: envolvente final 590 x 645 x 262.
2. Cota superior de recinto protegido Z = 3 430; despeje nominal de traslado: 90.
3. Salida libre DN250; interfaz de saco y balanza de plataforma 1 200 x 1 200 / 2 t.
4. Captación DN150: 800 m3/h a 1 500 Pa en colector; balance de presión según memoria.
5. Conexiones desmontables para limpieza y mantenimiento. Protección contra polvo combustible según análisis del proyecto.

Cotas en mm. ISO2768-m. Soldaduras según cuadro JF. Contornos: CAD/DXF.

**TALADROS DE PIEZAS DEL CONJUNTO / COORDENADAS LOCALES mm / ORIGEN CAD**

P120 T1: D9; X0 Y-25 Z0; eje Z


P120 T2: D9; X0 Y25 Z0; eje Z

**P05 - REVISIÓN TÉCNICA**

| | | | | | | |
|---|---|---|---|---|---|---|
| | | | | REBABAR Y ROMPER ARISTAS | NO CAMBIAR LA ESCALA | REVISIÓN **P05** |
| SESUVECA DEL PERÚ | | | | | | |
| | NOMBRE | FIRMA | FECHA | | | TÍTULO: Guarda, ensacado y captación |
| DIBUJ. | PROYECTO P05 | | 16/10/26 | | | |
| VERIF. | | | | | | |
| APROB. | | | | | | |
| FABR. | | | | | | |
| CALID. | | | | MATERIAL: SEGÚN LISTA DE MATERIALES | | N.º DE DIBUJO **P05-C-10** / **A1** |
| PESO: SEGÚN CAD / BOM | | | | ESCALA: INDICADA | | ESTACIÓN DE DESCARGA BIGBAG / HOJA 10 DE 17 |


# Carro, suspensión y traba de posición

**ALZADO ESCALA 1:5**

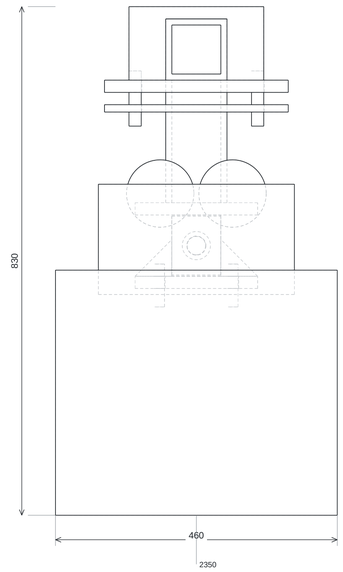


DATUM GLOBAL X (mm)


**PERFIL ESCALA 1:8**

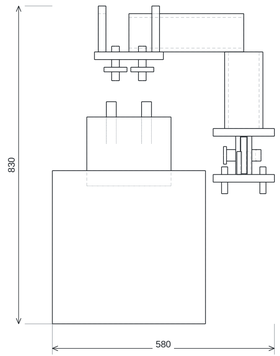


| POS. CAD | CANT. | DESCRIPCIÓN / CORTE NOMINAL mm | MATERIAL |
|---|---|---|---|
| 95 | 1 | TECLE 2IERENCIA | SEGÚN CATÁLOGO / COMPRA |
| 96 | 1 | CARRO MOTORIZADOERENCIA | SEGÚN CATÁLOGO / COMPRA |
| 97 | 1 | CADENA ENVELOPE | SEGÚN CATÁLOGO / COMPRA |
| 98 | 1 | BIGBAG 1000x1000x1000 | SEGÚN CATÁLOGO / COMPRA |
| 99 | 4 | ASA BIGBAG | SEGÚN CATÁLOGO / COMPRA |
| 133 | 8 | ANCLA ARANDELA D30 D18 t3 | SEGÚN CATÁLOGO / COMPRA |
| 134 | 8 | ANCLA TUERCA M16 AF24 H13 | Acero clase8 |
| 136 | 1 | TC01 SADDLE 300x180x20 | ASTM A36 |
| 137 | 2 | TC02 DUPLICADOR ALA 300x60x12 | ASTM A36 |
| 138 | 1 | TC03 BRAZO SHS100x100x10 S355 L300 | S355 certificado |
| 139 | 1 | TC04 POSTE SHS100x100x10 S355 L200 | S355 certificado |
| 140 | 1 | TC05 PLACA HORQUILLA 200x160x20 | ASTM A36 |
| 141 | 2 | TC06 OREJA 80x100x12 D31 | ASTM A36 |
| 142 | 1 | TC07 RECEPTOR 80x96x16 D31 | A36 |
| 143 | 1 | TC08 ADAPTADOR 200x160x20 4D18 | A36 |
| 144 | 2 | TC09 CARTABON SADDLE 220x120x20 | ASTM A36 |
| 145 | 2 | TC10 CARTABON RECEPTOR 60x60x12 | ASTM A36 |
| 146 | 1 | TC11 PASADOR D30 L90 FY355 | Acero certificado Fy>=355MPa |
| 147 | 1 | TC12 CABEZA D46 L8 | ASTM A36 / SEGÚN MEMORIA |
| 148 | 1 | TC13 CLIP R D3 L38 | SEGÚN CATÁLOGO / COMPRA |
| 149 | 1 | TC17 OJAL CABLE 40x12x3 | ASTM A36 |
| 150 | 1 | TC18 CABLE CAUTIVO D3 SEG1 | Cable inoxidable cautivo flexible; longitud min350mm |
| 151 | 1 | TC18 CABLE CAUTIVO D3 SEG2 | Cable inoxidable cautivo flexible; longitud min350mm |
| 152 | 1 | TC18 CABLE CAUTIVO D3 SEG3 | Cable inoxidable cautivo flexible; longitud min350mm |
| 153 | 4 | TC14 PERNO M20 L90 8p8 | Clase8.8 |
| 154 | 8 | TC15 ARANDELA D37 D22 t3 | SEGÚN CATÁLOGO / COMPRA |
| 155 | 8 | TC16 TUERCA M20 D36 ID21 H16 | SEGÚN CATÁLOGO / COMPRA |
| 156 | 4 | TC19 ESPARRAGO M16 L70 8p8 | Clase8.8 |
| 157 | 4 | KITO RUEDA D110 PASO118 | SEGÚN CATÁLOGO / COMPRA |

Cortes nominales agrupados; preparaciones finales identificadas por POS., JF y DXF.

**ISOMÉTRICO A COLOR / REFERENCIA DE MONTAJE**

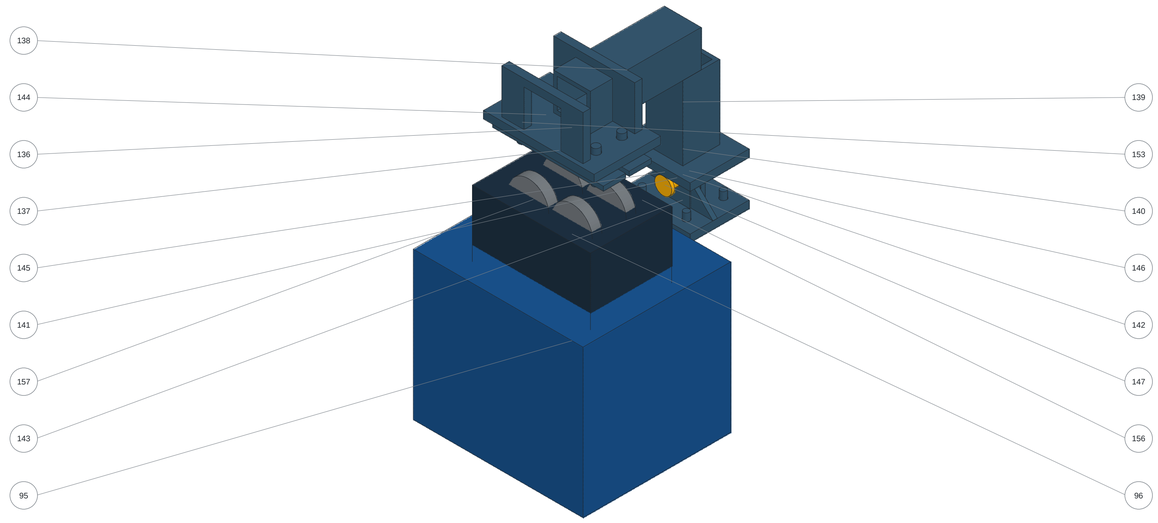


TALADROS PARAMETRIZADOS: 14 / coordenadas locales en Tabla_fabricacion_P05.csv

## NOTAS DE FABRICACIÓN Y MONTAJE

1. Referencia comercial KITO SHER2M020IS-IS / 2 t; C de catálogo = 475.
2. Mantener el conjunto comercial de tecle y carro según especificación de compra.
3. Pasador cautivo D30 Fy >=355 MPa; dos orejas t12 y placa receptora t16; taladros D31.
4. Inserción únicamente con carro detenido. Inhibir traslación con pasador insertado.
5. Patrones de fijación TC y tolerancias de montaje según detalle / CAD.

Cotas en mm. ISO2768-m. Soldaduras según cuadro JF. Contornos: CAD/DXF.

**TALADROS DE PIEZAS DEL CONJUNTO / COORDENADAS LOCALES mm / ORIGEN CAD**


P136 T1: D22; X-100 Y-35 Z0; eje Z
P136 T2: D22; X-100 Y35 Z0; eje Z
P136 T3: D22; X100 Y-35 Z0; eje Z
P136 T4: D22; X100 Y35 Z0; eje Z
P137 T1: D22; X-100 Y0 Z0; eje Z
P137 T2: D22; X100 Y0 Z0; eje Z
P141 T1: D31; X0 Y0 Z0; eje Z
P142 T1: D31; X0 Y0 Z0; eje Z
P143 T1: D18; X-60 Y-50 Z0; eje Z
P143 T2: D18; X-60 Y50 Z0; eje Z
P143 T3: D18; X60 Y-50 Z0; eje Z
P143 T4: D18; X60 Y50 Z0; eje Z
P146 B1: D4.5; X0 Y16 Z78; eje Y
P149 T1: D4; X12 Y0 Z0; eje Z

**P05 - REVISIÓN TÉCNICA**

| | | | | | | |
|---|---|---|---|---|---|---|
| | | | | REBABAR Y ROMPER ARISTAS | NO CAMBIAR LA ESCALA | REVISIÓN P05 |
| SESUVECA DEL PERÚ | | | | | | |
| | NOMBRE | FIRMA | FECHA | | | TÍTULO: Carro, suspensión y traba de posición |
| DIBUJ. | PROYECTO P05 | | 16/10/26 | | | |
| VERIF. | | | | | | |
| APROB. | | | | | | |
| FABR. | | | | | | |
| CALID. | | | | MATERIAL: SEGÚN LISTA DE MATERIALES | | N.º DE DIBUJO P05-C-11 / A1 |
| PESO: SEGÚN CAD / BOM | | | | ESCALA: INDICADA | | ESTACIÓN DE DESCARGA BIGBAG / HOJA 11 DE 17 |


# Plataforma de acceso ensamblada

**PLANTA ESCALA 1:8**

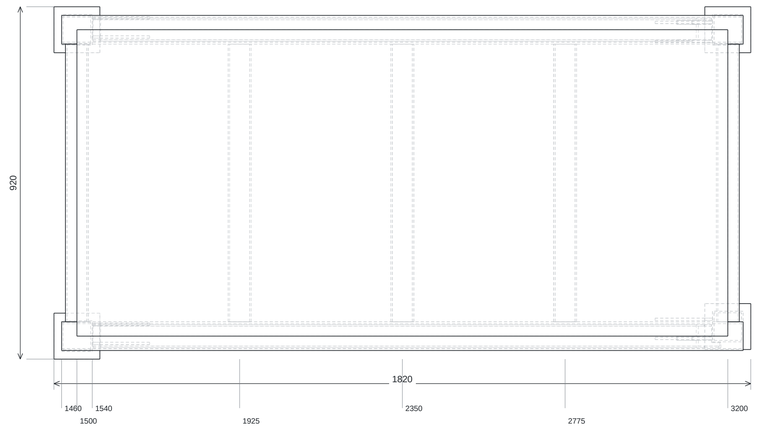


DATUM GLOBAL X (mm)


**ALZADO ESCALA 1:15**

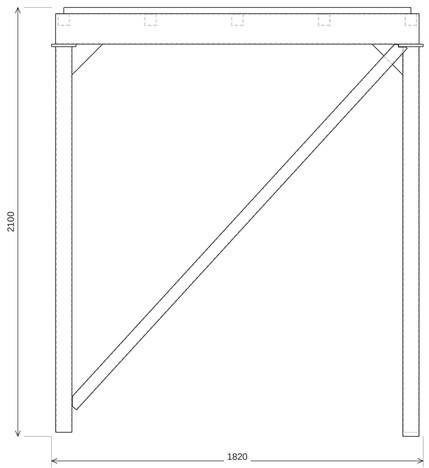


| POS. CAD | CANT. | DESCRIPCIÓN / CORTE NOMINAL mm | MATERIAL |
|---|---|---|---|
| 18 | 3 | SHS80x80x4 x 1888 | ASTM A500 Gr.B |
| 19 | 1 | SHS80x80x4 x 1908 | ASTM A500 Gr.B |
| 20 | 2 | RHS150x75x5 x 1780 | ASTM A500 Gr.B |
| 21 | 5 | SHS60x60x4 x 725 | ASTM A500 Gr.B |
| 68 | 4 | P02 CAP COLUMNA 120x120x12 | ASTM A36 |
| 69 | 8 | P02 CARTELA 150x150x6 | ASTM A36 |
| 123 | 1 | PLATAFORMA REJILLA COMERCIAL | SEGÚN CATÁLOGO / COMPRA |
| 193-194 | 2 | SHS60x60x4 x 2399.44 | ASTM A500 Gr.B |

Cortes nominales agrupados; preparaciones finales identificadas por POS., JF y DXF.

**ISOMÉTRICO A COLOR / REFERENCIA DE MONTAJE**

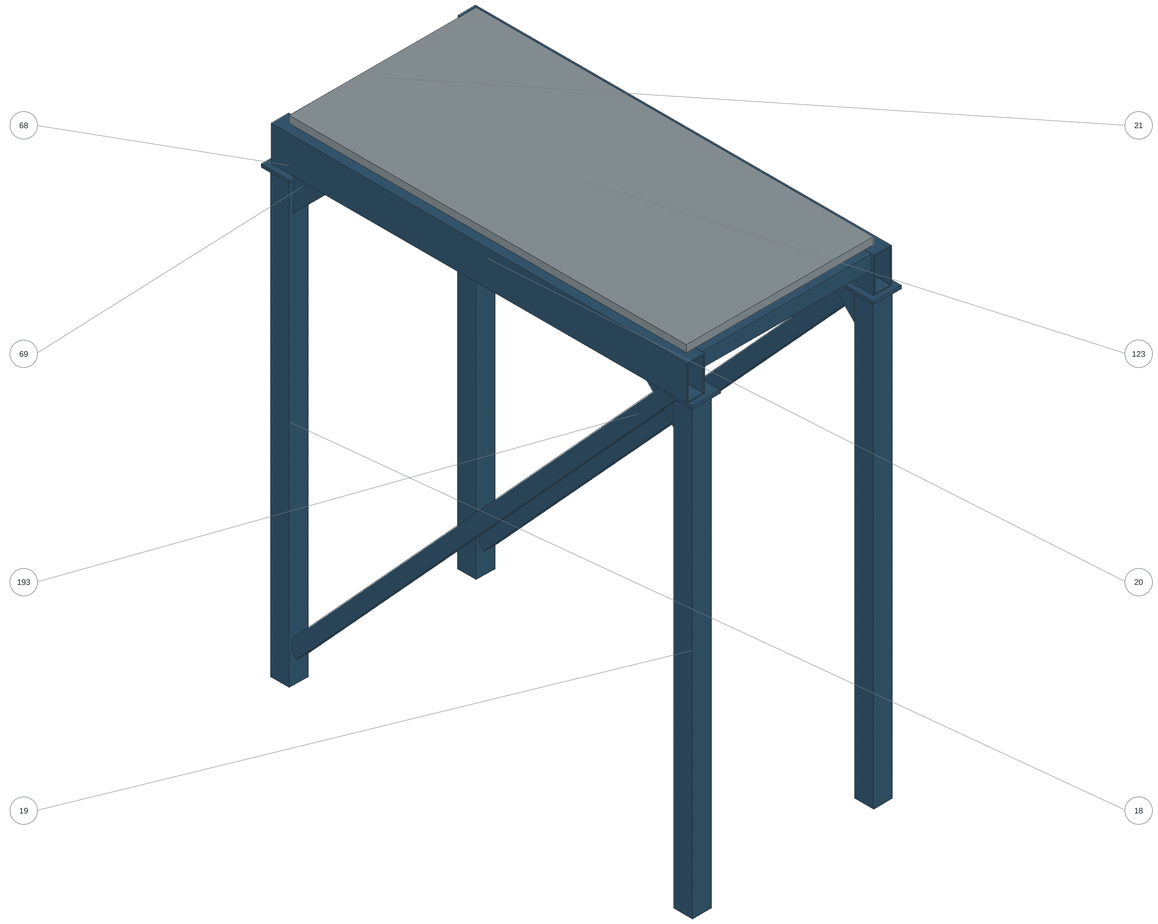


**NOTAS DE FABRICACIÓN Y MONTAJE**

1. Bastidor, cuatro postes y apoyos de rejilla forman el conjunto de plataforma.
2. No soldar la rejilla comercial a través de superficies de drenaje; fijaciones según compra.
3. Unión J01 con escalera según cuadro de juntas. Montaje en campo mediante uniones desmontables.


Cotas en mm. ISO2768-m. Soldaduras según cuadro JF. Contornos: CAD/DXF.

**P05 - REVISIÓN TÉCNICA**

| | | | | | | |
|---|---|---|---|---|---|---|
| | | | | REBABAR Y ROMPER ARISTAS | NO CAMBIAR LA ESCALA | REVISIÓN **P05** |
| SESUVECA DEL PERÚ | | | | | | |
| | NOMBRE | FIRMA | FECHA | | | TÍTULO: Plataforma de acceso ensamblada |
| DIBUJ. | PROYECTO P05 | | 16/10/26 | | | |
| VERIF. | | | | | | |
| APROB. | | | | | | |
| FABR. | | | | | | |
| CALID. | | | | MATERIAL: SEGÚN LISTA DE MATERIALES | | N.º DE DIBUJO **P05-C-12** — **A1** |
| PESO: SEGÚN CAD / BOM | | | | ESCALA: INDICADA | | ESTACIÓN DE DESCARGA BIGBAG — HOJA 12 DE 17 |


# Escalera y desembarco ensamblados

**ALZADO ESCALA 1:15**

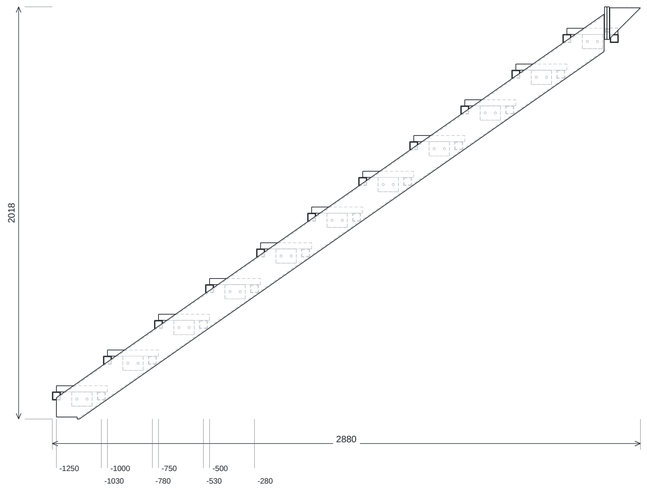


DATUM GLOBAL X (mm)


**PLANTA ESCALA 1:10**

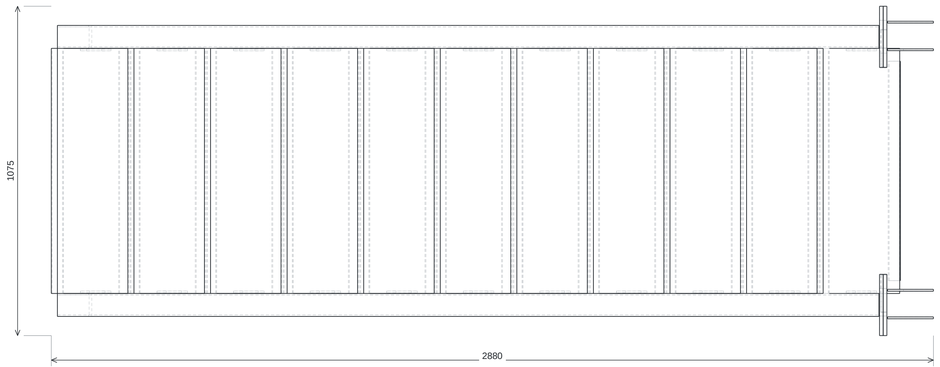


| POS. CAD | CANT. | DESCRIPCIÓN / CORTE NOMINAL mm | MATERIAL |
|---|---|---|---|
| 22,197 | 22 | SHS40x40x3 x 800 | ASTM A500 Gr.B |
| 75,198-199 | 4 | J01 CARTELA 150x150x6 | ASTM A36 |
| 76 | 22 | J02 PLACA 100x70x6 | ASTM A36 |
| 124 | 11 | PELDAÑO REJILLA COMERCIAL | SEGÚN CATÁLOGO / COMPRA |
| 195-196 | 2 | RHS150x75x5 x 3356.8 | ASTM A500 Gr.B |
| 216,218 | 2 | J01 EXTREMO 200x160x12 | ASTM A36 |
| 217,219 | 2 | J01 SOPORTE 200x160x12 | ASTM A36 |

Cortes nominales agrupados; preparaciones finales identificadas por POS., JF y DXF.

**ISOMÉTRICO A COLOR / REFERENCIA DE MONTAJE**

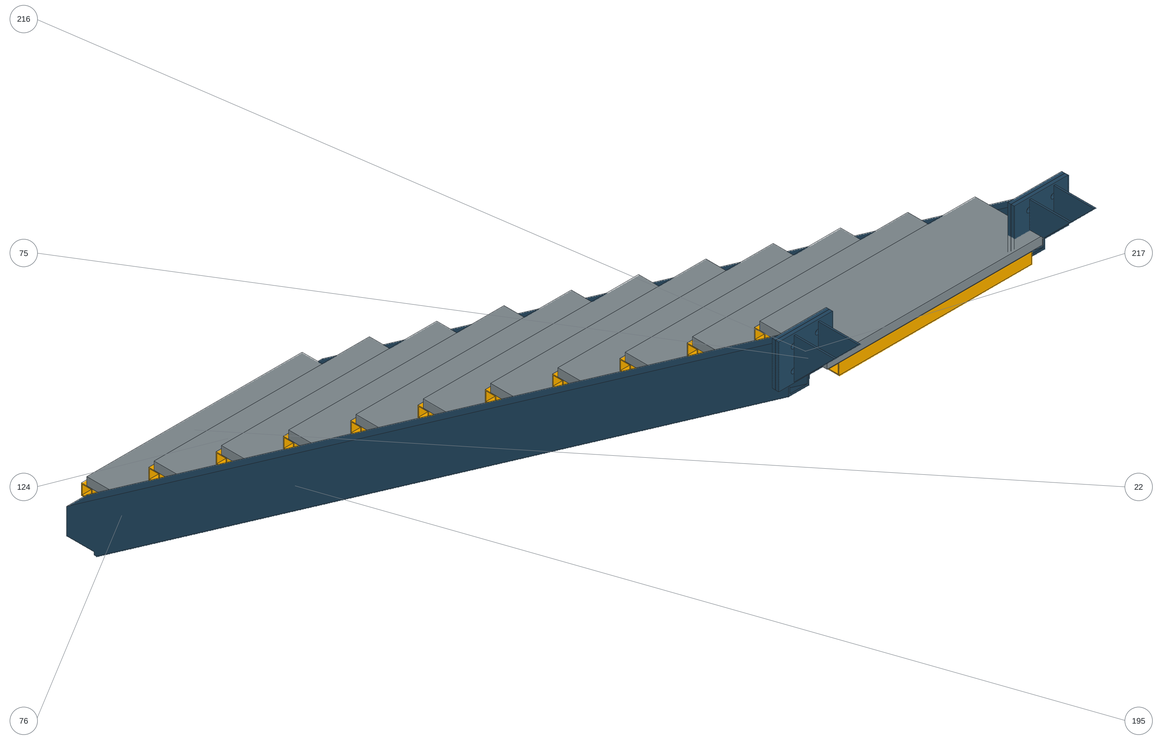


TALADROS PARAMETRIZADOS: 18 / coordenadas locales en Tabla_fabricacion_P05.csv

**NOTAS DE FABRICACIÓN Y MONTAJE**

1. Dos zancas RHS150x75x5 con recorte final de desembarco; peldaños según BOM.
2. Cortar según lista y ensamblar en útil sobre los ejes indicados.
3. Preparaciones J01 / J02 y extremos con luz 2 mm según las juntas indicadas; no soldar las holguras LUZ.

Cotas en mm. ISO2768-m. Soldaduras según cuadro JF. Contornos: CAD/DXF.

**TALADROS DE PIEZAS DEL CONJUNTO / COORDENADAS LOCALES mm / ORIGEN CAD**


P76 T1: D11; X-25 Y0 Z0; eje Z
P76 T2: D11; X25 Y0 Z0; eje Z
P216 T1: D18; X-45 Y-40 Z0; eje Z
P216 T2: D18; X-45 Y40 Z0; eje Z
P216 T3: D18; X45 Y-40 Z0; eje Z
P216 T4: D18; X45 Y40 Z0; eje Z
P217 T1: D18; X-45 Y-40 Z0; eje Z
P217 T2: D18; X-45 Y40 Z0; eje Z
P217 T3: D18; X45 Y-40 Z0; eje Z
P217 T4: D18; X45 Y40 Z0; eje Z
P218 T1: D18; X-45 Y-40 Z0; eje Z
P218 T2: D18; X-45 Y40 Z0; eje Z
P218 T3: D18; X45 Y-40 Z0; eje Z
P218 T4: D18; X45 Y40 Z0; eje Z
P219 T1: D18; X-45 Y-40 Z0; eje Z
P219 T2: D18; X-45 Y40 Z0; eje Z
P219 T3: D18; X45 Y-40 Z0; eje Z
P219 T4: D18; X45 Y40 Z0; eje Z

**P05 - REVISIÓN TÉCNICA**

| | | | | | | |
|---|---|---|---|---|---|---|
| | | | | REBABAR Y ROMPER ARISTAS | NO CAMBIAR LA ESCALA | REVISIÓN **P05** |
| SESUVECA DEL PERÚ | | | | | | |
| | NOMBRE | FIRMA | FECHA | | | TÍTULO: Escalera y desembarco ensamblados |
| DIBUJ. | PROYECTO P05 | | 16/10/26 | | | |
| VERIF. | | | | | | |
| APROB. | | | | | | |
| FABR. | | | | | | |
| CALID. | | | | MATERIAL: SEGÚN LISTA DE MATERIALES | | N.º DE DIBUJO **P05-C-13** — **A1** |
| PESO: SEGÚN CAD / BOM | | | | ESCALA: INDICADA | | ESTACIÓN DE DESCARGA BIGBAG — HOJA 13 DE 17 |


# Barandas, pasamanos y rodapiés

**ALZADO ESCALA 1:20**

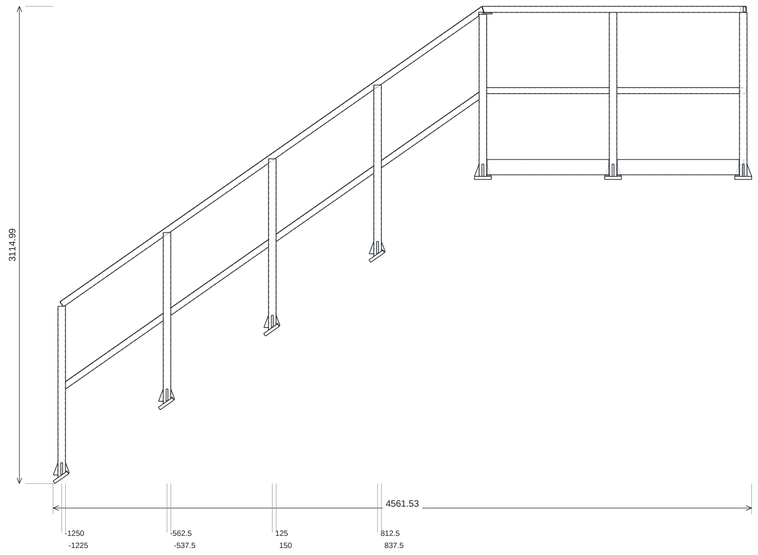


DATUM GLOBAL X (mm)


**PLANTA ESCALA 1:15**

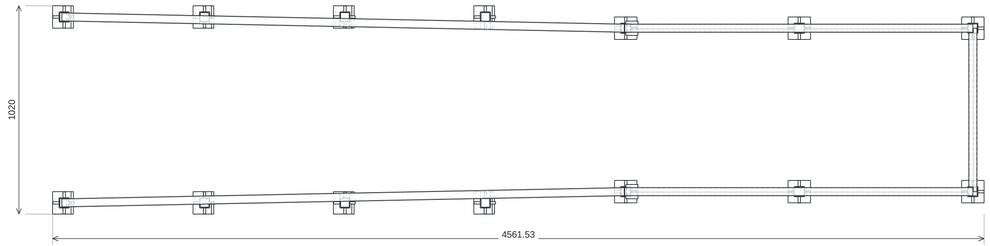


| POS. CAD | CANT. | DESCRIPCIÓN / CORTE NOMINAL mm | MATERIAL |
|---|---|---|---|
| 22,207 | 5 | SHS40x40x3 x 800 | ASTM A500 Gr.B |
| 23,185 | 6 | SHS50x50x4 x 1070 | ASTM A500 Gr.B |
| 24-31 | 8 | SHS40x40x3 x 778.27 | ASTM A500 Gr.B |
| 32 | 1 | SHS40x40x3 x 750 | ASTM A500 Gr.B |
| 35,208-210,213-215 | 8 | SHS50x50x4 x 1101.27 | ASTM A500 Gr.B |
| 77 | 14 | U05 BASE POSTE 110x110x20 | ASTM A36 |
| 78,220-253 | 56 | U05 CARTELA 30x80x12 / PREPARACIÓN POR JF | ASTM A36 |
| 183-184 | 2 | SHS40x40x3 x 1700 | ASTM A500 Gr.B |
| 186 | 2 | JF CAP TRANSICION 60x70x8 | ASTM A36 |
| 204,211 | 2 | SHS40x40x3 x 3357.25 | ASTM A500 Gr.B |
| 205,212 | 2 | RODAPIE LARGO 1700x100x5 | ASTM A36 |
| 206 | 1 | RODAPIE TESTERO 800x100x5 | ASTM A36 |

Cortes nominales agrupados; preparaciones finales identificadas por POS., JF y DXF.

**ISOMÉTRICO A COLOR / REFERENCIA DE MONTAJE**

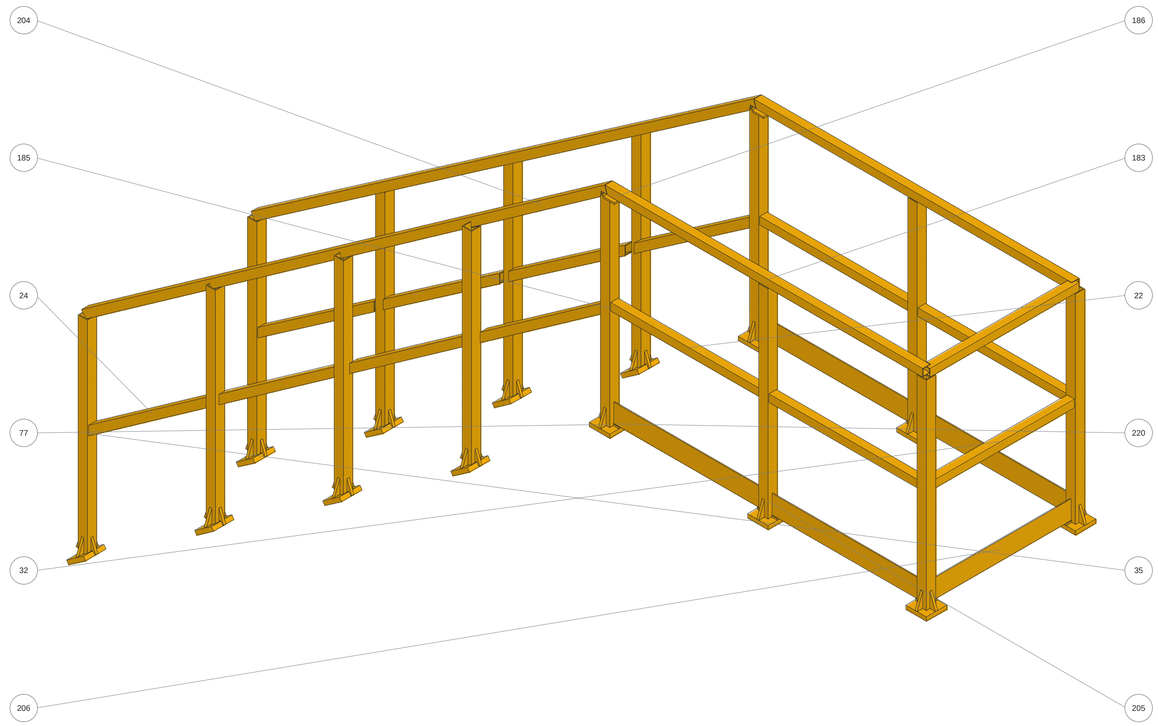


**NOTAS DE FABRICACIÓN Y MONTAJE**

1. Rodapiés t5; postes SHS50x50x4; pasamanos SHS40x40x3.
2. Conservar ingletes reales y tapas de transición 60x70x8 en extremos superiores.
3. Uniones a pared de 3 mm: PJP a2 según preparación y cuadro de juntas.
4. Soldar en taller según cuadro; eliminar bordes cortantes y asegurar continuidad del pasamanos.


Cotas en mm. ISO2768-m. Soldaduras según cuadro JF. Contornos: CAD/DXF.

**P05 - REVISIÓN TÉCNICA**

| | | | | | | |
|---|---|---|---|---|---|---|
| | | | | REBABAR Y ROMPER ARISTAS | NO CAMBIAR LA ESCALA | REVISIÓN **P05** |
| SESUVECA DEL PERÚ | | | | | | |
| | NOMBRE | FIRMA | FECHA | | | TÍTULO: Barandas, pasamanos y rodapiés |
| DIBUJ. | PROYECTO P05 | | 16/10/26 | | | |
| VERIF. | | | | | | |
| APROB. | | | | | | |
| FABR. | | | | | | |
| CALID. | | | | MATERIAL: SEGÚN LISTA DE MATERIALES | | N.º DE DIBUJO **P05-C-14** — **A1** |
| PESO: SEGÚN CAD / BOM | | | | ESCALA: INDICADA | | ESTACIÓN DE DESCARGA BIGBAG — HOJA 14 DE 17 |


# Cruceta de izaje 2 t ensamblada

**PLANTA ESCALA 1:8**

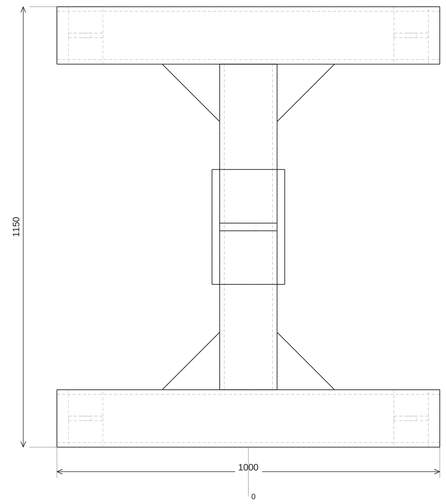


DATUM GLOBAL X (mm)


**ALZADO ESCALA 1:4**

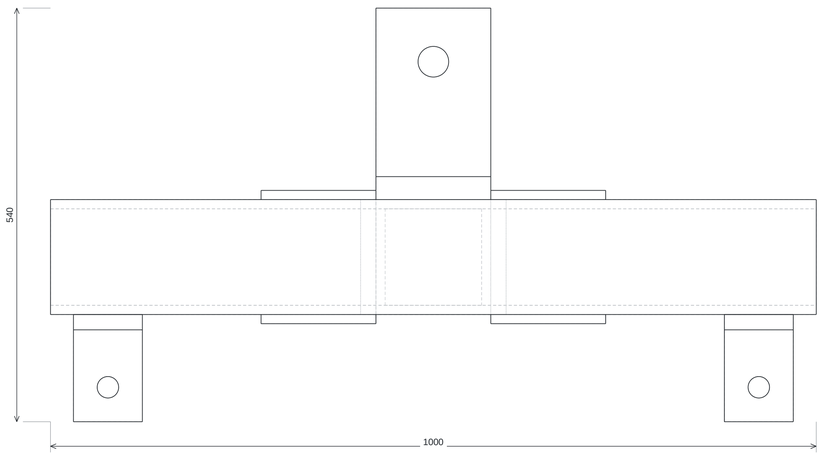


| POS. CAD | CANT. | DESCRIPCIÓN / CORTE NOMINAL mm | MATERIAL |
|---|---|---|---|
| 33 | 2 | SHS150x150x12 x 1000 | ASTM A500 Gr.B |
| 34 | 1 | SHS150x150x12 x 850 | ASTM A500 Gr.B |
| 79 | 1 | OREJA CENTRAL 150x220x20 | ASTM A36 |
| 80 | 4 | OREJA EXTREMA 90x120x12 | ASTM A36 |
| 81 | 4 | CR RESPALDO EXTREMA 90x150x20 | ASTM A36 |
| 82 | 8 | CR CARTELA TRIANGULAR 150x150x12 | ASTM A36 |
| 83 | 1 | CR CAP CENTRAL 150x300x30 | ASTM A36 |
| 84 | 2 | CR CHEEK 300x150x20 | ASTM A36 |

Cortes nominales agrupados; preparaciones finales identificadas por POS., JF y DXF.

**ISOMÉTRICO A COLOR / REFERENCIA DE MONTAJE**

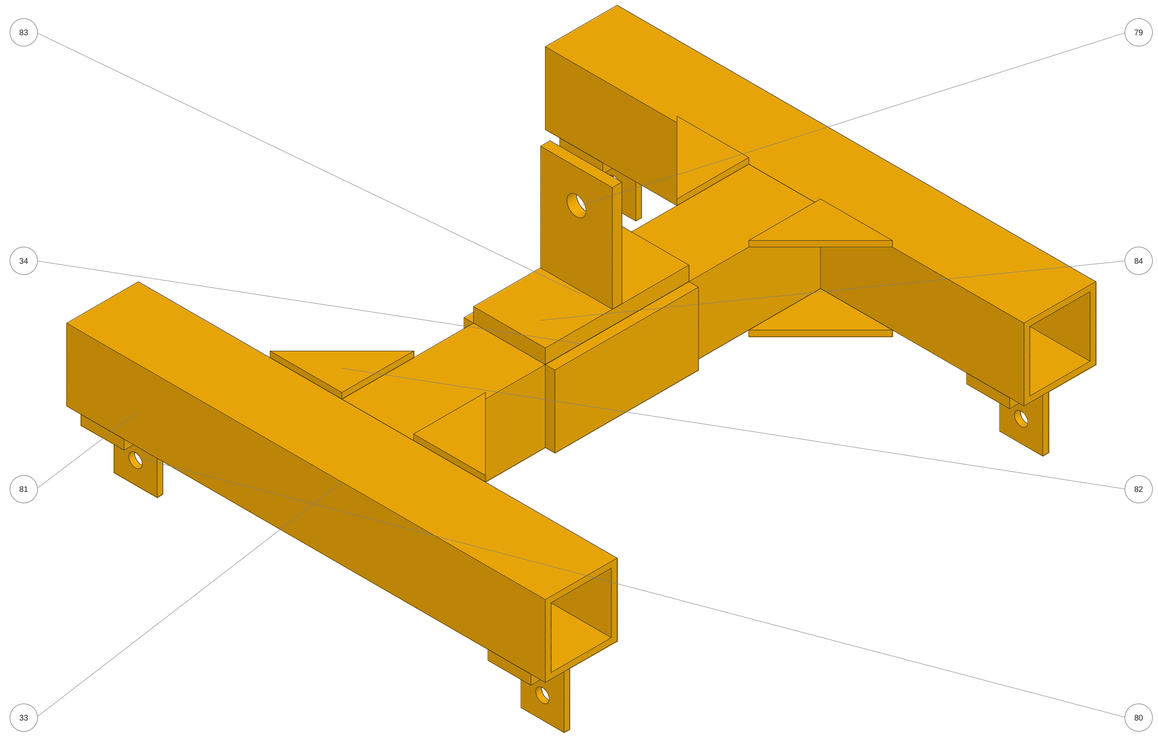


TALADROS PARAMETRIZADOS: 2 / coordenadas locales en Tabla_fabricacion_P05.csv

**NOTAS DE FABRICACIÓN Y MONTAJE**

1. Capacidad nominal 2 000 kg; 125 000 ciclos; Categoría B / Servicio Clase 2.
2. Perfiles SHS150x150x12; oreja central, orejas de asas, respaldos y cartelas según BOM.
3. Mantener reparto y geometría de toma del cálculo; identificación indeleble de capacidad y trazabilidad.
4. Ejecutar inspección y prueba de carga según protocolo antes de la puesta en servicio.

Cotas en mm. ISO2768-m. Soldaduras según cuadro JF. Contornos: CAD/DXF.

**TALADROS DE PIEZAS DEL CONJUNTO / COORDENADAS LOCALES mm / ORIGEN CAD**

P79 T1: D40; X0 Y150 Z0; eje Z

P80 T1: D28; X0 Y75 Z0; eje Z

**P05 - REVISIÓN TÉCNICA**

| | | | | | | |
|---|---|---|---|---|---|---|
| | | | | REBABAR Y ROMPER ARISTAS | NO CAMBIAR LA ESCALA | REVISIÓN **P05** |
| SESUVECA DEL PERÚ | | | | | | |
| | NOMBRE | FIRMA | FECHA | | | TÍTULO: Cruceta de izaje 2 t ensamblada |
| DIBUJ. | PROYECTO P05 | | 16/10/26 | | | |
| VERIF. | | | | | | |
| APROB. | | | | | | |
| FABR. | | | | | | |
| CALID. | | | | MATERIAL: SEGÚN LISTA DE MATERIALES | | N.º DE DIBUJO **P05-C-15** — **A1** |
| PESO: SEGÚN CAD / BOM | | | | ESCALA: INDICADA | | ESTACIÓN DE DESCARGA BIGBAG — HOJA 15 DE 17 |

## Uniones de fabricación / Cuadro 1 de 2

| ID | MIEMBRO | SOPORTE | TIPO | a mm | L mm | CENTRO GLOBAL X/Y/Z mm | EJECUCIÓN |
|---|---|---|---|---|---|---|---|
| JF-001 | BRL-A--1 | COL-0--1 | LUZ | - | - | POR MIEMBRO / SOPORTE | NO SOLDAR / LUZ 2 |
| JF-002 | BRL-A--1 | COL-3.2--1 | LUZ | - | - | POR MIEMBRO / SOPORTE | NO SOLDAR / LUZ 2 |
| JF-003 | BRL-B--1 | COL-0--1 | LUZ | - | - | POR MIEMBRO / SOPORTE | NO SOLDAR / LUZ 2 |
| JF-004 | BRL-B--1 | COL-3.2--1 | LUZ | - | - | POR MIEMBRO / SOPORTE | NO SOLDAR / LUZ 2 |
| JF-005 | KNE--1 | COL-0--1 | LUZ | - | - | POR MIEMBRO / SOPORTE | NO SOLDAR / LUZ 2 |
| JF-006 | BRL-A-1 | COL-0-1 | LUZ | - | - | POR MIEMBRO / SOPORTE | NO SOLDAR / LUZ 2 |
| JF-007 | BRL-A-1 | COL-3.2-1 | LUZ | - | - | POR MIEMBRO / SOPORTE | NO SOLDAR / LUZ 2 |
| JF-008 | BRL-B-1 | COL-0-1 | LUZ | - | - | POR MIEMBRO / SOPORTE | NO SOLDAR / LUZ 2 |
| JF-009 | BRL-B-1 | COL-3.2-1 | LUZ | - | - | POR MIEMBRO / SOPORTE | NO SOLDAR / LUZ 2 |
| JF-010 | KNE-1 | COL-0-1 | LUZ | - | - | POR MIEMBRO / SOPORTE | NO SOLDAR / LUZ 2 |
| JF-011 | PBRACE-1.1 | PPOST-1.5-1.1 | CJP | 3.72 | 173.92 | 1542 / 1300 / 181.8 | TALLER / WPS |
| JF-012 | PBRACE-1.1 | PPOST-3.2-1.125 | CJP | 3.72 | 115.05 | 3161.3 / 1306.2 / 1883.7 | TALLER / WPS |
| JF-013 | PBRACE-1.9 | PPOST-1.5-1.9 | CJP | 3.72 | 173.92 | 1542 / 2100 / 181.8 | TALLER / WPS |
| JF-014 | PBRACE-1.9 | PPOST-3.2-1.9 | CJP | 3.72 | 94.83 | 3158 / 2106.7 / 1880.9 | TALLER / WPS |
| JF-015 | STRING-1.1 | BASE_ACCESO_STRING-1.1 | CJP | 4.65 | 224 | -1194.4 / 1262.5 / 21.6 | TALLER / WPS |
| JF-016 | STRING-1.9 | BASE_ACCESO_STRING-1.9 | CJP | 4.65 | 224 | -1194.4 / 2137.5 / 21.6 | TALLER / WPS |
| JF-017 | STEP-11-1.47 | PPOST-1.5-1.1 | CJP | 2.79 | 148 | 1482 / 1342 / 1875 | TALLER / WPS |
| JF-018 | STEP-11-1.47 | PPOST-1.5-1.9 | CJP | 2.79 | 148 | 1482 / 2058 / 1875 | TALLER / WPS |
| JF-019 | KNE--1 | TRA-0 | CJP | 3.72 | 156.71 | 0 / -381 / 5498 | TALLER / WPS |
| JF-020 | KNE-1 | TRA-0 | CJP | 3.72 | 156.71 | -0 / 381 / 5498 | TALLER / WPS |
| JF-021 | BRL-A--1 | TIE--1-0.15 | LUZ | - | - | POR MIEMBRO / SOPORTE | NO SOLDAR / LUZ 2 |
| JF-022 | BRL-B--1 | TIE--1-0.15 | LUZ | - | - | POR MIEMBRO / SOPORTE | NO SOLDAR / LUZ 2 |
| JF-023 | TIE--1-0.15 | U02_COLLARX_0_1 | CJP | 3.72 | 224 | 89 / -1000 / 150 | TALLER / WPS |
| JF-024 | TIE--1-0.15 | BRT_COLLARX_-1_0.15_-1 | CJP | 3.72 | 224 | 3111 / -1000 / 150 | TALLER / WPS |
| JF-025 | BRL-A--1 | TIE--1-4.79 | LUZ | - | - | POR MIEMBRO / SOPORTE | NO SOLDAR / LUZ 2 |
| JF-026 | BRL-B--1 | TIE--1-4.79 | LUZ | - | - | POR MIEMBRO / SOPORTE | NO SOLDAR / LUZ 2 |
| JF-027 | TIE--1-4.79 | BRT_COLLARX_-1_5.338_-1 | CJP | 3.72 | 224 | 3111 / -1000 / 5430 | TALLER / WPS |
| JF-028 | BRL-A--1 | U02_COLLARX_0_1 | LUZ | - | - | POR MIEMBRO / SOPORTE | NO SOLDAR / LUZ 2 |
| JF-029 | BRL-A--1 | BRT_COLLARX_-1_5.338_-1 | LUZ | - | - | POR MIEMBRO / SOPORTE | NO SOLDAR / LUZ 2 |
| JF-030 | BRL-B--1 | BRT_COLLARX_-1_0.15_-1 | LUZ | - | - | POR MIEMBRO / SOPORTE | NO SOLDAR / LUZ 2 |
| JF-031 | KNE--1 | U02_COLLARY_8_1 | LUZ | - | - | POR MIEMBRO / SOPORTE | NO SOLDAR / LUZ 2 |
| JF-032 | BRL-A-1 | TIE-1-0.15 | LUZ | - | - | POR MIEMBRO / SOPORTE | NO SOLDAR / LUZ 2 |
| JF-033 | BRL-B-1 | TIE-1-0.15 | LUZ | - | - | POR MIEMBRO / SOPORTE | NO SOLDAR / LUZ 2 |
| JF-034 | TIE-1-0.15 | U02_COLLARX_2_1 | CJP | 3.72 | 224 | 89 / 1000 / 150 | TALLER / WPS |
| JF-035 | TIE-1-0.15 | BRT_COLLARX_1_0.15_-1 | CJP | 3.72 | 224 | 3111 / 1000 / 150 | TALLER / WPS |
| JF-036 | BRL-A-1 | TIE-1-4.79 | LUZ | - | - | POR MIEMBRO / SOPORTE | NO SOLDAR / LUZ 2 |
| JF-037 | BRL-B-1 | TIE-1-4.79 | LUZ | - | - | POR MIEMBRO / SOPORTE | NO SOLDAR / LUZ 2 |
| JF-038 | TIE-1-4.79 | BRT_COLLARX_1_5.338_-1 | CJP | 3.72 | 224 | 3111 / 1000 / 5430 | TALLER / WPS |
| JF-039 | BRL-A-1 | U02_COLLARX_2_1 | LUZ | - | - | POR MIEMBRO / SOPORTE | NO SOLDAR / LUZ 2 |
| JF-040 | BRL-A-1 | BRT_COLLARX_1_5.338_-1 | LUZ | - | - | POR MIEMBRO / SOPORTE | NO SOLDAR / LUZ 2 |
| JF-041 | BRL-B-1 | BRT_COLLARX_1_0.15_-1 | LUZ | - | - | POR MIEMBRO / SOPORTE | NO SOLDAR / LUZ 2 |
| JF-042 | KNE-1 | U02_COLLARY_9_-1 | LUZ | - | - | POR MIEMBRO / SOPORTE | NO SOLDAR / LUZ 2 |
| JF-043 | PBRACE-1.1 | PLONG-1.1 | CJP | 3.72 | 97.93 | 3123.4 / 1300.8 / 1918 | TALLER / WPS |

a = garganta efectiva de cálculo; L = longitud efectiva. CJP atraviesa la pared menor; PJP según preparación indicada.

LUZ = holgura de 2 mm libre de soldadura. Transferencia de carga por conexión primaria según memoria.

**CJP / V60 / RAÍZ 2**




**PJP a2 / 2 x 45**




**FILETE / a SEGÚN CÁLCULO**




### NOTAS DE FABRICACIÓN Y MONTAJE

1. Soldadura conforme a AWS D1.1; verificación AISC360 según memoria.
2. Material de aporte compatible con metal base. CJP/PJP: procedimiento WPS calificado y aceptación según especificación.
3. Juntas primarias U01 / U02 / BRT / TC y anclajes: ver detalles y memoria. Interfaces JF según este cuadro.
4. Montaje en campo mediante uniones desmontables; conservar piezas KITO sin mecanizado ni soldaduras.

Cotas en mm. ISO2768-m. Soldaduras según cuadro JF. Contornos: CAD/DXF.

**P05 - REVISIÓN TÉCNICA**

| | | | | | | | |
|---|---|---|---|---|---|---|---|
| | | | | REBABAR Y ROMPER ARISTAS | NO CAMBIAR LA ESCALA | | REVISIÓN P05 |
| SESUVECA DEL PERÚ | | | | | | | |
| | NOMBRE | FIRMA | FECHA | | | TÍTULO: Uniones de fabricación / Cuadro 1 de 2 | |
| DIBUJ. | PROYECTO P05 | | 16/10/26 | | | | |
| VERIF. | | | | | | | |
| APROB. | | | | | | | |
| FABR. | | | | | | | |
| CALID. | | | | MATERIAL: SEGÚN LISTA DE MATERIALES | | N.º DE DIBUJO P05-C-16 | A1 |
| PESO: SEGÚN CAD / BOM | | | | ESCALA: INDICADA | | ESTACIÓN DE DESCARGA BIGBAG | HOJA 16 DE 17 |

## Uniones de fabricación / Cuadro 2 de 2

| ID | MIEMBRO | SOPORTE | TIPO | a mm | L mm | CENTRO GLOBAL X/Y/Z mm | EJECUCIÓN |
|---|---|---|---|---|---|---|---|
| JF-044 | PBRACE-1.9 | PLONG-1.9 | CJP | 3.72 | 77.43 | 3122.2 / 2104.1 / 1918 | TALLER / WPS |
| JF-045 | PBRACE-1.1 | P02_CAP_PPOST-3.2-1.125 | CJP | 3.72 | 79.58 | 3149.3 / 1293.9 / 1907.8 | TALLER / WPS |
| JF-046 | PBRACE-1.1 | P02_CARTELA_PPOST-3.2-1.125_-0.025 | CJP | 3.72 | 325.48 | 3111.4 / 1294 / 1867.6 | TALLER / WPS |
| JF-047 | PBRACE-1.9 | P02_CAP_PPOST-3.2-1.9 | CJP | 3.72 | 31.14 | 3144.4 / 2128 / 1908.3 | TALLER / WPS |
| JF-048 | PBRACE-1.9 | P02_CARTELA_PPOST-3.2-1.9_-0.025 | CJP | 3.72 | 227.65 | 3104.5 / 2073.5 / 1859.9 | TALLER / WPS |
| JF-049 | PBRACE-1.9 | P02_CARTELA_PPOST-3.2-1.9_0.025 | CJP | 3.72 | 325.48 | 3111.4 / 2119 / 1867.6 | TALLER / WPS |
| JF-050 | RPOST-1.5-1.1 | JF_CAP_RPOST-1.5-1.1 | CJP | 3.72 | 96 | 1516.5 / 1300 / 3148 | TALLER / WPS |
| JF-051 | RODAPIE_1.1 | RPOST-1.5-1.1 | CJP | 3.72 | 100 | 1527 / 1297.5 / 2150 | TALLER / WPS |
| JF-052 | RODAPIE_1.1 | RPOST-2.35-1.1 | CJP | 3.72 | 200 | 2350 / 1297.5 / 2150 | TALLER / WPS |
| JF-053 | RODAPIE_1.1 | RPOST-3.2-1.1 | CJP | 3.72 | 100 | 3173 / 1297.5 / 2150 | TALLER / WPS |
| JF-054 | RODAPIE_TESTERO | RPOST-3.2-1.1 | CJP | 3.72 | 100 | 3202.5 / 1327 / 2150 | TALLER / WPS |
| JF-055 | SRAIL-1.1-1.1 | RLONG-1.1-3.2 | CJP | 2.79 | 126.71 | 1497.8 / 1300.1 / 3183.7 | TALLER / WPS |
| JF-056 | REND-3.2 | RLONG-1.1-3.2 | CJP | 2.79 | 120.28 | 3192.2 / 1318 / 3180 | TALLER / WPS |
| JF-057 | SRAILPOST--0.5625-1.045 | SRAIL-1.1-1.1 | CJP | 2.79 | 120.57 | -576.2 / 1255.2 / 1703.6 | TALLER / WPS |
| JF-058 | SRAILPOST-0.125-1.045 | SRAIL-1.1-1.1 | CJP | 2.79 | 104.13 | 112.9 / 1261.1 / 2186.5 | TALLER / WPS |
| JF-059 | SRAILPOST-0.8125-1.045 | SRAIL-1.1-1.1 | CJP | 2.79 | 87.7 | 802.6 / 1266.5 / 2670 | TALLER / WPS |
| JF-060 | RPOST-1.5-1.9 | JF_CAP_RPOST-1.5-1.9 | CJP | 3.72 | 96 | 1516.5 / 2100 / 3148 | TALLER / WPS |
| JF-061 | RODAPIE_1.9 | RPOST-1.5-1.9 | CJP | 3.72 | 100 | 1527 / 2097.5 / 2150 | TALLER / WPS |
| JF-062 | RODAPIE_1.9 | RPOST-2.35-1.9 | CJP | 3.72 | 200 | 2350 / 2097.5 / 2150 | TALLER / WPS |
| JF-063 | RODAPIE_1.9 | RPOST-3.2-1.9 | CJP | 3.72 | 100 | 3173 / 2097.5 / 2150 | TALLER / WPS |
| JF-064 | RODAPIE_TESTERO | RPOST-3.2-1.9 | CJP | 3.72 | 100 | 3202.5 / 2073 / 2150 | TALLER / WPS |
| JF-065 | SRAIL-1.9-1.1 | RLONG-1.9-3.2 | CJP | 2.79 | 126.71 | 1497.8 / 2099.9 / 3183.7 | TALLER / WPS |
| JF-066 | REND-3.2 | RLONG-1.9-3.2 | CJP | 2.79 | 120.28 | 3192.2 / 2082 / 3180 | TALLER / WPS |
| JF-067 | SRAILPOST--0.5625-1.955 | SRAIL-1.9-1.1 | CJP | 2.79 | 120.57 | -576.2 / 2144.8 / 1703.6 | TALLER / WPS |
| JF-068 | SRAILPOST-0.125-1.955 | SRAIL-1.9-1.1 | CJP | 2.79 | 104.13 | 112.9 / 2138.9 / 2186.5 | TALLER / WPS |
| JF-069 | SRAILPOST-0.8125-1.955 | SRAIL-1.9-1.1 | CJP | 2.79 | 87.7 | 802.6 / 2133.5 / 2670 | TALLER / WPS |
| JF-070 | J01_EXTREMO_1.0625 | P02_CAP_PPOST-1.5-1.1 | LUZ | - | - | POR MIEMBRO / SOPORTE | NO SOLDAR / LUZ 2 |
| JF-071 | J01_SOPORTE_1.0625 | P02_CAP_PPOST-1.5-1.1 | CJP | 11.16 | 280.43 | 1452 / 1300.1 / 1913.7 | TALLER / WPS |
| JF-072 | J01_CARTELA_1.0625_1 | P02_CAP_PPOST-1.5-1.1 | LUZ | - | - | POR MIEMBRO / SOPORTE | NO SOLDAR / LUZ 2 |
| JF-073 | J01_EXTREMO_1.9375000000000002 | P02_CAP_PPOST-1.5-1.9 | LUZ | - | - | POR MIEMBRO / SOPORTE | NO SOLDAR / LUZ 2 |
| JF-074 | J01_SOPORTE_1.9375000000000002 | P02_CAP_PPOST-1.5-1.9 | CJP | 11.16 | 280.43 | 1452 / 2099.9 / 1913.7 | TALLER / WPS |
| JF-075 | J01_CARTELA_1.9375000000000002_-1 | P02_CAP_PPOST-1.5-1.9 | LUZ | - | - | POR MIEMBRO / SOPORTE | NO SOLDAR / LUZ 2 |
| JF-076 | J01_CARTELA_1.0625_-1 | J01_EXTREMO_1.0625 | LUZ | - | - | POR MIEMBRO / SOPORTE | NO SOLDAR / LUZ 2 |
| JF-077 | J01_CARTELA_1.0625_1 | J01_EXTREMO_1.0625 | LUZ | - | - | POR MIEMBRO / SOPORTE | NO SOLDAR / LUZ 2 |
| JF-078 | J01_CARTELA_1.0625_-1 | J01_SOPORTE_1.0625 | CJP | 5.58 | 150 | 1460 / 1220.5 / 1950 | TALLER / WPS |
| JF-079 | J01_CARTELA_1.0625_1 | J01_SOPORTE_1.0625 | CJP | 5.58 | 98 | 1460 / 1310.5 / 1976 | TALLER / WPS |
| JF-080 | J01_CARTELA_1.9375000000000002_-1 | J01_EXTREMO_1.9375000000000002 | LUZ | - | - | POR MIEMBRO / SOPORTE | NO SOLDAR / LUZ 2 |
| JF-081 | J01_CARTELA_1.9375000000000002_1 | J01_EXTREMO_1.9375000000000002 | LUZ | - | - | POR MIEMBRO / SOPORTE | NO SOLDAR / LUZ 2 |
| JF-082 | J01_CARTELA_1.9375000000000002_-1 | J01_SOPORTE_1.9375000000000002 | CJP | 5.58 | 98 | 1460 / 2095.5 / 1976 | TALLER / WPS |
| JF-083 | J01_CARTELA_1.9375000000000002_1 | J01_SOPORTE_1.9375000000000002 | CJP | 5.58 | 150 | 1460 / 2185.5 / 1950 | TALLER / WPS |
| JF_CAP_RPOST-1.5-1.1-RAIL | JF_CAP_RPOST-1.5-1.1 | RLONG-1.1-3.2 | PJP | 2 | 90 | 1532.5 / 1300 / 3158 | TALLER / WPS |
| JF_CAP_RPOST-1.5-1.9-RAIL | JF_CAP_RPOST-1.5-1.9 | RLONG-1.9-3.2 | PJP | 2 | 90 | 1532.5 / 2100 / 3158 | TALLER / WPS |

a = garganta efectiva de cálculo; L = longitud efectiva. CJP atraviesa la pared menor; PJP según preparación indicada.

LUZ = holgura de 2 mm libre de soldadura. Transferencia de carga por conexión primaria según memoria.

**CJP / V60 / RAÍZ 2**




**PJP a2 / 2 x 45**




**FILETE / a SEGÚN CÁLCULO**




**POSICIÓN DE LOS 37 MIEMBROS JF / ORIGEN X,Y,Z mm / VECTOR LOCAL LONGITUDINAL**

BRL-A--1 | 87,-955,150 | 0.5,0,0.87
BRL-B--1 | 87,-1045,5430 | 0.5,0,-0.87
KNE--1 | 0,-913,5006.29 | 0,0.75,0.66
BRL-A-1 | 87,1045,150 | 0.5,0,0.87
BRL-B-1 | 87,955,5430 | 0.5,0,-0.87
KNE-1 | 0,913,5006.29 | 0,-0.75,0.66
PBRACE-1.1 | 1540,1300,150 | 0.68,0,0.74
PBRACE-1.9 | 1540,2100,150 | 0.68,0,0.74
STRING-1.1 | -1250,1262.5,25 | 0.82,0,0.57
STRING-1.9 | -1250,2137.5,25 | 0.82,0,0.57
STEP-11-1.47 | 1482,1300,1875 | 0,1,0
TIE--1-0.15 | 75,-1000,150 | 1,0,0
TIE--1-4.79 | 75,-1000,5430 | 1,0,0
TIE-1-0.15 | 75,1000,150 | 1,0,0
TIE-1-4.79 | 75,1000,5430 | 1,0,0
RPOST-1.5-1.1 | 1500,1300,2090 | 0,0,1
RODAPIE_1.1 | 2350,1300,2150 | 0,-1,0
RODAPIE_TESTERO | 3200,1700,2150 | 1,0,0
SRAIL-1.1-1.1 | -1250,1245,1255 | 0.82,0.02,0.57
REND-3.2 | 3200,1300,3180 | 0,1,0
SRAILPOST--0.5625-1.045 | -562.5,1245,622.21 | 0,0,1
SRAILPOST-0.125-1.045 | 125,1245,1103.46 | 0,0,1
SRAILPOST-0.8125-1.045 | 812.5,1245,1584.71 | 0,0,1
RPOST-1.5-1.9 | 1500,2100,2090 | 0,0,1
RODAPIE_1.9 | 2350,2100,2150 | 0,-1,0
SRAIL-1.9-1.1 | -1250,2155,1255 | 0.82,-0.02,0.57
SRAILPOST--0.5625-1.955 | -562.5,2155,622.21 | 0,0,1
SRAILPOST-0.125-1.955 | 125,2155,1103.46 | 0,0,1
SRAILPOST-0.8125-1.955 | 812.5,2155,1584.71 | 0,0,1
J01_EXTREMO_1.0625 | 1434,1262.5,1950 | 1,0,0
J01_SOPORTE_1.0625 | 1446,1262.5,1950 | 1,0,0
J01_CARTELA_1.0625_1 | 1460,1307.5,2025 | 0,1,0
J01_EXTREMO_1.9375000000000002 | 1434,2137.5,1950 | 1,0,0
J01_SOPORTE_1.9375000000000002 | 1446,2137.5,1950 | 1,0,0
J01_CARTELA_1.9375000000000002_-1 | 1460,2092.5,2025 | 0,1,0
J01_CARTELA_1.0625_-1 | 1460,1217.5,2025 | 0,1,0
J01_CARTELA_1.9375000000000002_1 | 1460,2182.5,2025 | 0,1,0

El vector local define la orientación; perfiles / cortes nominales por POS. y conjunto. Preparaciones exactas: CAD / DXF.

**P05 - REVISIÓN TÉCNICA**

| | | | | | | | |
|---|---|---|---|---|---|---|---|
| | | | | REBABAR Y ROMPER ARISTAS | NO CAMBIAR LA ESCALA | | REVISIÓN P05 |
| SESUVECA DEL PERÚ | | | | | | | |
| | NOMBRE | FIRMA | FECHA | | | TÍTULO: Uniones de fabricación / Cuadro 2 de 2 | |
| DIBUJ. | PROYECTO P05 | | 16/10/26 | | | | |
| VERIF. | | | | | | | |
| APROB. | | | | | | | |
| FABR. | | | | | | | |
| CALID. | | | | MATERIAL: SEGÚN LISTA DE MATERIALES | | N.º DE DIBUJO P05-C-17 | A1 |
| PESO: SEGÚN CAD / BOM | | | | ESCALA: INDICADA | | ESTACIÓN DE DESCARGA BIGBAG | HOJA 17 DE 17 |