

Estación Bigbag / Conjunto general

ALZADO LONGITUDINAL ESCALA 1:40

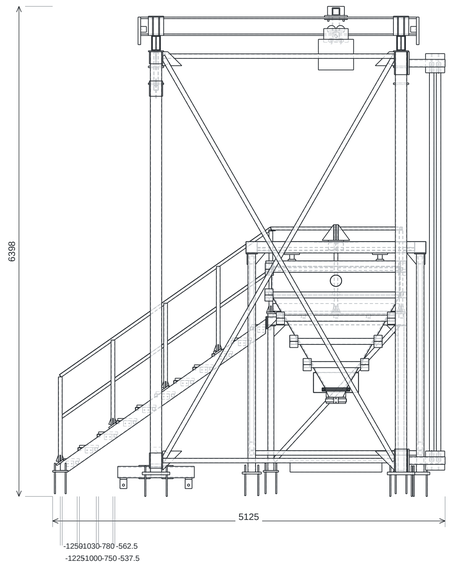

DATUM GLOBAL X (mm)


ALZADO TRANSVERSAL ESCALA 1:50

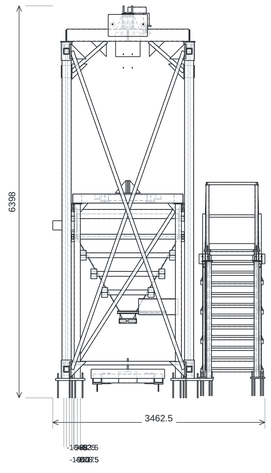

DATUM GLOBAL Y (mm)

CONJUNTO	PLANO
Cimentación y placas base	EB-02
Pórticos transversales ensamblados	EB-03
Arriostramiento longitudinal y uniones	EB-04
Viga carril y topes de fin de carrera	EB-05
Bastidor de tolva ensamblado	EB-06
Tolva, anillos y revestimiento	EB-07
Cortador y parrilla de apoyo de bolsa	EB-08
Compuerta de descarga ensamblada	EB-09
Guarda, ensacado y captación	EB-10
Carro, suspensión y traba de posición	EB-11
Plataforma de acceso ensamblada	EB-12
Escalera y desembarco ensamblados	EB-13
Barandas, pasamanos y rodapiés	EB-14
Cruceta de izaje 2 t ensamblada	EB-15

ISOMÉTRICO A COLOR / REFERENCIA DE MONTAJE

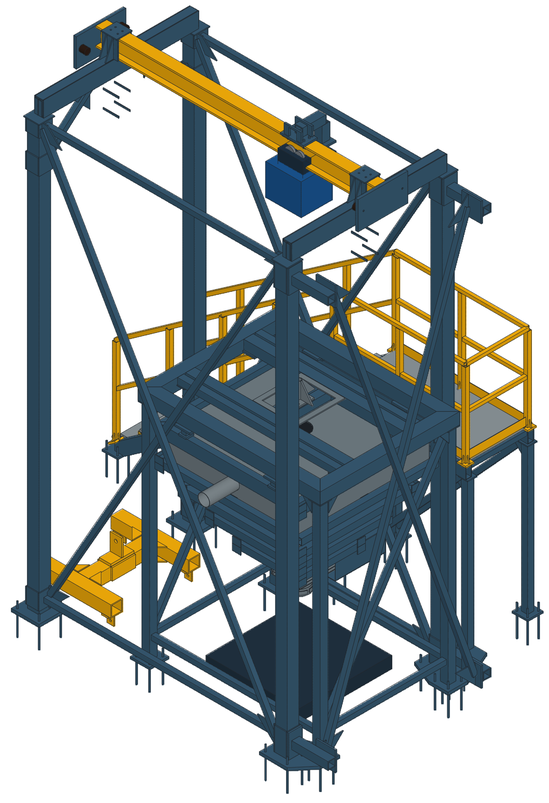

NOTAS DE FABRICACIÓN Y MONTAJE


1. Cruceta y tecle nominales 2 t; proceso de bolsas de 1 t.
2. Traslado con fondo de bolsa a Z = 3 520; guarda superior Z = 3 430; punta de cortador Z = 3 230.
3. Enclavamientos, prueba de carga y recepción según memoria.
4. POS.: número de pieza en el BOM de 253 piezas únicas.

Cotas en mm. ISO2768-m. Soldaduras según cuadro JF. Contornos: CAD/DXF.


				REBABAR Y ROMPER ARISTAS	NO CAMBIAR LA ESCALA	REVISIÓN
SESUVECA DEL PERÚ						
	NOMBRE	FIRMA	FECHA			TÍTULO: Estación Bigbag / Conjunto general
DIBUJ.	Javier Acevedo		16/10/26			
VERIF.						
APROB.						
FABR.						
CALID.				MATERIAL: SEGÚN LISTA DE MATERIALES		N.º DE DIBUJO EB-01 / A1
PESO: SEGÚN CAD / BOM				ESCALA: INDICADA		ESTACIÓN DE DESCARGA BIGBAG / HOJA 1 DE 17

Cimentación y placas base

PLANTA ESCALA 1:20

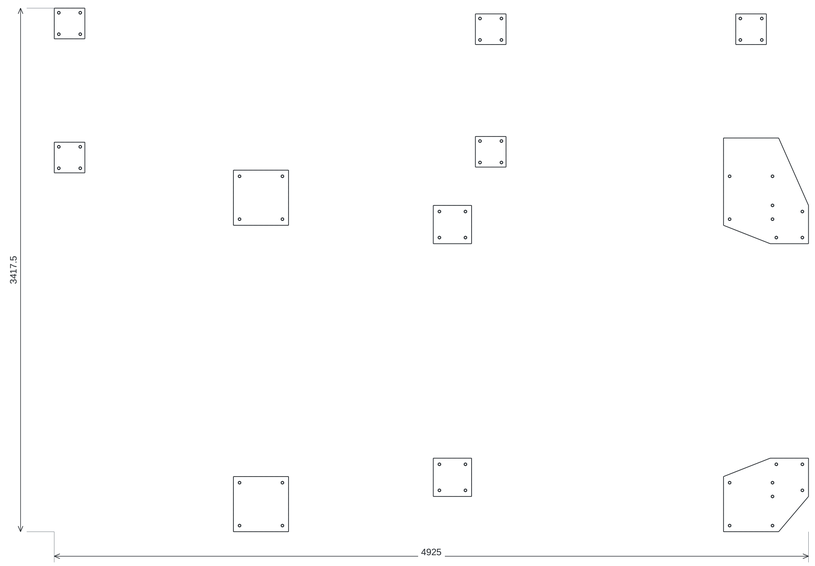


ALZADO ESCALA 1:15

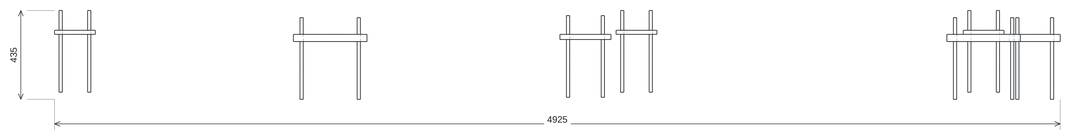

POS.	CANT.	DESCRIPCIÓN / CORTE NOMINAL mm	MATERIAL
42	2	BASE PORTICO 360x360x35	ASTM A36
43	2	BASE TOLVA 250x250x25	ASTM A36
44	5	P02 BASE ACCESO 200x200x12	ASTM A36
130	1	BASE COMBINADA PORTICO TOLVA SUR t35	A36
131	1	BASE COMBINADA PORTICO TOLVA NORTE t35	A36
132	52	ANCLA HASU 8p8 M16 L400 HEF275	HAS-U8.8
133	52	ANCLA ARANDELA D30 D18 t3	SEGÚN CATÁLOGO / COMPRA
134	52	ANCLA TUERCA M16 AF24 H13	Acero clase8

ISOMÉTRICO A COLOR / REFERENCIA DE MONTAJE

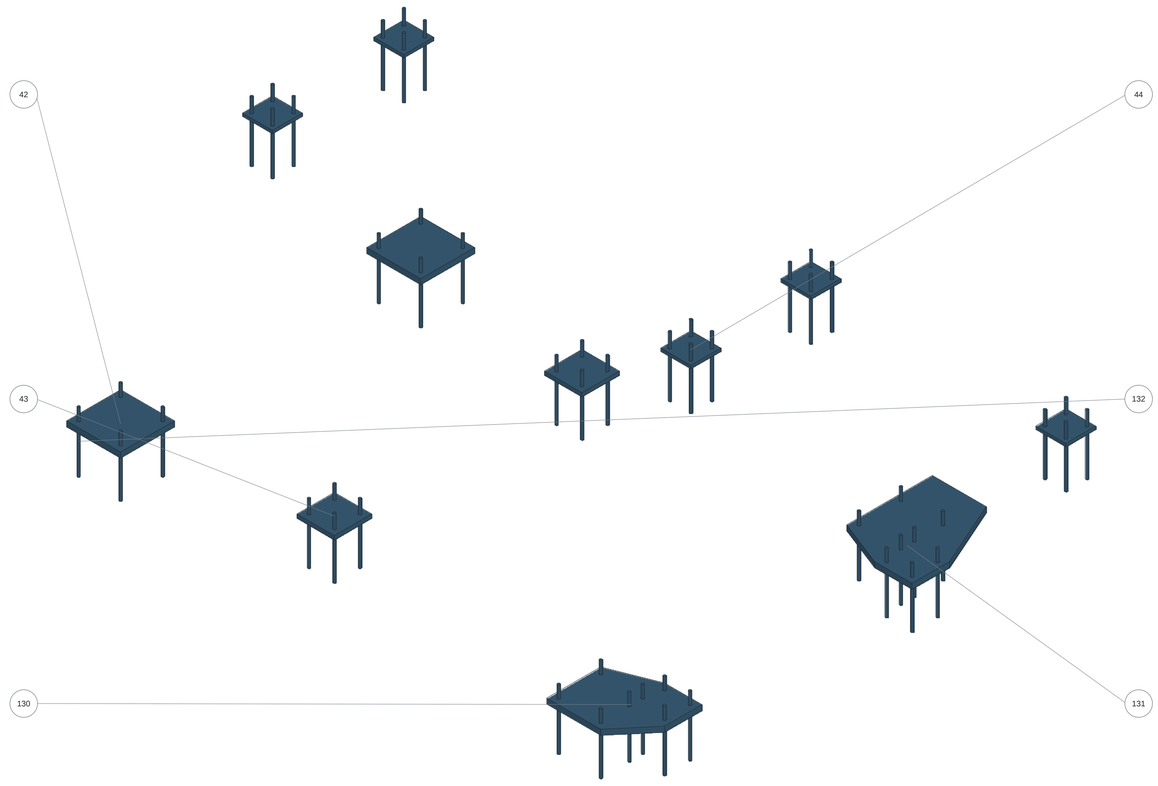

NOTAS DE FABRICACIÓN Y MONTAJE

1. Losa: espesor 650 mm; f'c = 20,59 MPa (datos del cliente).
2. HAS-U 8.8 M16: longitud total 400; empotramiento efectivo 275; resina HIT-RE 500 V4.
3. Replanteo en coordenadas globales; cota Z0 = cara superior del concreto. Borde mínimo de proyecto: 500 mm.
4. Respetar patrón y diámetro de agujeros del CAD; instalación, limpieza y curado según fabricante.

Cotas en mm. ISO2768-m. Soldaduras según cuadro JF. Contornos: CAD/DXF.


TALADROS DE PIEZAS DEL CONJUNTO / COORDENADAS LOCALES mm / ORIGEN LOCAL

P42 T1: D18; X-140 Y-140 Z0; eje Z
P42 T2: D18; X-140 Y140 Z0; eje Z
P42 T3: D18; X140 Y-140 Z0; eje Z
P42 T4: D18; X140 Y140 Z0; eje Z
P43 T1: D18; X-85 Y-85 Z0; eje Z
P43 T2: D18; X-85 Y85 Z0; eje Z
P43 T3: D18; X85 Y-85 Z0; eje Z
P43 T4: D18; X85 Y85 Z0; eje Z
P44 T1: D18; X-70 Y-70 Z0; eje Z
P44 T2: D18; X-70 Y70 Z0; eje Z
P44 T3: D18; X70 Y-70 Z0; eje Z
P44 T4: D18; X70 Y70 Z0; eje Z
P130 T1: D18; X-140 Y-140 Z0; eje Z
P130 T2: D18; X-140 Y140 Z0; eje Z
P130 T3: D18; X140 Y-140 Z0; eje Z
P130 T4: D18; X140 Y140 Z0; eje Z
P130 T5: D18; X140 Y50 Z0; eje Z
P130 T6: D18; X165 Y260 Z0; eje Z
P130 T7: D18; X335 Y90 Z0; eje Z
P130 T8: D18; X335 Y260 Z0; eje Z
P131 T1: D18; X-140 Y-140 Z0; eje Z
P131 T2: D18; X-140 Y140 Z0; eje Z
P131 T3: D18; X140 Y-140 Z0; eje Z
P131 T4: D18; X140 Y140 Z0; eje Z
P131 T5: D18; X165 Y-260 Z0; eje Z
P131 T6: D18; X140 Y-50 Z0; eje Z
P131 T7: D18; X335 Y-260 Z0; eje Z
P131 T8: D18; X335 Y-90 Z0; eje Z

				REBABAR Y ROMPER ARISTAS	NO CAMBIAR LA ESCALA	REVISIÓN
SESUVECA DEL PERÚ						
	NOMBRE	FIRMA	FECHA			TÍTULO: Cimentación y placas base
DIBUJ.	Javier Acevedo		16/10/26			
VERIF.						
APROB.						
FABR.						
CALID.				MATERIAL: SEGÚN LISTA DE MATERIALES		N.º DE DIBUJO EB-02 / A1
PESO: SEGÚN CAD / BOM				ESCALA: INDICADA		ESTACIÓN DE DESCARGA BIGBAG / HOJA 2 DE 17

Pórticos transversales ensamblados

PERFIL ESCALA 1:40

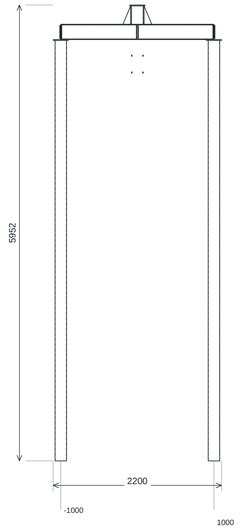


DATUM GLOBAL Y (mm)

PLANTA ESCALA 1:15



POS.	CANT.	DESCRIPCIÓN / CORTE NOMINAL mm	MATERIAL
1	4	SHS150x150x6 x 5488	ASTM A500 Gr.B
2	2	IPE200 x 2000	ASTM A36
45	2	U01 CAP 200x200x12	ASTM A36
46	4	U01 LATERAL 200x240x12	ASTM A36
47	8	U01 CALCE 200x20x6	ASTM A36
48	24	U01 RIGIDIZADOR 44x175x6	ASTM A36
49	8	U01 CARTELA 100x240x12	ASTM A36
50	4	P01 CAP COLUMNA 200x200x12	ASTM A36

ISOMÉTRICO A COLOR / REFERENCIA DE MONTAJE

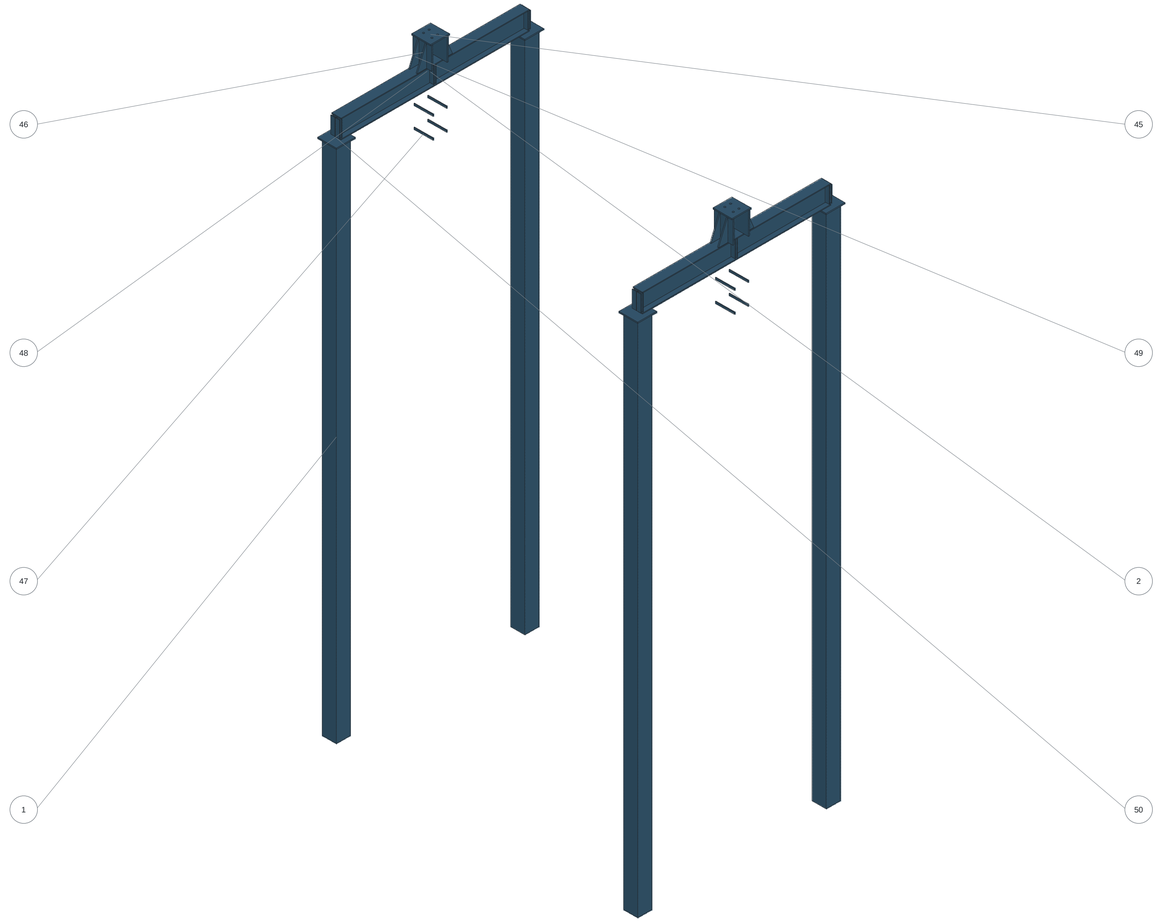

NOTAS DE FABRICACIÓN Y MONTAJE

1. Dos pórticos, ejes X = 0 y 3 200; separación Y = 2 000 entre columnas.
2. Columnas SHS150x150x6; travesaños IPE200. Chapas de unión U01 / P01 según BOM.
3. Cotas referidas a la posición nominal montada. Soldadura de taller; montaje desmontable según detalle.

Cotas en mm. ISO2768-m. Soldaduras según cuadro JF. Contornos: CAD/DXF.


TALADROS DE PIEZAS DEL CONJUNTO / COORDENADAS LOCALES mm / ORIGEN LOCAL

P45 T1: D18; X-45 Y-30 Z0; eje Z
P45 T2: D18; X-45 Y30 Z0; eje Z
P45 T3: D18; X45 Y-30 Z0; eje Z
P45 T4: D18; X45 Y30 Z0; eje Z

				REBABAR Y ROMPER ARISTAS	NO CAMBIAR LA ESCALA	REVISIÓN
SESUVECA DEL PERÚ						
	NOMBRE	FIRMA	FECHA			TÍTULO: Pórticos transversales ensamblados
DIBUJ.	Javier Acevedo		16/10/26			
VERIF.						
APROB.						
FABR.						
CALID.				MATERIAL: SEGÚN LISTA DE MATERIALES		N.º DE DIBUJO EB-03 / A1
PESO: SEGÚN CAD / BOM				ESCALA: INDICADA		ESTACIÓN DE DESCARGA BIGBAG / HOJA 3 DE 17


Arriostramiento longitudinal y uniones

ALZADO ESCALA 1:40

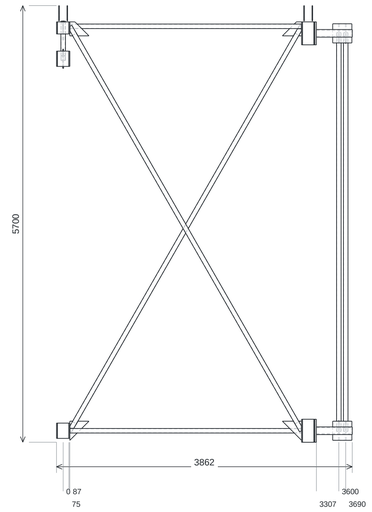

DATUM GLOBAL X (mm)

PLANTA ESCALA 1:15

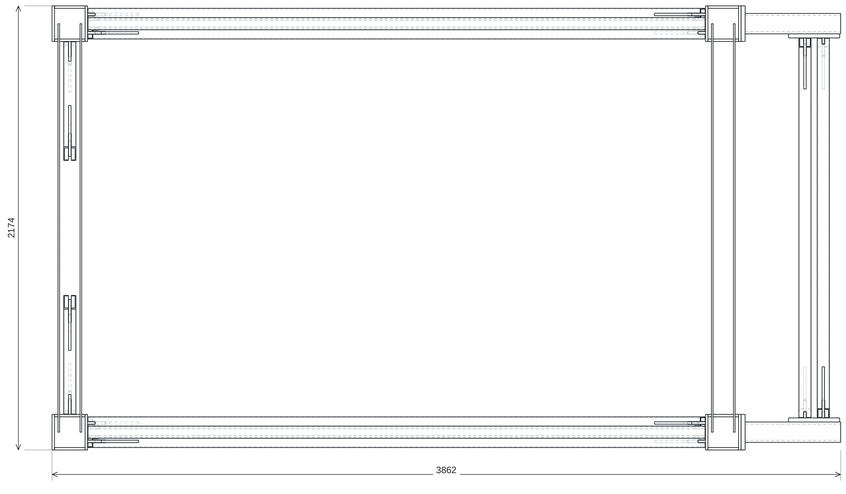

POS.	CANT.	DESCRIPCIÓN / CORTE NOMINAL mm	MATERIAL
51	8	U02 COLLAR 150x200x12	ASTM A36
52	8	U02 COLLAR 174x200x12	ASTM A36
53	4	U02 COLLAR 150x158x12	ASTM A36
54	4	U02 COLLAR 174x158x12	ASTM A36
55	1	U02 CARTELA BRL-A--1 0	ASTM A36
56	1	U02 CARTELA BRL-A--1 1	ASTM A36
57	1	U02 CARTELA BRL-B--1 0	ASTM A36
58	1	U02 CARTELA BRL-B--1 1	ASTM A36
59	1	U02 CARTELA KNE--1 0	ASTM A36
60	1	U02 CARTELA KNE--1 1	ASTM A36
61	1	U02 CARTELA BRL-A-1 0	ASTM A36
62	1	U02 CARTELA BRL-A-1 1	ASTM A36
63	1	U02 CARTELA BRL-B-1 0	ASTM A36
64	1	U02 CARTELA BRL-B-1 1	ASTM A36
65	1	U02 CARTELA KNE-1 0	ASTM A36
66	1	U02 CARTELA KNE-1 1	ASTM A36
135	4	PORTICO CIERRE IPE200 2000x200x8	A36
158	1	BRT A FINAL	A36
159	1	BRT LENGUETA BRT-A 0 250x250x12	ASTM A36
160	1	BRT LENGUETA BRT-A 1 250x250x12	ASTM A36
161	1	BRT B FINAL	A36
162	1	BRT LENGUETA BRT-B 0 250x250x12	ASTM A36
163	1	BRT LENGUETA BRT-B 1 250x250x12	ASTM A36
164	8	BRT COLLAR 150x300x12	ASTM A36
165	8	BRT COLLAR 174x300x12	ASTM A36
166	4	BRT RESPALDO 174x300x20	ASTM A36
167	4	BRT OUTRIGGER SHS100x100x10 S355 L468	S355 certificado Fy>=355MPa
168	4	BRT CONTRACARA 250x250x20	ASTM A36
187-188,190-191	4	SHS60x60x4 x 6085.65	ASTM A500 Gr.B
189,192	2	SHS60x60x4 x 748.81	ASTM A500 Gr.B
200-203	4	SHS60x60x4 x 3050	ASTM A500 Gr.B

ISOMÉTRICO A COLOR / REFERENCIA DE MONTAJE

NOTAS DE FABRICACIÓN Y MONTAJE


1. Dos planos longitudinales Y = -1 000 y +1 000. Luz entre pórticos: 3 200.
2. Conservar ranuras y recortes de extremos; no soldar las holguras JF identificadas como LUZ.
3. Collares, lengüetas y diagonales: preparaciones según CAD; mantener holguras libres de soldadura.
4. Geometría BRT y posición de collares según CAD final; reacción longitudinal de diseño: 12 kN.

Cotas en mm. ISO2768-m. Soldaduras según cuadro JF. Contornos: CAD/DXF.

				REBABAR Y ROMPER ARISTAS	NO CAMBIAR LA ESCALA	REVISIÓN
SESUVECA DEL PERÚ						
	NOMBRE	FIRMA	FECHA			TÍTULO: Arriostramiento longitudinal y uniones
DIBUJ.	Javier Acevedo		16/10/26			
VERIF.						
APROB.						
FABR.						
CALID.				MATERIAL: SEGÚN LISTA DE MATERIALES		N.º DE DIBUJO EB-04 / A1
PESO: SEGÚN CAD / BOM				ESCALA: INDICADA		ESTACIÓN DE DESCARGA BIGBAG / HOJA 4 DE 17


Viga carril y topes de fin de carrera

ALZADO ESCALA 1:15

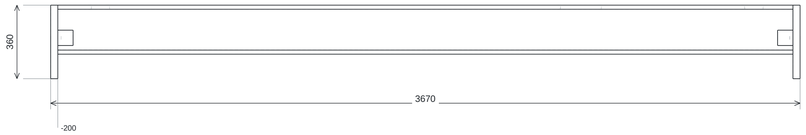


DATUM GLOBAL X (mm)

PLANTA ESCALA 1:15

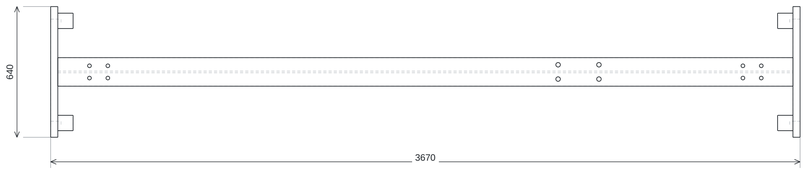

POS.	CANT.	DESCRIPCIÓN / CORTE NOMINAL mm	MATERIAL
3	1	I_A240x140x8x20 x 3600	ASTM A36
180	2	TOPE PLACA REACCION 640x360x35	A36
181	4	TOPE ACE TS75 39 D75 L75	Elastomero copoliester Shore40D
182	4	TOPE ACE FIJACION M16 L51 ENVELOPE	Tornillo especial suministrado con ACE

ISOMÉTRICO A COLOR / REFERENCIA DE MONTAJE

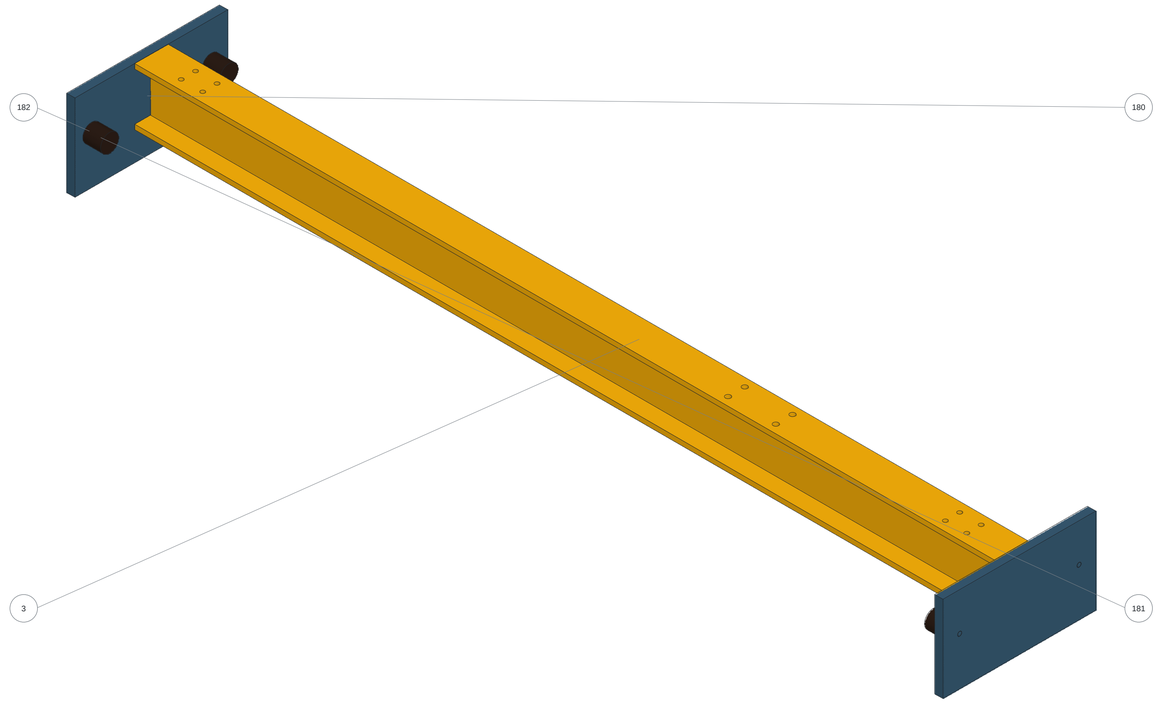

NOTAS DE FABRICACIÓN Y MONTAJE

1. Viga fabricada I240x140x8x20; longitud 3 600; ala de rodadura 140 x 20.
2. Dos topes ACE TS75-39 por extremo; placas de reacción 640 x 360 x 35.
3. Carrera nominal del amortiguador 39; energía de proyecto 419,45 J; reacción estructural adoptada 12 kN.
4. Montaje KITO y topes: ver especificación y memoria.

Cotas en mm. ISO2768-m. Soldaduras según cuadro JF. Contornos: CAD/DXF.


TALADROS DE PIEZAS DEL CONJUNTO / COORDENADAS LOCALES mm / ORIGEN LOCAL

P3 B1: D18; X-30 Y95 Z155; eje Y
P3 B2: D18; X30 Y95 Z155; eje Y
P3 B3: D18; X-30 Y95 Z245; eje Y
P3 B4: D18; X30 Y95 Z245; eje Y
P3 B5: D18; X-30 Y95 Z3355; eje Y
P3 B6: D18; X30 Y95 Z3355; eje Y
P3 B7: D18; X-30 Y95 Z3445; eje Y
P3 B8: D18; X30 Y95 Z3445; eje Y
P3 B9: D22; X-35 Y99 Z2450; eje Y
P3 B10: D22; X35 Y99 Z2450; eje Y
P3 B11: D22; X-35 Y99 Z2650; eje Y
P3 B12: D22; X35 Y99 Z2650; eje Y
P180 T1: D18; X-250 Y20 Z0; eje Z
P180 T2: D18; X250 Y20 Z0; eje Z

				REBABAR Y ROMPER ARISTAS	NO CAMBIAR LA ESCALA		REVISIÓN
SESUVECA DEL PERÚ							
	NOMBRE	FIRMA	FECHA			TÍTULO: Viga carril y topes de fin de carrera	
DIBUJ.	Javier Acevedo		16/10/26				
VERIF.							
APROB.							
FABR.							
CALID.				MATERIAL: SEGÚN LISTA DE MATERIALES		N.º DE DIBUJO EB-05	A1
PESO: SEGÚN CAD / BOM				ESCALA: INDICADA		ESTACIÓN DE DESCARGA BIGBAG	HOJA 5 DE 17


Bastidor de tolva ensamblado

ALZADO ESCALA 1:20

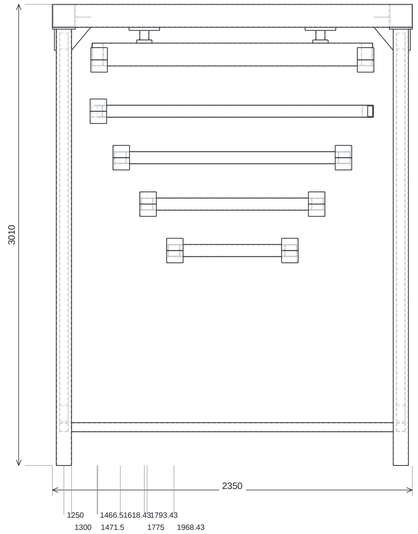


DATUM GLOBAL X (mm)

PLANTA ESCALA 1:15

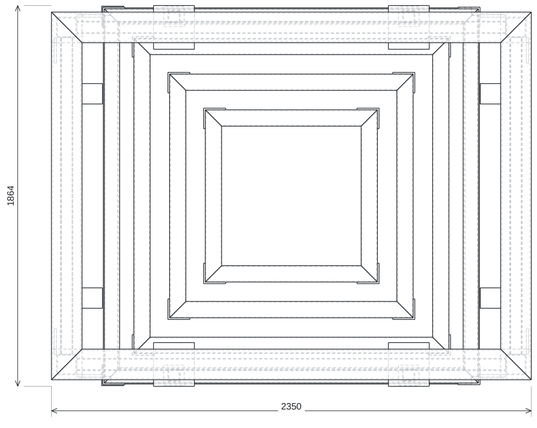

POS.	CANT.	DESCRIPCIÓN / CORTE NOMINAL mm	MATERIAL
4	4	SHS100x100x5 x 2848	ASTM A500 Gr.B
5	2	SHS150x150x6 x 2200	ASTM A500 Gr.B
6	2	SHS150x150x6 x 1650	ASTM A500 Gr.B
7	2	SHS60x60x4 x 2100	ASTM A500 Gr.B
8	2	SHS60x60x4 x 1550	ASTM A500 Gr.B
9-10	4	SHS80x80x4 x 763.14	ASTM A500 Gr.B
11-12	4	SHS80x80x4 x 1113.14	ASTM A500 Gr.B
13	4	SHS80x80x4 x 1463.14	ASTM A500 Gr.B
14-15	4	RHS150x75x5 x 1757	ASTM A500 Gr.B
16	2	SHS60x60x4 x 2882.26	ASTM A500 Gr.B
36	4	SHS60x60x4 x 62.41	ASTM A500 Gr.B
67	4	U04 CAP PATA 150x150x12	ASTM A36
70	8	U04 CARTELA 125x150x12	ASTM A36
71	36	U04 ANGULO ARMADO 2x100x80x8	ASTM A36
72	4	T01 ASIENTO 100x100x6	ASTM A36
73	4	T02 ASIENTO INFERIOR 100x100x20	ASTM A36
74	4	T02 ASIENTO SUPERIOR 200x214x20	ASTM A36
175	1	HR 2p3124 1 FINAL	A36
176	1	HR 2p3124 2 FINAL	A36
177	1	HR 2p3124 3 FINAL	A36
178	1	HR 2p3124 4 FINAL	A36

ISOMÉTRICO A COLOR / REFERENCIA DE MONTAJE

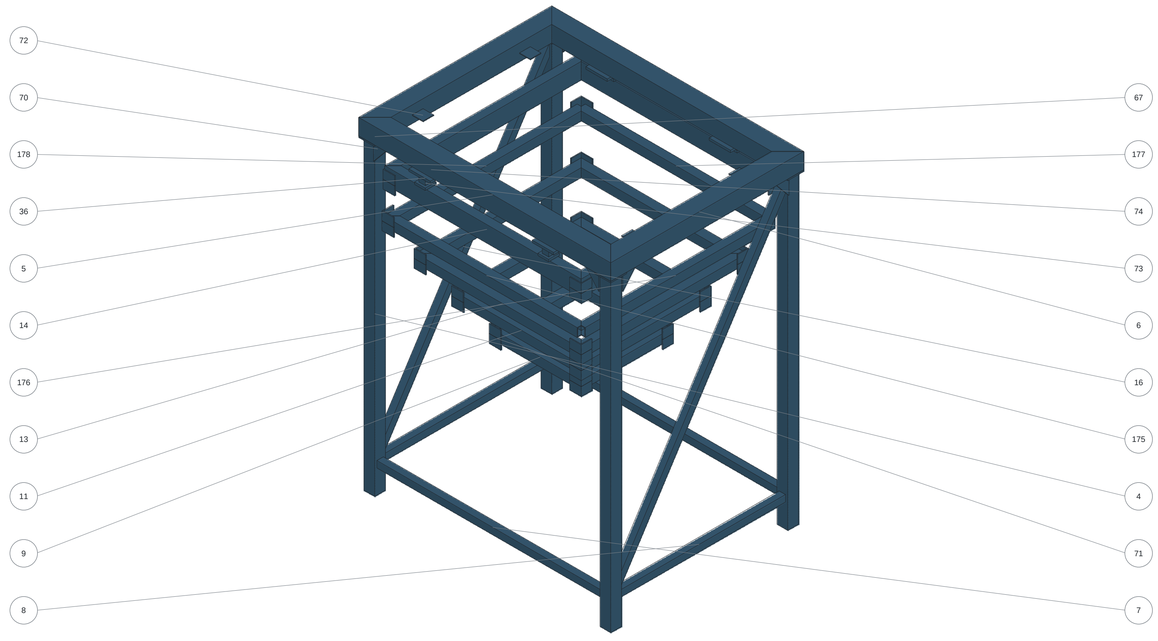

NOTAS DE FABRICACIÓN Y MONTAJE


1. Cuatro patas SHS100x100x5; marco superior SHS150x150x6. Longitudes y cantidades en BOM.
2. Ejes de patas X = 1 250 / 3 450; Y = -825 / +825.
3. Mantener posiciones de anillos y apoyos; cortes de encuentro incluidos en CAD / DXF.
4. Soldadura de taller según conjunto y espesores; mantener libres las superficies de apoyo y revestimiento.

Cotas en mm. ISO2768-m. Soldaduras según cuadro JF. Contornos: CAD/DXF.


				REBABAR Y ROMPER ARISTAS	NO CAMBIAR LA ESCALA	REVISIÓN
SESUVECA DEL PERÚ						
	NOMBRE	FIRMA	FECHA			TÍTULO: Bastidor de tolva ensamblado
DIBUJ.	Javier Acevedo		16/10/26			
VERIF.						
APROB.						
FABR.						
CALID.				MATERIAL: SEGÚN LISTA DE MATERIALES		N.º DE DIBUJO EB-06 / A1
PESO: SEGÚN CAD / BOM				ESCALA: INDICADA		ESTACIÓN DE DESCARGA BIGBAG / HOJA 6 DE 17

Tolva, anillos y revestimiento

ALZADO ESCALA 1:10

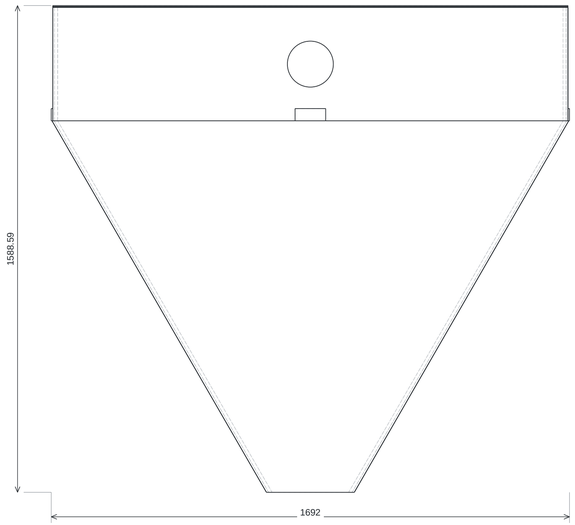


PLANTA ESCALA 1:15

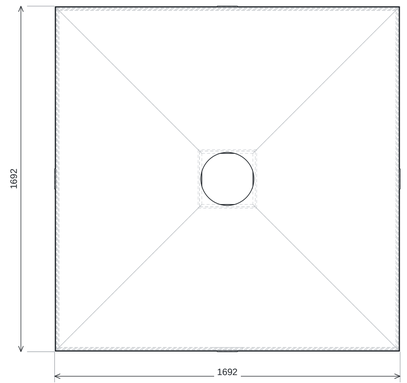

POS.	CANT.	DESCRIPCIÓN / CORTE NOMINAL mm	MATERIAL
37	4	TOL PANEL CONO 6mm	ASTM A36
38	3	TOL PANEL CUERPO 6mm	ASTM A36
39	1	TOL PANEL CUERPO DN150 6mm	ASTM A36
40	1	TOL TAPA POLVO 1662x1662x3	ASTM A36
41	1	TOL	EPDM
85	4	LINER CONO UHMW10	UHMWPE disipativo
86	3	LINER CUERPO UHMW10	UHMWPE disipativo
87	1	LINER CUERPO UHMW10 DN150	UHMWPE disipativo
179	4	HR4 PAD 100x40x5	ASTM A36

ISOMÉTRICO A COLOR / REFERENCIA DE MONTAJE

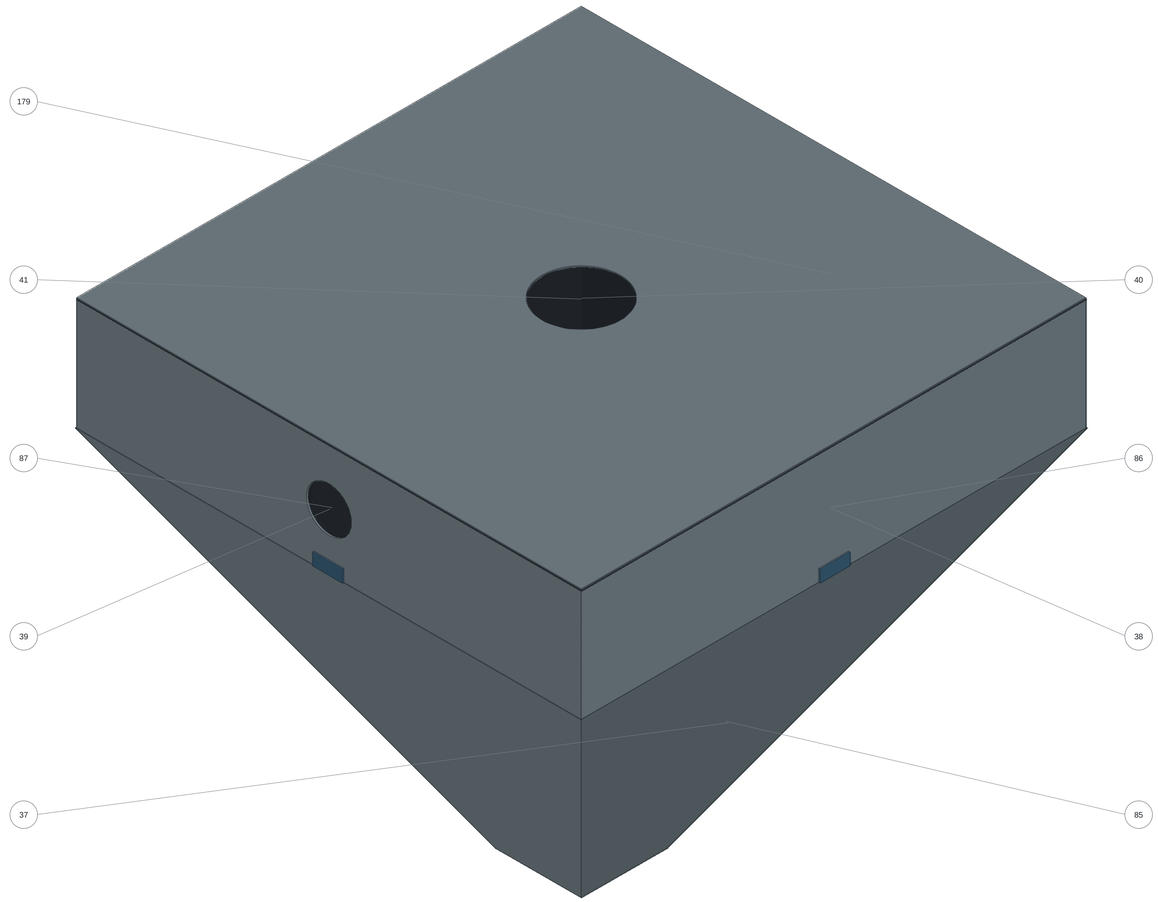

NOTAS DE FABRICACIÓN Y MONTAJE

1. Boca interior libre 1 650; salida libre 250; paredes a 60 grados.
2. Tronco piramidal: altura interior 1 212,44. Cuerpo interior: altura 370,15.
3. Revestimiento UHMWPE disipativo de 10 mm; dimensiones interiores libres después del revestimiento.
4. Puerto DN150 con paso continuo a través de casco y liner; no obstruir el conducto.
5. Volumen útil y ensayo de descarga por gravedad según memoria.

Cotas en mm. ISO2768-m. Soldaduras según cuadro JF. Contornos: CAD/DXF.

TALADROS DE PIEZAS DEL CONJUNTO / COORDENADAS LOCALES mm / ORIGEN LOCAL


P39 B1: D150; X0 Y185.08 Z9; eje Z
P40 T1: D260; X0 Y0 Z0; eje Z

P87 B1: D150; X0 Y185.08 Z-1; eje Z

				REBABAR Y ROMPER ARISTAS	NO CAMBIAR LA ESCALA	REVISIÓN
SESUVECA DEL PERÚ						
	NOMBRE	FIRMA	FECHA			TÍTULO: Tolva, anillos y revestimiento
DIBUJ.	Javier Acevedo		16/10/26			
VERIF.						
APROB.						
FABR.						
CALID.				MATERIAL: SEGÚN LISTA DE MATERIALES		N.º DE DIBUJO EB-07 / A1
PESO: SEGÚN CAD / BOM				ESCALA: INDICADA		ESTACIÓN DE DESCARGA BIGBAG / HOJA 7 DE 17


Cortador y parrilla de apoyo de bolsa

ALZADO ESCALA 1:8

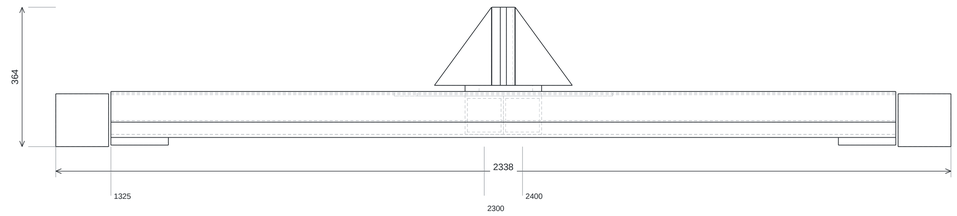


DATUM GLOBAL X (mm)

PLANTA ESCALA 1:8

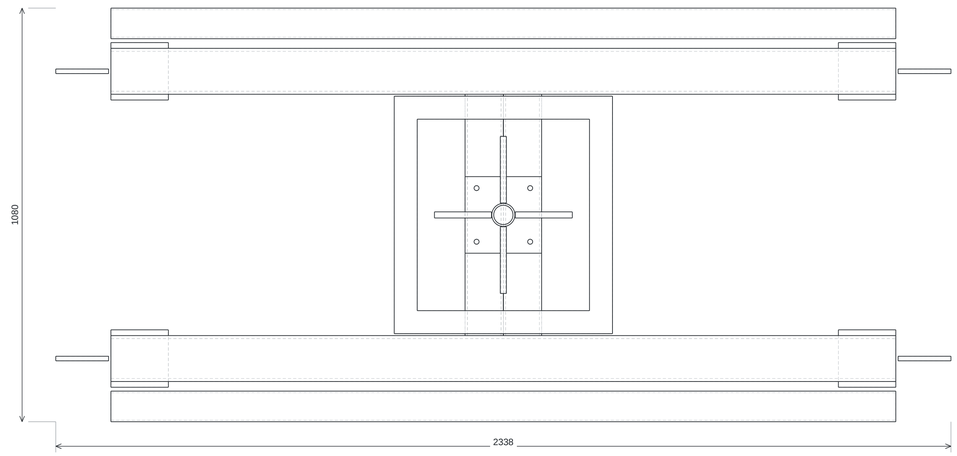

POS.	CANT.	DESCRIPCIÓN / CORTE NOMINAL mm	MATERIAL
17	2	SHS80x80x4 x 2050	ASTM A500 Gr.B
88	1	CORTE ALETA 1 304 t16	AISI304
89	1	CORTE ALETA 2 304 t16	AISI304
90	1	CORTE ALETA 3 304 t16	AISI304
91	1	CORTE ALETA 4 304 t16	AISI304
92	1	CORTE MASTIL 60p3x5	AISI304
93	1	CORTE MARCO 570x620x12	AISI 304
94	1	CORTE BASE 200x200x16	AISI 304
169	1	GRID 0p25 FINAL	A36
170	4	GRID ASIENTO 150x150x20	ASTM A36
171	4	GRID DIAFRAGMA HUP 138x138x12	ASTM A36
172	1	GRID 0p25 FINAL	A36
173	2	CORTE TRAVESANO100x100x6 L630	A36
174	1	CORTE ESPACIADOR CENTRAL 200x200x12	AISI 304

ISOMÉTRICO A COLOR / REFERENCIA DE MONTAJE

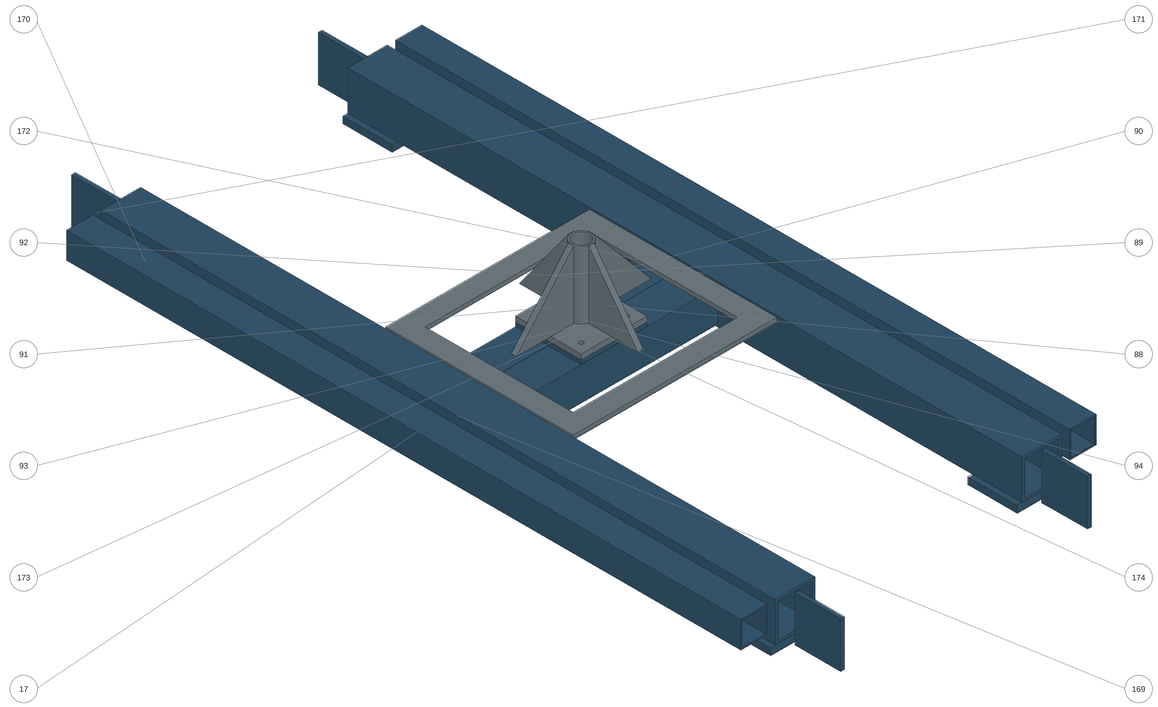

NOTAS DE FABRICACIÓN Y MONTAJE

1. Cuchilla piramidal fija de cuatro filos AISI304; chapas de filo t16 según BOM.
2. Mástil, marco y travesaños forman un conjunto. Mantener posición centrada sobre salida.
3. Altura de punta Z = 3 230. El bigbag se desplaza con fondo a Z = 3 520.
4. Sustituir filos con equipo aislado, bolsa retirada y protección de acceso instalada.

Cotas en mm. ISO2768-m. Soldaduras según cuadro JF. Contornos: CAD/DXF.


TALADROS DE PIEZAS DEL CONJUNTO / COORDENADAS LOCALES mm / ORIGEN LOCAL

P94 T1: D13; X-70 Y-70 Z0; eje Z
P94 T2: D13; X70 Y-70 Z0; eje Z
P94 T3: D13; X-70 Y70 Z0; eje Z
P94 T4: D13; X70 Y70 Z0; eje Z


				REBABAR Y ROMPER ARISTAS	NO CAMBIAR LA ESCALA		REVISIÓN
SESUVECA DEL PERÚ							
	NOMBRE	FIRMA	FECHA			TÍTULO: Cortador y parrilla de apoyo de bolsa	
DIBUJ.	Javier Acevedo		16/10/26				
VERIF.							
APROB.							
FABR.							
CALID.				MATERIAL: SEGÚN LISTA DE MATERIALES		N.º DE DIBUJO EB-08	A1
PESO: SEGÚN CAD / BOM				ESCALA: INDICADA		ESTACIÓN DE DESCARGA BIGBAG	HOJA 8 DE 17

Compuerta de descarga ensamblada

PLANTA ESCALA 1:5

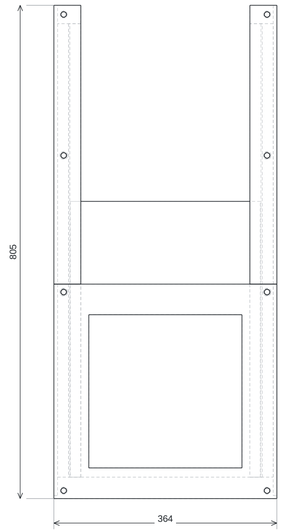


ALZADO ESCALA 1:2

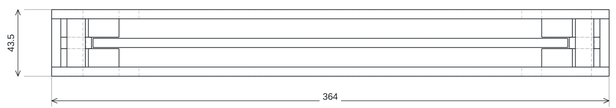

POS.	CANT.	DESCRIPCIÓN / CORTE NOMINAL mm	MATERIAL
100	1	MG02 FLANGE 364x350x6	ASTM A36
101	1	MG03 FLANGE 364x350x6	ASTM A36
102	1	MG01 HOJA 310x450x6	ASTM A36
103	1	MG04 SUP 1	ASTM A36
104	1	MG04 SUP 2	ASTM A36
105	1	MG05 INF 1	ASTM A36
106	1	MG05 INF 2	ASTM A36
107	1	MG06 ESP 1	ASTM A36
108	1	MG06 ESP 2	ASTM A36
109	1	MG07 UHMW SUP 1	UHMW-PE
110	1	MG07 UHMW SUP 2	UHMW-PE
111	1	MG08 UHMW INF 1	UHMW-PE
112	1	MG08 UHMW INF 2	UHMW-PE
113	1	MG09 UHMW LADO 1	UHMW-PE
114	1	MG09 UHMW LADO 2	UHMW-PE
115	8	MG10 CASQUILLO 12x9 L31p5	ACERO

ISOMÉTRICO A COLOR / REFERENCIA DE MONTAJE

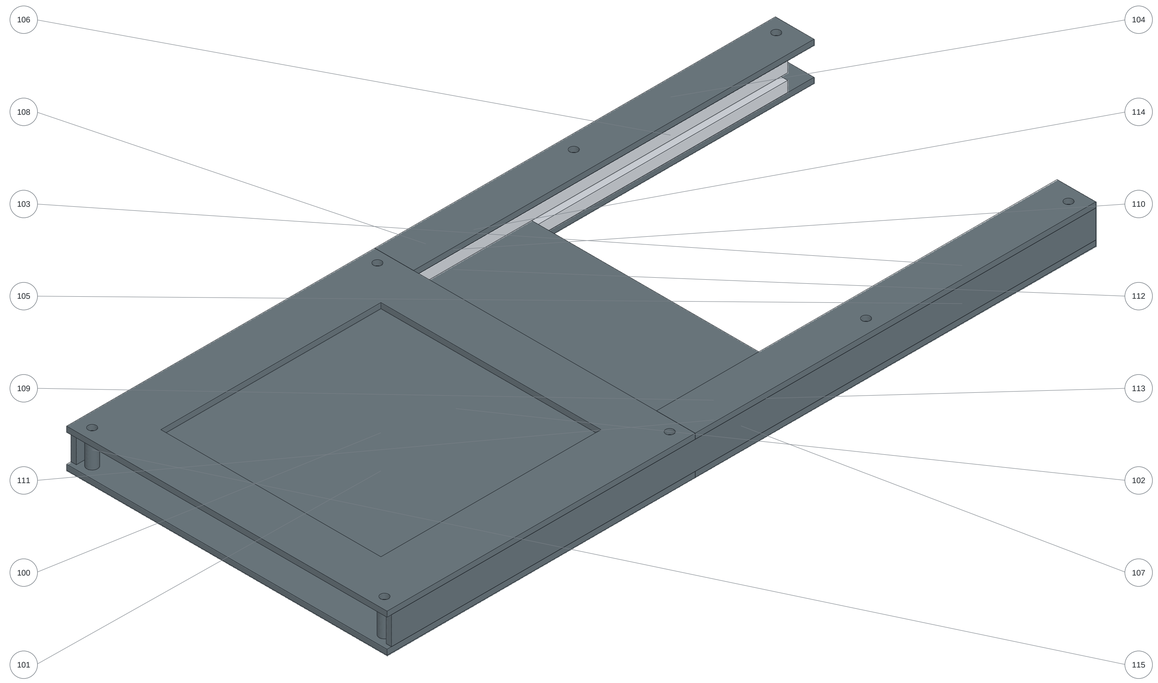

NOTAS DE FABRICACIÓN Y MONTAJE

1. Hoja de cierre, guías y liners se muestran en posición cerrada de referencia.
2. Accionamiento: cremallera y piñón con reducción manual; pasador cautivo de bloqueo.
3. Ajustar paralelismo de guías y comprobar recorrido completo antes del montaje de la guarda.
4. Conservar espesores de casquillos y UHMWPE del CAD; ajustar fijaciones manteniendo libre la corredera.

Cotas en mm. ISO2768-m. Soldaduras según cuadro JF. Contornos: CAD/DXF.

TALADROS DE PIEZAS DEL CONJUNTO / COORDENADAS LOCALES mm / ORIGEN LOCAL


P100 T1: D9; X-166 Y-162 Z0; eje Z
P100 T2: D9; X166 Y-162 Z0; eje Z
P100 T3: D9; X-166 Y162 Z0; eje Z
P100 T4: D9; X166 Y162 Z0; eje Z
P101 T1: D9; X-166 Y-162 Z0; eje Z
P101 T2: D9; X166 Y-162 Z0; eje Z
P101 T3: D9; X-166 Y162 Z0; eje Z
P101 T4: D9; X166 Y162 Z0; eje Z

P103 T1: D9; X6 Y-17.5 Z0; eje Z
P103 T2: D9; X6 Y212.5 Z0; eje Z
P104 T1: D9; X-6 Y-17.5 Z0; eje Z
P104 T2: D9; X-6 Y212.5 Z0; eje Z
P105 T1: D9; X6 Y-17.5 Z0; eje Z
P105 T2: D9; X6 Y212.5 Z0; eje Z
P106 T1: D9; X-6 Y-17.5 Z0; eje Z
P106 T2: D9; X-6 Y212.5 Z0; eje Z


				REBABAR Y ROMPER ARISTAS	NO CAMBIAR LA ESCALA	REVISIÓN
SESUVECA DEL PERÚ						
	NOMBRE	FIRMA	FECHA			TÍTULO: Compuerta de descarga ensamblada
DIBUJ.	Javier Acevedo		16/10/26			
VERIF.						
APROB.						
FABR.						
CALID.				MATERIAL: SEGÚN LISTA DE MATERIALES		N.º DE DIBUJO EB-09 / A1
PESO: SEGÚN CAD / BOM				ESCALA: INDICADA		ESTACIÓN DE DESCARGA BIGBAG / HOJA 9 DE 17

Guarda, ensacado y captación

ALZADO ESCALA 1:15

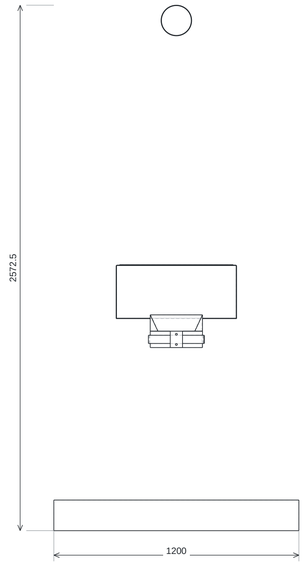


PLANTA ESCALA 1:15

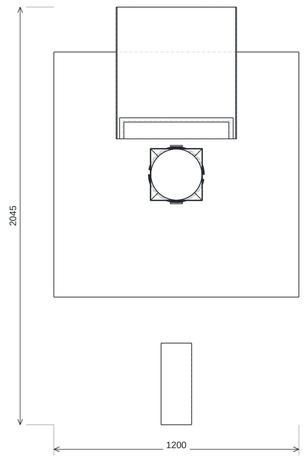

POS.	CANT.	DESCRIPCIÓN / CORTE NOMINAL mm	MATERIAL
116	1	MS01 TRANSICION CUADRADO REDONDO 3	ASTM A36
117	1	MS02 CUELLO ID250 OD256 L80	ACERO
118	2	MS03 SECTOR 170deg ID268 t3 H40	ASTM A36
119	2	MS04 LINER EPDM3 SECTOR 170	EPDM
120	2	MS05 SOPORTE 60x80x6	ASTM A36
121	1	SACO 25 50kg	SEGÚN CATÁLOGO / COMPRA
122	1	BALANZA 2t 1200	SEGÚN CATÁLOGO / COMPRA
125	1	CAPTACION POLVO DN150	SEGÚN CATÁLOGO / COMPRA
126	1	MG11 GUARDA U 590x645x260 R3 t2	ASTM A36
127	1	MG12 GUARDA FONDO 590x645x2	ASTM A36
128	1	MG13 GUARDA TESTERO 586x258x2	ASTM A36
129	1	MG14	Junta flexible disipativa compatible con polvo; seleccion final conforme materiales del proyecto

ISOMÉTRICO A COLOR / REFERENCIA DE MONTAJE

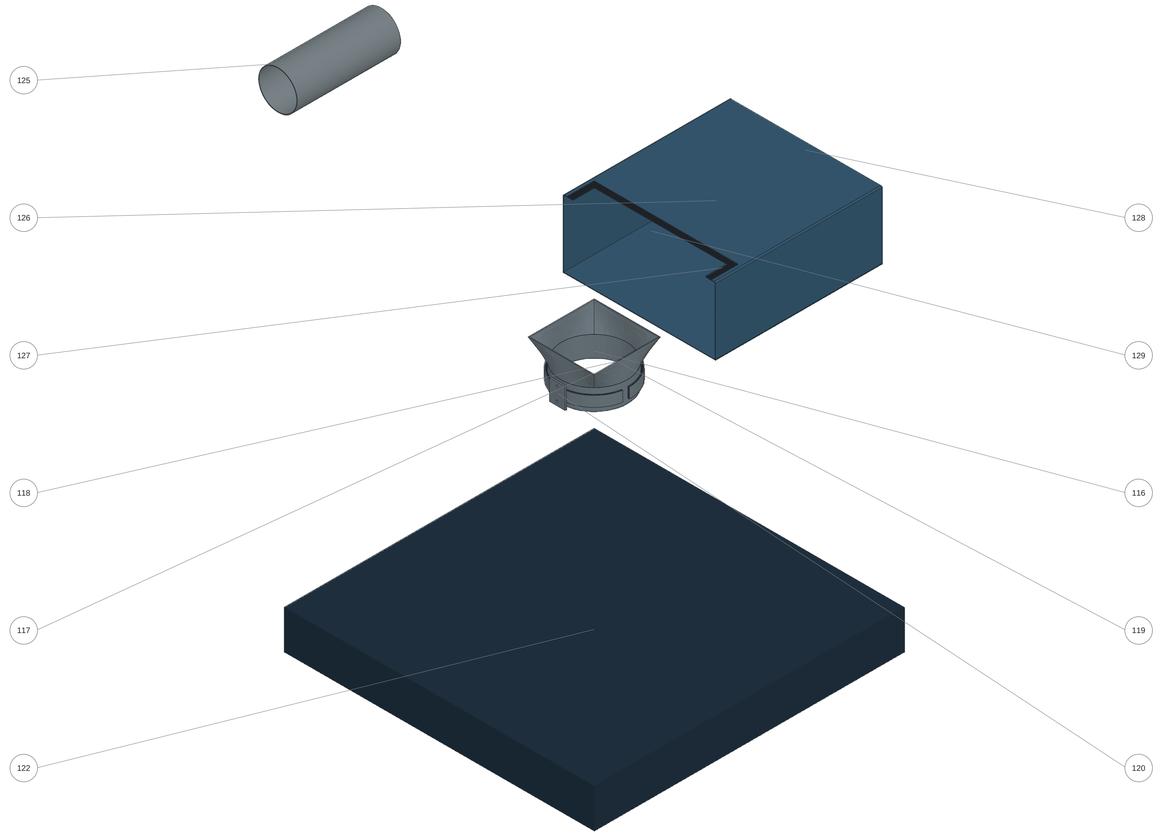

NOTAS DE FABRICACIÓN Y MONTAJE

1. Guarda cerrada de compuerta: envolvente final 590 x 645 x 262.
2. Cota superior de recinto protegido Z = 3 430; despeje nominal de traslado: 90.
3. Salida libre DN250; interfaz de saco y balanza de plataforma 1 200 x 1 200 / 2 t.
4. Captación DN150: 800 m3/h a 1 500 Pa en colector; balance de presión según memoria.
5. Conexiones desmontables para limpieza y mantenimiento. Protección contra polvo combustible según análisis del proyecto.

Cotas en mm. ISO2768-m. Soldaduras según cuadro JF. Contornos: CAD/DXF.

TALADROS DE PIEZAS DEL CONJUNTO / COORDENADAS LOCALES mm / ORIGEN LOCAL


P120 T1: D9; X0 Y-25 Z0; eje Z

P120 T2: D9; X0 Y25 Z0; eje Z

				REBABAR Y ROMPER ARISTAS	NO CAMBIAR LA ESCALA	REVISIÓN
SESUVECA DEL PERÚ						
	NOMBRE	FIRMA	FECHA			TÍTULO: Guarda, ensacado y captación
DIBUJ.	Javier Acevedo		16/10/26			
VERIF.						
APROB.						
FABR.						
CALID.				MATERIAL: SEGÚN LISTA DE MATERIALES		N.º DE DIBUJO EB-10 / A1
PESO: SEGÚN CAD / BOM				ESCALA: INDICADA		ESTACIÓN DE DESCARGA BIGBAG / HOJA 10 DE 17


Carro, suspensión y traba de posición

ALZADO ESCALA 1:5

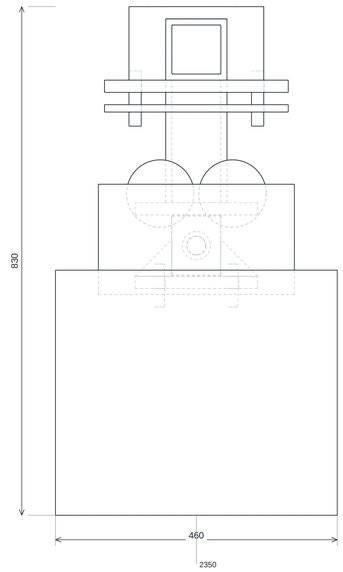


DATUM GLOBAL X (mm)

PERFIL ESCALA 1:8

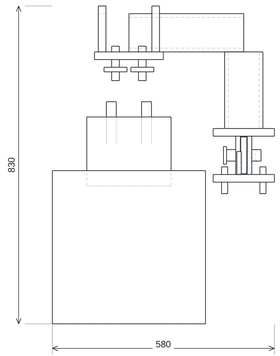

POS.	CANT.	DESCRIPCIÓN / CORTE NOMINAL mm	MATERIAL
95	1	TECLE 2IERENCIA	SEGÚN CATÁLOGO / COMPRA
96	1	CARRO MOTORIZADOERENCIA	SEGÚN CATÁLOGO / COMPRA
97	1	CADENA ENVELOPE	SEGÚN CATÁLOGO / COMPRA
98	1	BIGBAG 1000x1000x1000	SEGÚN CATÁLOGO / COMPRA
99	4	ASA BIGBAG	SEGÚN CATÁLOGO / COMPRA
133	8	ANCLA ARANDELA D30 D18 t3	SEGÚN CATÁLOGO / COMPRA
134	8	ANCLA TUERCA M16 AF24 H13	Acero clase8
136	1	TC01 SADDLE 300x180x20	ASTM A36
137	2	TC02 DUPLICADOR ALA 300x60x12	ASTM A36
138	1	TC03 BRAZO SHS100x100x10 S355 L300	S355 certificado
139	1	TC04 POSTE SHS100x100x10 S355 L200	S355 certificado
140	1	TC05 PLACA HORQUILLA 200x160x20	ASTM A36
141	2	TC06 OREJA 80x100x12 D31	ASTM A36
142	1	TC07 RECEPTOR 80x96x16 D31	A36
143	1	TC08 ADAPTADOR 200x160x20 4D18	A36
144	2	TC09 CARTABON SADDLE 220x120x20	ASTM A36
145	2	TC10 CARTABON RECEPTOR 60x60x12	ASTM A36
146	1	TC11 PASADOR D30 L90 FY355	Acero certificado Fy>=355MPa
147	1	TC12 CABEZA D46 L8	ASTM A36 / SEGÚN MEMORIA
148	1	TC13 CLIP R D3 L38	SEGÚN CATÁLOGO / COMPRA
149	1	TC17 OJAL CABLE 40x12x3	ASTM A36
150	1	TC18 CABLE CAUTIVO D3 SEG1	Cable inoxidable cautivo flexible; longitud min350mm
151	1	TC18 CABLE CAUTIVO D3 SEG2	Cable inoxidable cautivo flexible; longitud min350mm
152	1	TC18 CABLE CAUTIVO D3 SEG3	Cable inoxidable cautivo flexible; longitud min350mm
153	4	TC14 PERNO M20 L90 8p8	Clase8.8
154	8	TC15 ARANDELA D37 D22 t3	SEGÚN CATÁLOGO / COMPRA
155	8	TC16 TUERCA M20 D36 ID21 H16	SEGÚN CATÁLOGO / COMPRA
156	4	TC19 ESPARRAGO M16 L70 8p8	Clase8.8
157	4	KITO RUEDA D110 PASO118	SEGÚN CATÁLOGO / COMPRA

ISOMÉTRICO A COLOR / REFERENCIA DE MONTAJE

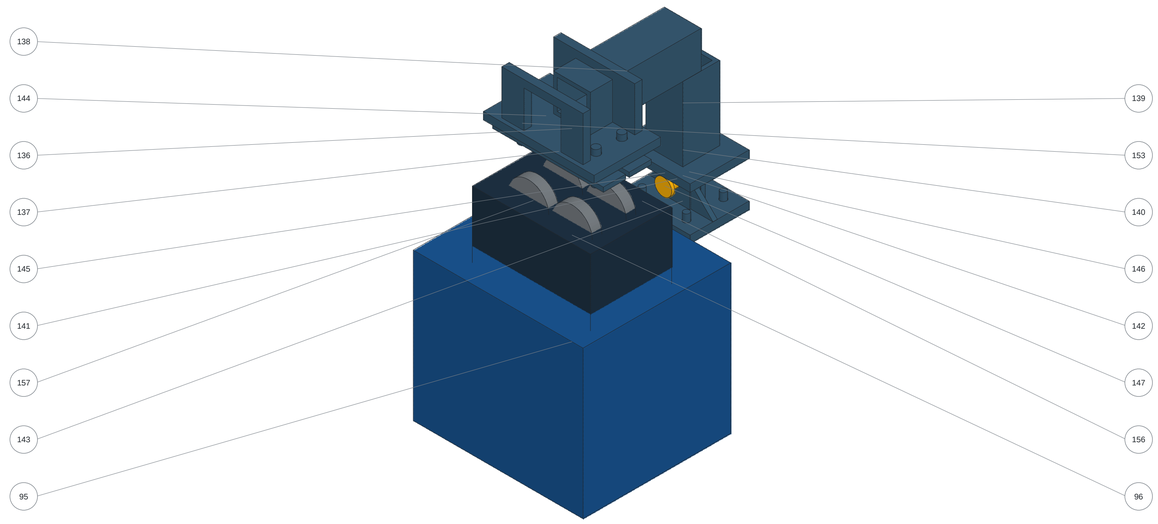

NOTAS DE FABRICACIÓN Y MONTAJE

1. Referencia comercial KITO SHER2M020IS-IS / 2 t; C de catálogo = 475.
2. Mantener el conjunto comercial de tecle y carro según especificación de compra.
3. Pasador cautivo D30 Fy >=355 MPa; dos orejas t12 y placa receptora t16; taladros D31.
4. Inserción únicamente con carro detenido. Inhibir traslación con pasador insertado.
5. Patrones de fijación TC y tolerancias de montaje según detalle / CAD.

Cotas en mm. ISO2768-m. Soldaduras según cuadro JF. Contornos: CAD/DXF.


TALADROS DE PIEZAS DEL CONJUNTO / COORDENADAS LOCALES mm / ORIGEN LOCAL

P136 T1: D22; X-100 Y-35 Z0; eje Z
P136 T2: D22; X-100 Y35 Z0; eje Z
P136 T3: D22; X100 Y-35 Z0; eje Z
P136 T4: D22; X100 Y35 Z0; eje Z
P137 T1: D22; X-100 Y0 Z0; eje Z
P137 T2: D22; X100 Y0 Z0; eje Z
P141 T1: D31; X0 Y0 Z0; eje Z
P142 T1: D31; X0 Y0 Z0; eje Z
P143 T1: D18; X-60 Y-50 Z0; eje Z
P143 T2: D18; X-60 Y50 Z0; eje Z
P143 T3: D18; X60 Y-50 Z0; eje Z
P143 T4: D18; X60 Y50 Z0; eje Z
P146 B1: D4.5; X0 Y16 Z78; eje Y
P149 T1: D4; X12 Y0 Z0; eje Z

				REBABAR Y ROMPER ARISTAS	NO CAMBIAR LA ESCALA		REVISIÓN
SESUVECA DEL PERÚ							
	NOMBRE	FIRMA	FECHA			TÍTULO:	
DIBUJ.	Javier Acevedo		16/10/26			Carro, suspensión y traba de posición	
VERIF.							
APROB.							
FABR.							
CALID.				MATERIAL: SEGÚN LISTA DE MATERIALES		N.º DE DIBUJO: EB-11	A1
PESO: SEGÚN CAD / BOM				ESCALA: INDICADA		ESTACIÓN DE DESCARGA BIGBAG	HOJA 11 DE 17


Plataforma de acceso ensamblada

PLANTA ESCALA 1:8

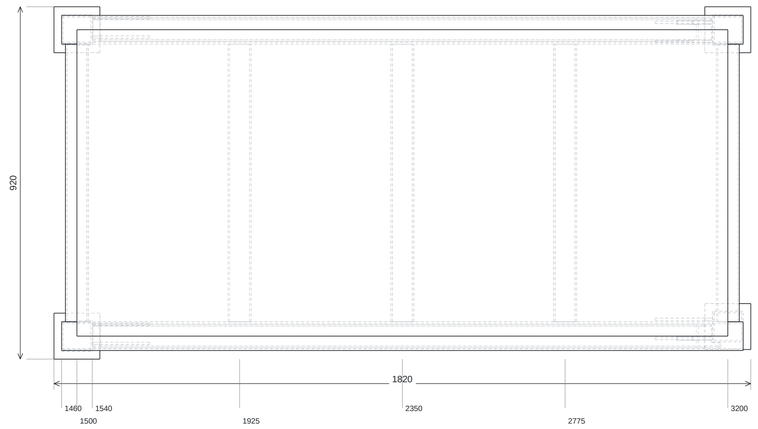


DATUM GLOBAL X (mm)

ALZADO ESCALA 1:15

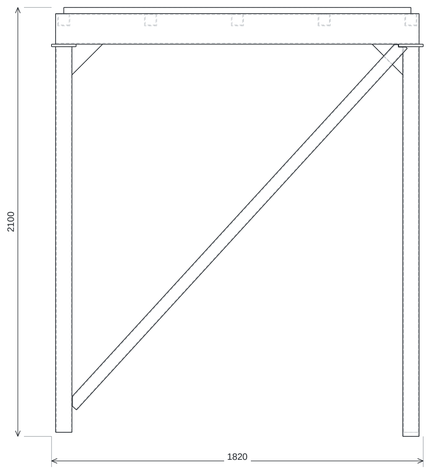

POS.	CANT.	DESCRIPCIÓN / CORTE NOMINAL mm	MATERIAL
18	3	SHS80x80x4 x 1888	ASTM A500 Gr.B
19	1	SHS80x80x4 x 1908	ASTM A500 Gr.B
20	2	RHS150x75x5 x 1780	ASTM A500 Gr.B
21	5	SHS60x60x4 x 725	ASTM A500 Gr.B
68	4	P02 CAP COLUMNA 120x120x12	ASTM A36
69	8	P02 CARTELA 150x150x6	ASTM A36
123	1	PLATAFORMA REJILLA COMERCIAL	SEGÚN CATÁLOGO / COMPRA
193-194	2	SHS60x60x4 x 2399.44	ASTM A500 Gr.B

ISOMÉTRICO A COLOR / REFERENCIA DE MONTAJE

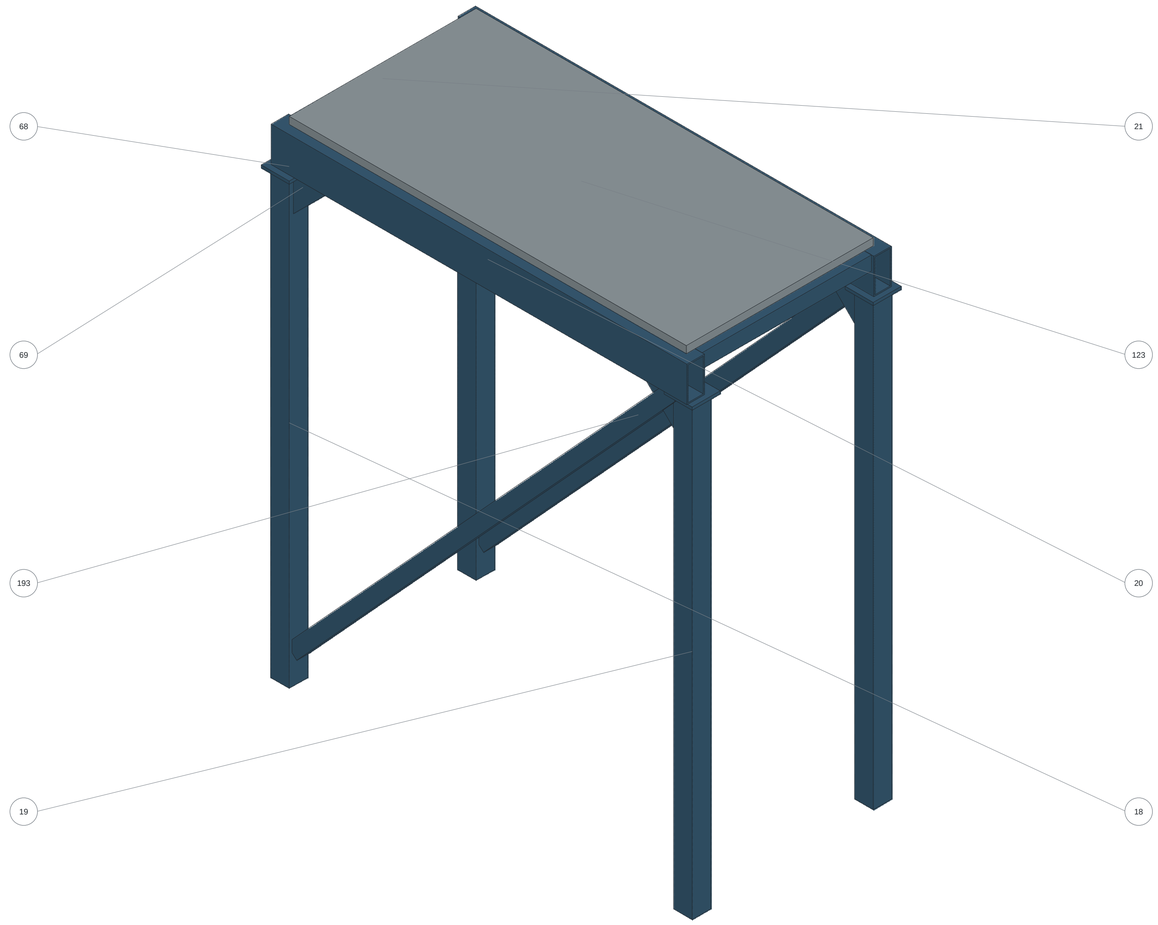

NOTAS DE FABRICACIÓN Y MONTAJE


1. Bastidor, cuatro postes y apoyos de rejilla forman el conjunto de plataforma.
2. No soldar la rejilla comercial a través de superficies de drenaje; fijaciones según compra.
3. Unión J01 con escalera según cuadro de juntas. Montaje en campo mediante uniones desmontables.

Cotas en mm. ISO2768-m. Soldaduras según cuadro JF. Contornos: CAD/DXF.

				REBABAR Y ROMPER ARISTAS	NO CAMBIAR LA ESCALA		REVISIÓN
SESUVECA DEL PERÚ							
	NOMBRE	FIRMA	FECHA			TÍTULO: Plataforma de acceso ensamblada	
DIBUJ.	Javier Acevedo		16/10/26				
VERIF.							
APROB.							
FABR.							
CALID.				MATERIAL: SEGÚN LISTA DE MATERIALES		N.º DE DIBUJO EB-12	A1
PESO: SEGÚN CAD / BOM				ESCALA: INDICADA		ESTACIÓN DE DESCARGA BIGBAG	HOJA 12 DE 17


Escalera y desembarco ensamblados

ALZADO ESCALA 1:15

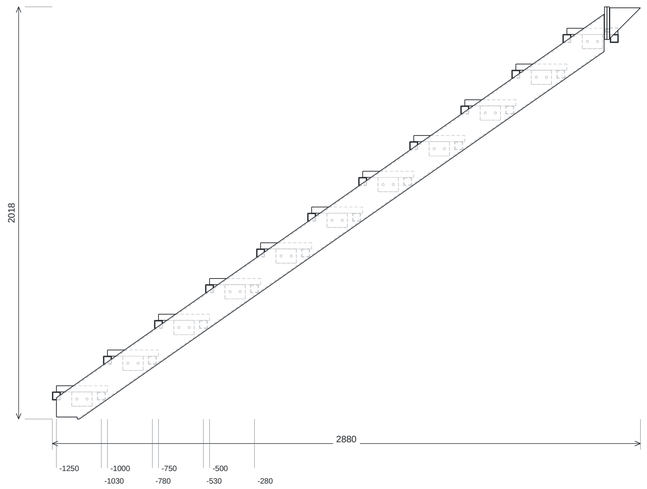


DATUM GLOBAL X (mm)

PLANTA ESCALA 1:10

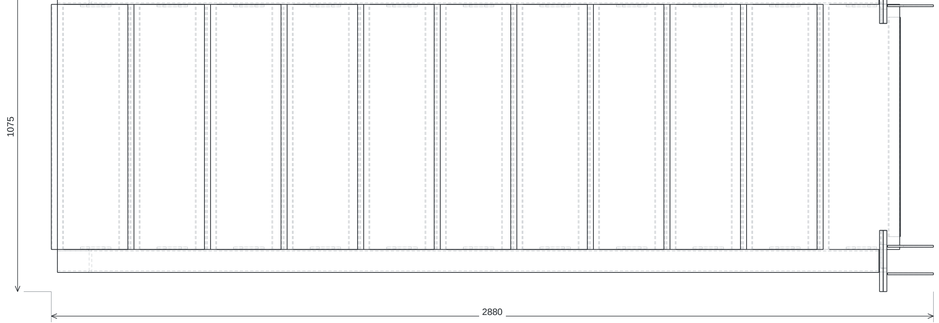

POS.	CANT.	DESCRIPCIÓN / CORTE NOMINAL mm	MATERIAL
22,197	22	SHS40x40x3 x 800	ASTM A500 Gr.B
75,198-199	4	J01 CARTELA 150x150x6	ASTM A36
76	22	J02 PLACA 100x70x6	ASTM A36
124	11	PELDAÑO REJILLA COMERCIAL	SEGÚN CATÁLOGO / COMPRA
195-196	2	RHS150x75x5 x 3356.8	ASTM A500 Gr.B
216,218	2	J01 EXTREMO 200x160x12	ASTM A36
217,219	2	J01 SOPORTE 200x160x12	ASTM A36

ISOMÉTRICO A COLOR / REFERENCIA DE MONTAJE

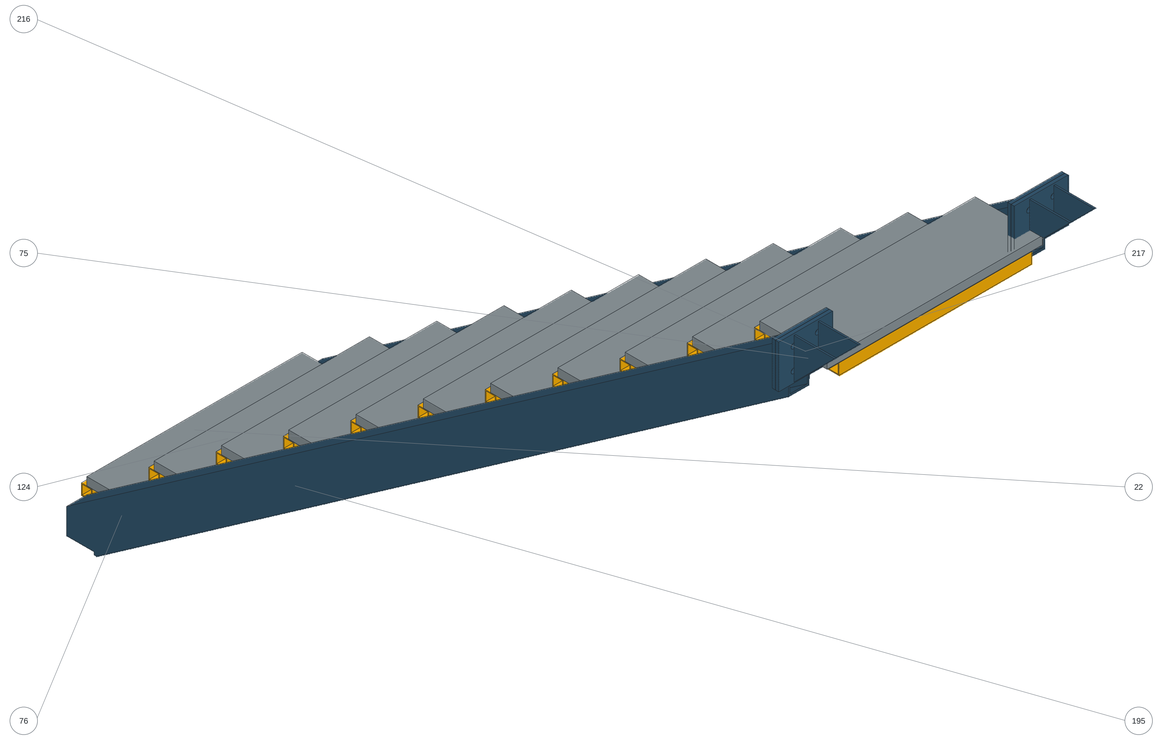

NOTAS DE FABRICACIÓN Y MONTAJE

1. Dos zancas RHS150x75x5 con recorte final de desembarco; peldaños según BOM.
2. Cortar según lista y ensamblar en útil sobre los ejes indicados.
3. Preparaciones J01 / J02 y extremos con luz 2 mm según las juntas indicadas; no soldar las holguras LUZ.

Cotas en mm. ISO2768-m. Soldaduras según cuadro JF. Contornos: CAD/DXF.


TALADROS DE PIEZAS DEL CONJUNTO / COORDENADAS LOCALES mm / ORIGEN LOCAL

P76 T1: D11; X-25 Y0 Z0; eje Z
P76 T2: D11; X25 Y0 Z0; eje Z
P216 T1: D18; X-45 Y-40 Z0; eje Z
P216 T2: D18; X-45 Y40 Z0; eje Z
P216 T3: D18; X45 Y-40 Z0; eje Z
P216 T4: D18; X45 Y40 Z0; eje Z
P217 T1: D18; X-45 Y-40 Z0; eje Z
P217 T2: D18; X-45 Y40 Z0; eje Z
P217 T3: D18; X45 Y-40 Z0; eje Z
P217 T4: D18; X45 Y40 Z0; eje Z
P218 T1: D18; X-45 Y-40 Z0; eje Z
P218 T2: D18; X-45 Y40 Z0; eje Z
P218 T3: D18; X45 Y-40 Z0; eje Z
P218 T4: D18; X45 Y40 Z0; eje Z
P219 T1: D18; X-45 Y-40 Z0; eje Z
P219 T2: D18; X-45 Y40 Z0; eje Z
P219 T3: D18; X45 Y-40 Z0; eje Z
P219 T4: D18; X45 Y40 Z0; eje Z

				REBABAR Y ROMPER ARISTAS	NO CAMBIAR LA ESCALA	REVISIÓN
SESUVECA DEL PERÚ						
	NOMBRE	FIRMA	FECHA			TÍTULO: Escalera y desembarco ensamblados
DIBUJ.	Javier Acevedo		16/10/26			
VERIF.						
APROB.						
FABR.						
CALID.				MATERIAL: SEGÚN LISTA DE MATERIALES		N.º DE DIBUJO EB-13 / A1
PESO: SEGÚN CAD / BOM				ESCALA: INDICADA		ESTACIÓN DE DESCARGA BIGBAG / HOJA 13 DE 17


Barandas, pasamanos y rodapiés

ALZADO ESCALA 1:20

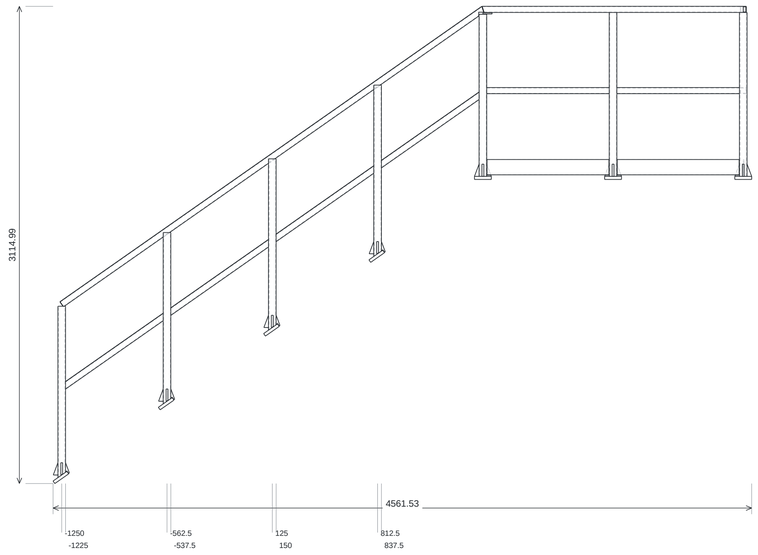


DATUM GLOBAL X (mm)

PLANTA ESCALA 1:15

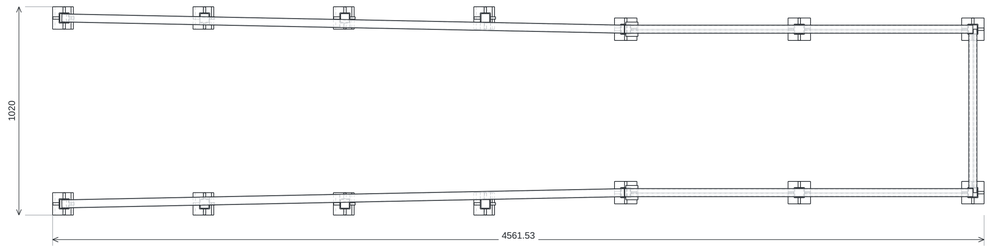

POS.	CANT.	DESCRIPCIÓN / CORTE NOMINAL mm	MATERIAL
22,207	5	SHS40x40x3 x 800	ASTM A500 Gr.B
23,185	6	SHS50x50x4 x 1070	ASTM A500 Gr.B
24-31	8	SHS40x40x3 x 778.27	ASTM A500 Gr.B
32	1	SHS40x40x3 x 750	ASTM A500 Gr.B
35,208-210,213-215	8	SHS50x50x4 x 1101.27	ASTM A500 Gr.B
77	14	U05 BASE POSTE 110x110x20	ASTM A36
78,220-253	56	U05 CARTELA 30x80x12 / PREPARACIÓN POR JF	ASTM A36
183-184	2	SHS40x40x3 x 1700	ASTM A500 Gr.B
186	2	JF CAP TRANSICION 60x70x8	ASTM A36
204,211	2	SHS40x40x3 x 3357.25	ASTM A500 Gr.B
205,212	2	RODAPIE LARGO 1700x100x5	ASTM A36
206	1	RODAPIE TESTERO 800x100x5	ASTM A36

ISOMÉTRICO A COLOR / REFERENCIA DE MONTAJE

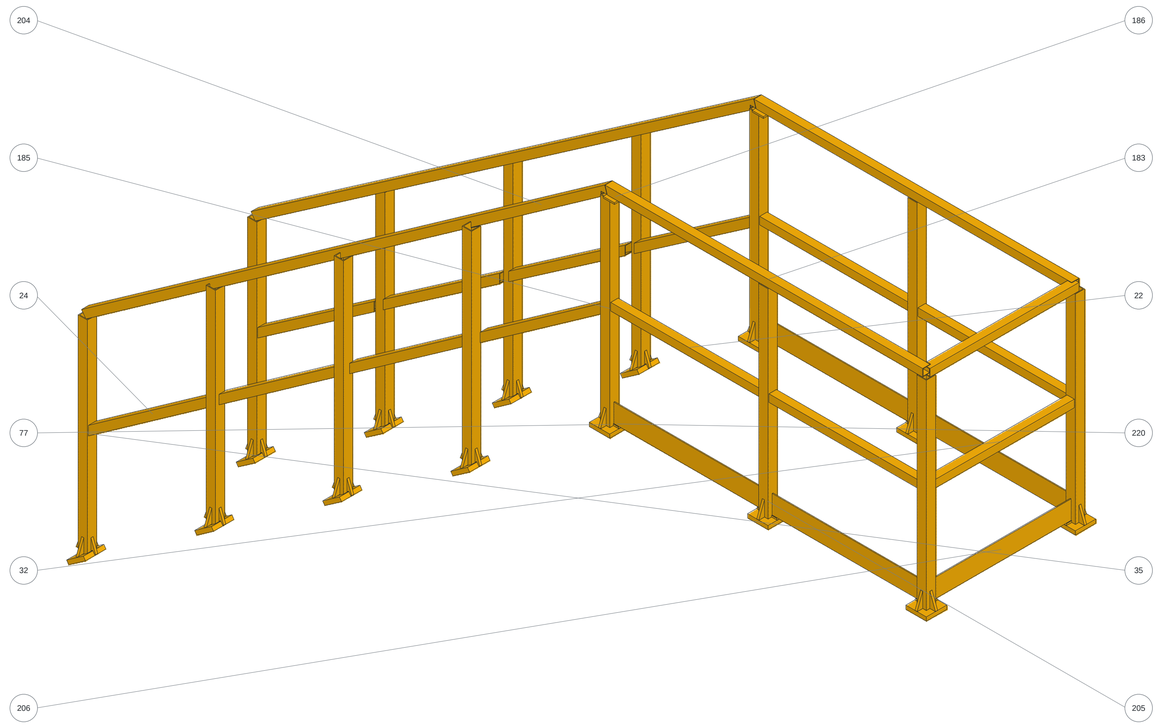

NOTAS DE FABRICACIÓN Y MONTAJE


1. Rodapiés t5; postes SHS50x50x4; pasamanos SHS40x40x3.
2. Conservar ingletes reales y tapas de transición 60x70x8 en extremos superiores.
3. Uniones a pared de 3 mm: PJP a2 según preparación y cuadro de juntas.
4. Soldar en taller según cuadro; eliminar bordes cortantes y asegurar continuidad del pasamanos.

Cotas en mm. ISO2768-m. Soldaduras según cuadro JF. Contornos: CAD/DXF.

				REBABAR Y ROMPER ARISTAS	NO CAMBIAR LA ESCALA		REVISIÓN
SESUVECA DEL PERÚ							
	NOMBRE	FIRMA	FECHA			TÍTULO: Barandas, pasamanos y rodapiés	
DIBUJ.	Javier Acevedo		16/10/26				
VERIF.							
APROB.							
FABR.							
CALID.				MATERIAL: SEGÚN LISTA DE MATERIALES		N.º DE DIBUJO EB-14	A1
PESO: SEGÚN CAD / BOM				ESCALA: INDICADA		ESTACIÓN DE DESCARGA BIGBAG	HOJA 14 DE 17


Cruceta de izaje 2 t ensamblada

PLANTA ESCALA 1:8

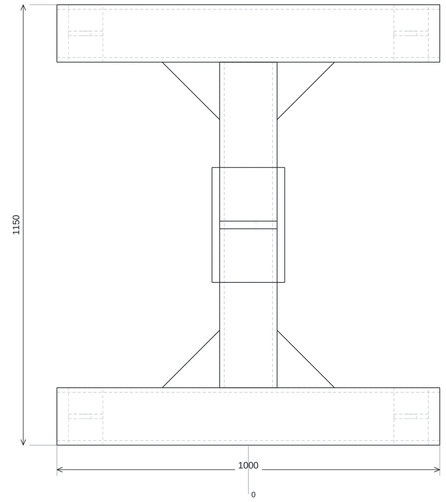


DATUM GLOBAL X (mm)

ALZADO ESCALA 1:4

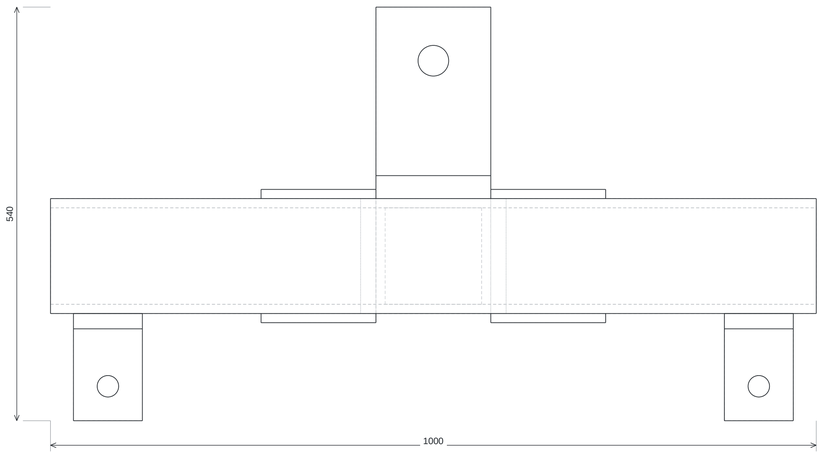

POS.	CANT.	DESCRIPCIÓN / CORTE NOMINAL mm	MATERIAL
33	2	SHS150x150x12 x 1000	ASTM A500 Gr.B
34	1	SHS150x150x12 x 850	ASTM A500 Gr.B
79	1	OREJA CENTRAL 150x220x20	ASTM A36
80	4	OREJA EXTREMA 90x120x12	ASTM A36
81	4	CR RESPALDO EXTREMA 90x150x20	ASTM A36
82	8	CR CARTELA TRIANGULAR 150x150x12	ASTM A36
83	1	CR CAP CENTRAL 150x300x30	ASTM A36
84	2	CR CHEEK 300x150x20	ASTM A36

ISOMÉTRICO A COLOR / REFERENCIA DE MONTAJE

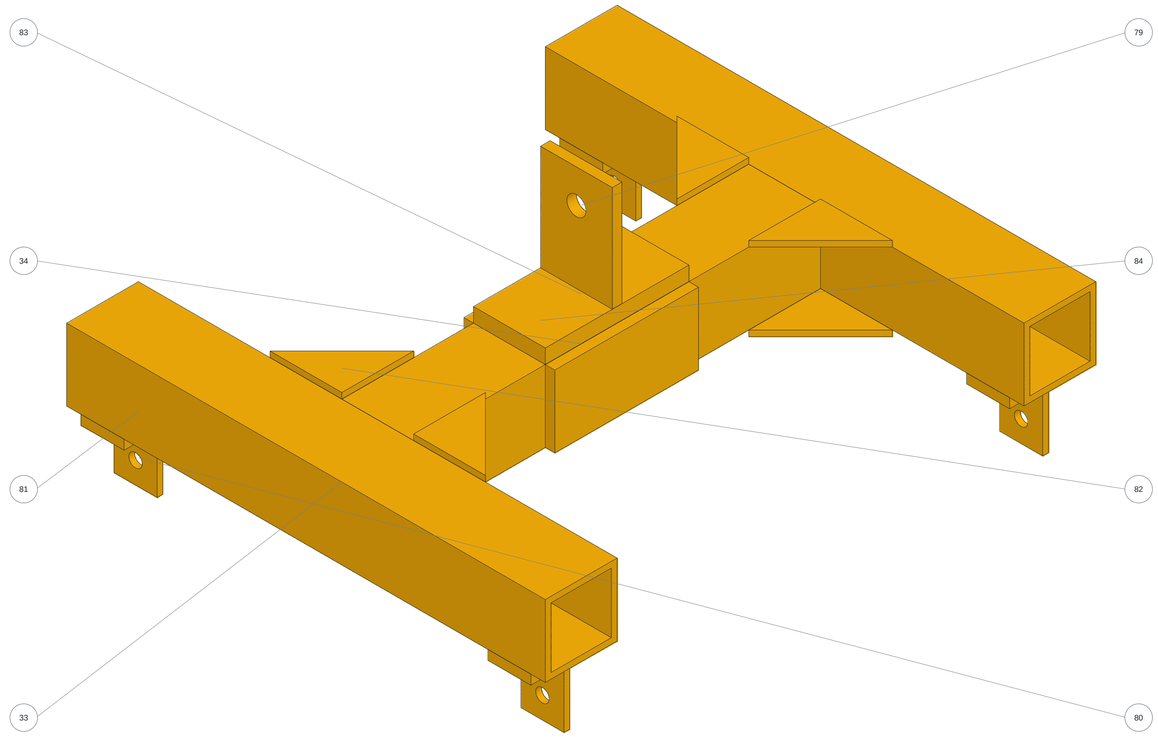

NOTAS DE FABRICACIÓN Y MONTAJE

1. Capacidad nominal 2 000 kg; 125 000 ciclos; Categoría B / Servicio Clase 2.
2. Perfiles SHS150x150x12; oreja central, orejas de asas, respaldos y cartelas según BOM.
3. Mantener reparto y geometría de toma del cálculo; identificación indeleble de capacidad y trazabilidad.
4. Ejecutar inspección y prueba de carga según protocolo antes de la puesta en servicio.

Cotas en mm. ISO2768-m. Soldaduras según cuadro JF. Contornos: CAD/DXF.

TALADROS DE PIEZAS DEL CONJUNTO / COORDENADAS LOCALES mm / ORIGEN LOCAL

P79 T1: D40; X0 Y150 Z0; eje Z

P80 T1: D28; X0 Y75 Z0; eje Z

				REBABAR Y ROMPER ARISTAS	NO CAMBIAR LA ESCALA	REVISIÓN
SESUVECA DEL PERÚ						
	NOMBRE	FIRMA	FECHA			TÍTULO: Cruceta de izaje 2 t ensamblada
DIBUJ.	Javier Acevedo		16/10/26			
VERIF.						
APROB.						
FABR.						
CALID.				MATERIAL: SEGÚN LISTA DE MATERIALES		N.º DE DIBUJO EB-15 / A1
PESO: SEGÚN CAD / BOM				ESCALA: INDICADA		ESTACIÓN DE DESCARGA BIGBAG / HOJA 15 DE 17

Uniones de fabricación / Cuadro 1 de 2

ID	MIEMBRO	SOPORTE	TIPO	a mm	L mm	CENTRO GLOBAL X/Y/Z mm	EJECUCIÓN
JF-001	BRL-A--1	COL-0--1	LUZ	-	-	POR MIEMBRO / SOPORTE	NO SOLDAR / LUZ 2
JF-002	BRL-A--1	COL-3.2--1	LUZ	-	-	POR MIEMBRO / SOPORTE	NO SOLDAR / LUZ 2
JF-003	BRL-B--1	COL-0--1	LUZ	-	-	POR MIEMBRO / SOPORTE	NO SOLDAR / LUZ 2
JF-004	BRL-B--1	COL-3.2--1	LUZ	-	-	POR MIEMBRO / SOPORTE	NO SOLDAR / LUZ 2
JF-005	KNE--1	COL-0--1	LUZ	-	-	POR MIEMBRO / SOPORTE	NO SOLDAR / LUZ 2
JF-006	BRL-A-1	COL-0-1	LUZ	-	-	POR MIEMBRO / SOPORTE	NO SOLDAR / LUZ 2
JF-007	BRL-A-1	COL-3.2-1	LUZ	-	-	POR MIEMBRO / SOPORTE	NO SOLDAR / LUZ 2
JF-008	BRL-B-1	COL-0-1	LUZ	-	-	POR MIEMBRO / SOPORTE	NO SOLDAR / LUZ 2
JF-009	BRL-B-1	COL-3.2-1	LUZ	-	-	POR MIEMBRO / SOPORTE	NO SOLDAR / LUZ 2
JF-010	KNE-1	COL-0-1	LUZ	-	-	POR MIEMBRO / SOPORTE	NO SOLDAR / LUZ 2
JF-011	PBRACE-1.1	PPOST-1.5-1.1	CJP	3.72	173.92	1542 / 1300 / 181.8	TALLER / WPS
JF-012	PBRACE-1.1	PPOST-3.2-1.125	CJP	3.72	115.05	3161.3 / 1306.2 / 1883.7	TALLER / WPS
JF-013	PBRACE-1.9	PPOST-1.5-1.9	CJP	3.72	173.92	1542 / 2100 / 181.8	TALLER / WPS
JF-014	PBRACE-1.9	PPOST-3.2-1.9	CJP	3.72	94.83	3158 / 2106.7 / 1880.9	TALLER / WPS
JF-015	STRING-1.1	BASE_ACCESO_STRING-1.1	CJP	4.65	224	-1194.4 / 1262.5 / 21.6	TALLER / WPS
JF-016	STRING-1.9	BASE_ACCESO_STRING-1.9	CJP	4.65	224	-1194.4 / 2137.5 / 21.6	TALLER / WPS
JF-017	STEP-11-1.47	PPOST-1.5-1.1	CJP	2.79	148	1482 / 1342 / 1875	TALLER / WPS
JF-018	STEP-11-1.47	PPOST-1.5-1.9	CJP	2.79	148	1482 / 2058 / 1875	TALLER / WPS
JF-019	KNE--1	TRA-0	CJP	3.72	156.71	0 / -381 / 5498	TALLER / WPS
JF-020	KNE-1	TRA-0	CJP	3.72	156.71	-0 / 381 / 5498	TALLER / WPS
JF-021	BRL-A--1	TIE--1-0.15	LUZ	-	-	POR MIEMBRO / SOPORTE	NO SOLDAR / LUZ 2
JF-022	BRL-B--1	TIE--1-0.15	LUZ	-	-	POR MIEMBRO / SOPORTE	NO SOLDAR / LUZ 2
JF-023	TIE--1-0.15	U02_COLLARX_0_1	CJP	3.72	224	89 / -1000 / 150	TALLER / WPS
JF-024	TIE--1-0.15	BRT_COLLARX_-1_0.15_-1	CJP	3.72	224	3111 / -1000 / 150	TALLER / WPS
JF-025	BRL-A--1	TIE--1-4.79	LUZ	-	-	POR MIEMBRO / SOPORTE	NO SOLDAR / LUZ 2
JF-026	BRL-B--1	TIE--1-4.79	LUZ	-	-	POR MIEMBRO / SOPORTE	NO SOLDAR / LUZ 2
JF-027	TIE--1-4.79	BRT_COLLARX_-1_5.338_-1	CJP	3.72	224	3111 / -1000 / 5430	TALLER / WPS
JF-028	BRL-A--1	U02_COLLARX_0_1	LUZ	-	-	POR MIEMBRO / SOPORTE	NO SOLDAR / LUZ 2
JF-029	BRL-A--1	BRT_COLLARX_-1_5.338_-1	LUZ	-	-	POR MIEMBRO / SOPORTE	NO SOLDAR / LUZ 2
JF-030	BRL-B--1	BRT_COLLARX_-1_0.15_-1	LUZ	-	-	POR MIEMBRO / SOPORTE	NO SOLDAR / LUZ 2
JF-031	KNE--1	U02_COLLARY_8_1	LUZ	-	-	POR MIEMBRO / SOPORTE	NO SOLDAR / LUZ 2
JF-032	BRL-A-1	TIE-1-0.15	LUZ	-	-	POR MIEMBRO / SOPORTE	NO SOLDAR / LUZ 2
JF-033	BRL-B-1	TIE-1-0.15	LUZ	-	-	POR MIEMBRO / SOPORTE	NO SOLDAR / LUZ 2
JF-034	TIE-1-0.15	U02_COLLARX_2_1	CJP	3.72	224	89 / 1000 / 150	TALLER / WPS
JF-035	TIE-1-0.15	BRT_COLLARX_1_0.15_-1	CJP	3.72	224	3111 / 1000 / 150	TALLER / WPS
JF-036	BRL-A-1	TIE-1-4.79	LUZ	-	-	POR MIEMBRO / SOPORTE	NO SOLDAR / LUZ 2
JF-037	BRL-B-1	TIE-1-4.79	LUZ	-	-	POR MIEMBRO / SOPORTE	NO SOLDAR / LUZ 2
JF-038	TIE-1-4.79	BRT_COLLARX_1_5.338_-1	CJP	3.72	224	3111 / 1000 / 5430	TALLER / WPS
JF-039	BRL-A-1	U02_COLLARX_2_1	LUZ	-	-	POR MIEMBRO / SOPORTE	NO SOLDAR / LUZ 2
JF-040	BRL-A-1	BRT_COLLARX_1_5.338_-1	LUZ	-	-	POR MIEMBRO / SOPORTE	NO SOLDAR / LUZ 2
JF-041	BRL-B-1	BRT_COLLARX_1_0.15_-1	LUZ	-	-	POR MIEMBRO / SOPORTE	NO SOLDAR / LUZ 2
JF-042	KNE-1	U02_COLLARY_9_-1	LUZ	-	-	POR MIEMBRO / SOPORTE	NO SOLDAR / LUZ 2
JF-043	PBRACE-1.1	PLONG-1.1	CJP	3.72	97.93	3123.4 / 1300.8 / 1918	TALLER / WPS

a = garganta efectiva de cálculo; L = longitud efectiva. CJP atraviesa la pared menor; PJP según preparación indicada.

LUZ = holgura de 2 mm libre de soldadura. Transferencia de carga por conexión primaria según memoria.

CJP / V60 / RAÍZ 2



PJP a2 / 2 x 45



FILETE / a SEGÚN CÁLCULO



NOTAS DE FABRICACIÓN Y MONTAJE

1. Soldadura conforme a AWS D1.1; verificación AISC360 según memoria.
2. Material de aporte compatible con metal base. CJP/PJP: procedimiento WPS calificado y aceptación según especificación.
3. Juntas primarias U01 / U02 / BRT / TC y anclajes: ver detalles y memoria. Interfaces JF según este cuadro.
4. Montaje en campo mediante uniones desmontables; conservar piezas KITO sin mecanizado ni soldaduras.

Cotas en mm. ISO2768-m. Soldaduras según cuadro JF. Contornos: CAD/DXF.

				REBABAR Y ROMPER ARISTAS	NO CAMBIAR LA ESCALA		REVISIÓN
SESUVECA DEL PERÚ							
	NOMBRE	FIRMA	FECHA			TÍTULO: Uniones de fabricación / Cuadro 1 de 2	
DIBUJ.	Javier Acevedo		16/10/26				
VERIF.							
APROB.							
FABR.							
CALID.				MATERIAL: SEGÚN LISTA DE MATERIALES		N.º DE DIBUJO EB-16	A1
PESO: SEGÚN CAD / BOM				ESCALA: INDICADA		ESTACIÓN DE DESCARGA BIGBAG	HOJA 16 DE 17

Uniones de fabricación / Cuadro 2 de 2

ID	MIEMBRO	SOPORTE	TIPO	a mm	L mm	CENTRO GLOBAL X/Y/Z mm	EJECUCIÓN
JF-044	PBRACE-1.9	PLONG-1.9	CJP	3.72	77.43	3122.2 / 2104.1 / 1918	TALLER / WPS
JF-045	PBRACE-1.1	P02_CAP_PPOST-3.2-1.125	CJP	3.72	79.58	3149.3 / 1293.9 / 1907.8	TALLER / WPS
JF-046	PBRACE-1.1	P02_CARTELA_PPOST-3.2-1.125_-0.025	CJP	3.72	325.48	3111.4 / 1294 / 1867.6	TALLER / WPS
JF-047	PBRACE-1.9	P02_CAP_PPOST-3.2-1.9	CJP	3.72	31.14	3144.4 / 2128 / 1908.3	TALLER / WPS
JF-048	PBRACE-1.9	P02_CARTELA_PPOST-3.2-1.9_-0.025	CJP	3.72	227.65	3104.5 / 2073.5 / 1859.9	TALLER / WPS
JF-049	PBRACE-1.9	P02_CARTELA_PPOST-3.2-1.9_0.025	CJP	3.72	325.48	3111.4 / 2119 / 1867.6	TALLER / WPS
JF-050	RPOST-1.5-1.1	JF_CAP_RPOST-1.5-1.1	CJP	3.72	96	1516.5 / 1300 / 3148	TALLER / WPS
JF-051	RODAPIE_1.1	RPOST-1.5-1.1	CJP	3.72	100	1527 / 1297.5 / 2150	TALLER / WPS
JF-052	RODAPIE_1.1	RPOST-2.35-1.1	CJP	3.72	200	2350 / 1297.5 / 2150	TALLER / WPS
JF-053	RODAPIE_1.1	RPOST-3.2-1.1	CJP	3.72	100	3173 / 1297.5 / 2150	TALLER / WPS
JF-054	RODAPIE_TESTERO	RPOST-3.2-1.1	CJP	3.72	100	3202.5 / 1327 / 2150	TALLER / WPS
JF-055	SRAIL-1.1-1.1	RLONG-1.1-3.2	CJP	2.79	126.71	1497.8 / 1300.1 / 3183.7	TALLER / WPS
JF-056	REND-3.2	RLONG-1.1-3.2	CJP	2.79	120.28	3192.2 / 1318 / 3180	TALLER / WPS
JF-057	SRAILPOST--0.5625-1.045	SRAIL-1.1-1.1	CJP	2.79	120.57	-576.2 / 1255.2 / 1703.6	TALLER / WPS
JF-058	SRAILPOST-0.125-1.045	SRAIL-1.1-1.1	CJP	2.79	104.13	112.9 / 1261.1 / 2186.5	TALLER / WPS
JF-059	SRAILPOST-0.8125-1.045	SRAIL-1.1-1.1	CJP	2.79	87.7	802.6 / 1266.5 / 2670	TALLER / WPS
JF-060	RPOST-1.5-1.9	JF_CAP_RPOST-1.5-1.9	CJP	3.72	96	1516.5 / 2100 / 3148	TALLER / WPS
JF-061	RODAPIE_1.9	RPOST-1.5-1.9	CJP	3.72	100	1527 / 2097.5 / 2150	TALLER / WPS
JF-062	RODAPIE_1.9	RPOST-2.35-1.9	CJP	3.72	200	2350 / 2097.5 / 2150	TALLER / WPS
JF-063	RODAPIE_1.9	RPOST-3.2-1.9	CJP	3.72	100	3173 / 2097.5 / 2150	TALLER / WPS
JF-064	RODAPIE_TESTERO	RPOST-3.2-1.9	CJP	3.72	100	3202.5 / 2073 / 2150	TALLER / WPS
JF-065	SRAIL-1.9-1.1	RLONG-1.9-3.2	CJP	2.79	126.71	1497.8 / 2099.9 / 3183.7	TALLER / WPS
JF-066	REND-3.2	RLONG-1.9-3.2	CJP	2.79	120.28	3192.2 / 2082 / 3180	TALLER / WPS
JF-067	SRAILPOST--0.5625-1.955	SRAIL-1.9-1.1	CJP	2.79	120.57	-576.2 / 2144.8 / 1703.6	TALLER / WPS
JF-068	SRAILPOST-0.125-1.955	SRAIL-1.9-1.1	CJP	2.79	104.13	112.9 / 2138.9 / 2186.5	TALLER / WPS
JF-069	SRAILPOST-0.8125-1.955	SRAIL-1.9-1.1	CJP	2.79	87.7	802.6 / 2133.5 / 2670	TALLER / WPS
JF-070	J01_EXTREMO_1.0625	P02_CAP_PPOST-1.5-1.1	LUZ	-	-	POR MIEMBRO / SOPORTE	NO SOLDAR / LUZ 2
JF-071	J01_SOPORTE_1.0625	P02_CAP_PPOST-1.5-1.1	CJP	11.16	280.43	1452 / 1300.1 / 1913.7	TALLER / WPS
JF-072	J01_CARTELA_1.0625_1	P02_CAP_PPOST-1.5-1.1	LUZ	-	-	POR MIEMBRO / SOPORTE	NO SOLDAR / LUZ 2
JF-073	J01_EXTREMO_1.9375000000000002	P02_CAP_PPOST-1.5-1.9	LUZ	-	-	POR MIEMBRO / SOPORTE	NO SOLDAR / LUZ 2
JF-074	J01_SOPORTE_1.9375000000000002	P02_CAP_PPOST-1.5-1.9	CJP	11.16	280.43	1452 / 2099.9 / 1913.7	TALLER / WPS
JF-075	J01_CARTELA_1.9375000000000002_-1	P02_CAP_PPOST-1.5-1.9	LUZ	-	-	POR MIEMBRO / SOPORTE	NO SOLDAR / LUZ 2
JF-076	J01_CARTELA_1.0625_-1	J01_EXTREMO_1.0625	LUZ	-	-	POR MIEMBRO / SOPORTE	NO SOLDAR / LUZ 2
JF-077	J01_CARTELA_1.0625_1	J01_EXTREMO_1.0625	LUZ	-	-	POR MIEMBRO / SOPORTE	NO SOLDAR / LUZ 2
JF-078	J01_CARTELA_1.0625_-1	J01_SOPORTE_1.0625	CJP	5.58	150	1460 / 1220.5 / 1950	TALLER / WPS
JF-079	J01_CARTELA_1.0625_1	J01_SOPORTE_1.0625	CJP	5.58	98	1460 / 1310.5 / 1976	TALLER / WPS
JF-080	J01_CARTELA_1.9375000000000002_-1	J01_EXTREMO_1.9375000000000002	LUZ	-	-	POR MIEMBRO / SOPORTE	NO SOLDAR / LUZ 2
JF-081	J01_CARTELA_1.9375000000000002_1	J01_EXTREMO_1.9375000000000002	LUZ	-	-	POR MIEMBRO / SOPORTE	NO SOLDAR / LUZ 2
JF-082	J01_CARTELA_1.9375000000000002_-1	J01_SOPORTE_1.9375000000000002	CJP	5.58	98	1460 / 2095.5 / 1976	TALLER / WPS
JF-083	J01_CARTELA_1.9375000000000002_1	J01_SOPORTE_1.9375000000000002	CJP	5.58	150	1460 / 2185.5 / 1950	TALLER / WPS
JF_CAP_RPOST-1.5-1.1-RAIL	JF_CAP_RPOST-1.5-1.1	RLONG-1.1-3.2	PJP	2	90	1532.5 / 1300 / 3158	TALLER / WPS
JF_CAP_RPOST-1.5-1.9-RAIL	JF_CAP_RPOST-1.5-1.9	RLONG-1.9-3.2	PJP	2	90	1532.5 / 2100 / 3158	TALLER / WPS

a = garganta efectiva de cálculo; L = longitud efectiva. CJP atraviesa la pared menor; PJP según preparación indicada.

LUZ = holgura de 2 mm libre de soldadura. Transferencia de carga por conexión primaria según memoria.

CJP / V60 / RAÍZ 2



PJP a2 / 2 x 45



FILETE / a SEGÚN CÁLCULO



POSICIÓN DE LOS 37 MIEMBROS JF / ORIGEN X,Y,Z mm / VECTOR LOCAL LONGITUDINAL

BRL-A--1 | 87,-955,150 | 0.5,0,0.87
BRL-B--1 | 87,-1045,5430 | 0.5,0,-0.87
KNE--1 | 0,-913,5006.29 | 0,0.75,0.66
BRL-A-1 | 87,1045,150 | 0.5,0,0.87
BRL-B-1 | 87,955,5430 | 0.5,0,-0.87
KNE-1 | 0,913,5006.29 | 0,-0.75,0.66
PBRACE-1.1 | 1540,1300,150 | 0.68,0,0.74
PBRACE-1.9 | 1540,2100,150 | 0.68,0,0.74
STRING-1.1 | -1250,1262.5,25 | 0.82,0,0.57
STRING-1.9 | -1250,2137.5,25 | 0.82,0,0.57
STEP-11-1.47 | 1482,1300,1875 | 0,1,0
TIE--1-0.15 | 75,-1000,150 | 1,0,0
TIE--1-4.79 | 75,-1000,5430 | 1,0,0
TIE-1-0.15 | 75,1000,150 | 1,0,0
TIE-1-4.79 | 75,1000,5430 | 1,0,0
RPOST-1.5-1.1 | 1500,1300,2090 | 0,0,1
RODAPIE_1.1 | 2350,1300,2150 | 0,-1,0
RODAPIE_TESTERO | 3200,1700,2150 | 1,0,0
SRAIL-1.1-1.1 | -1250,1245,1255 | 0.82,0.02,0.57
REND-3.2 | 3200,1300,3180 | 0,1,0
SRAILPOST--0.5625-1.045 | -562.5,1245,622.21 | 0,0,1
SRAILPOST-0.125-1.045 | 125,1245,1103.46 | 0,0,1
SRAILPOST-0.8125-1.045 | 812.5,1245,1584.71 | 0,0,1
RPOST-1.5-1.9 | 1500,2100,2090 | 0,0,1
RODAPIE_1.9 | 2350,2100,2150 | 0,-1,0
SRAIL-1.9-1.1 | -1250,2155,1255 | 0.82,-0.02,0.57
SRAILPOST--0.5625-1.955 | -562.5,2155,622.21 | 0,0,1
SRAILPOST-0.125-1.955 | 125,2155,1103.46 | 0,0,1
SRAILPOST-0.8125-1.955 | 812.5,2155,1584.71 | 0,0,1
J01_EXTREMO_1.0625 | 1434,1262.5,1950 | 1,0,0
J01_SOPORTE_1.0625 | 1446,1262.5,1950 | 1,0,0
J01_CARTELA_1.0625_1 | 1460,1307.5,2025 | 0,1,0
J01_EXTREMO_1.9375000000000002 | 1434,2137.5,1950 | 1,0,0
J01_SOPORTE_1.9375000000000002 | 1446,2137.5,1950 | 1,0,0
J01_CARTELA_1.9375000000000002_-1 | 1460,2092.5,2025 | 0,1,0
J01_CARTELA_1.0625_-1 | 1460,1217.5,2025 | 0,1,0
J01_CARTELA_1.9375000000000002_1 | 1460,2182.5,2025 | 0,1,0

El vector local define la orientación; perfiles / cortes nominales por POS. y conjunto. Preparaciones exactas: CAD / DXF.

				REBABAR Y ROMPER ARISTAS	NO CAMBIAR LA ESCALA		REVISIÓN
SESUVECA DEL PERÚ							
	NOMBRE	FIRMA	FECHA			TÍTULO: Uniones de fabricación / Cuadro 2 de 2	
DIBUJ.	Javier Acevedo		16/10/26				
VERIF.							
APROB.							
FABR.							
CALID.							
				MATERIAL: SEGÚN LISTA DE MATERIALES		N.º DE DIBUJO EB-17	A1
PESO: SEGÚN CAD / BOM				ESCALA: INDICADA		ESTACIÓN DE DESCARGA BIGBAG	HOJA 17 DE 17